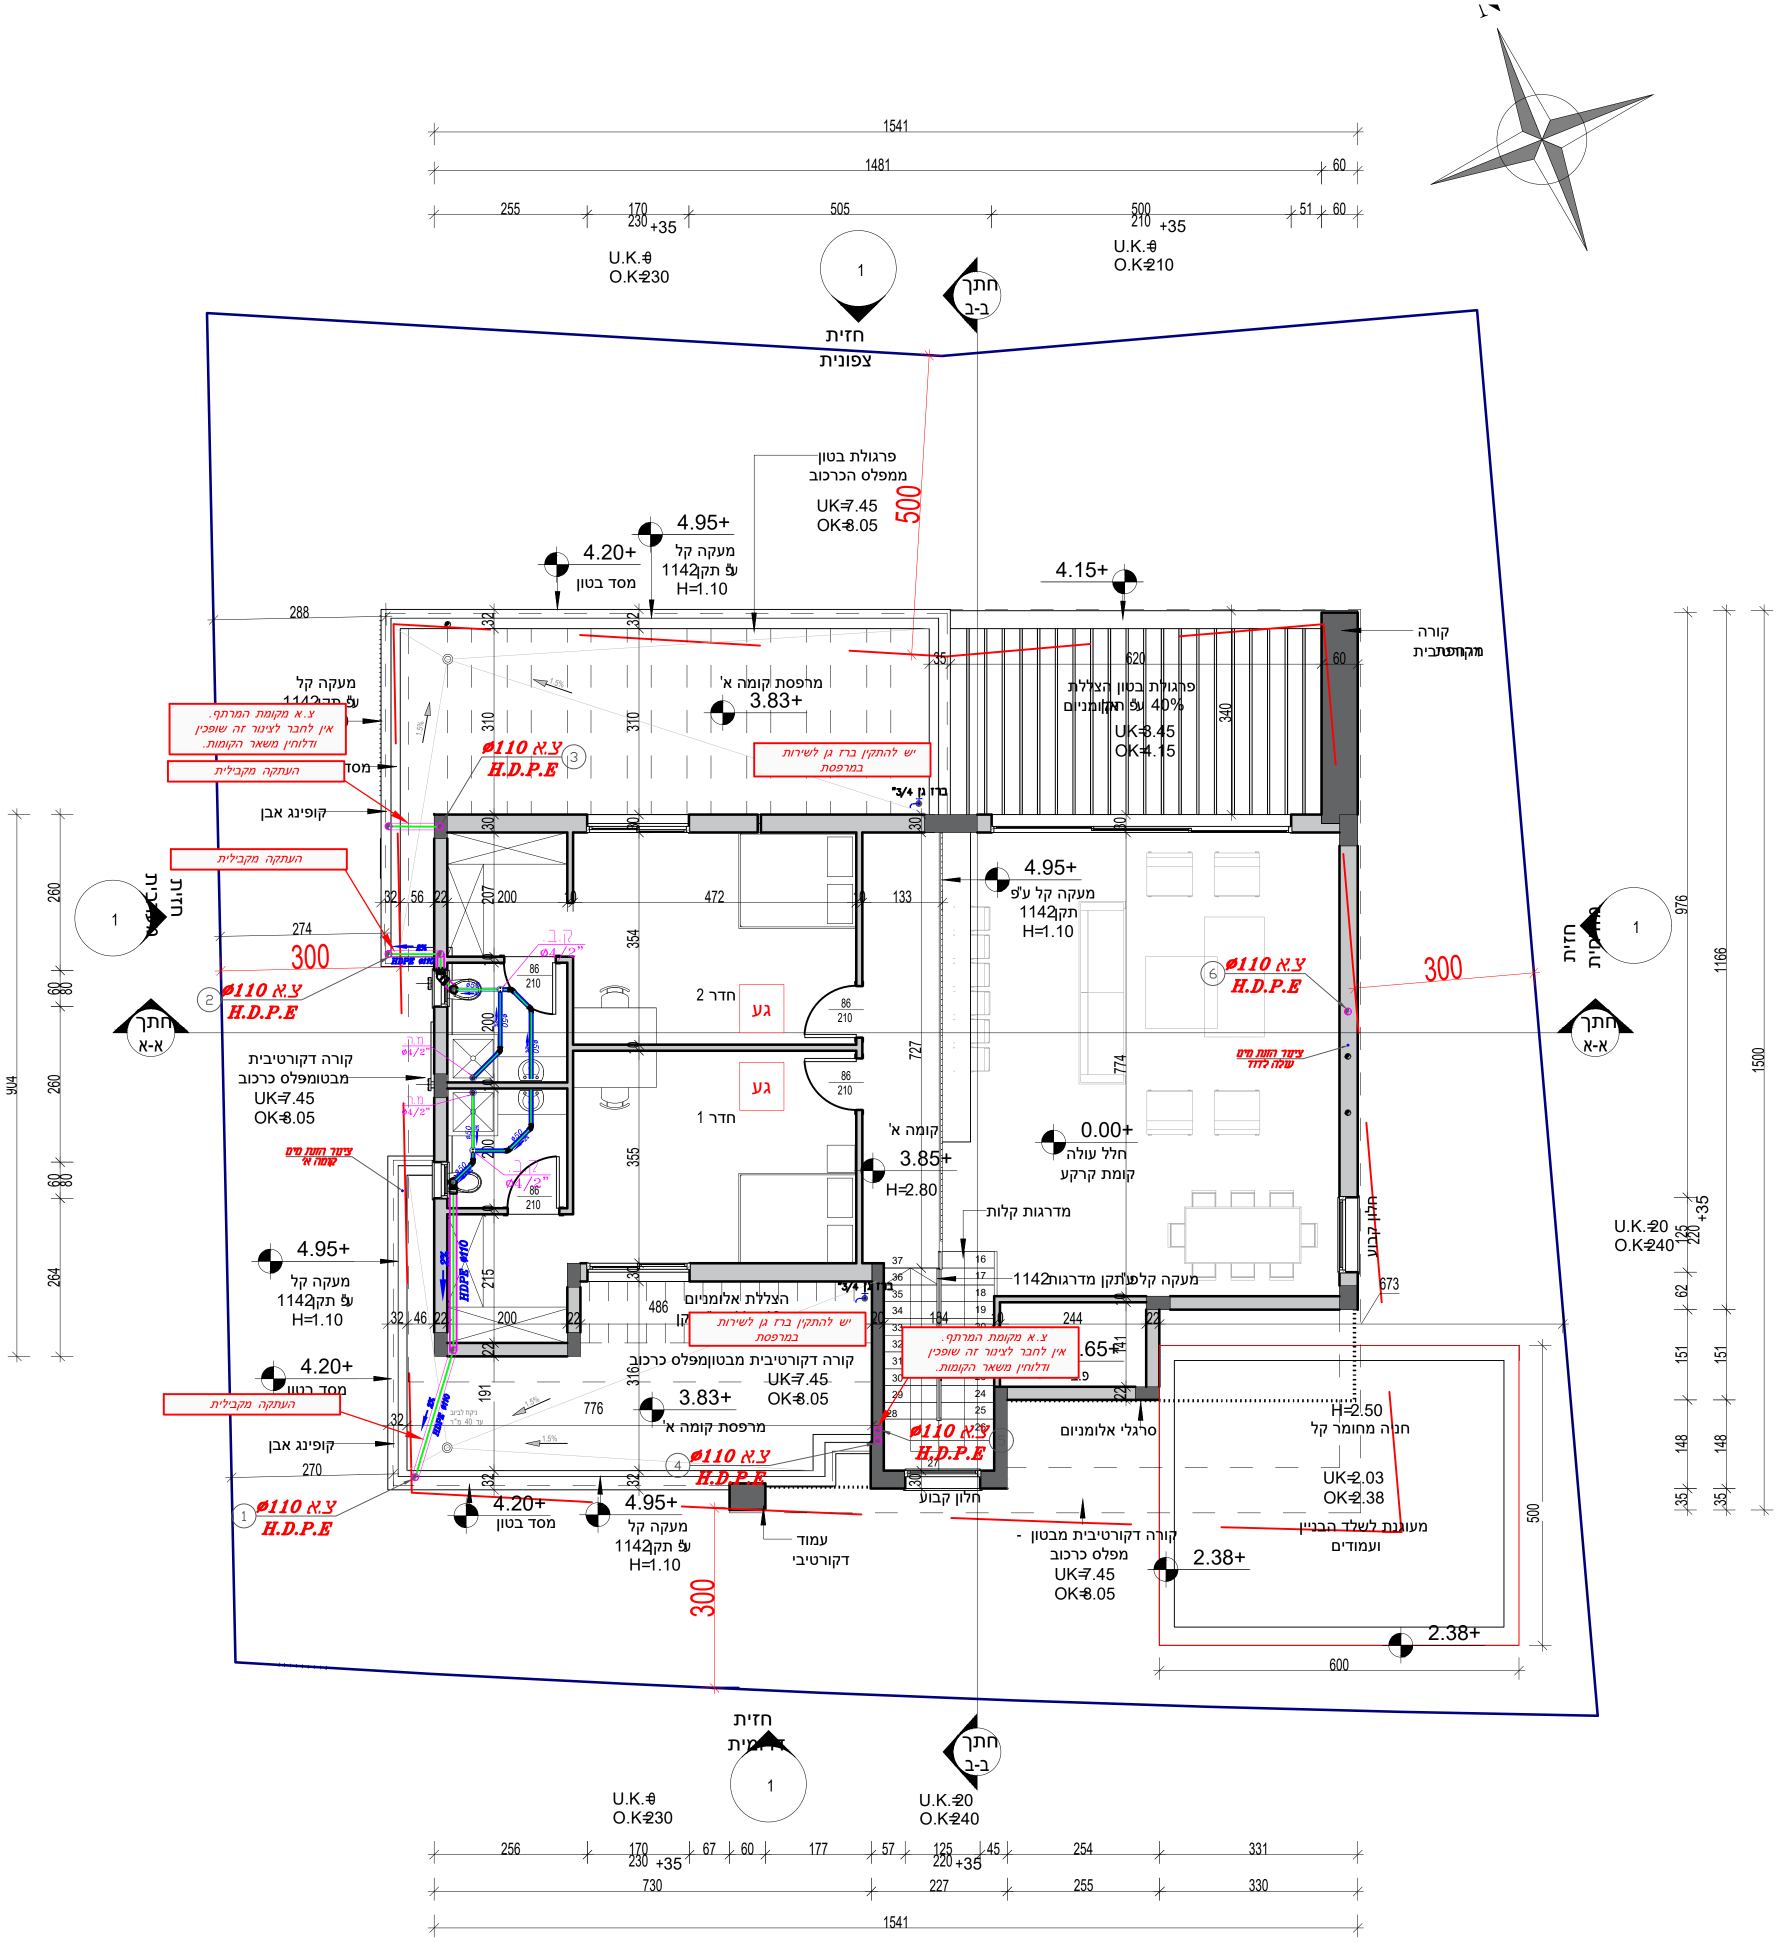
חזית צפונית
חזית מזרחית
חזית מערבית
חזית דרומית
חתך א-א
חתך ב-ב
פרגולת בטון ממפלס הכרכוב
UK=7.45
OK=8.05
500
300
4.20+
מסד בטון
4.95+
מעקה קל ע"פ תקן 1142
H=1.10
4.15+
פרגולת בטון הצללת עץ / אלומיניום 40%
UK=3.45
OK=4.15
קורה מקורה תבנית
מרפסת קומה א'
3.83+
צ.א מקומת המרתף. אין לחבר לציוד זה שופכין ודלוחין משאר הקומות.
העתקה מקבילית
יש להתקין ברז גן לשירות במרפסת
ברז גן 3/4"
ø110 צ.א H.D.P.E
קופינג אבן
חדר 2
חדר 1
גע
קומה א'
3.85+
H=2.80
0.00+
חלל עולה קומת קרקע
מדרגות קלות
מעקה קל ע"פ תקן 1142 מדרגות
קורה דקורטיבית מבטומפלס כרכוב
ציוד הזנת מים קומה א'
ציוד הזנת מים שלה לדוד
הצללת אלומיניום
סרגלי אלומיניום
חלון קבוע
עמוד דקורטיבי
קורה דקורטיבית מבטון - מפלס כרכוב
חניה מחומר קל
H=2.50
UK=2.03
OK=2.38
2.38+
מעוגנת לשלד הבניין ועמודים
U.K.=6
O.K.=230
U.K.=6
O.K.=210
U.K.=20
O.K.=240
HDPE ø110
1541
1481
730
600
1500
1166
976