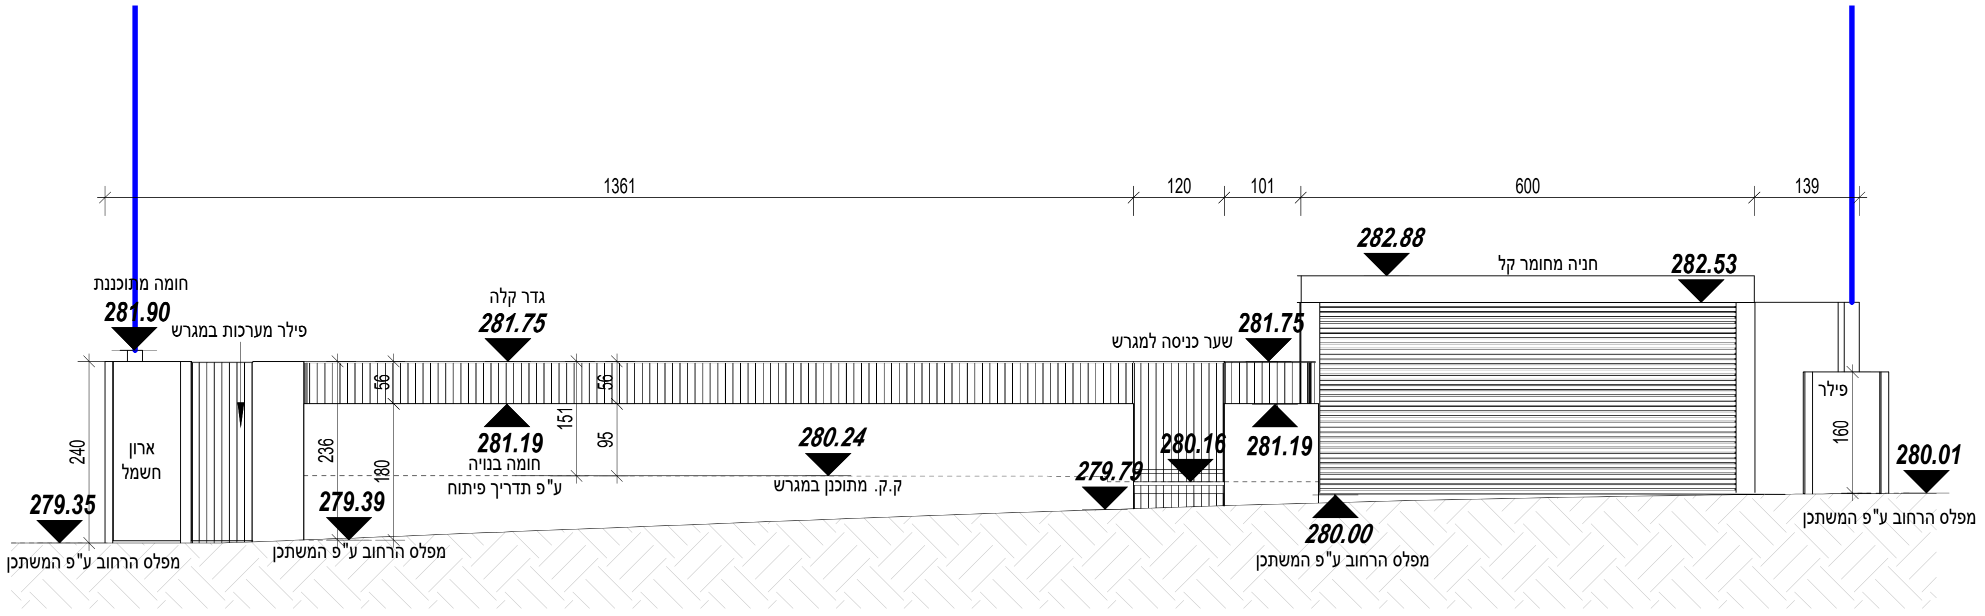

1361
120
101
600
139
חומה מתוכננת
281.90
פילר מערכות במגרש
ארון
חשמל
240
279.35
מפלס הרחוב ע"פ המשתכן
גדר קלה
281.75
56
56
151
95
236
180
281.19
חומה בנויה
ע"פ תדריך פיתוח
279.39
מפלס הרחוב ע"פ המשתכן
280.24
ק.ק. מתוכנן במגרש
279.79
280.16
שער כניסה למגרש
281.75
281.19
282.88
חניה מחומר קל
282.53
280.00
מפלס הרחוב ע"פ המשתכן
פילר
160
280.01
מפלס הרחוב ע"פ המשתכן

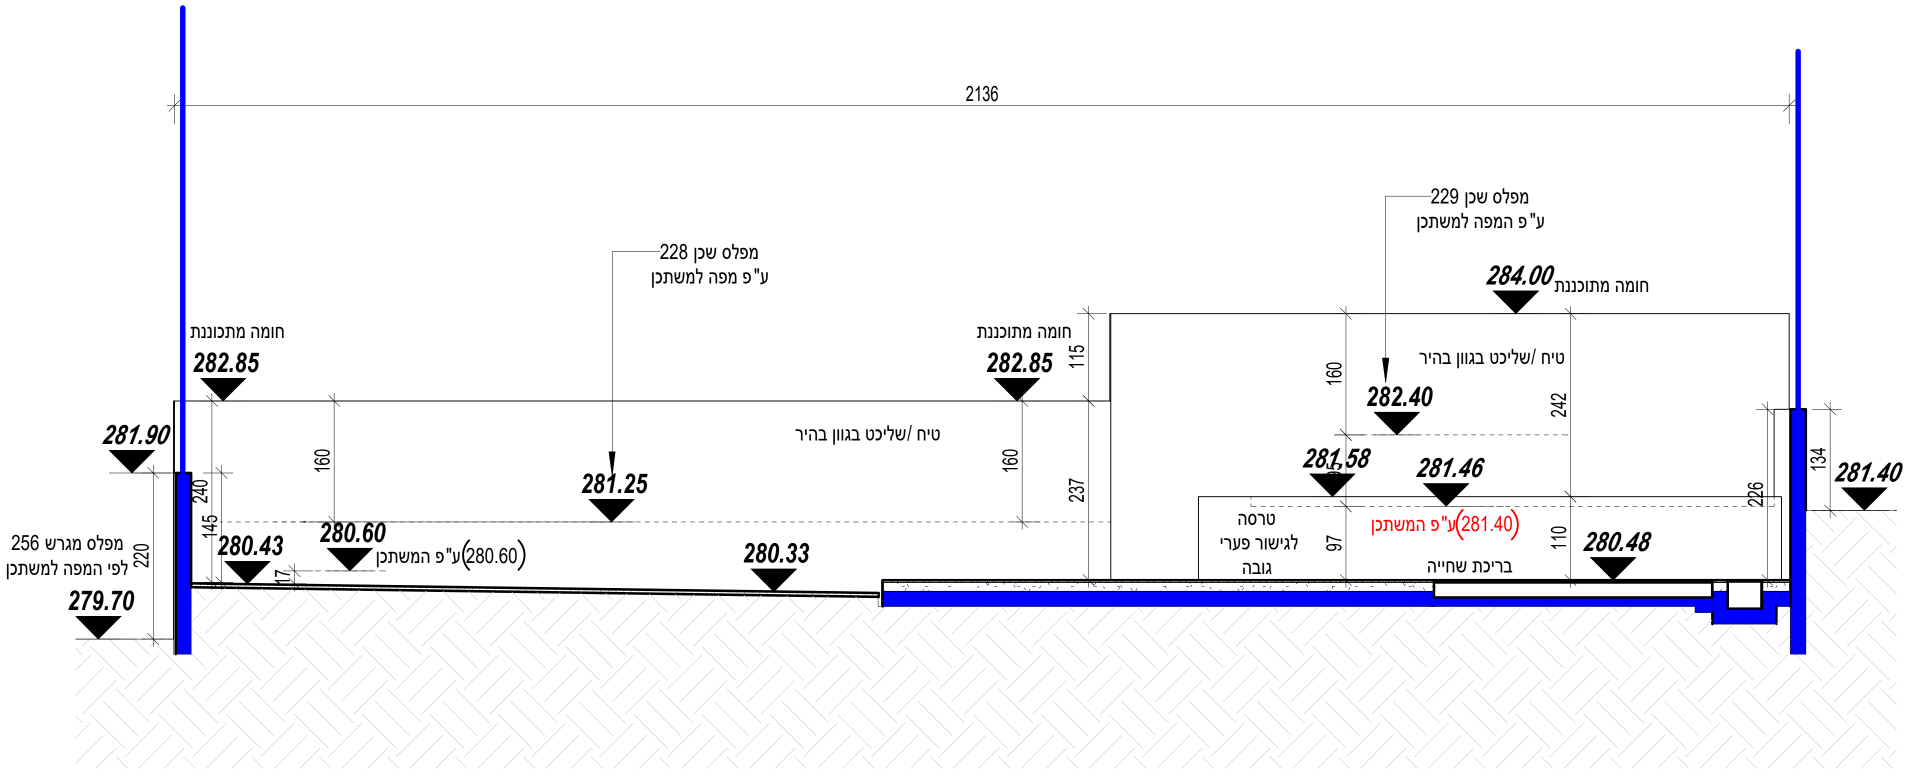

2136
מפלס שכן 228
ע"פ מפה למשתכן
חומה מתכוננת
282.85
281.90
240
145
160
220
מפלס מגרש 256
לפי המפה למשתכן
279.70
280.43
17
280.60
(280.60)ע"פ המשתכן
281.25
טיח /שליכט בגוון בהיר
280.33
חומה מתוכננת
282.85
115
160
237
מפלס שכן 229
ע"פ המפה למשתכן
284.00
חומה מתוכננת
טיח /שליכט בגוון בהיר
160
282.40
242
281.58
281.46
(281.40)ע"פ המשתכן
טרסה
לגישור פערי
גובה
97
110
בריכת שחייה
280.48
226
134
281.40