7.2	שכונת הרקפות באר שבע

נספחים
פרטי פיתוח

תאריך: 29.07.2024 | קנ"מ: משתנה

מהדורה: 009

1/08/24
עיריית באר-שבע
אולגה חריטונוב
אגף הנדסה
מנהלת מחלקת
תיאום תשתיות דרכים ופיתוח

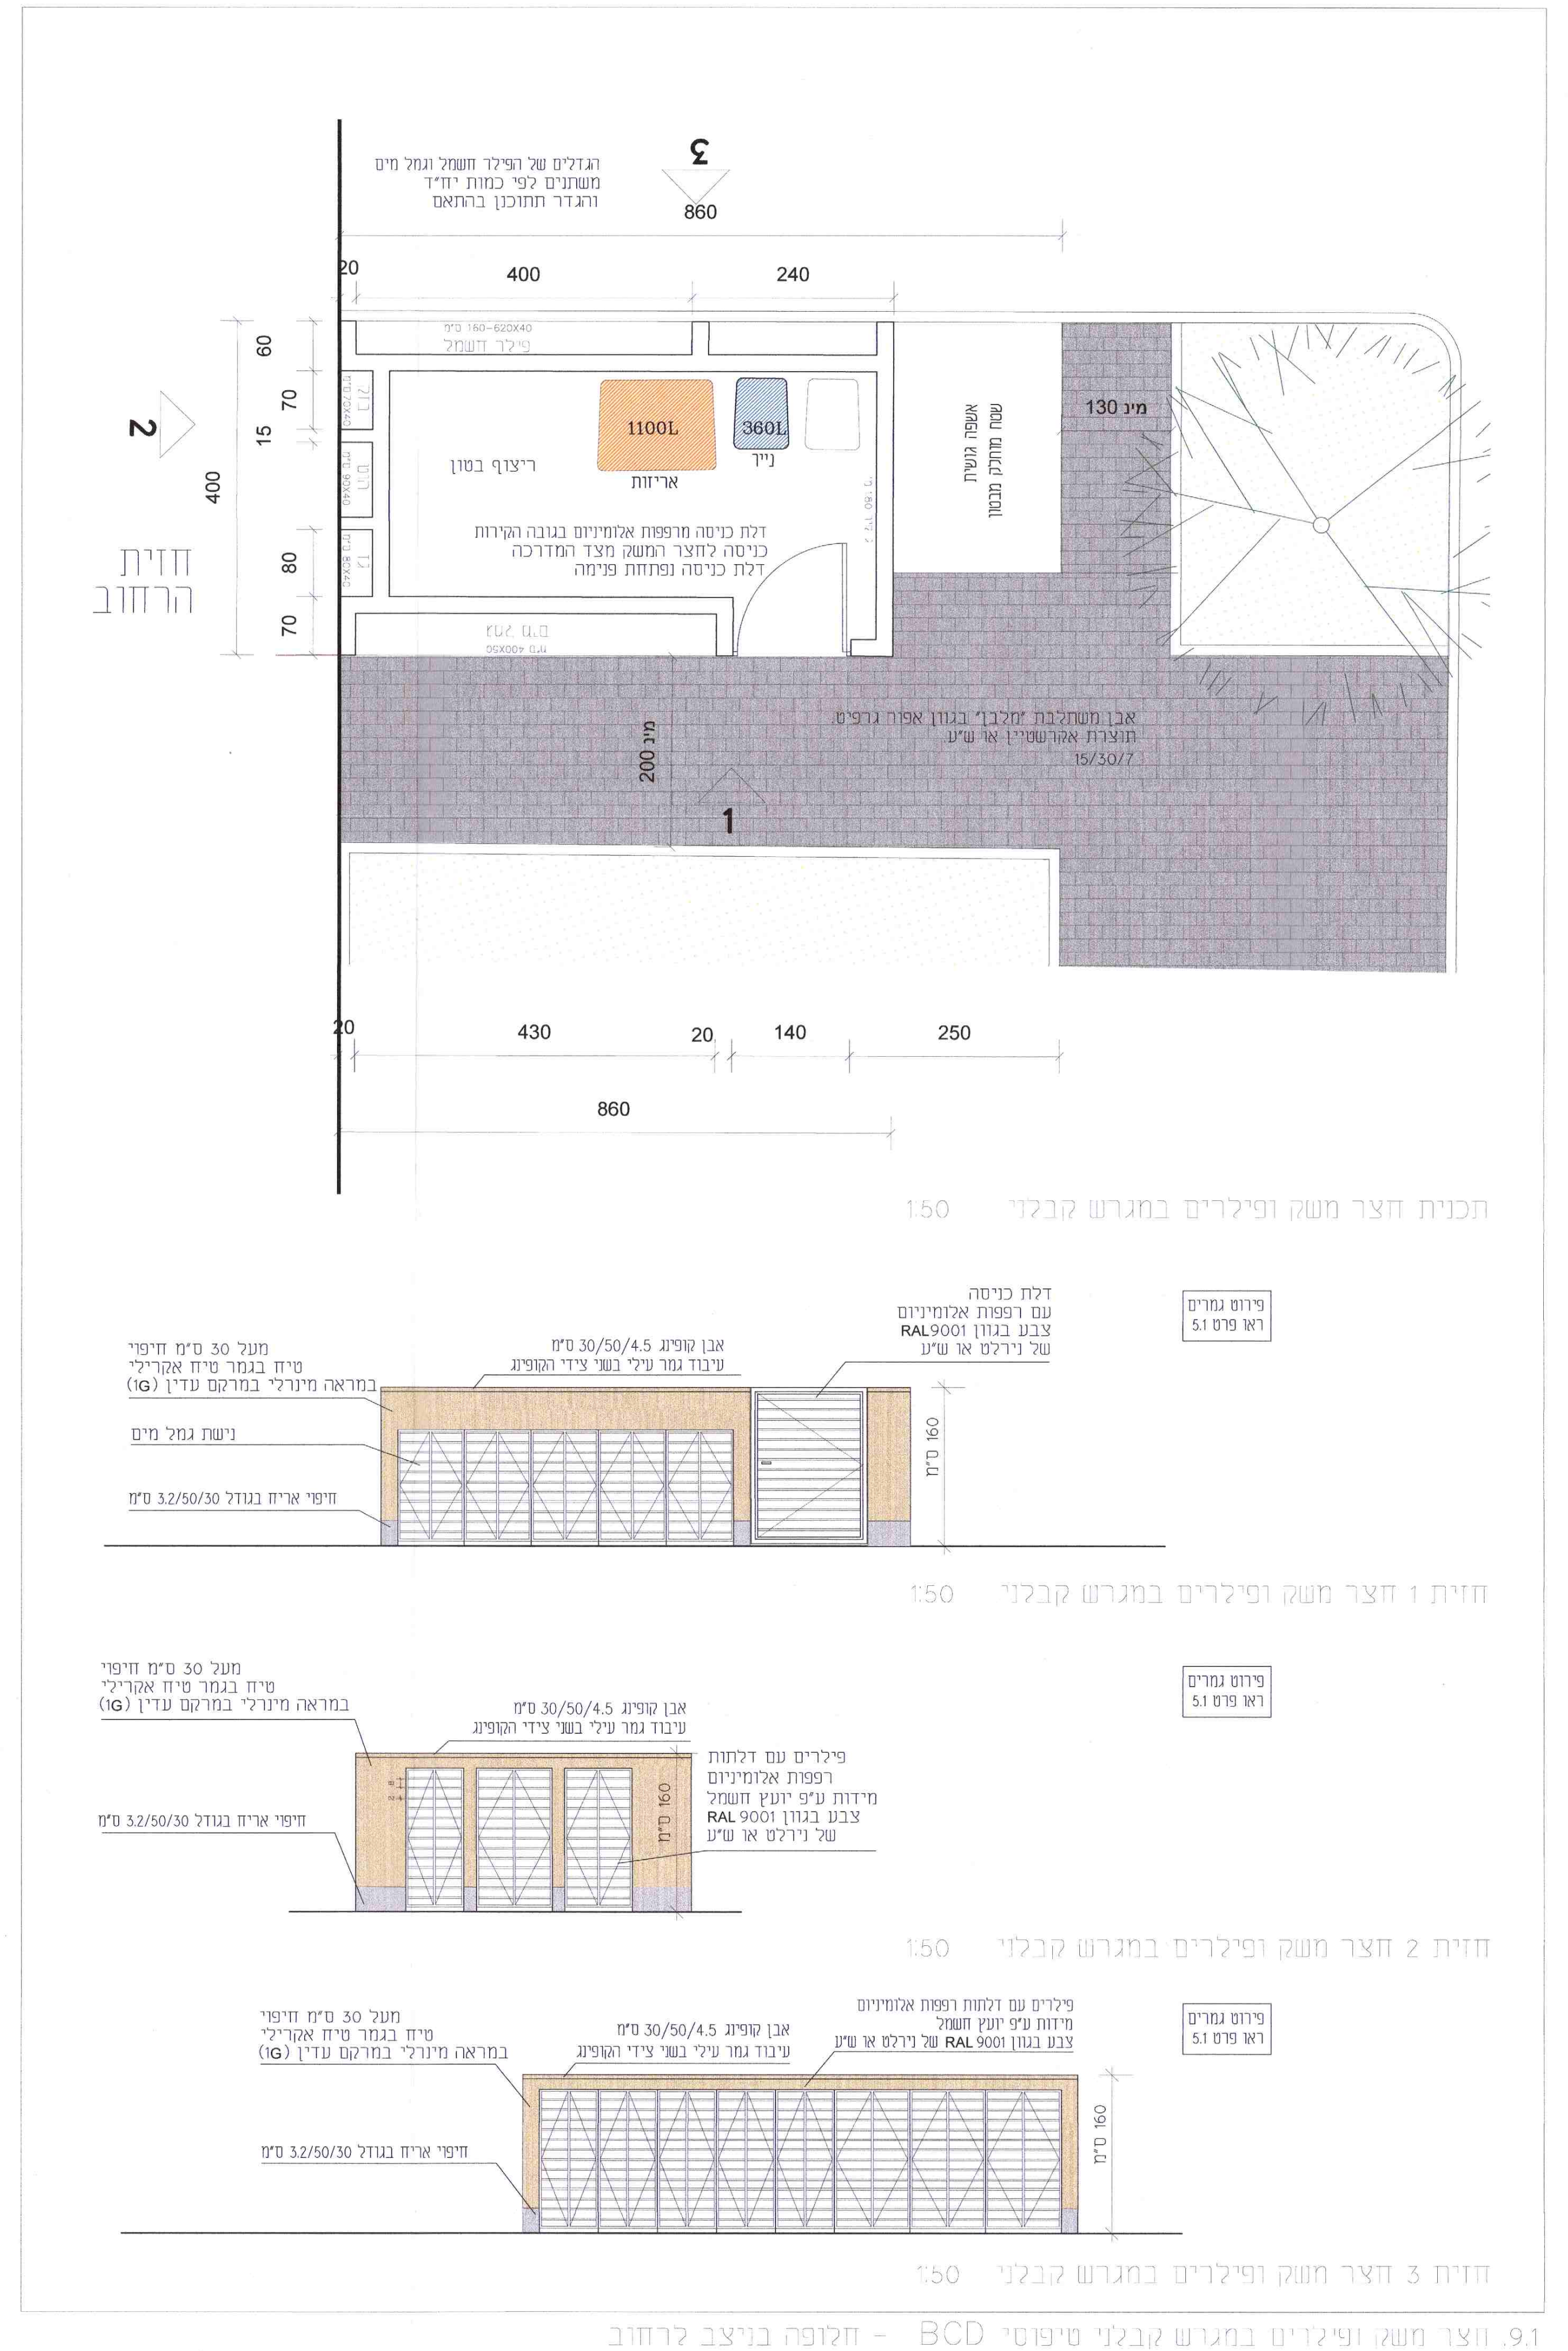

חזית הרחוב
חזית 3 חצר משק ופילרים במגרש קבלני 1:50
חיפוי אריח בגודל 3.2/50/30 ס"מ

9.1. חצר משק ופילרים במגרש קבלני טיפוסי BCD - חלופה בניצב לרחוב

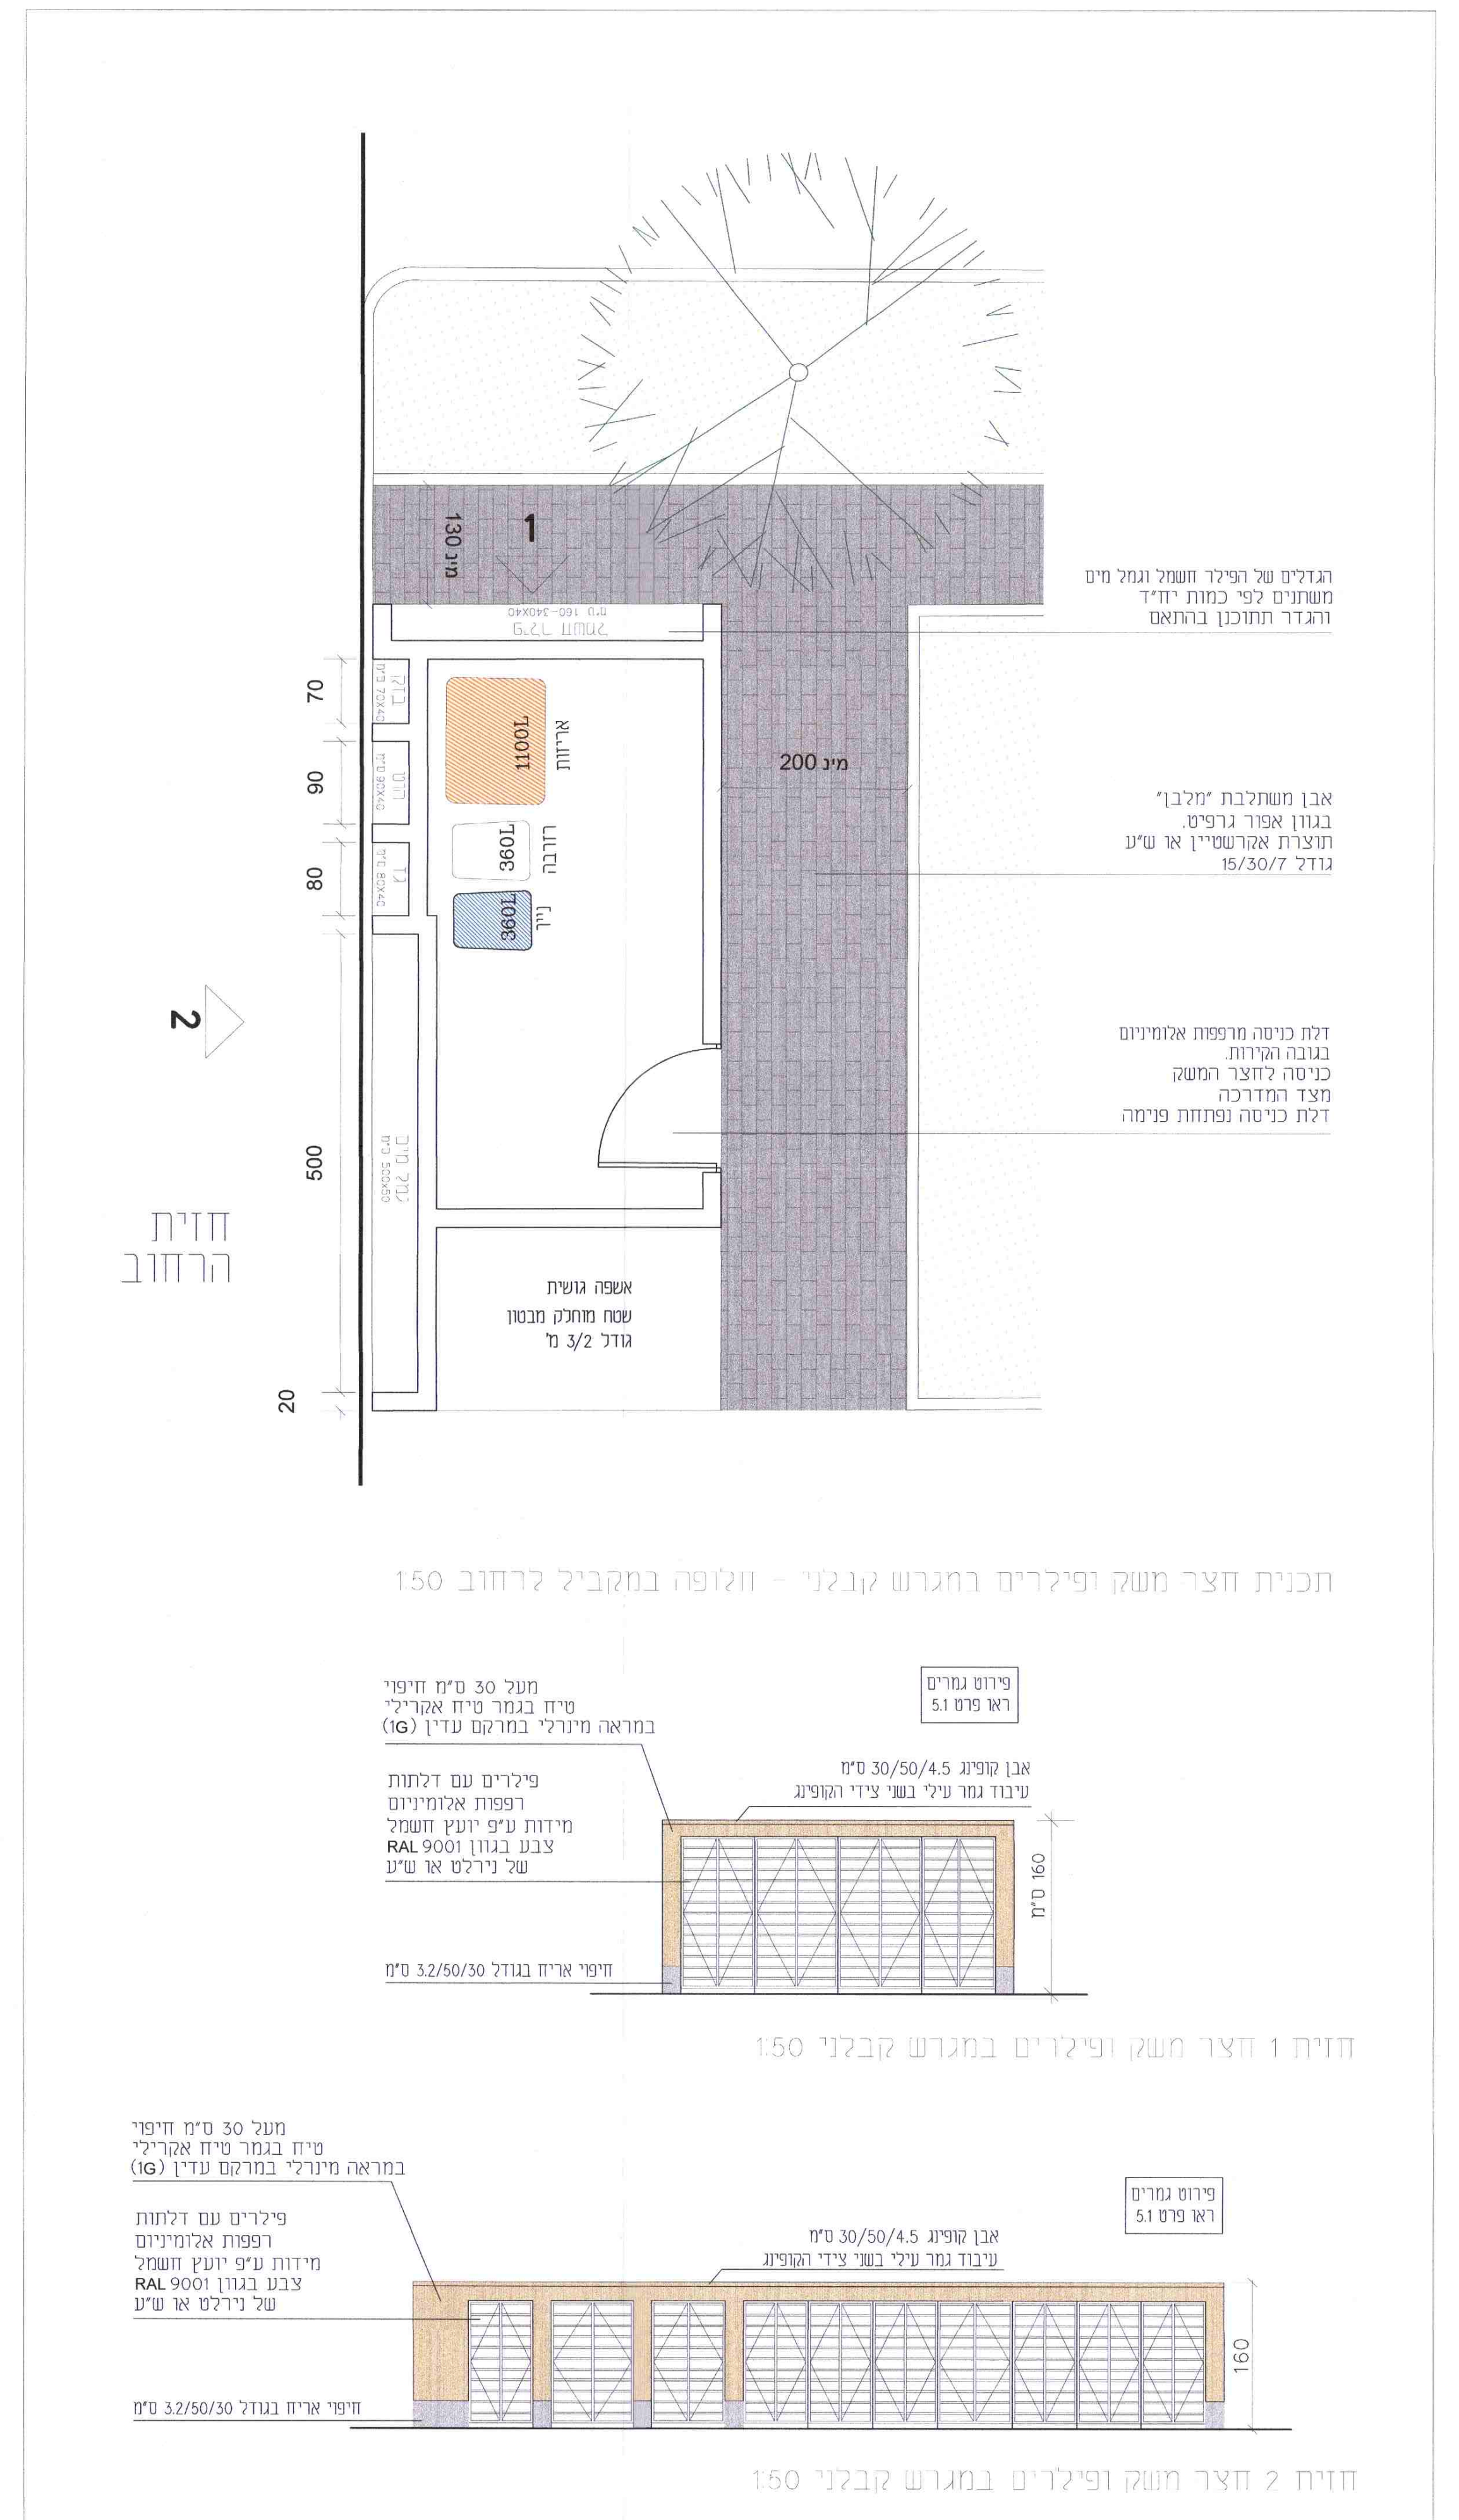

חזית הרחוב
חזית 2 חצר משק ופילרים במגרש קבלני 1:50
חיפוי אריח בגודל 3.2/50/30 ס"מ

9.1. חצר משק ופילרים במגרש קבלני טיפוסי BCD - חלופה במקביל לרחוב

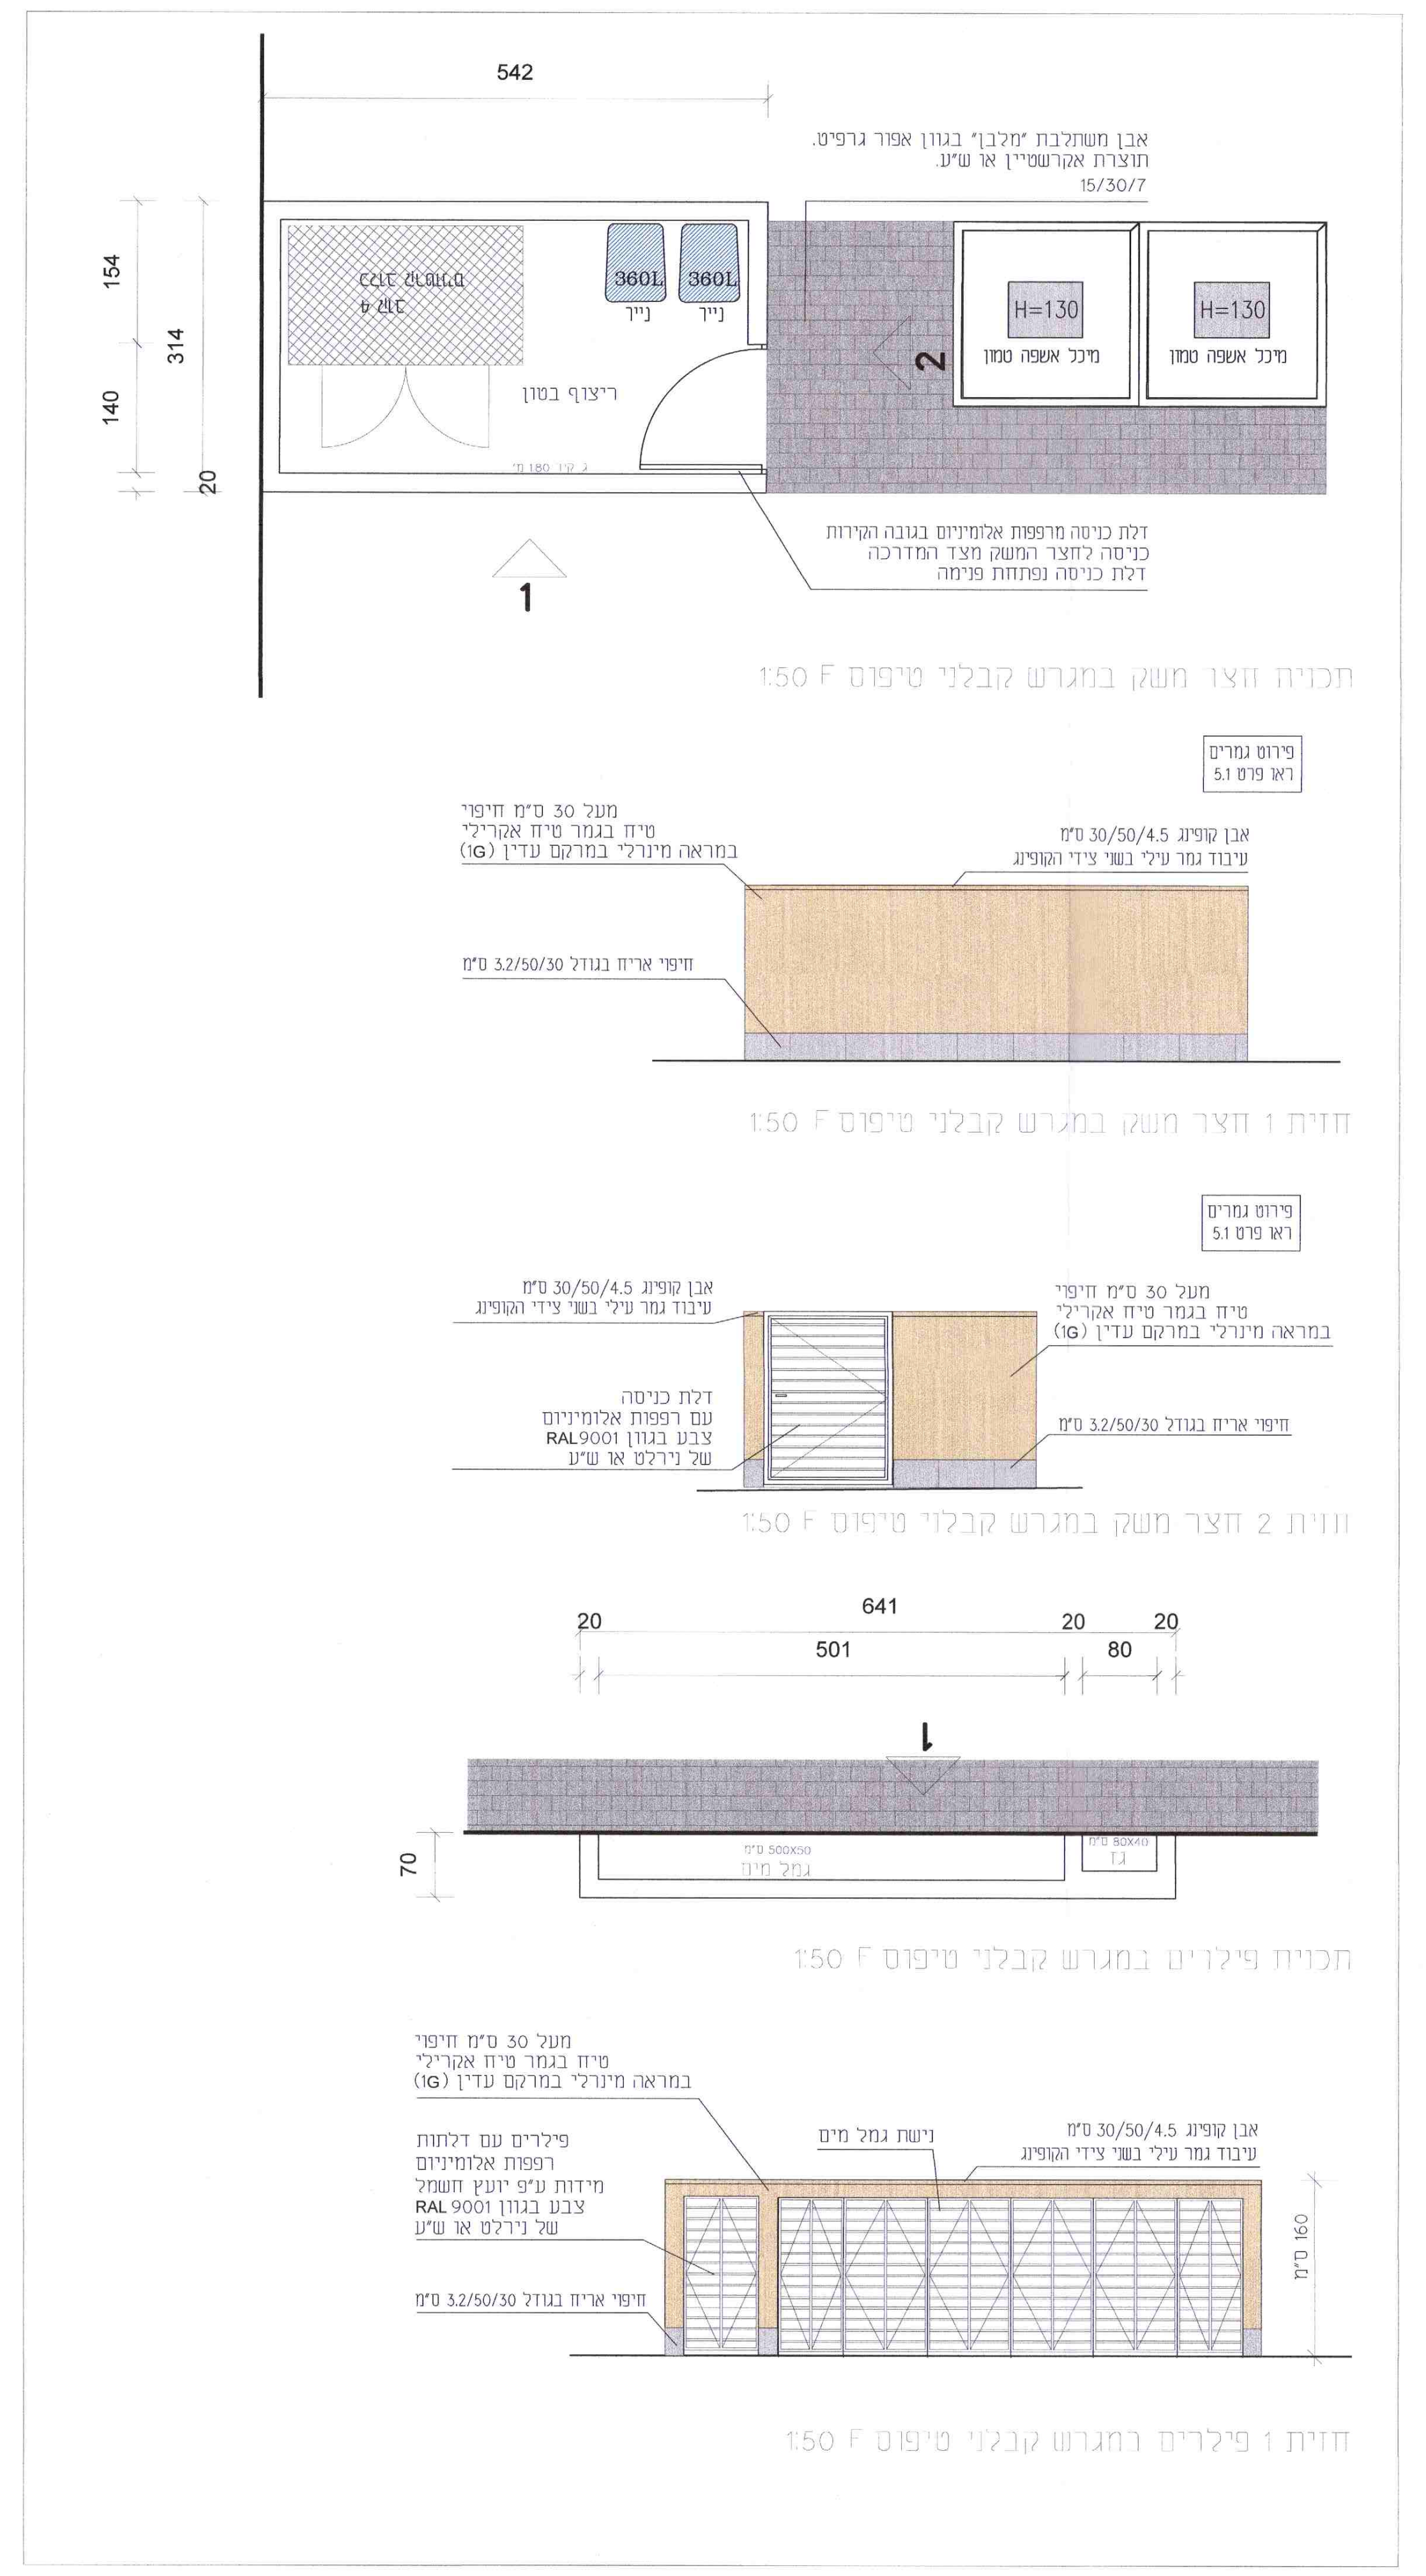

9.2. תכנית וחזיתות חצר משק ופילרים במגרש קבלני טיפוס F

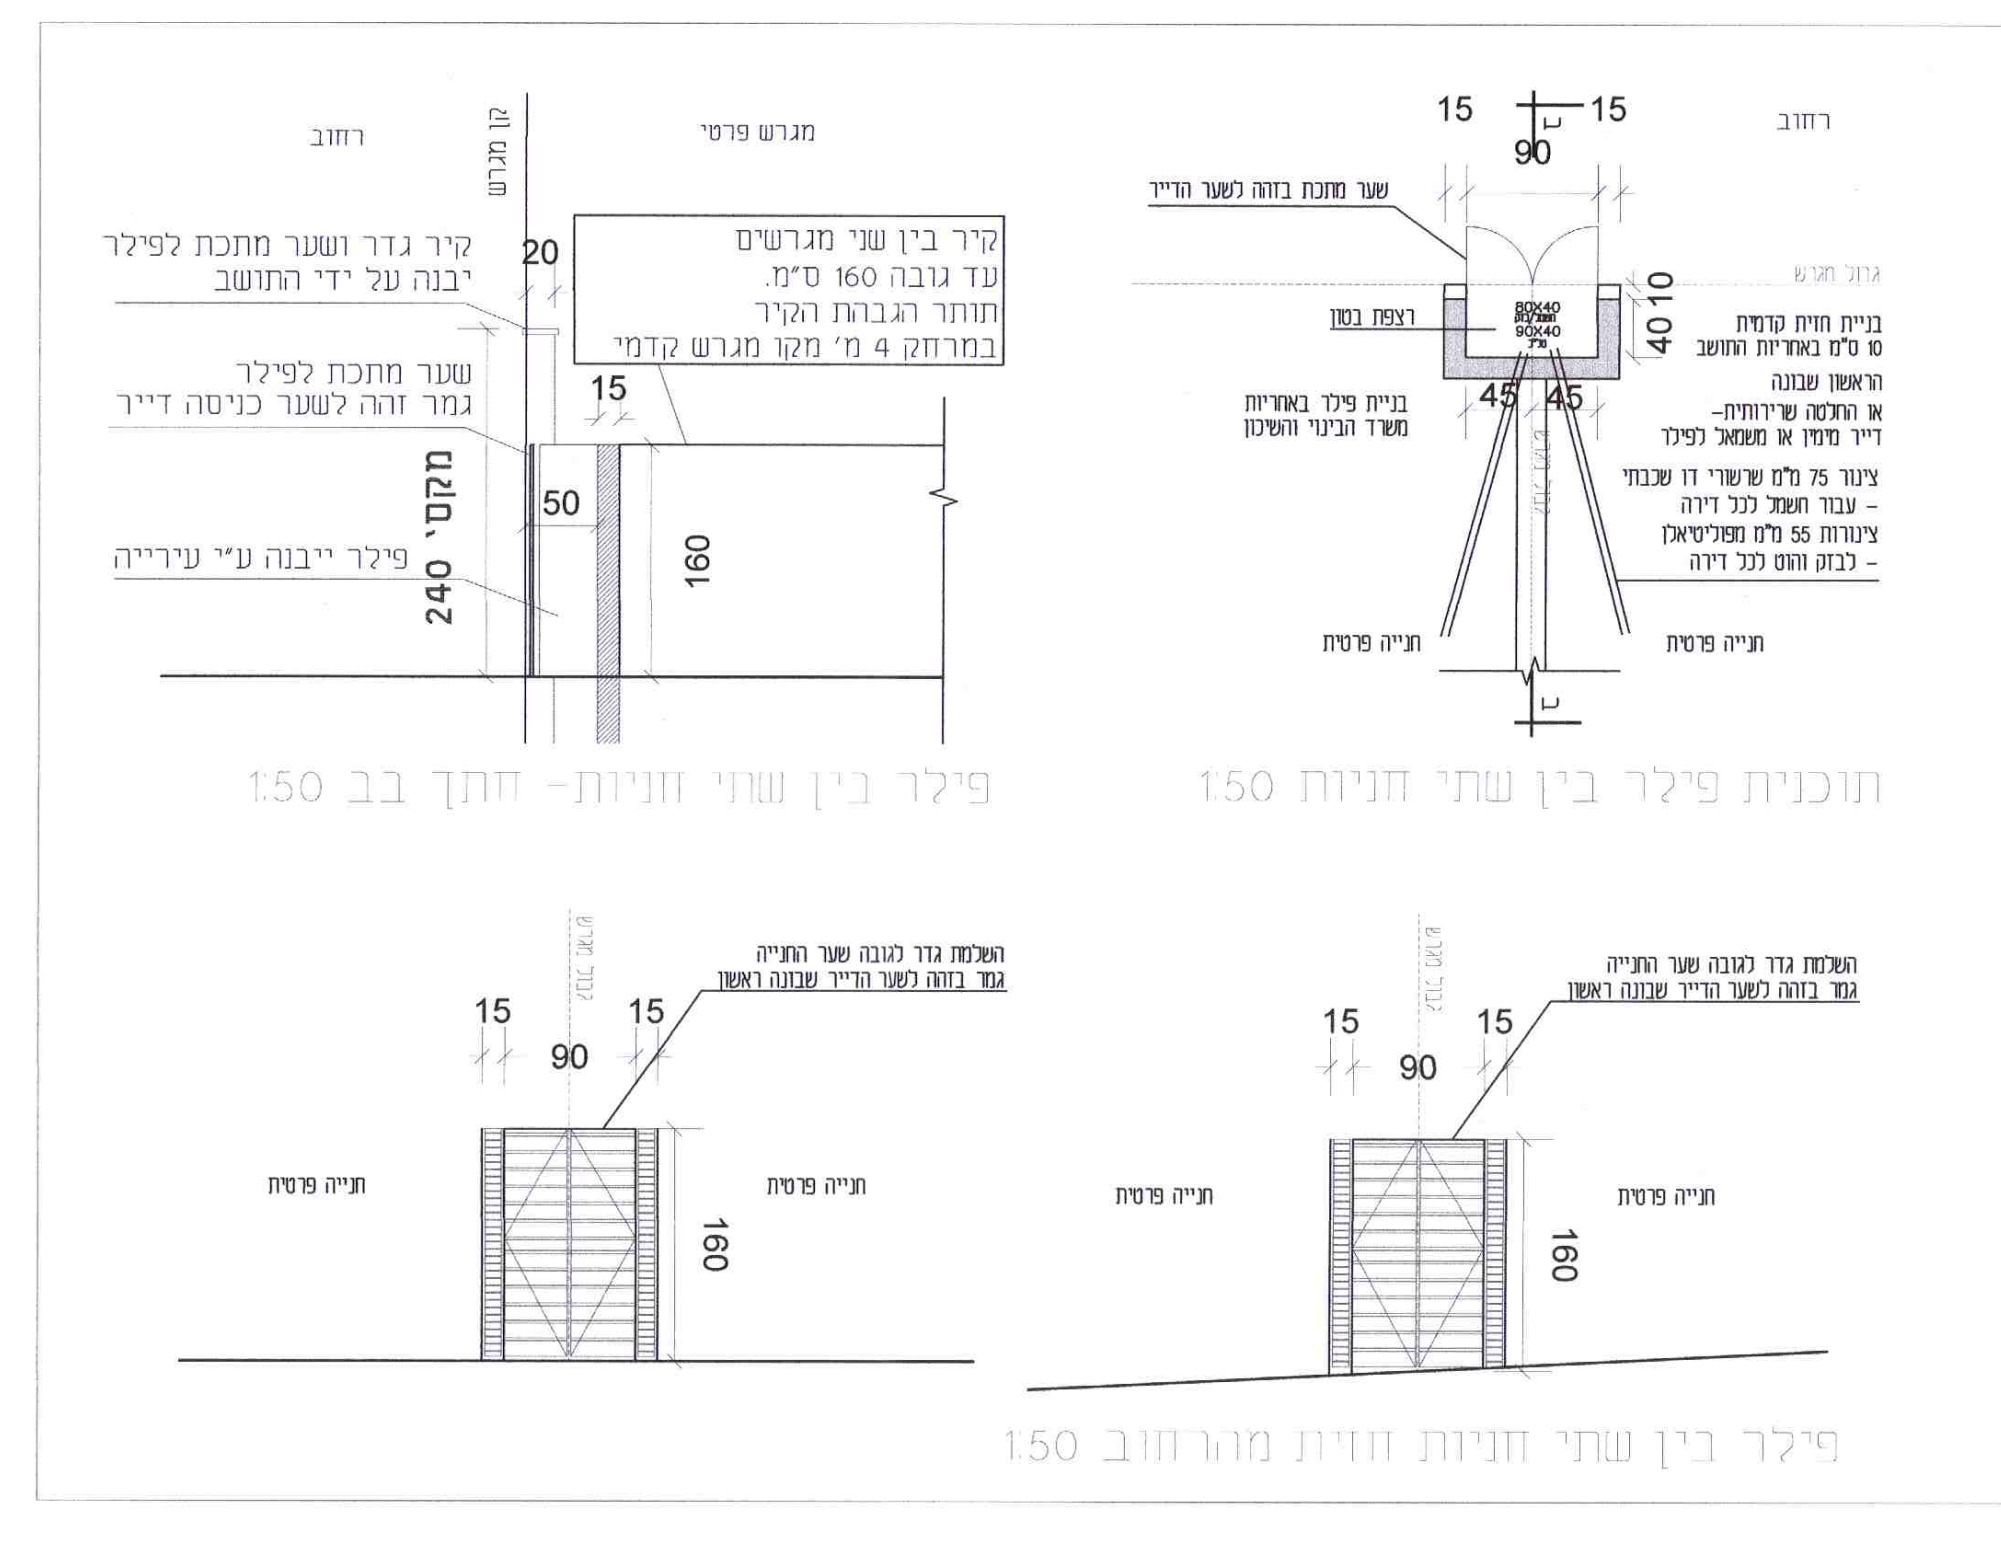

פילר בין שתי חניות- חתך בב 1:50
תוכנית פילר בין שתי חניות 1:50
2.8 תכנית פילרים במגרש פרטי 1:50 ללא גז
1.8 תכנית פילרים במגרש פרטי 1:50 כולל גז
חתך אא 1:50

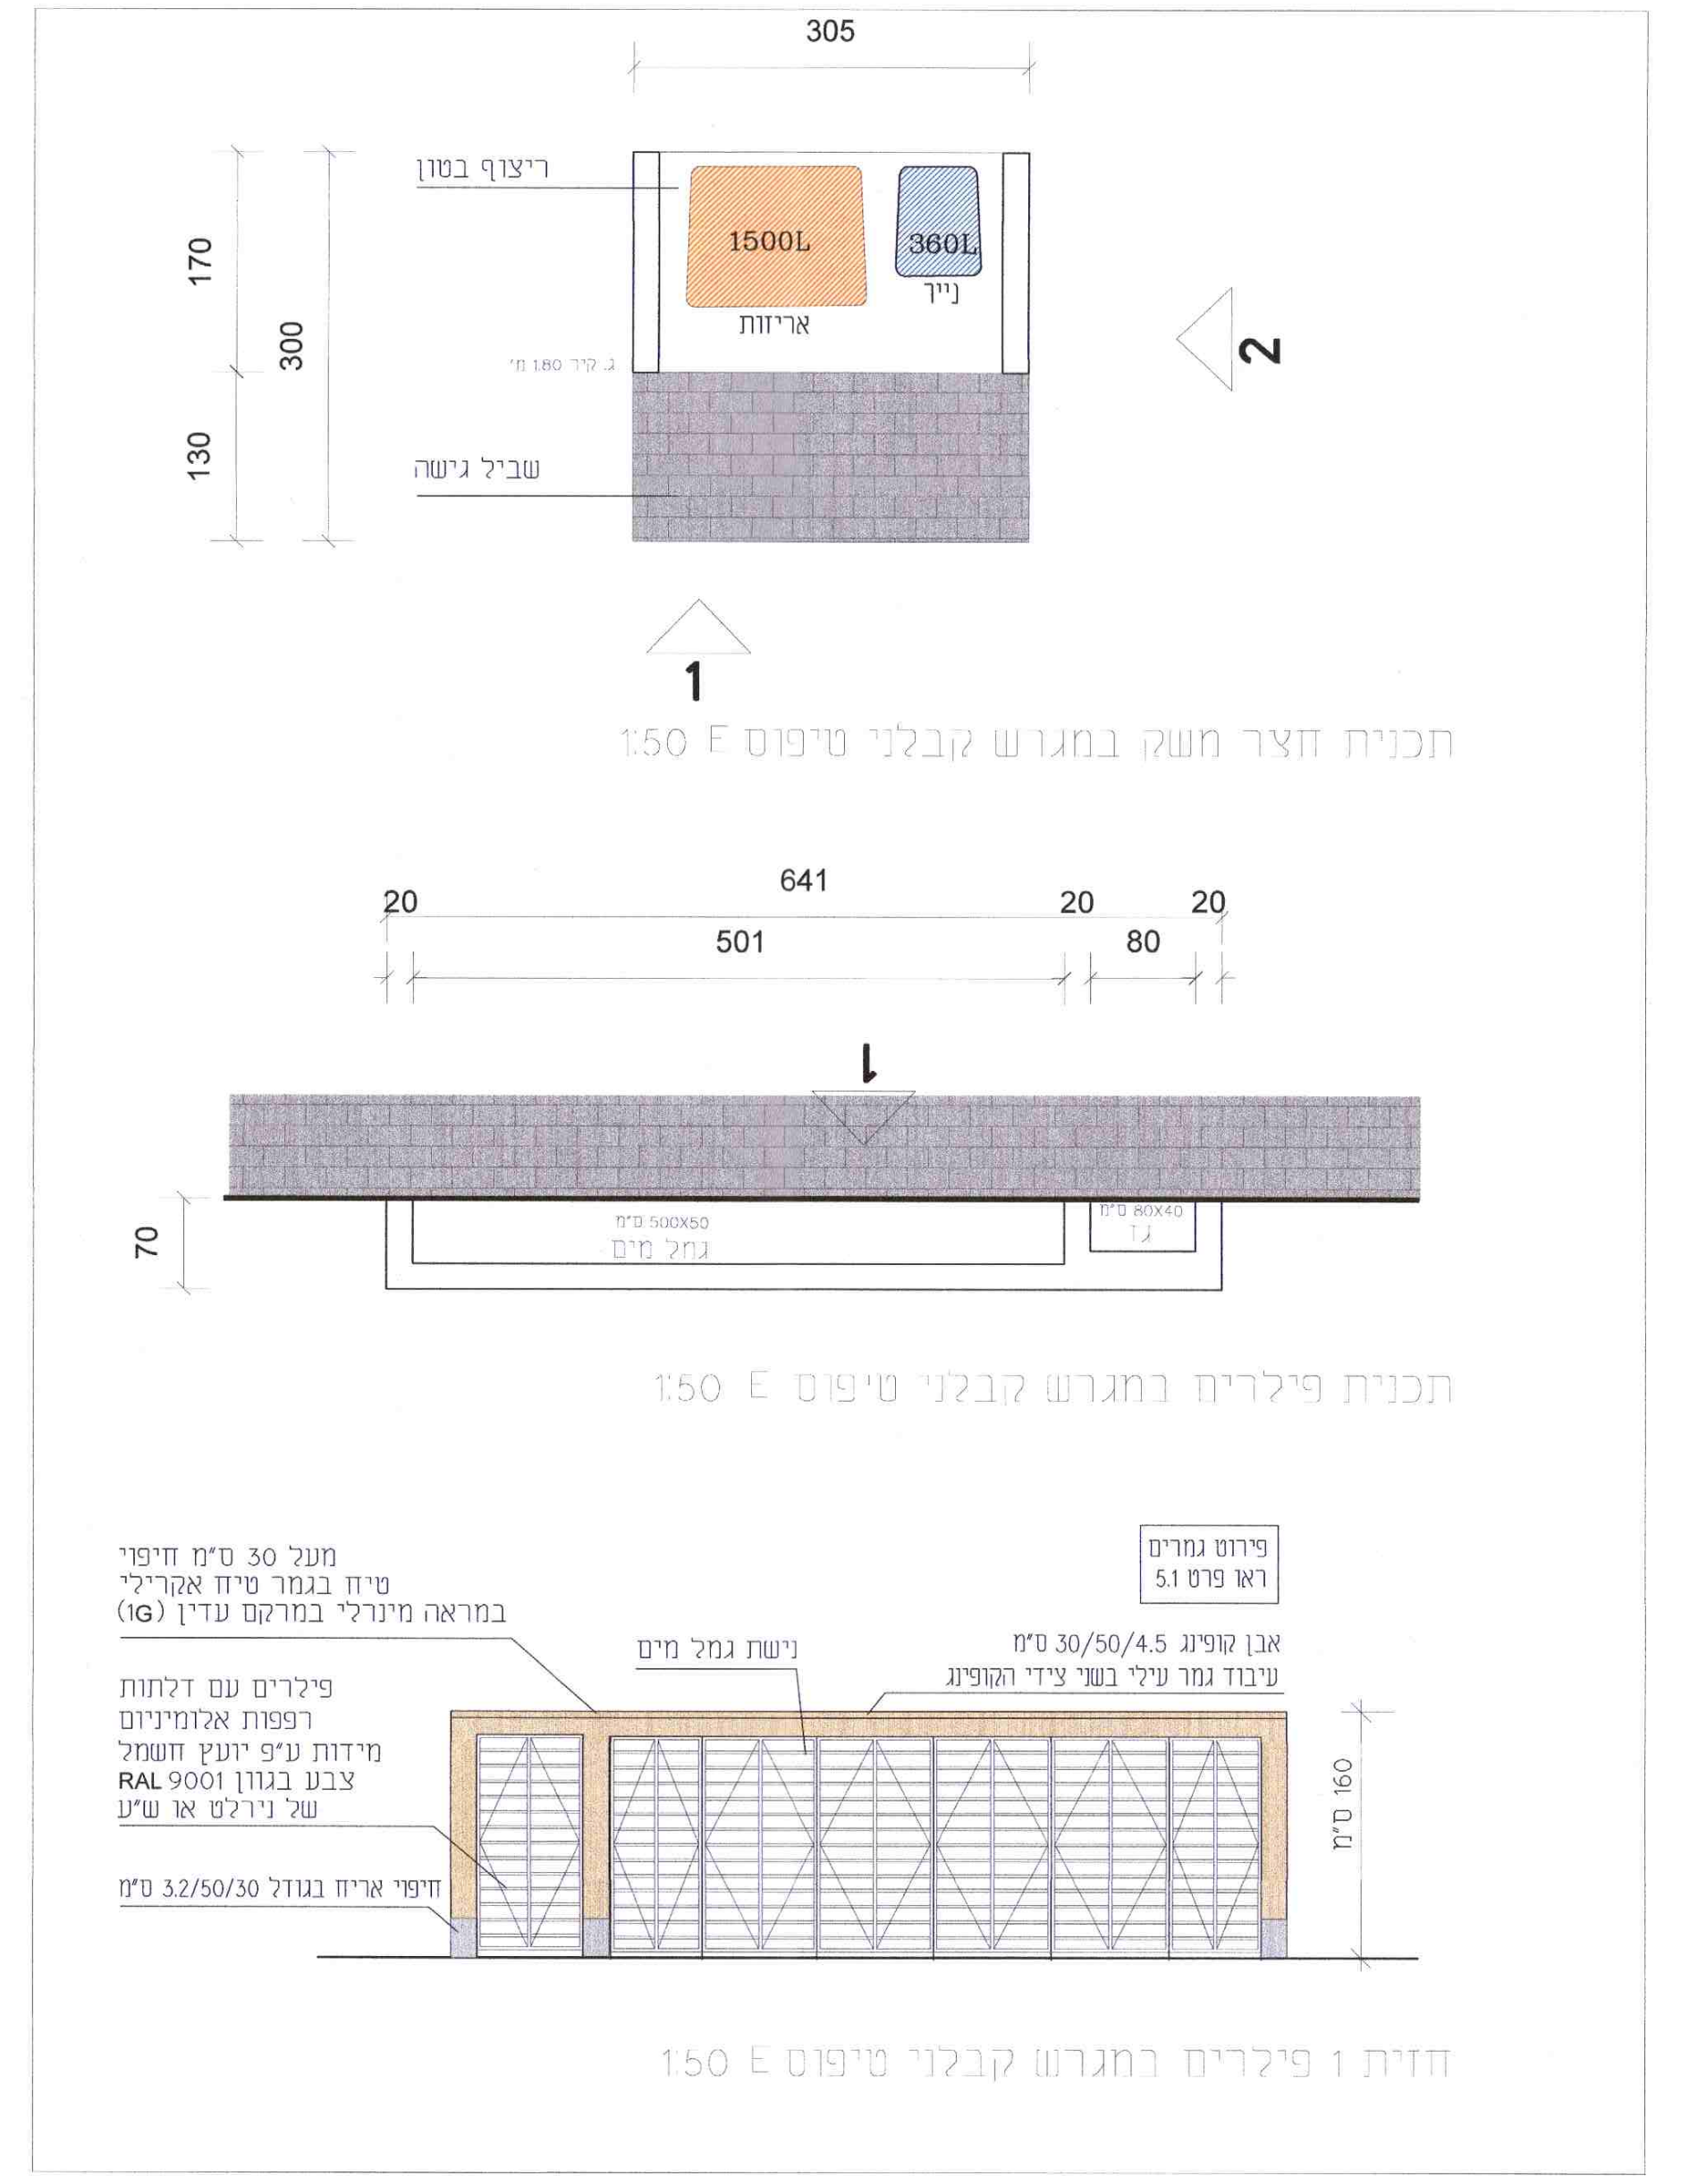

9.2. תכנית וחזיתות חצר משק ופילרים במגרש קבלני טיפוס E

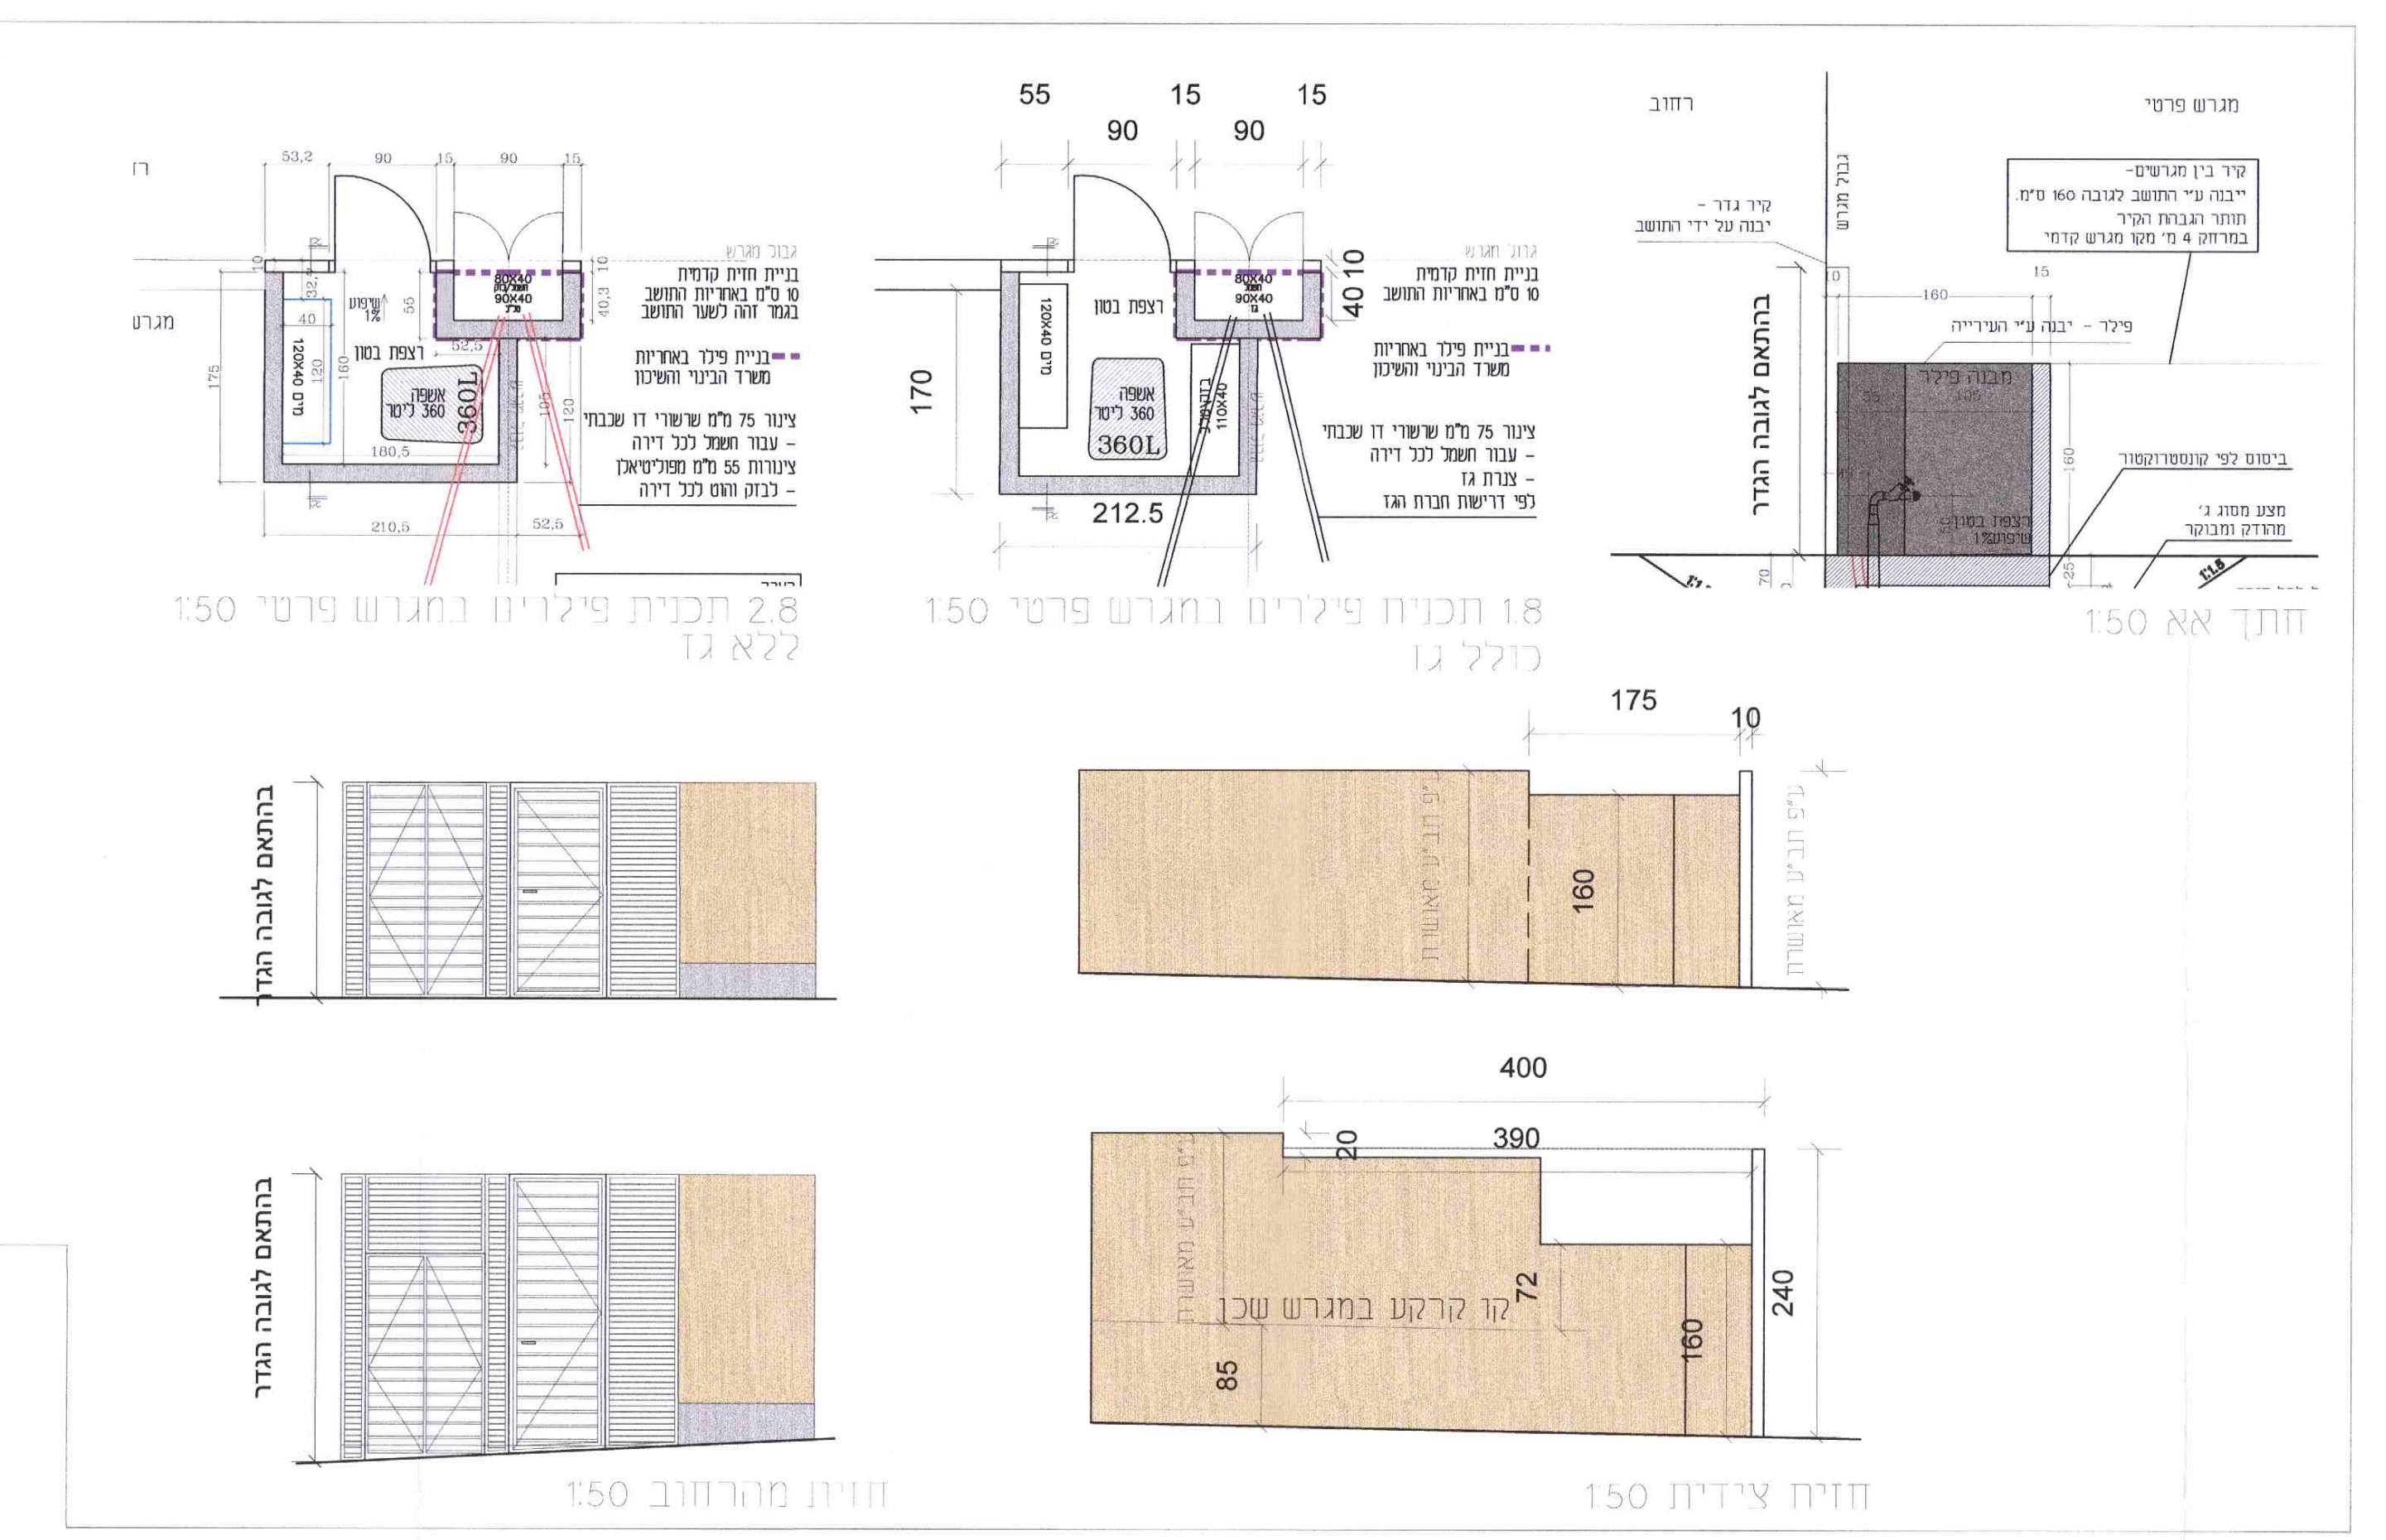

8. תכנית וחזית פילרים במגרש הפרטי - הפרט יאושר בהמשך על ידי העירייה

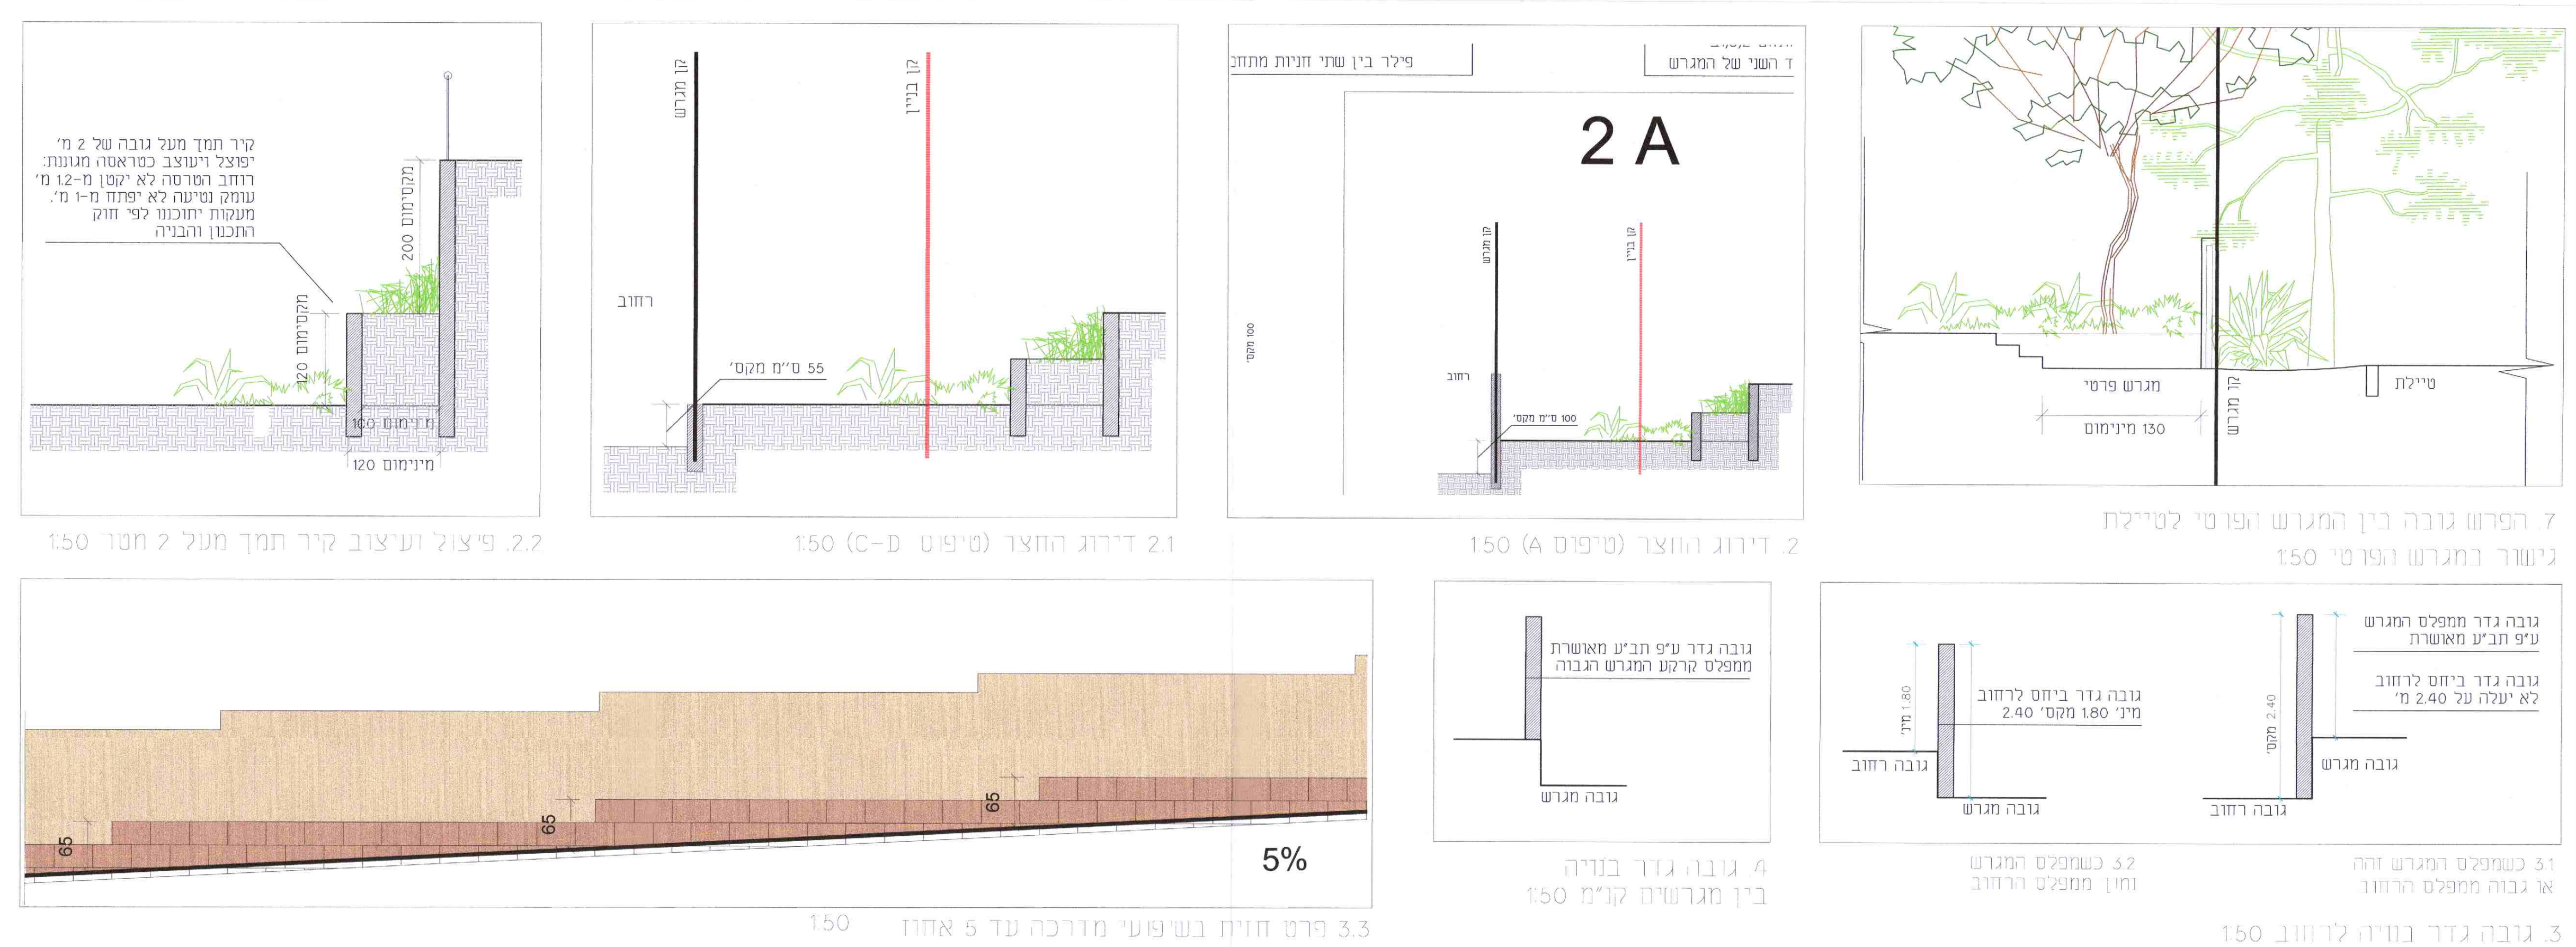

2.2 פיצול ועיצוב קיר תמך מעל 2 מטר 1:50
2.1 דירוג החצר (טיפוס C-D) 1:50
2. דירוג החצר (טיפוס A) 1:50
7. הפרש גובה בין המגרש הפרטי לטיילת גישור במגרש הפרטי 1:50
3.3 פרט חזית בשיפועי מדרכה עד 5 אחוז 1:50
5%
4. גובה גדר בנויה בין מגרשים קיים 1:50
3. גובה גדר בנויה לרחוב 1:50
2 A

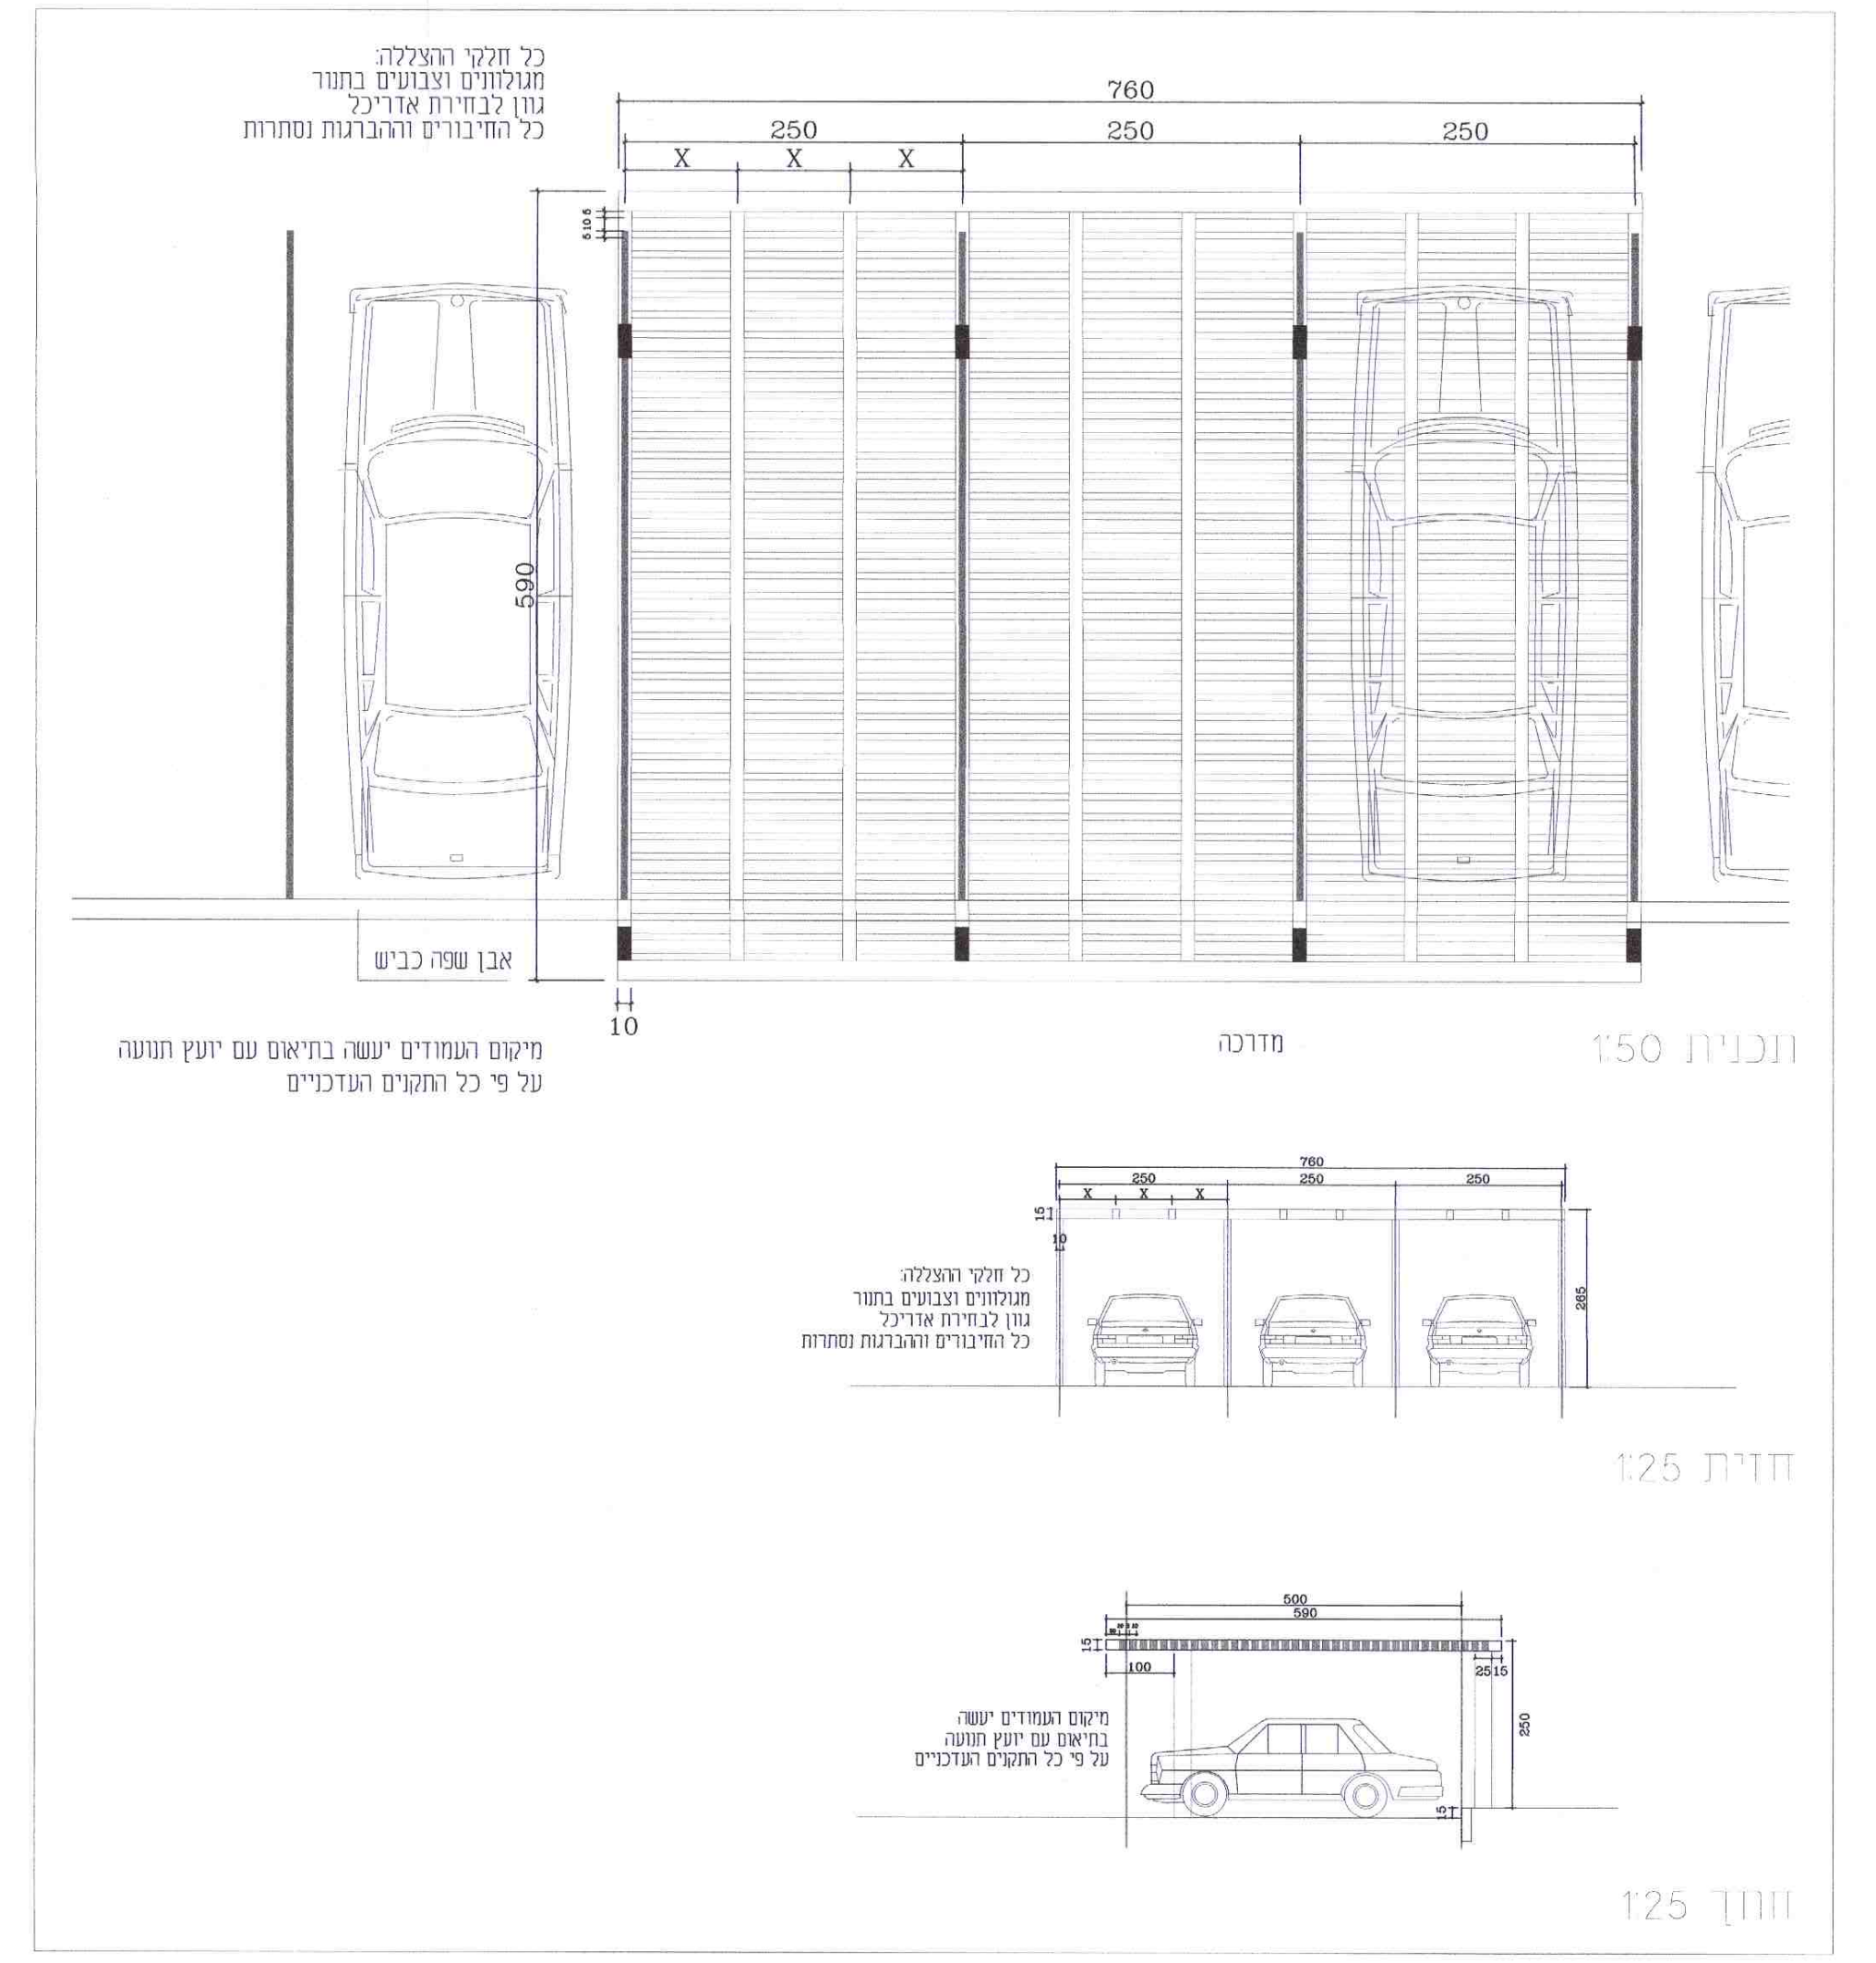

15. פרט קירוי לחניה

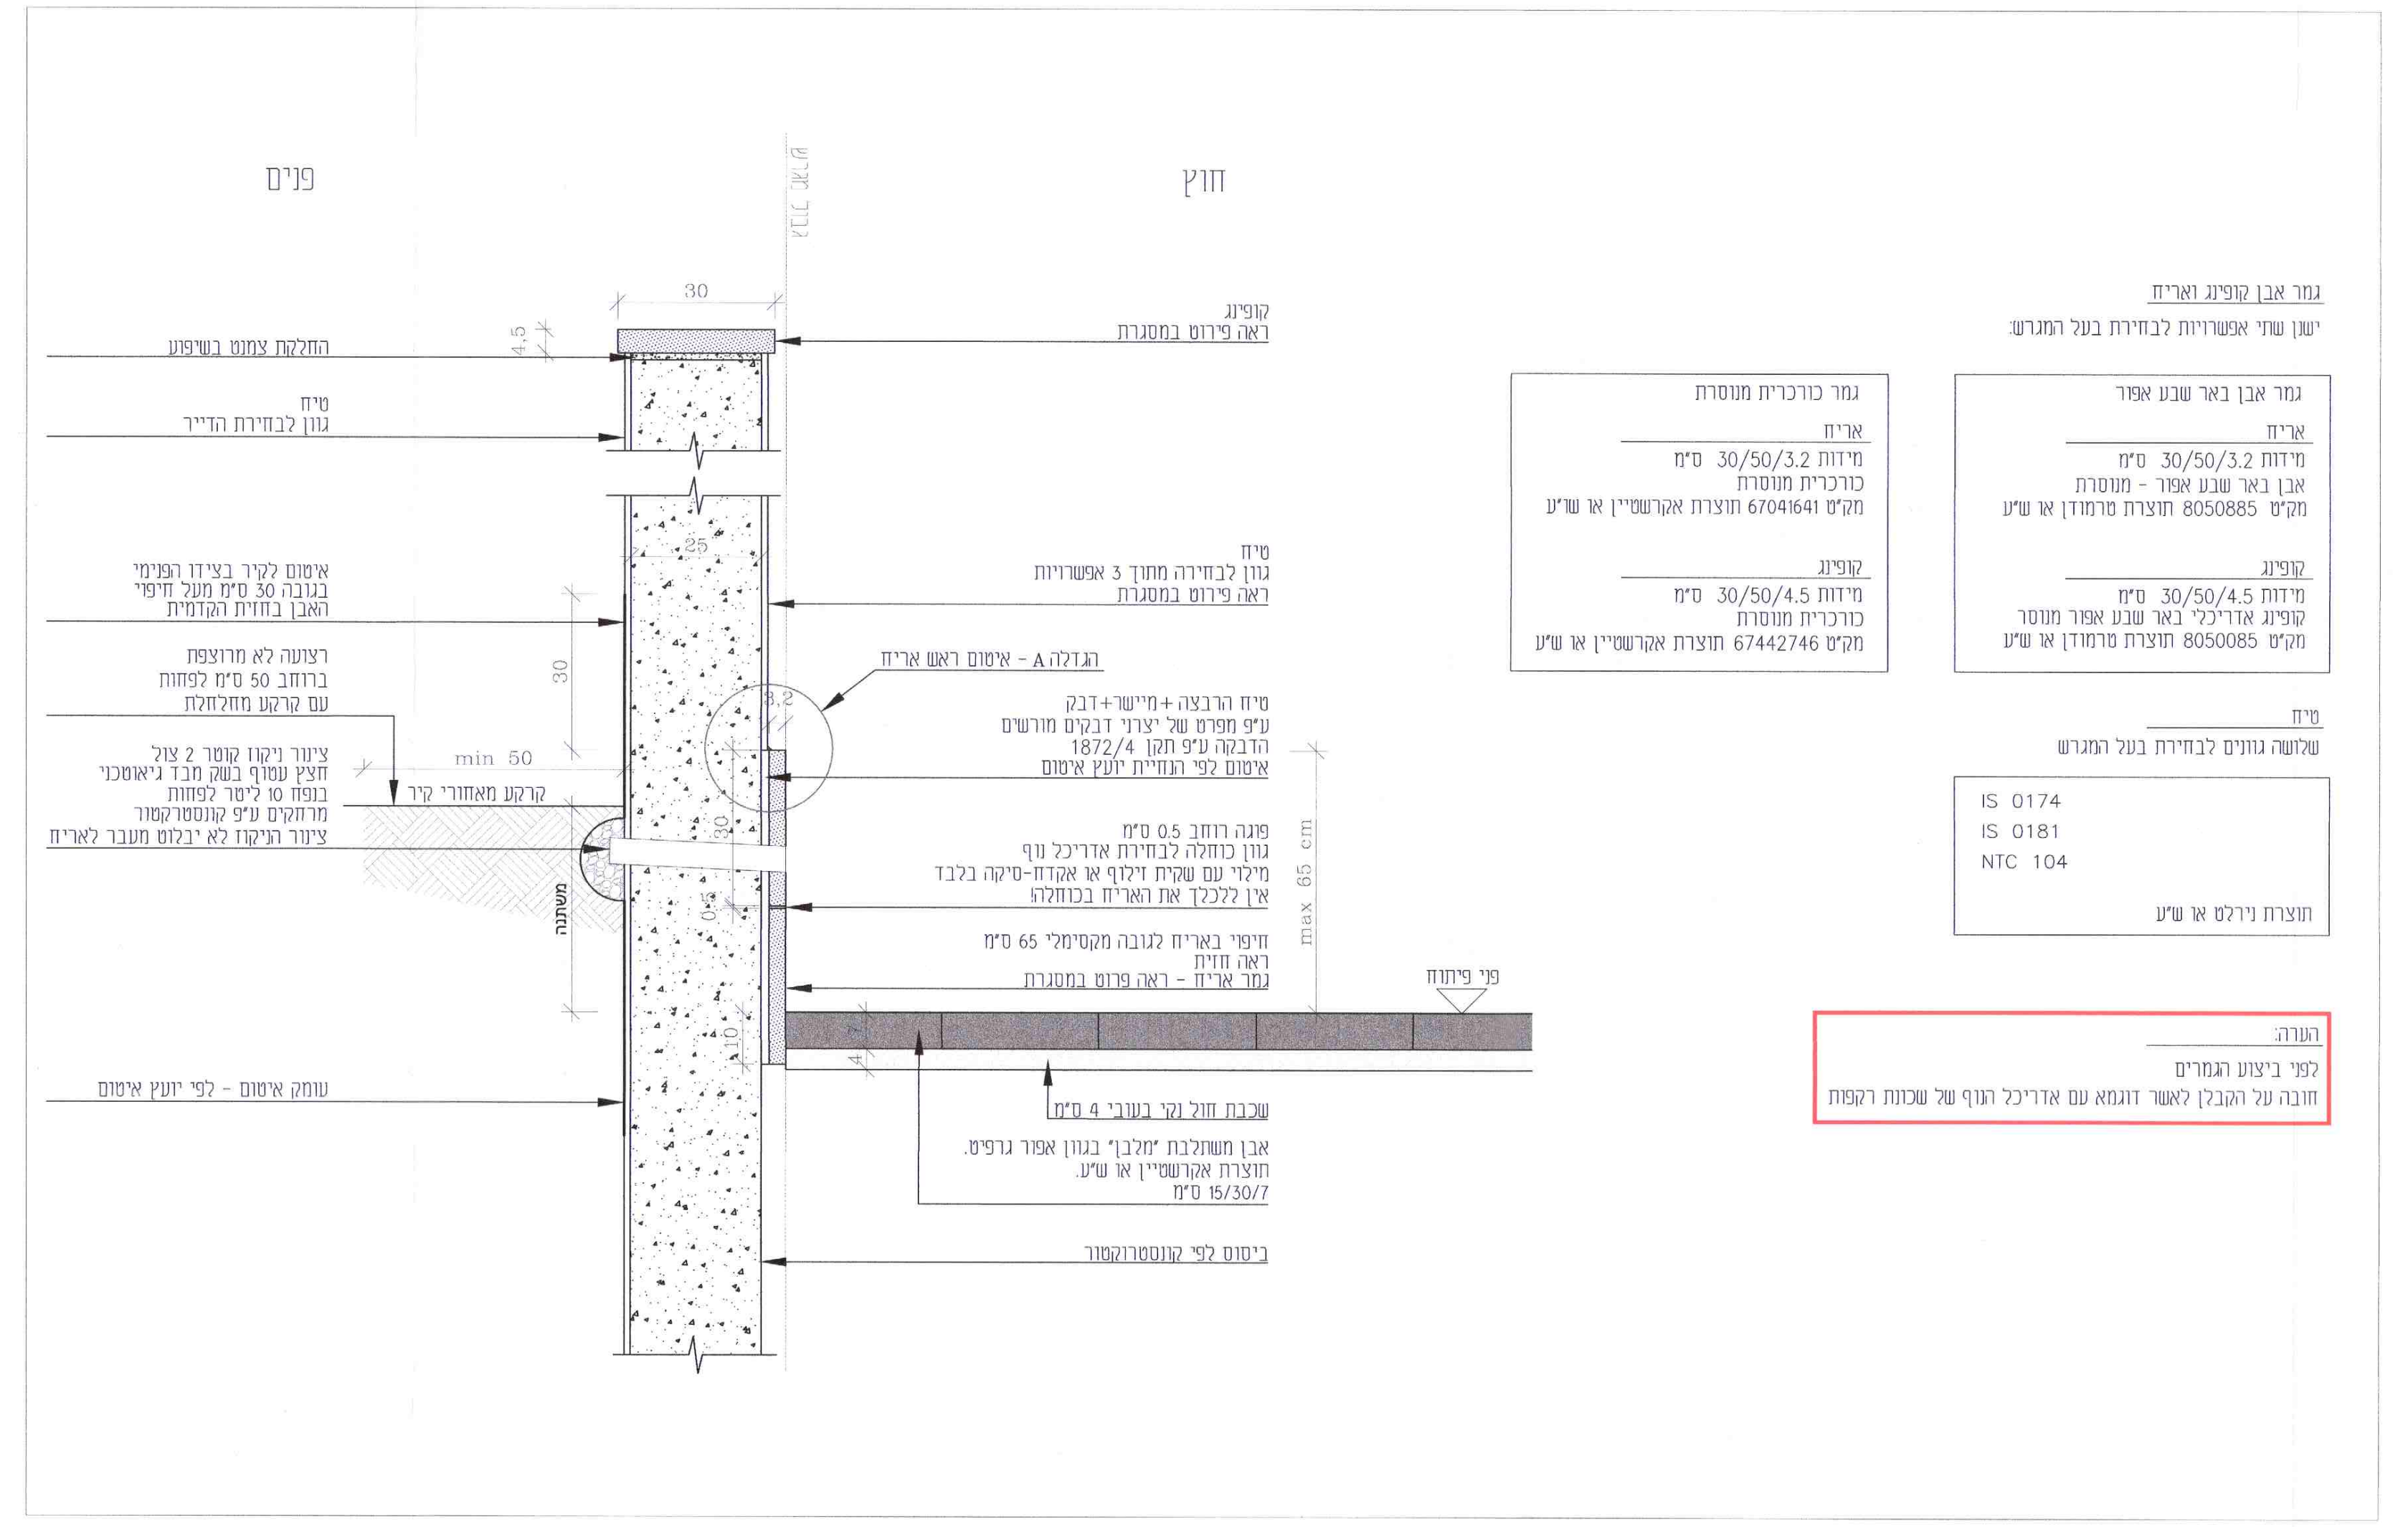

5.1 פרט גדר בנויה וצינור ניקוז 1:10

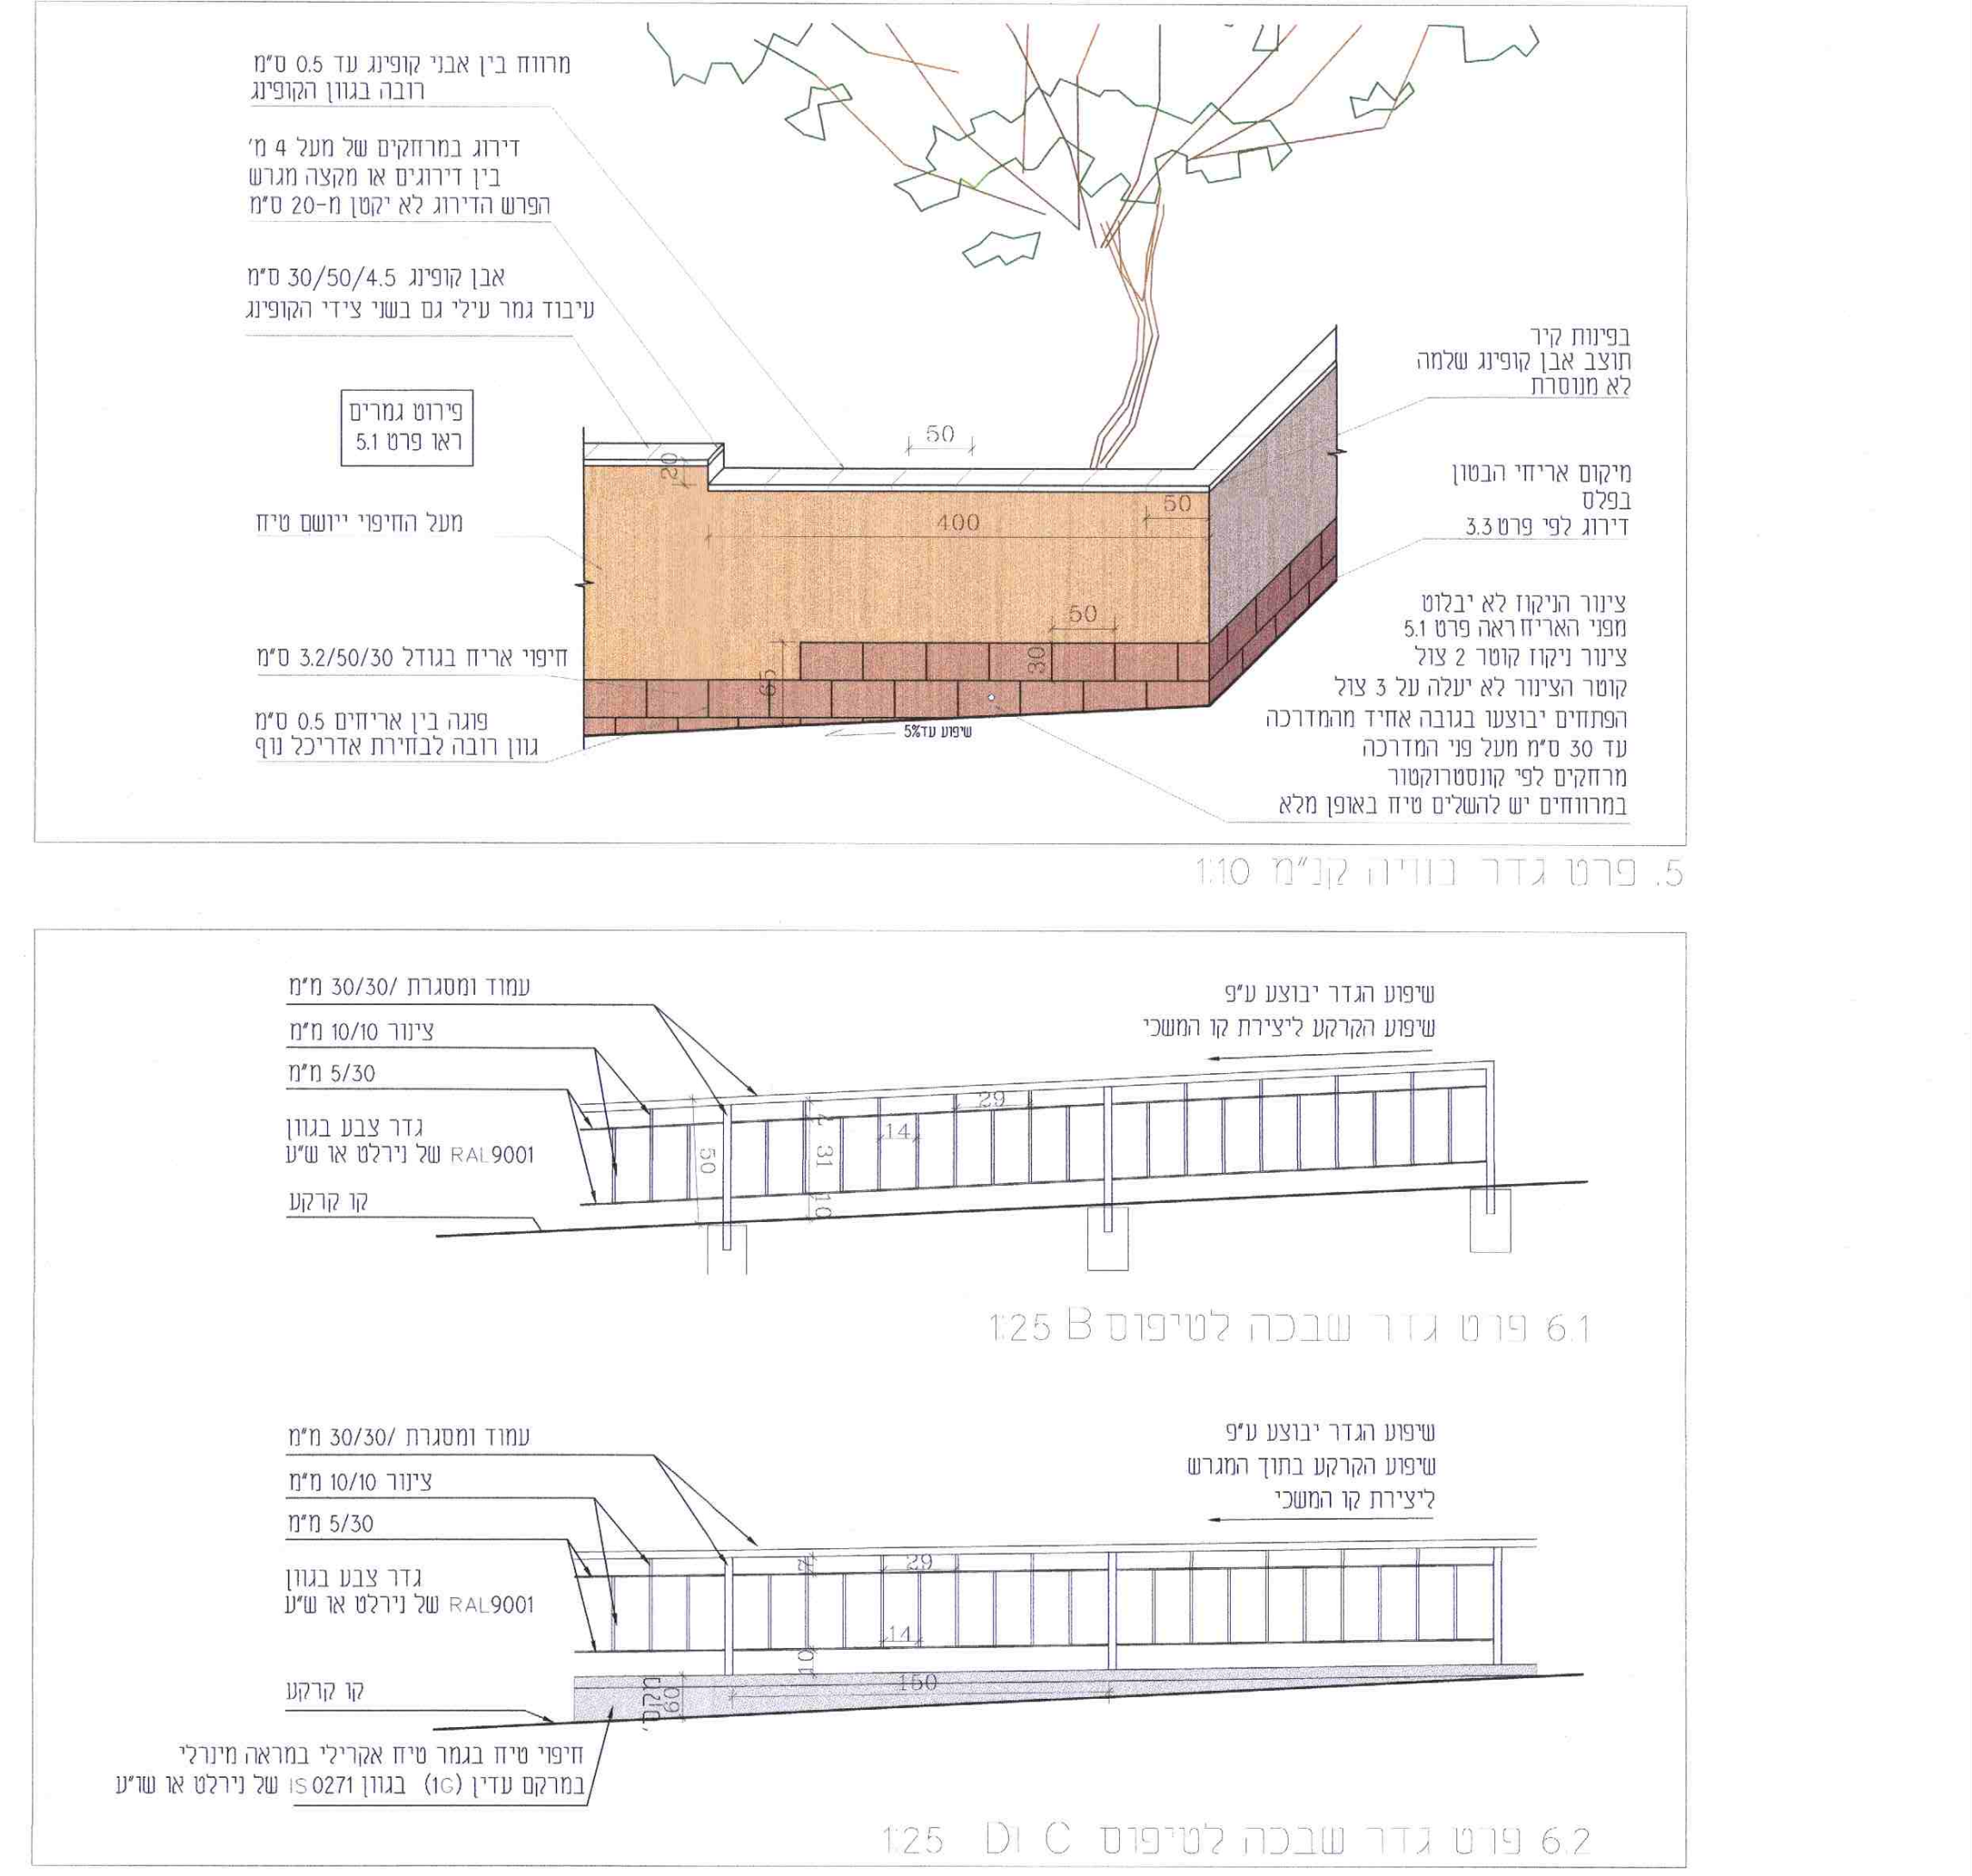

6. פרט גדר שבכה קנ"מ 1:25 - הפרט יאושר בהמשך על ידי העירייה