שכונת הרקפות
באר שבע

1.1

תכניות חזיתות וחתכים
טיפוס 1A

תאריך: 03.05.2022	קנ"מ: 1:200
מהדורה: 108	

6/3/24
אדר' מור שוייצר
צוות אדריכל העיר
עיריית באר שבע

אין התנגדות
9/08/2022
עיריית באר-שבע
אולגה חריטונוב
אגף הנדסה
מנהלת מחלקת
תיאום תשתיות דרכים ופיתוח

ועדה מקומית באר-שבע
אישור תוכנית מס' מגרש 1616 (2)
הועדה המקומית החליטה לאשר את התוכנית
בישיבה מס' 20230012 מיום 30/6/24

שלומי גומה
סגן ומ"מ ראש העיר
יו"ר ועדה לתכנון ובניה
עיריית באר שבע

אדר' תמר פוריה שרביט
מהנדסת העיר
באר שבע

0 2 -05- 2024

27-11-22
187-2022

מנהלת הסכם הגג
באר שבע

באר שבע
בירת ההזדמנויות של ישראל

מקרא :

━	גבול מגרש
- - -	קו בניין
⬚	חצר אפקטיבית
▒	חצר פרטית
▦	ריצוף/שביל
🟩	אשפה
-0.20	מפלס עקרוני בשטחים ציבוריים
+0.00	מפלס קומה
▼ 1	מס' חזית וסימונה
▨	שטח השהיה
▩	שביל כניסה ראשית

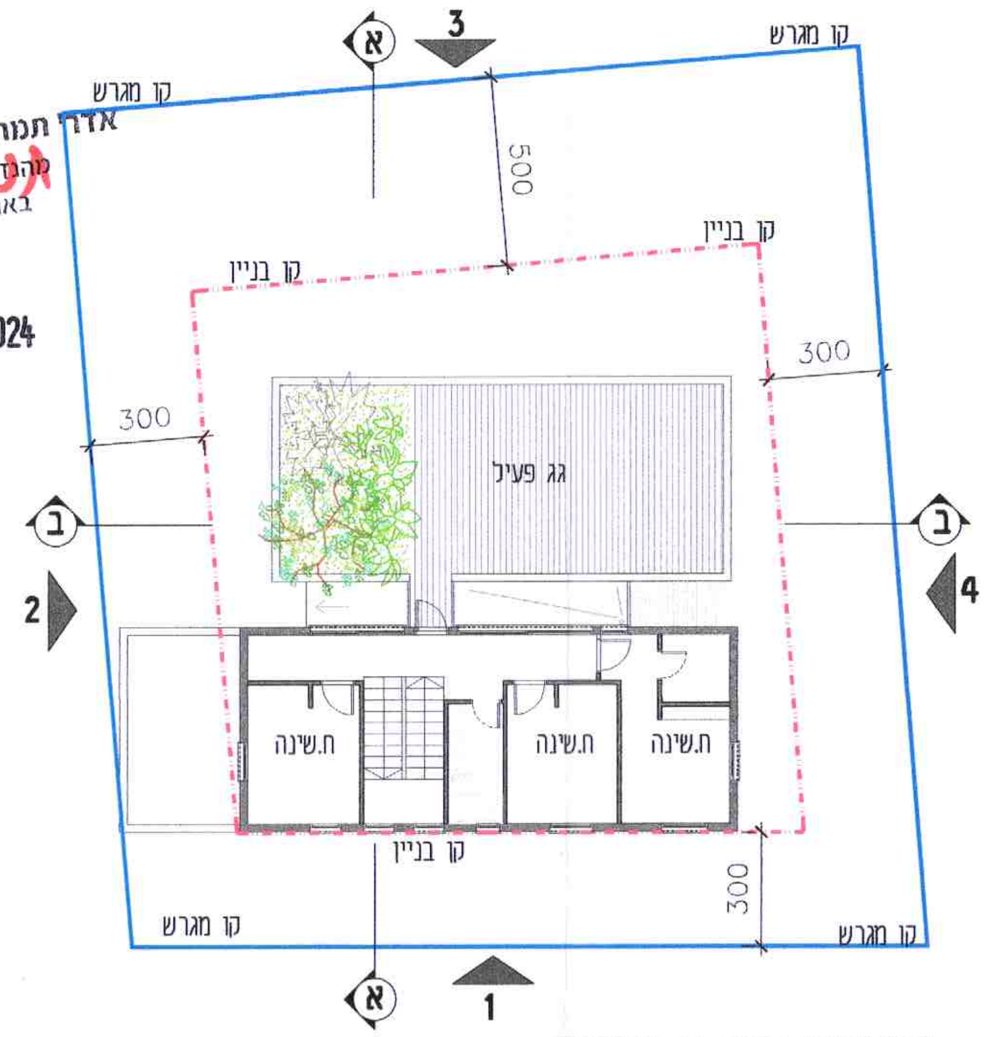

תוכנית קומה ראשונה

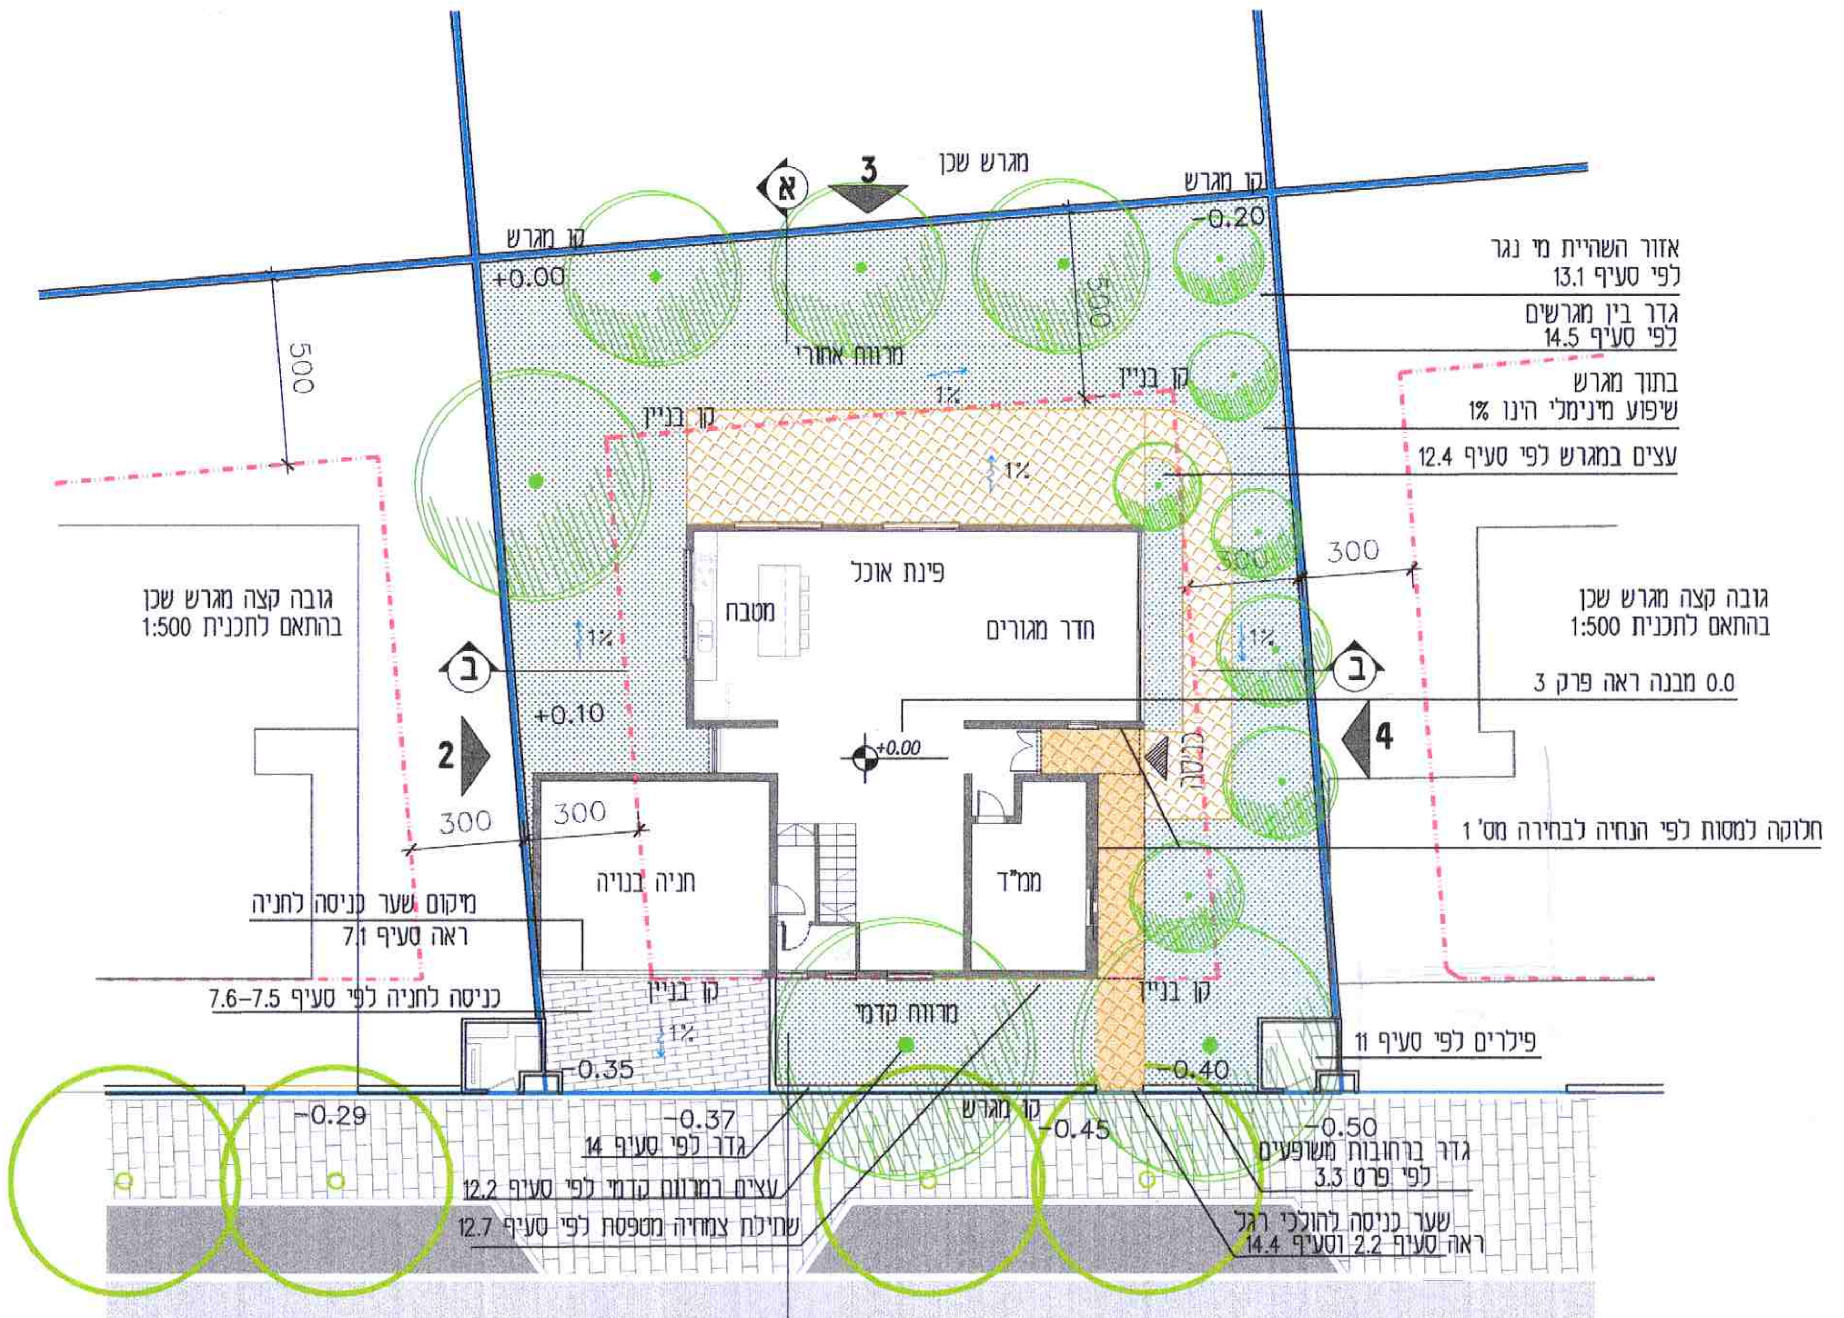

מגרש שכן
קו מגרש
קו בניין
+0.00
-0.20
500
300
מרווח אחורי
1%
פינת אוכל
מטבח
חדר מגורים
+0.10
+0.00
כניסה
חניה בנויה
ממ"ד
מרווח קדמי
-0.35
-0.29
-0.37
-0.45
-0.40
-0.50
אזור השהיית מי נגר לפי סעיף 13.1
גדר בין מגרשים לפי סעיף 14.5
בתוך מגרש שיפוע מינימלי הינו 1%
עצים במגרש לפי סעיף 12.4
גובה קצה מגרש שכן בהתאם לתכנית 1:500
0.0 מבנה ראה פרק 3
חלוקה למסות לפי הנחיה לבחירה מס' 1
פילרים לפי סעיף 11
מיקום שער כניסה לחניה ראה סעיף 7.1
כניסה לחניה לפי סעיף 7.5-7.6
גדר לפי סעיף 14
עצים במרווח קדמי לפי סעיף 12.2
שתילת צמחיה מטפסת לפי סעיף 12.7
גדר ברחובות משופעים לפי פרט 3.3
שער כניסה להולכי רגל ראה סעיף 2.2 וסעיף 14.4
א
ב
1
2
3
4

תוכנית קומת קרקע

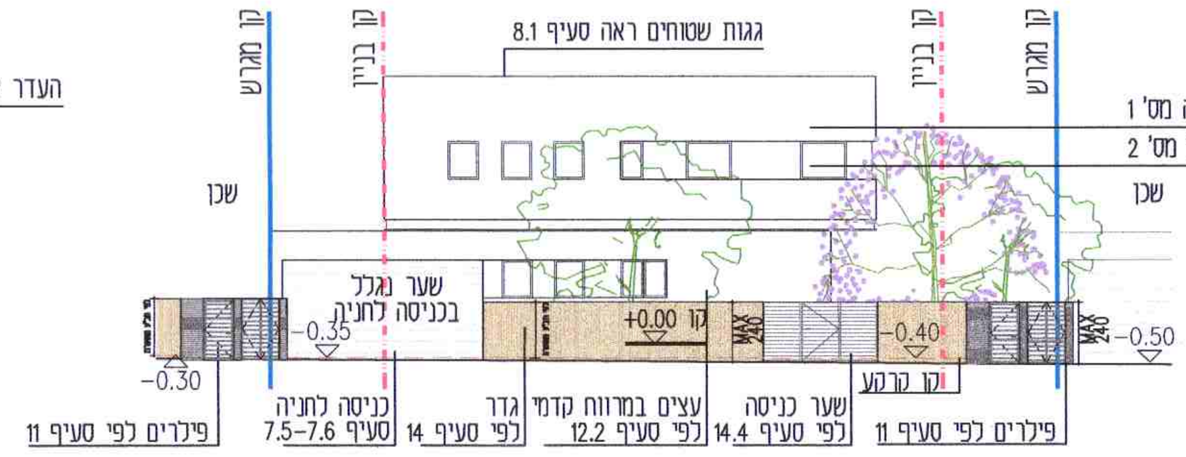

חזית 1

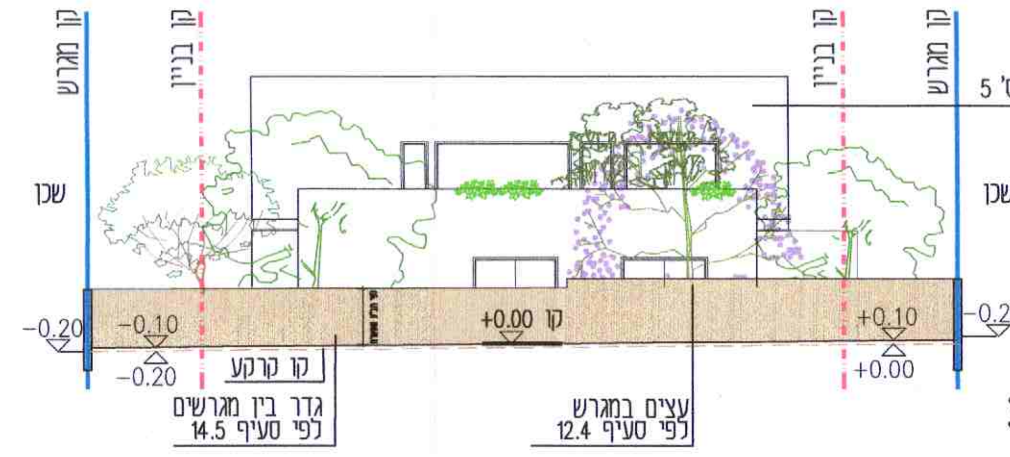

חזית 3

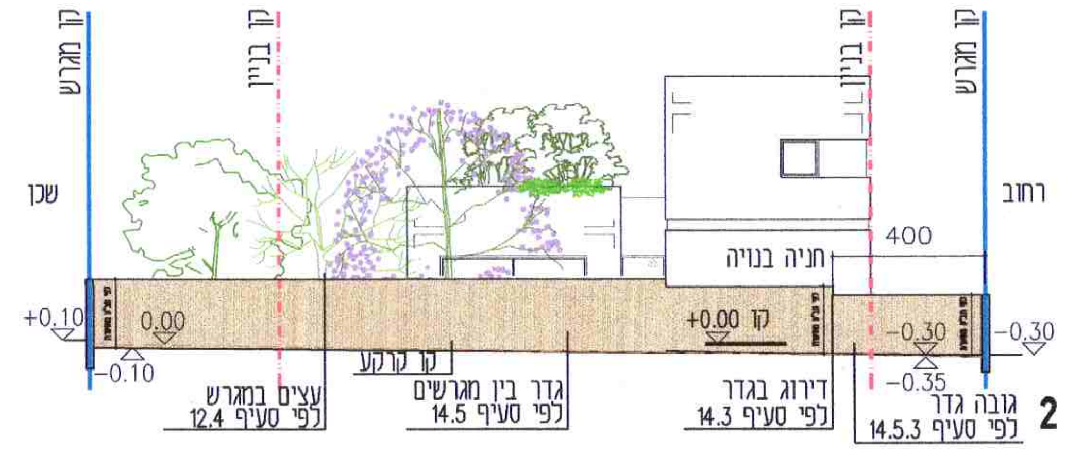

חזית 2

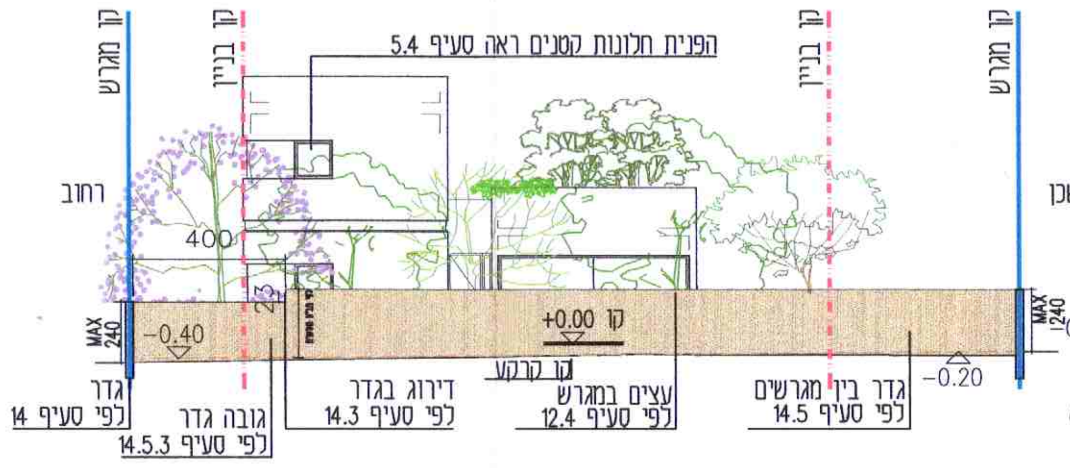

חזית 4

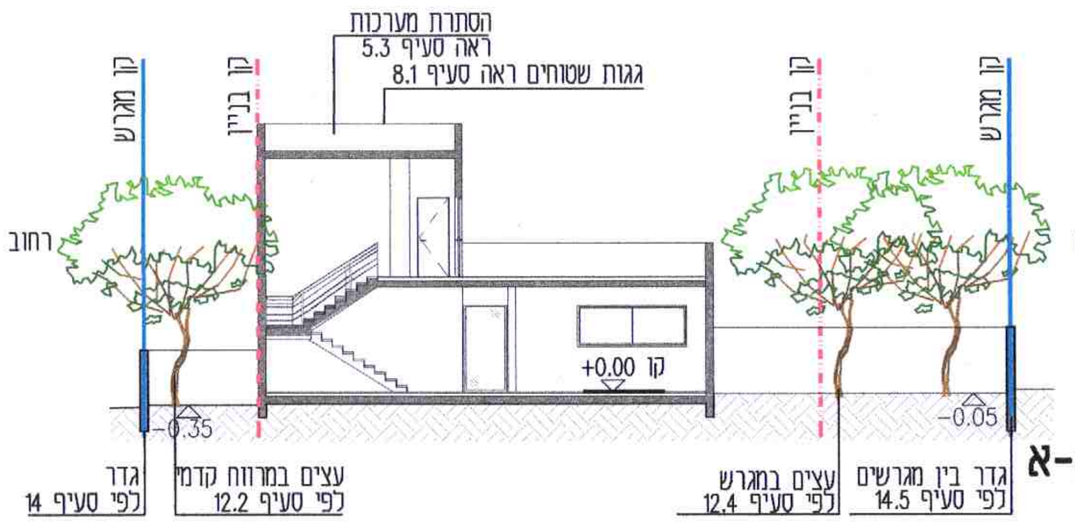

חתך א-א

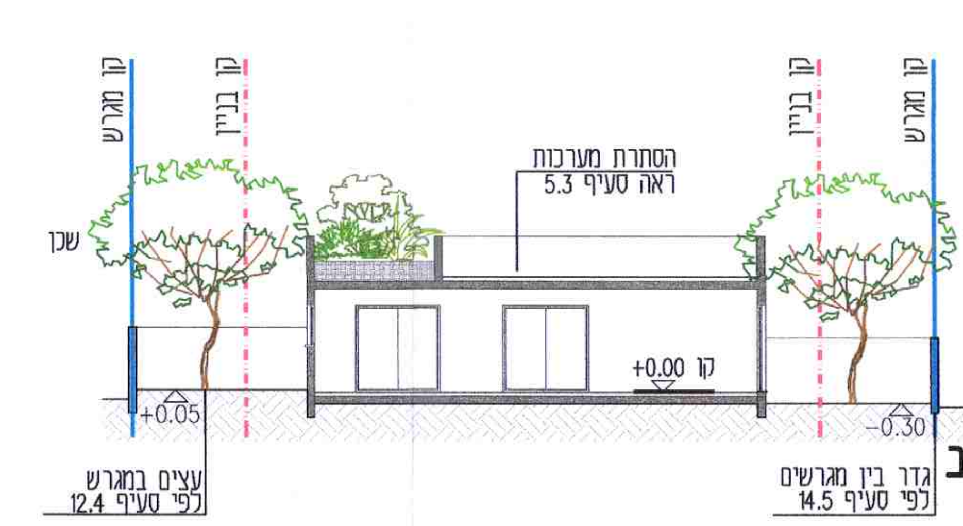

חתך ב-ב