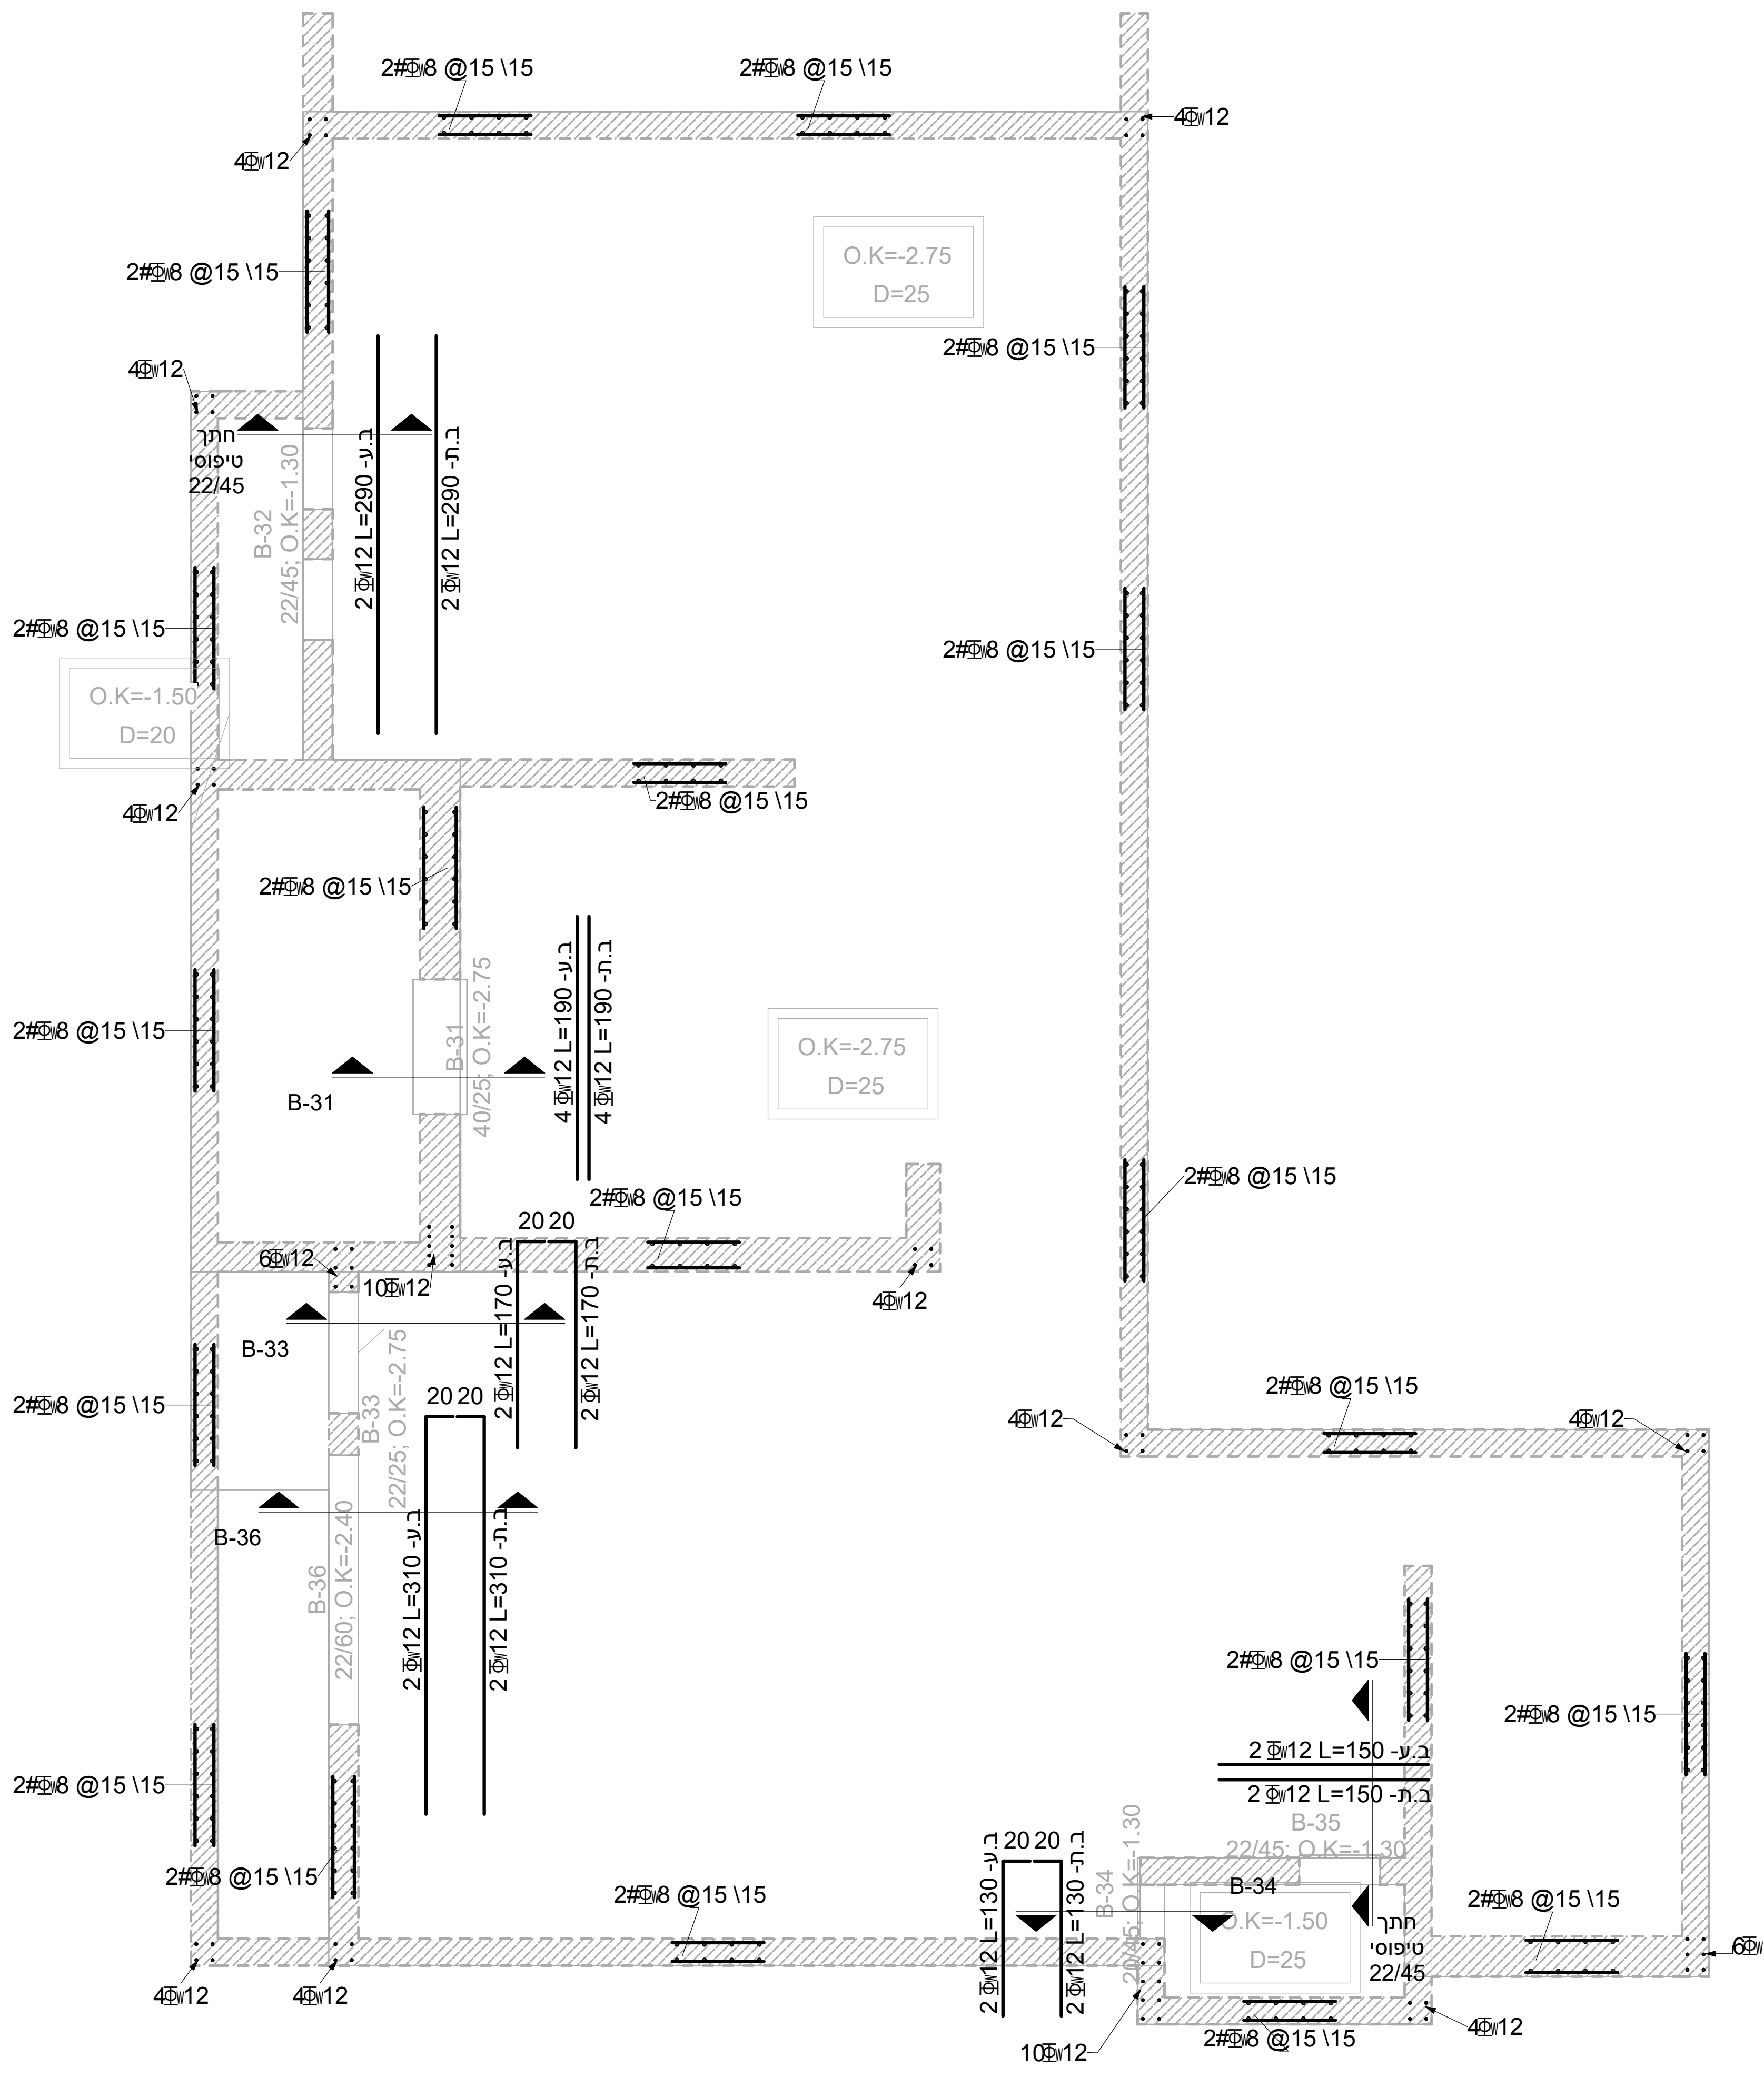
2#Φ8 @15 \15
4Φ12
6Φ12
10Φ12
O.K=-2.75
D=25
O.K=-1.50
D=20
חתך
טיפוסי
22/45
B-32
22/45; O.K=-1.30
ב.ע- 2Φ12 L=290
ב.ת- 2Φ12 L=290
B-31
40/25; O.K=-2.75
ב.ע- 4Φ12 L=190
ב.ת- 4Φ12 L=190
20 20
ב.ע- 2Φ12 L=170
ב.ת- 2Φ12 L=170
B-33
22/25; O.K=-2.75
B-36
22/60; O.K=-2.40
ב.ע- 2Φ12 L=310
ב.ת- 2Φ12 L=310
ב.ע- 2Φ12 L=150
ב.ת- 2Φ12 L=150
B-35
22/45; O.K=-1.30
B-34
20/45; O.K=-1.30
ב.ע- 2Φ12 L=130
ב.ת- 2Φ12 L=130

ברזל קורות קירות ועמודים

1 : 50

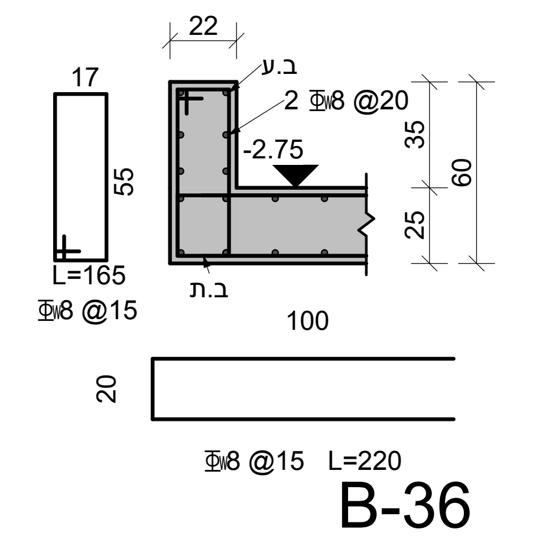
22
17
ב.ע
2 Φ8 @20
-2.75
55
35
60
25
L=165
Φ8 @15
ב.ת
100
20
Φ8 @15 L=220

B-36

1 : 25

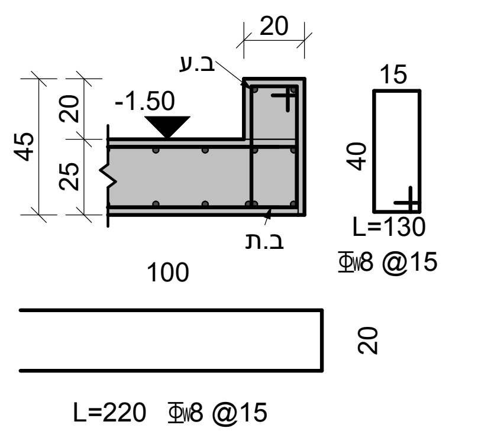
20
ב.ע
-1.50
15
45
20
25
40
L=130
Φ8 @15
ב.ת
100
20
L=220 Φ8 @15

B-34

1 : 25

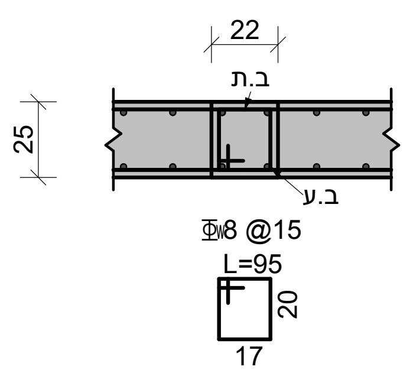
22
ב.ת
25
ב.ע
Φ8 @15
L=95
20
17

B-33

1 : 25

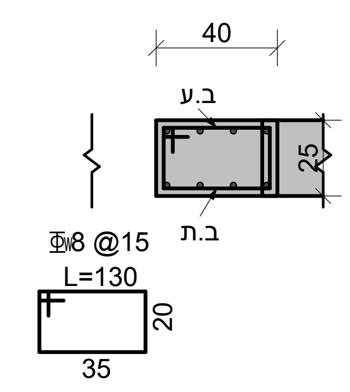
40
ב.ע
25
ב.ת
Φ8 @15
L=130
20
35

B-31

1 : 25

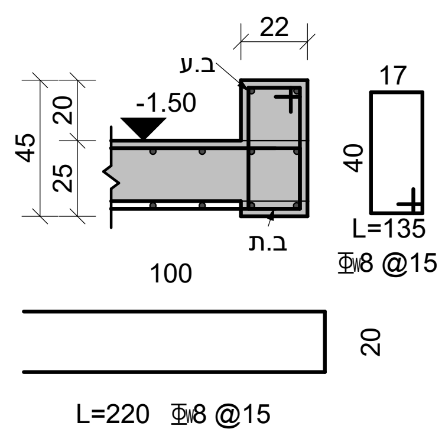
22
ב.ע
-1.50
17
45
20
25
40
L=135
Φ8 @15
ב.ת
100
20
L=220 Φ8 @15

חתך טיפוסי22/45

1 : 25

הערות

1. יש לקרוא תוכנית זו יחד עם תוכנית חשמל אינסטלציה ואיטום.
2. תכנית זאת מיועדת לביצוע רק במידה ומולאו שני תנאים בסיסיים:
   א .אישור האדריכל
   ב . התוכנית מתאימה להיתר הבניה)באישור המהנדס האחראי על הביצוע)
3. תוכנית זאת תבוצע רק לאחר חתימת האדריכל והמודד עליה המאשרים כי היא מתאימה להיתר בניה והתקנים מבחינת העמדת המבנים במגרש
4. מיקום המבנה ביחס למגרש יקבע ע" י המודד בהתאם לתוכנית העמדה של האדריכל.
5. עובי כיסוי הבטון יהיה2.5ס " מ בכל האלמנטים מלבד אלה שבאים במגע עם הקרקע - שם עובי הכיסוי יהיה4ס "מ.
6. הארקת יסוד -יש לעיין בתכנית יועץ חשמל.
7. אין להעביר צינורות בקוטר גדול מ-50מ "מ ללא אישור מהמהנדס המתכנן.
8. דוח קרקע הינו חלק בלתי נפרד מתכנית זו.
9. סוג בטון ב-30 דרגת חשיפה 3.
10. יש לבצע התאמה בין תכניות האדריכליות ושאר היועצים לבין תכנית זו - לפני ביצוע.
11. אין להעמיס את המרפסות הן לפני הבנייה , והן אחרי הבנייה בעומס הגדול מהמצויין בתכנית!
12. פירוק טפסות בכל שלב יהיה - אך ורק באישור בכתב ממתכנן הקונסטרוקציה.

▨ עמוד / קיר-צומח

■ עמוד / קיר-מפסיק

*סוגי בטון ראה ברשימת כמויות

מס 'עידכון	מהות העידכון	ע"י	תאריך
P0	תוכניות לביצוע		5.10.26

עומסים

עומס קבוע נוסף 500 =ק"ג /מ"ר

עומס שימושי 150 =ק"ג /מ"ר

עומס מרפסות 350=ק"ג /מ"ר

גובה מפלס)אדריכלות): -2.60

מפלס פני בטון: -2.75

P0 מעודכן לתאריך: 5.10.26

לעיון	לאישור	למכרז	לביצוע
○	○	○	●

שם הפרויקט:

וילה ליאור ואביחי אטואן

תאור השרטוט:

קומת מרתף -פריסת ברזל קורות

מס 'השרטוט:

K-12

מס 'פרויקט: WORK-167

קנ"מ:

דוא" ל: tal@yarin-eng.co.il

גודל גליון: 541 X 900

מהנדס אחראי: טל שי אטיאס

מהנדס: רותם מאיר

ירין הנדסה
טל אטיאס: 050-444-4730
tal@yarin-eng.co.il

YARIN
תכנון | ניהול | פיקוח מבנים

01/11/2026 10:16:00
C:\Users\LENOVO P340\Desktop\העבודה\תוכניות עבודות\רותם\work\רוויט\מודל רוויט\קובץ\cons\פתיחת תיקייה ריטאביחי אטואן\167-התחלתי.rvt