קיר מבטון מזוין ב-30

התפרים כל5מ') ראה פרט תפר בK-300)

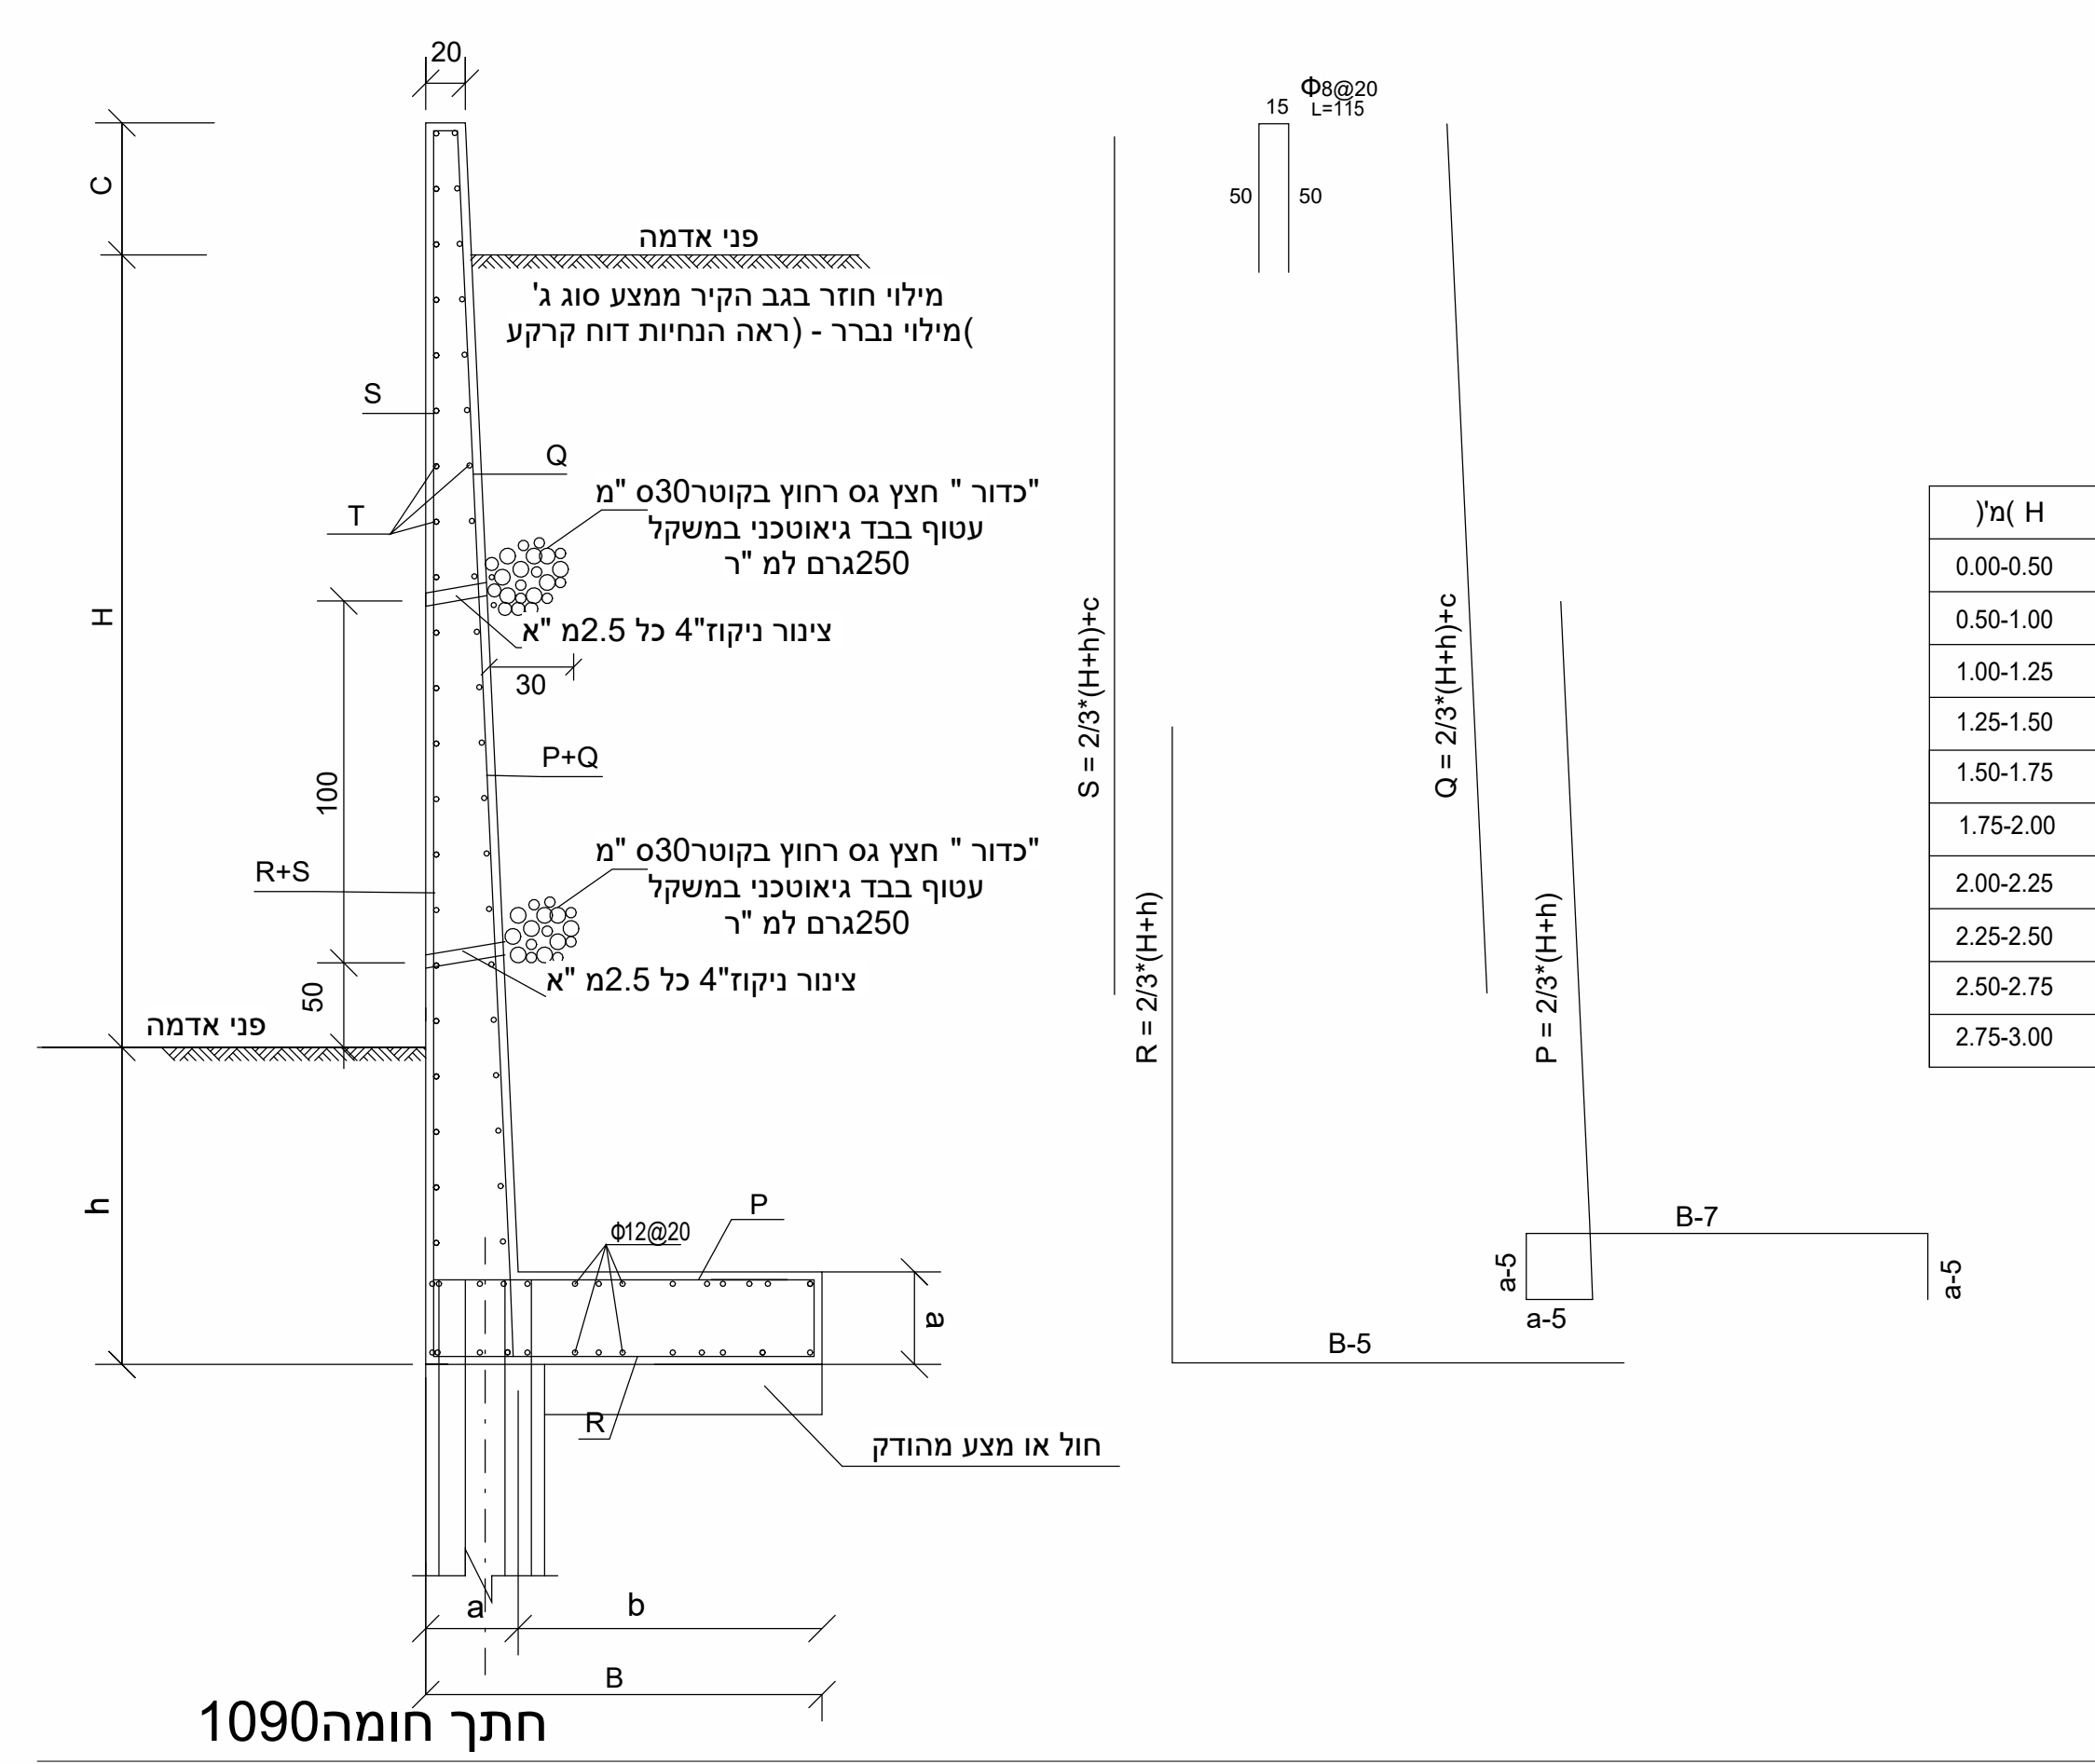
פני אדמה
מילוי חוזר בבג הקיר ממצע סוג א'
מילוי נברר - (ראה הנחיות דוח קרקע)
"כדור " מצע גס רחוץ בקוטר30o"מ עטוף בבד גיאוטכני במשקל 250גרם למ"ר
צינור ניקוז4" כל 2.5מ"א
פני אדמה
חול או מצע מהודק
P
Q
R
S
T
H
h
B
a
b
B-5
B-7
a-5

חתך חומה1090

1 : 25

זיון)מ'(H	L	h	B	a	b	P	Q	R	S
0.00-0.50	6.00	0.60	0	0.20	0	Φ8@20	Φ8@20Φ 6.5@20)	Φ8@15Φ 8@20)	Φ8@20Φ 6.5@20)
0.50-1.00	6.00	0.60	0.80	0.20	0.60	Φ8@20	Φ8@20Φ 6.5@20)	Φ8@15Φ 8@20)	Φ8@20Φ 6.5@20)
1.00-1.25	6.00	0.60	1.20	0.20	1.00	Φ8@15	Φ8@20Φ 6.5@20)	Φ8@15Φ 8@20)	Φ8@20Φ 6.5@20)
1.25-1.50	3.00	0.60	1.20	0.20	1.00	Φ8@10	Φ8@20Φ 6.5@20)	Φ8@15Φ 8@20)	Φ8@20Φ 6.5@20)
1.50-1.75	3.00	0.60	1.20	0.20	1.00	Φ10@15	Φ10@25Φ 8@20)	Φ8@15Φ 8@20)	Φ8@20Φ 6.5@20)
1.75-2.00	3.00	0.60	1.20	0.20	1.00	Φ10@10	Φ10@25Φ 8@20)	Φ8@15Φ 8@20)	Φ8@20Φ 6.5@20)
2.00-2.25	3.00	0.60	2.05	0.25	1.80	Φ12@12.5	Φ10@20Φ 8@20)	Φ10@15Φ 10@20)	Φ10@25Φ 8@20)
2.25-2.50	3.00	0.60	2.05	0.25	1.80	Φ12@10	Φ10@20Φ 8@20)	Φ10@15Φ 10@20)	Φ10@25Φ 8@20)
2.50-2.75	3.00	0.60	2.05	0.25	1.80	Φ12@10	Φ10@20Φ 8@20)	Φ10@15Φ 10@20)	Φ10@25Φ 8@20)
2.75-3.00	3.00	0.60	2.05	0.25	1.80	Φ14@10	Φ10@15Φ 8@15)	Φ10@15Φ 10@20)	Φ10@25Φ 8@20)

פרט חיבור ראש כלונס טיפוסי

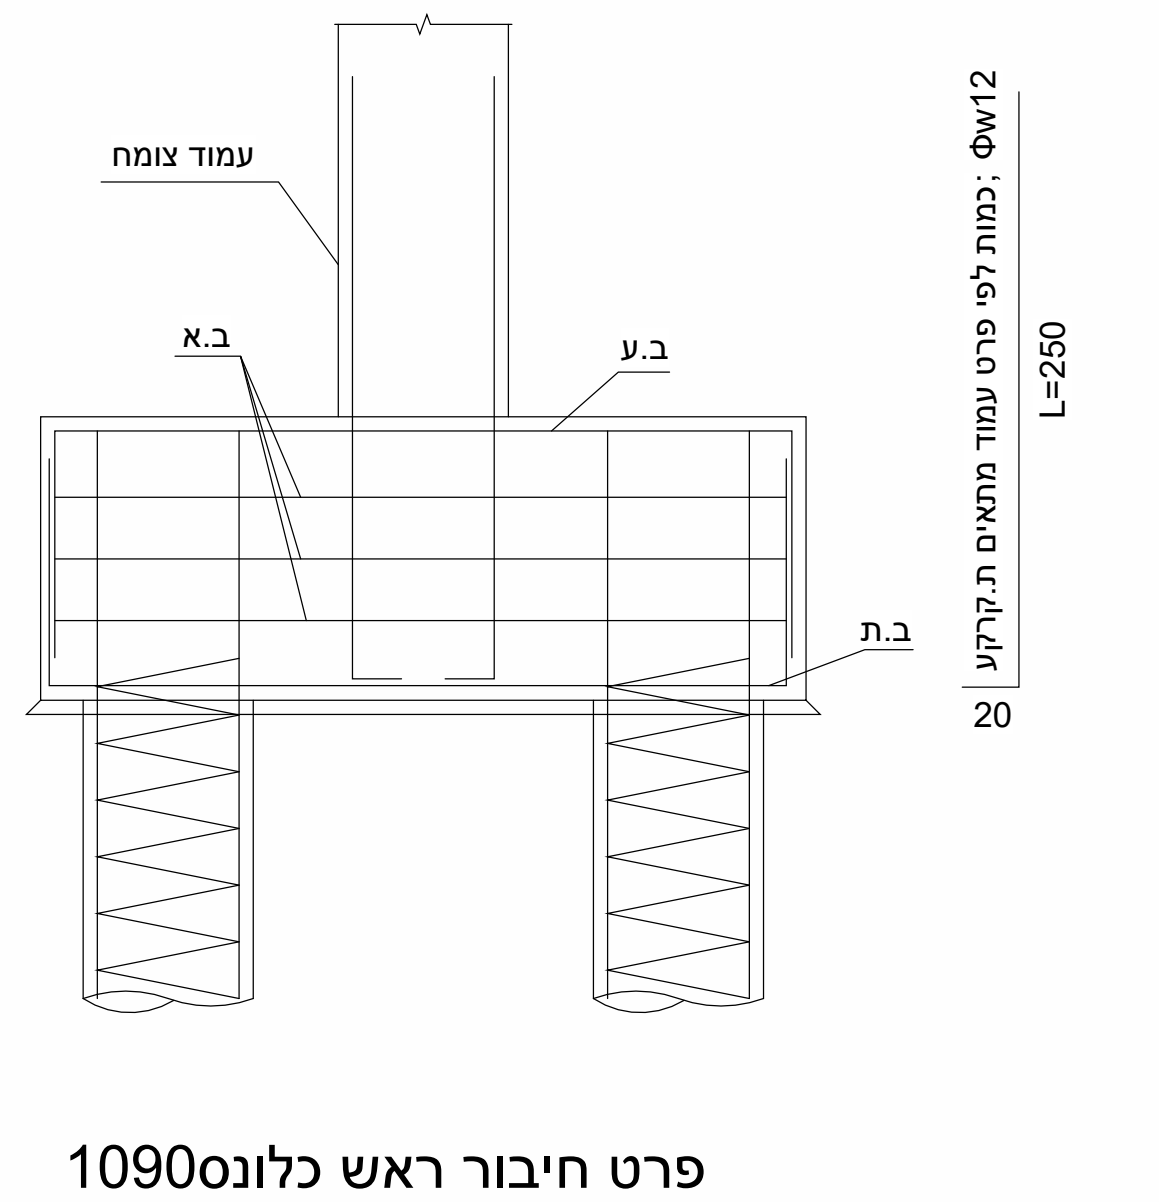
עמוד צומח
ב.א
ב.ע
ב.ת
20
Φw12 ;כמות לפי זיון עמוד מוצא ת.קרקע
L=250
100
Φw12 ;כמות לפי זיון הכלונס
L=250

פרט חיבור ראש כלונס1090

1 : 25

פרט חיבור בין קיר בטון לכלונס

1:25 ק.מ

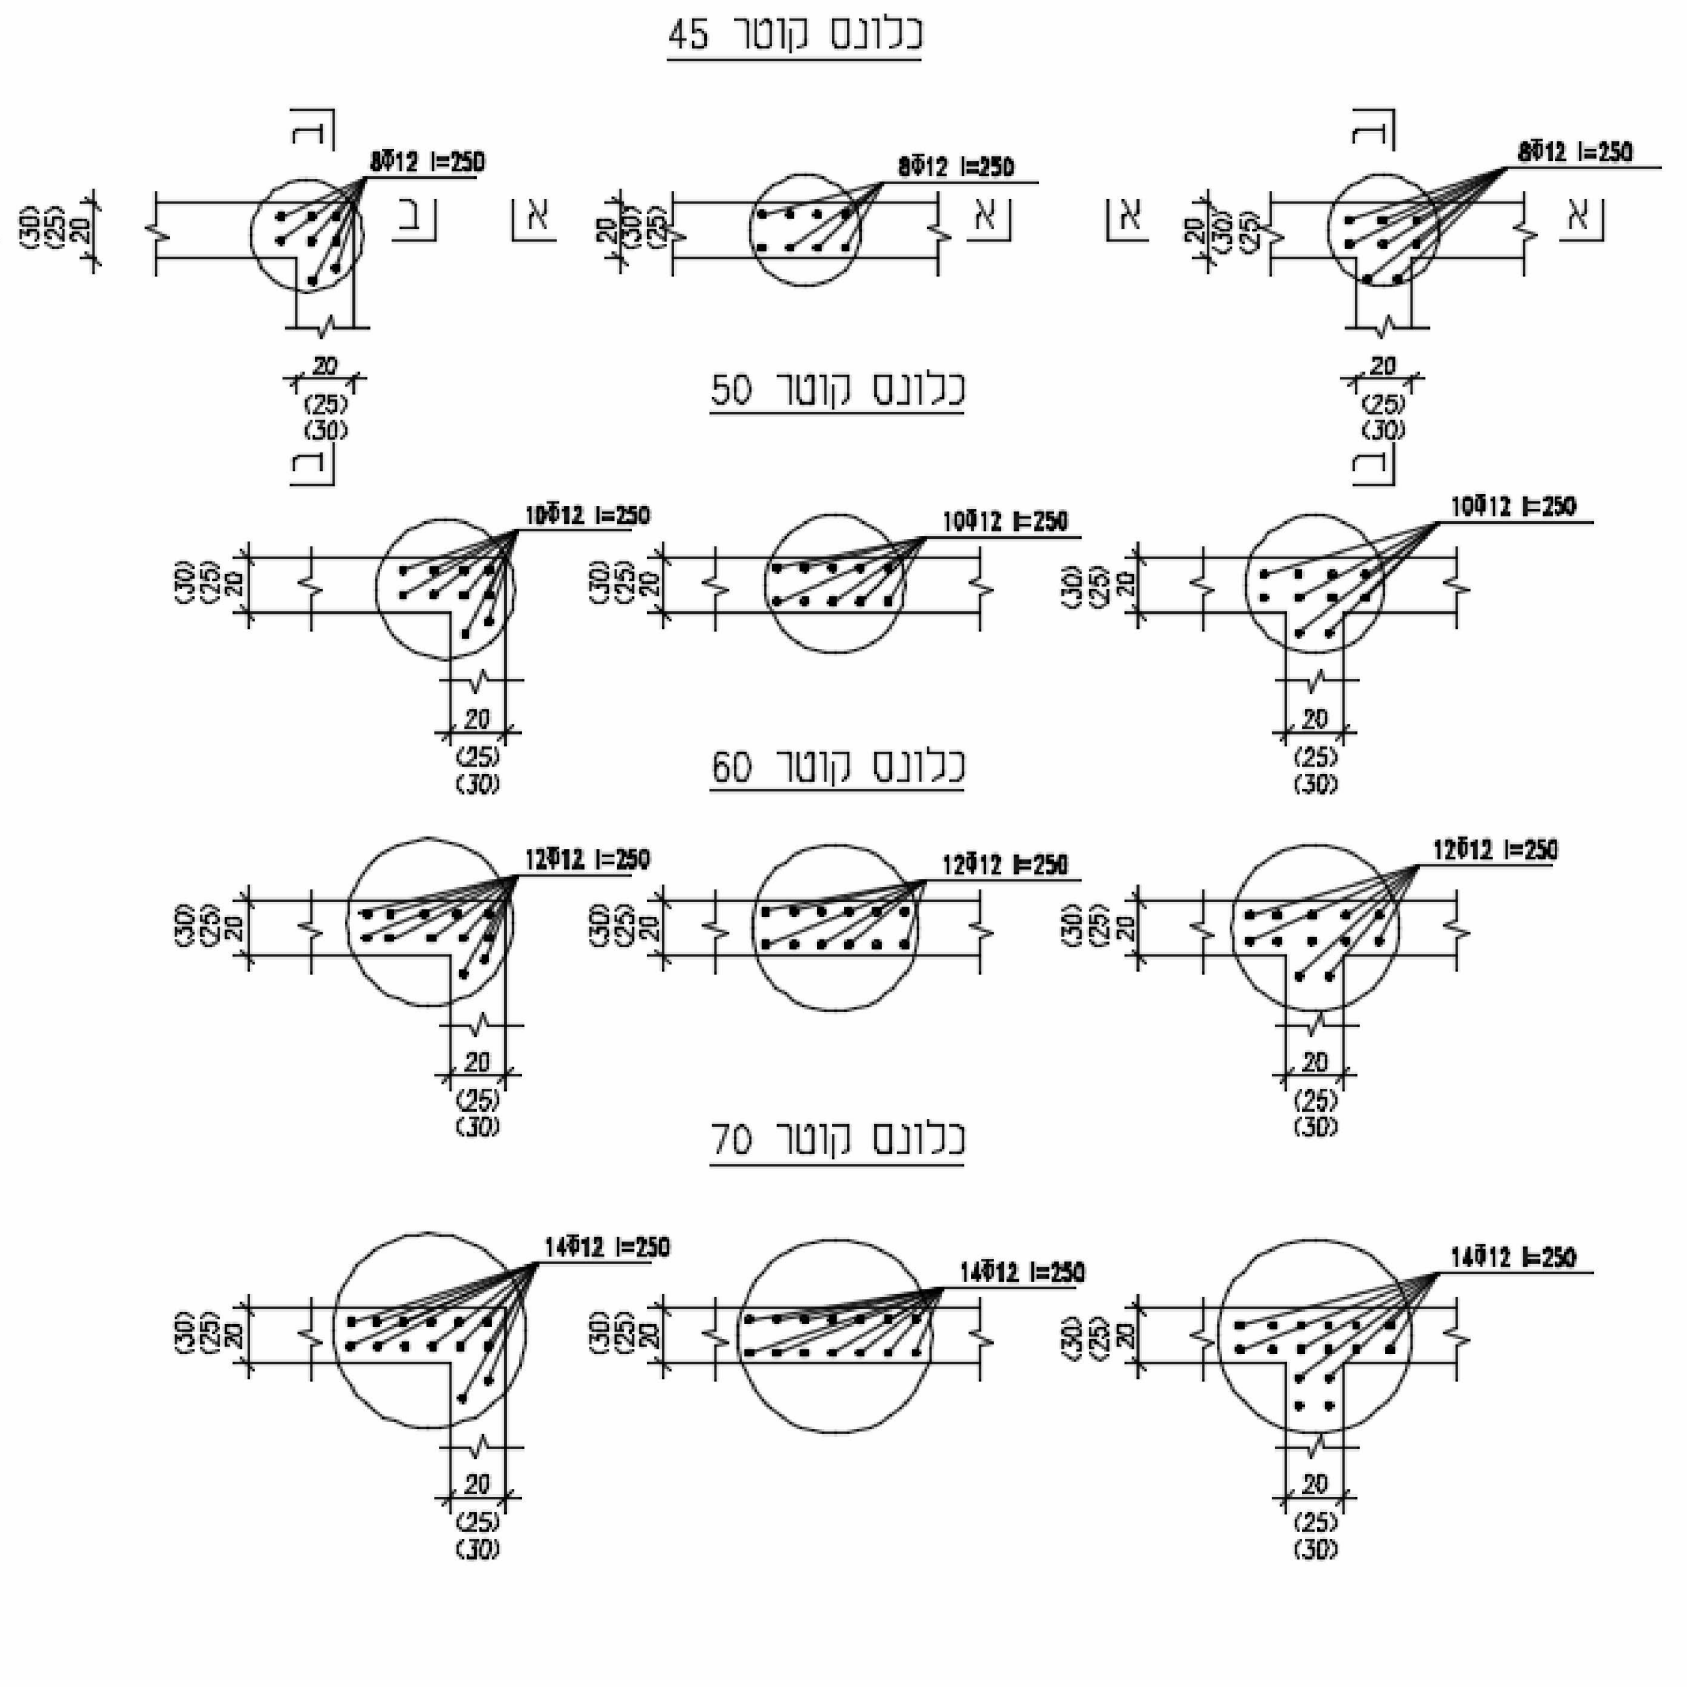

1:25

1-המפקח באתר יוודא את עומק הכלונסאות, אנכיותם (בעזרת פלסים) ומרכזיותם בתחילת הקדיחה ובגמר המטר הראשון. הקידוח המבוצע לא יסטה יותר מ-1% מהאנך, כן לא יסטה המרכז המבוצע מעל ל-3% קוטר הכלונס מהמרכז המתוכנן. סטיות ובליטות (מעל ל-5 ס"מ) יסותתו ע"י הקבלן ו על חשבונו.

2-הבטון בכלונסאות יהיה ב 30 בעל שקיעת הקונוס של 6". דרגת סומך זו הכרחית לעטיפה נאותה של הזיון.

3-יציקה כל כלונס תהיה רצופה ותבוצע מיד עם תום הקדיחה. היציקה תבוצע באמצעות צינור היורד 2 מ' לפחות בתוך הקידוח.

4-קוטר המקדח יהיה זהה לקוטר המפורט לתכנית היסודות.

5-מהנדס הביסוסיאשר את תכנית היסודות ויאשר את הכלונסאות הראשונים באתר בטרם יציקתם.

6-קבלן הקידוחים יביא בחשבון הצורך בשימוש בצינור מגן עליון באורך עד מטר.

7-קבלן הקידוחים יצטייד במכונת קידוח חזקה ומקדחים סגורים כדי למנוע נפילת חול מהמקדח.

8-ביציע קידוחים יעשה בהשגחה של מפקח צמוד באתר בעל הכשרה מקצועית נאותה, אשר יהיה נוכח בכל מהלך העבודה, יאשר יציקת כל יסוד וידווח למהנדס הביסוס.

***המבצע אחראי לבדיקת כל המידות. על כל טעות או אי התאמה עליו להודיע למהנדס. אין לקבוע מידה ע"י מדידה בשרטוט. התכניות נשארות רכוש הפרטי של המהנדס.

פרט רצפה תלויה

1 : 20

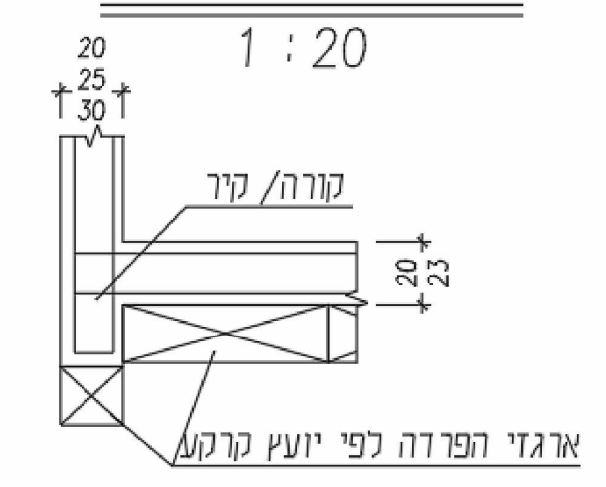

פרט חיבור בין רצפה לקיר(קורה)

1 : 25

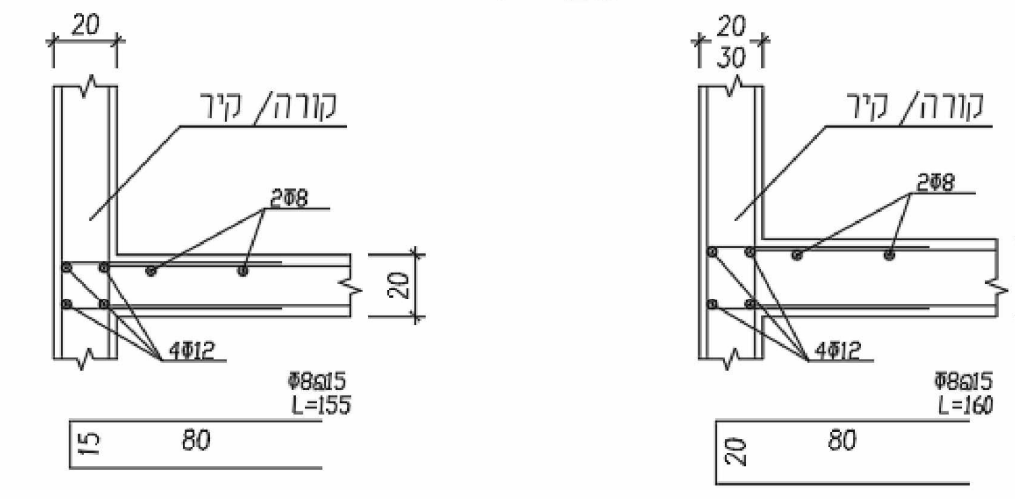

אזור חתך קורה על כלונס

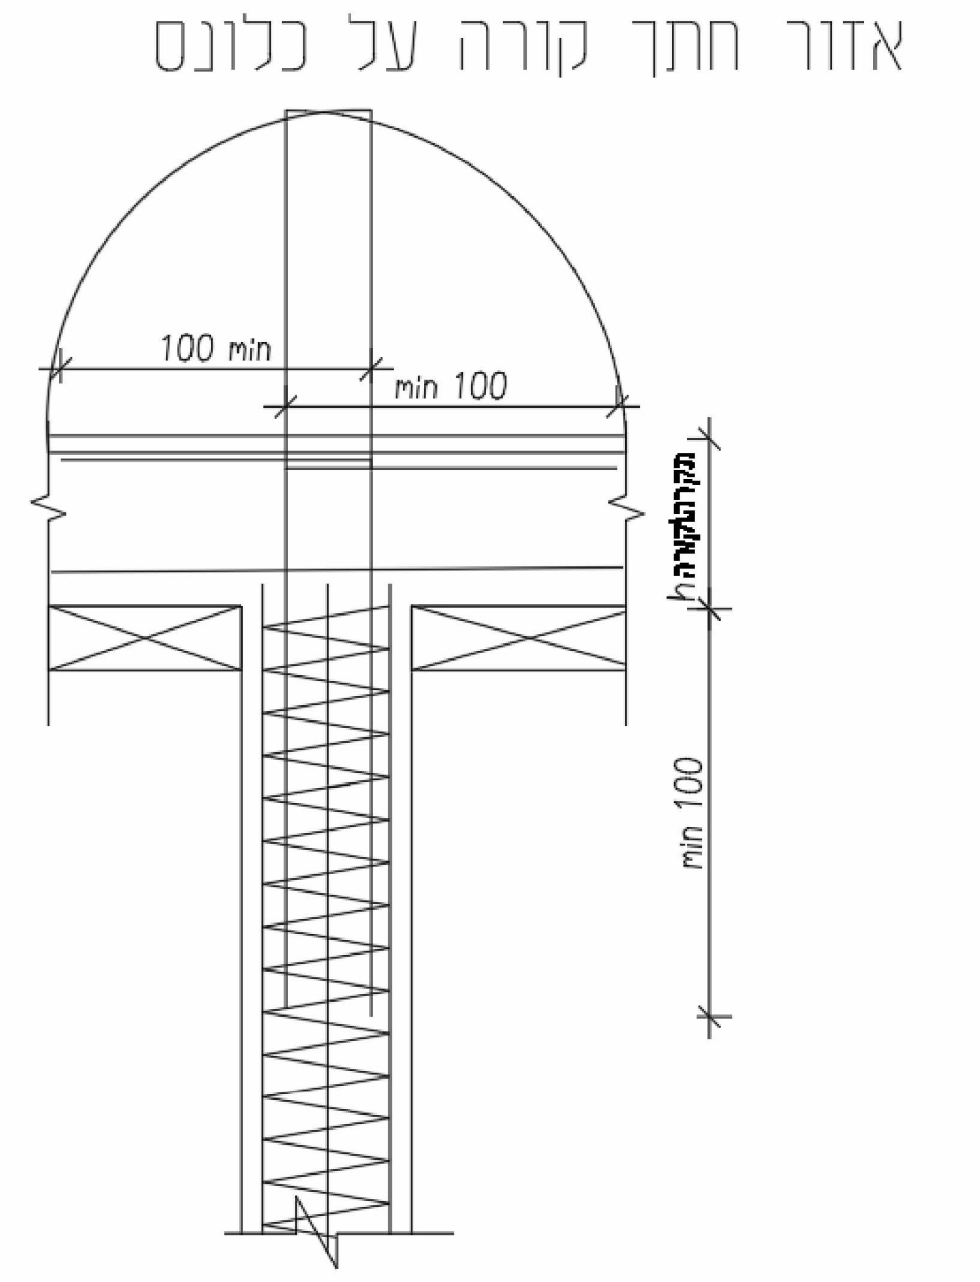

פרט כלונס טיפוסי מתחת לקורת יסוד

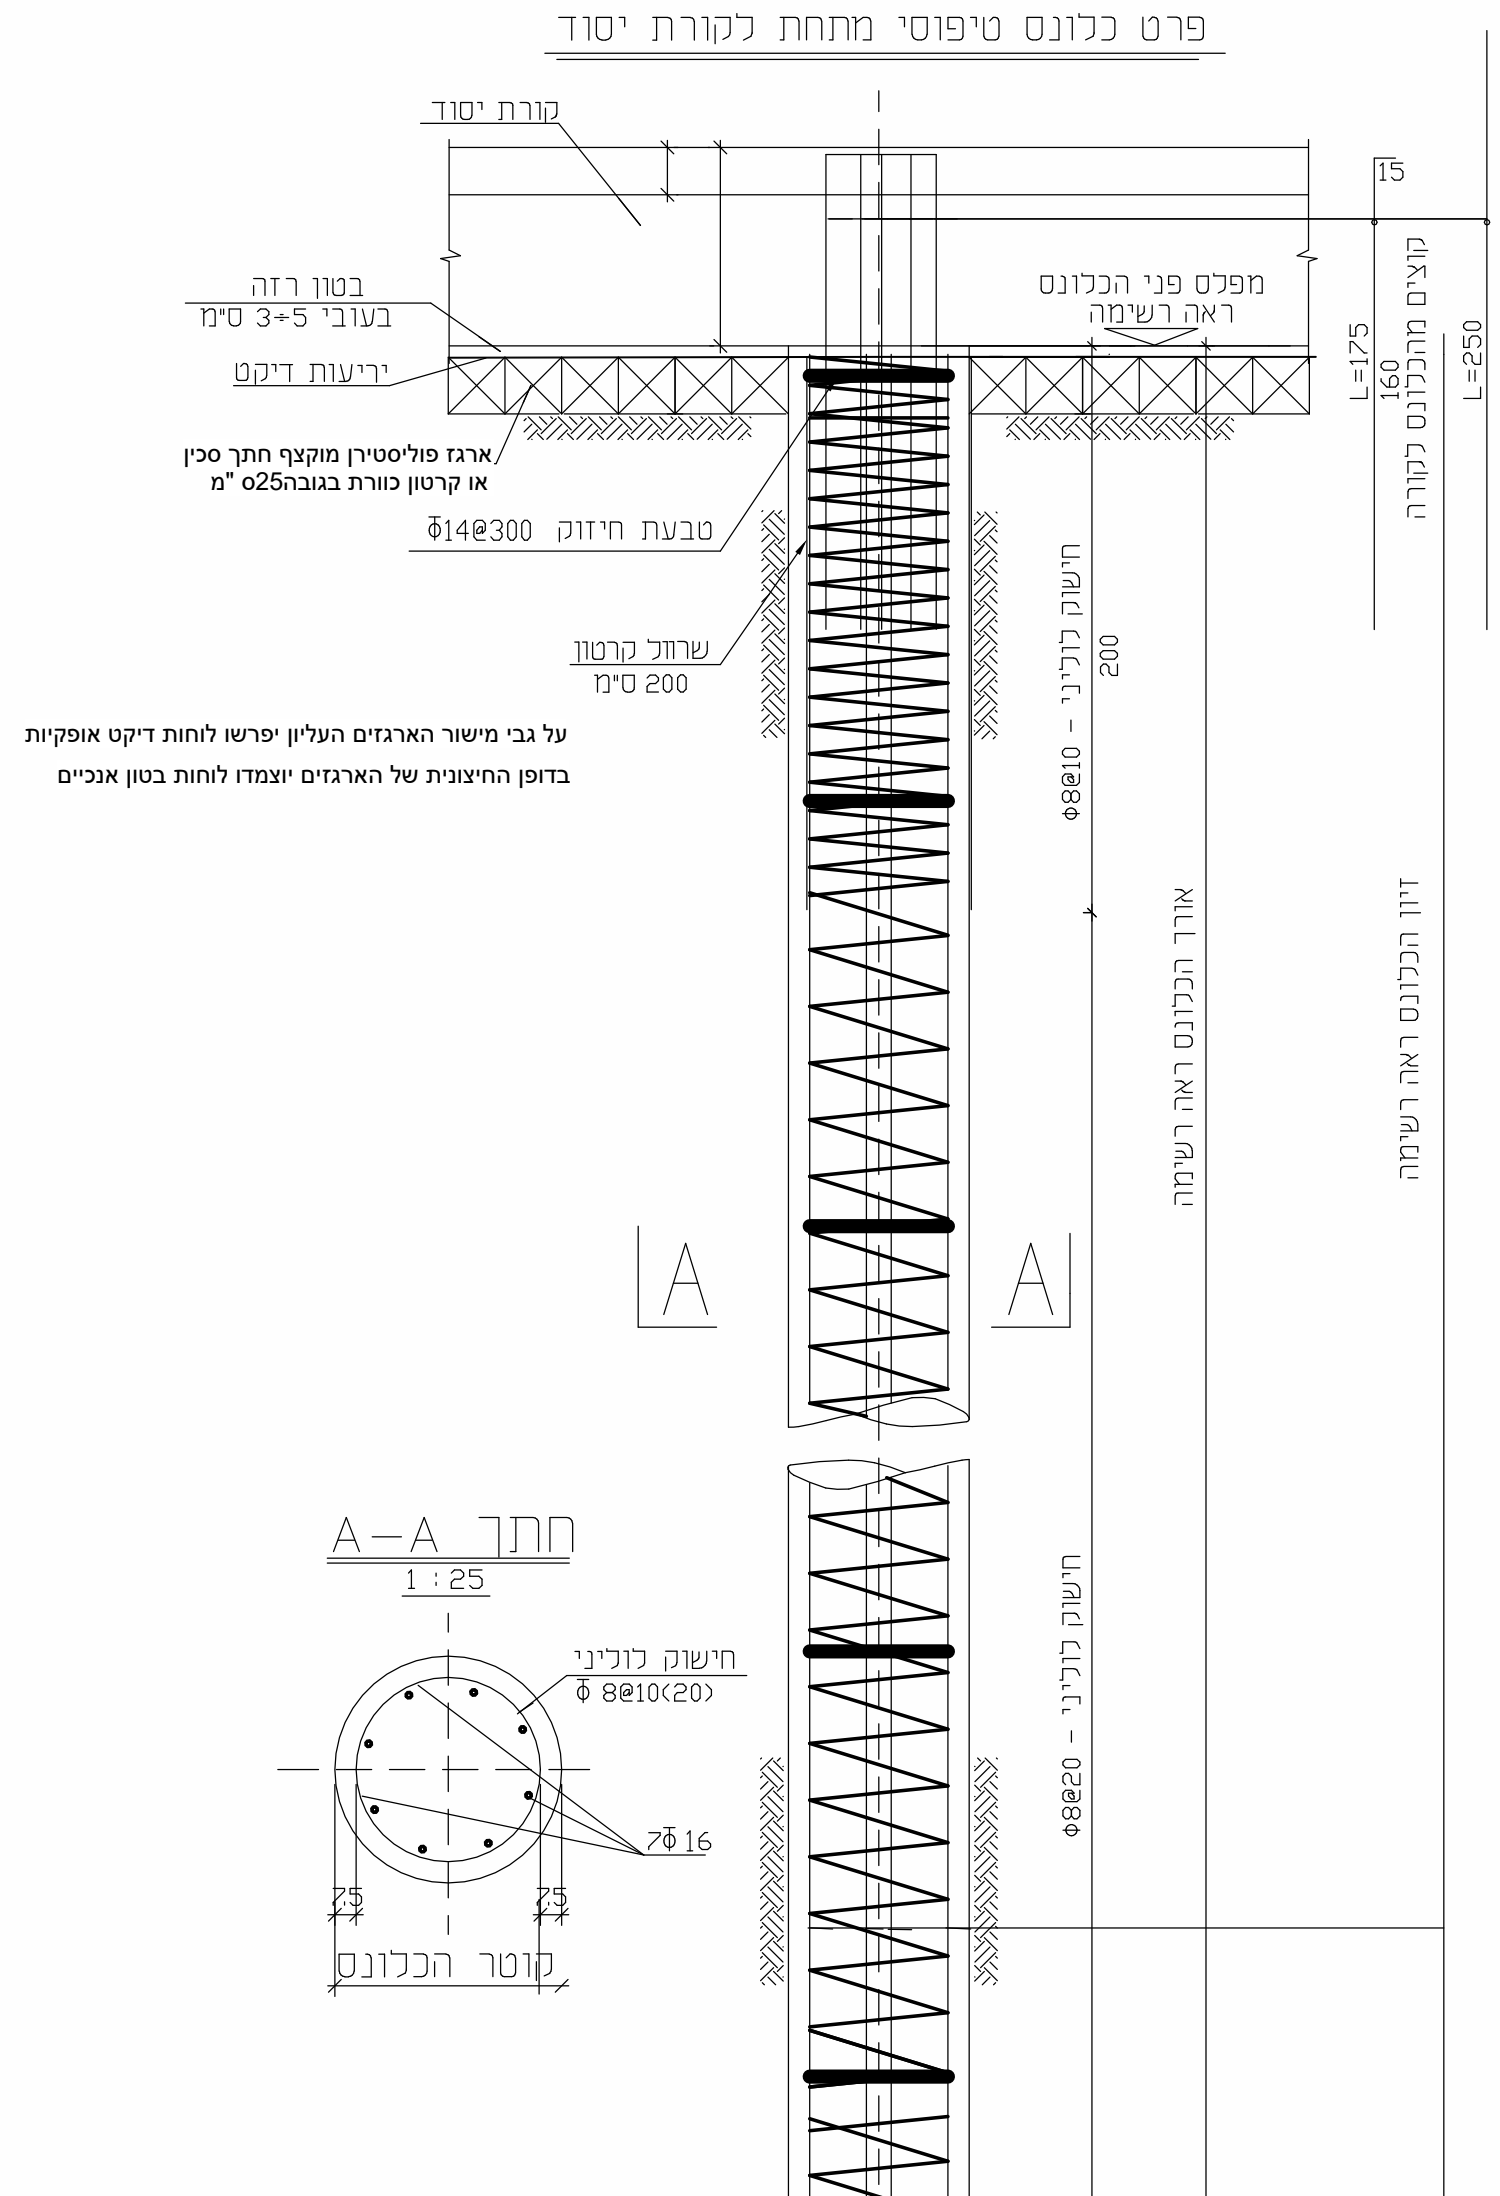

יש לבצע בדיקות סוניות בכל הכלונסאות שבוע לאחר יציקתו

רק לאחר קבלת אישור יש להמשיך בבניית השלד

אורך כלוב הזיון יהיה בהתאם לטבלת כלונסאות

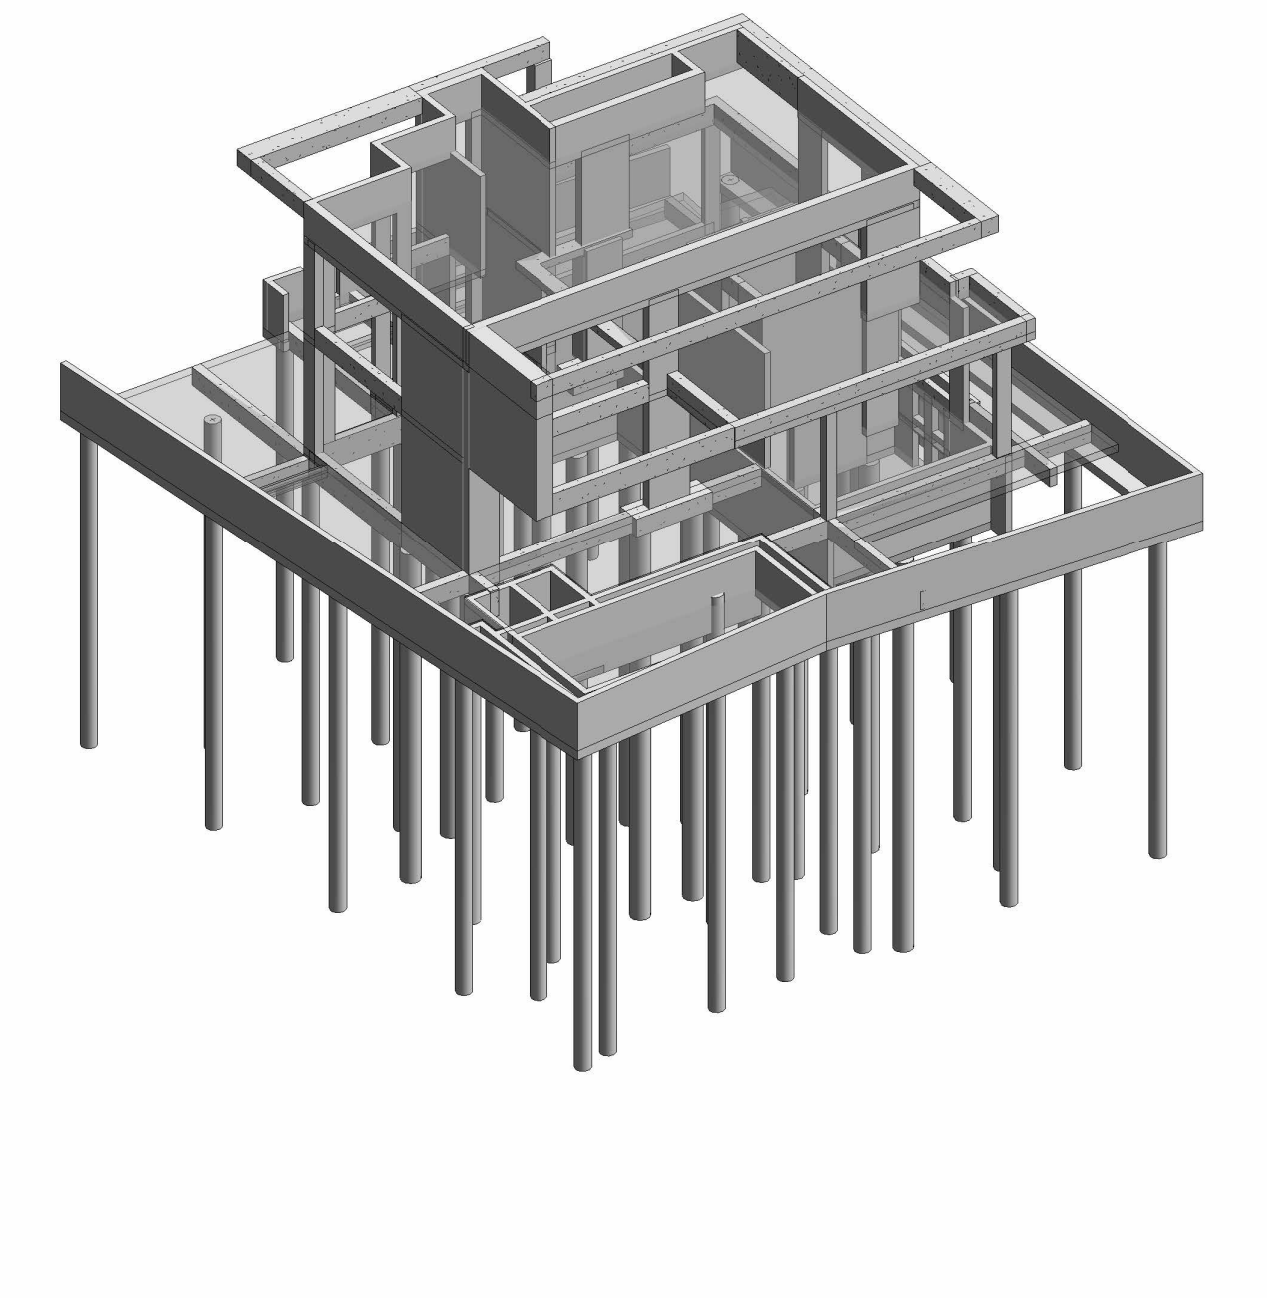

3D 1090

טבלת כלונסאות-כמויות-

מספר כלונס	עומס(טון)	עומק חדירה מינימלי בקרקע טבעית ס"מ	נפח	Elevation at Top	Diameter	קוצים לעמודים L=250	זיון כלונס
1	22	1100	2.16 m³	-3.00 m	50	7Φω16	10Φω12
2	35	1100	2.16 m³	-3.00 m	50	7Φω16	6Φω12
3	69	1300	3.68 m³	-3.00 m	60	8Φω16	ראה פרט חיבור כלונס לקיר
4	49	1100	2.16 m³	-3.00 m	50	7Φω16	ראה פרט חיבור כלונס לקיר
5	29	1100	2.16 m³	-3.00 m	50	7Φω16	ראה פרט חיבור כלונס לקיר
6	70	1300	3.68 m³	-0.75 m	60	8Φω16	ראה פרט ראש כלונס קוטר 60
6A	70	1300	3.68 m³	-0.75 m	60	8Φω16	ראה פרט ראש כלונס קוטר 60
7	70	1100	3.11 m³	-0.80 m	60	8Φω16	ראה פרט חיבור כלונס לקיר
8	70	1100	3.11 m³	-1.00 m	60	8Φω16	ראה פרט חיבור כלונס לקיר
9	47	1100	2.16 m³	-1.07 m	50	7Φω16	ראה פרט חיבור כלונס לקיר
10	60	1300	2.55 m³	-1.07 m	50	7Φω16	10Φω12
11	15	1100	2.16 m³	-1.07 m	50	7Φω16	10Φω12
12	65	1300	3.68 m³	-3.00 m	60	8Φω16	ראה פרט חיבור כלונס לקיר
13	65	1300	3.68 m³	-3.00 m	60	8Φω16	ראה פרט ראש כלונס קוטר 60
13A	65	1300	3.68 m³	-3.00 m	60	8Φω16	ראה פרט ראש כלונס קוטר 60
14	60	1300	2.55 m³	-3.00 m	50	7Φω16	ראה פרט חיבור כלונס לקיר
15	22	1100	2.16 m³	-3.00 m	50	7Φω16	ראה פרט חיבור כלונס לקיר
16	70	1100	3.11 m³	-3.00 m	60	8Φω16	ראה פרט חיבור כלונס לקיר
17	50	1100	2.16 m³	-3.00 m	50	7Φω16	ראה פרט חיבור כלונס לקיר
18	18	1100	2.16 m³	-3.00 m	50	7Φω16	ראה פרט חיבור כלונס לקיר
19	19	1100	2.16 m³	-3.00 m	50	7Φω16	ראה פרט חיבור כלונס לקיר
20	26	1100	2.16 m³	-3.00 m	50	7Φω16	ראה פרט חיבור כלונס לקיר
21	70	1300	3.68 m³	-3.00 m	60	8Φω16	ראה פרט חיבור כלונס לקיר
22	70	1300	3.68 m³	-3.00 m	60	8Φω16	ראה פרט חיבור כלונס לקיר
23	60	1300	2.55 m³	-3.00 m	50	7Φω16	ראה פרט חיבור כלונס לקיר
24	60	1300	2.55 m³	-3.00 m	50	7Φω16	ראה פרט חיבור כלונס לקיר
25	36	1100	2.16 m³	-3.00 m	50	7Φω16	ראה פרט חיבור כלונס לקיר
27	25	1100	2.16 m³	-1.85 m	50	7Φω16	ראה פרט חיבור כלונס לקורה
28	28	1100	2.16 m³	-1.20 m	50	7Φω16	ראה פרט חיבור כלונס לקיר
29	26	1100	2.16 m³	-1.50 m	50	7Φω16	ראה פרט חיבור כלונס לקיר
30	36	1100	2.16 m³	-1.20 m	50	7Φω16	ראה פרט חיבור כלונס לקיר
31	45	1100	2.16 m³	-1.50 m	50	7Φω16	ראה פרט חיבור כלונס לקורה
32	30	1100	2.16 m³	-2.25 m	50	7Φω16	ראה פרט חיבור כלונס לקיר
100	15	1100	2.16 m³	-0.80 m	50	7Φω16	ראה פרט חיבור כלונס לקיר
101	15	1100	2.16 m³	-0.80 m	50	7Φω16	ראה פרט חיבור כלונס לקיר
102	15	1100	2.16 m³	-0.80 m	50	7Φω16	ראה פרט חיבור כלונס לקיר
104	15	1100	2.16 m³	-0.80 m	50	7Φω16	ראה פרט חיבור כלונס לקיר
105	15	1100	2.16 m³	-0.80 m	50	7Φω16	ראה פרט חיבור כלונס לקיר
106	15	1100	2.16 m³	-0.80 m	50	7Φω16	ראה פרט חיבור כלונס לקיר
107	15	1100	2.16 m³	-0.80 m	50	7Φω16	ראה פרט חיבור כלונס לקיר
108	15	1100	2.16 m³	-0.80 m	50	7Φω16	ראה פרט חיבור כלונס לקיר
109	15	1100	2.16 m³	-0.80 m	50	7Φω16	ראה פרט חיבור כלונס לקיר
110	15	1100	2.16 m³	-1.07 m	50	7Φω16	ראה פרט חיבור כלונס לקיר
111	15	1100	2.16 m³	-0.80 m	50	7Φω16	ראה פרט חיבור כלונס לקיר
114	15	1100	2.16 m³	-0.80 m	50	7Φω16	ראה פרט חיבור כלונס לקיר
115	15	1100	2.16 m³	-0.80 m	50	7Φω16	ראה פרט חיבור כלונס לקיר
116	15	1100	2.16 m³	-0.80 m	50	7Φω16	ראה פרט חיבור כלונס לקיר
117	15	1100	2.16 m³	-0.80 m	50	7Φω16	ראה פרט חיבור כלונס לקיר
118	15	1100	2.16 m³	-0.80 m	50	7Φω16	ראה פרט חיבור כלונס לקיר

Grand total: 49 — 122.38 m³

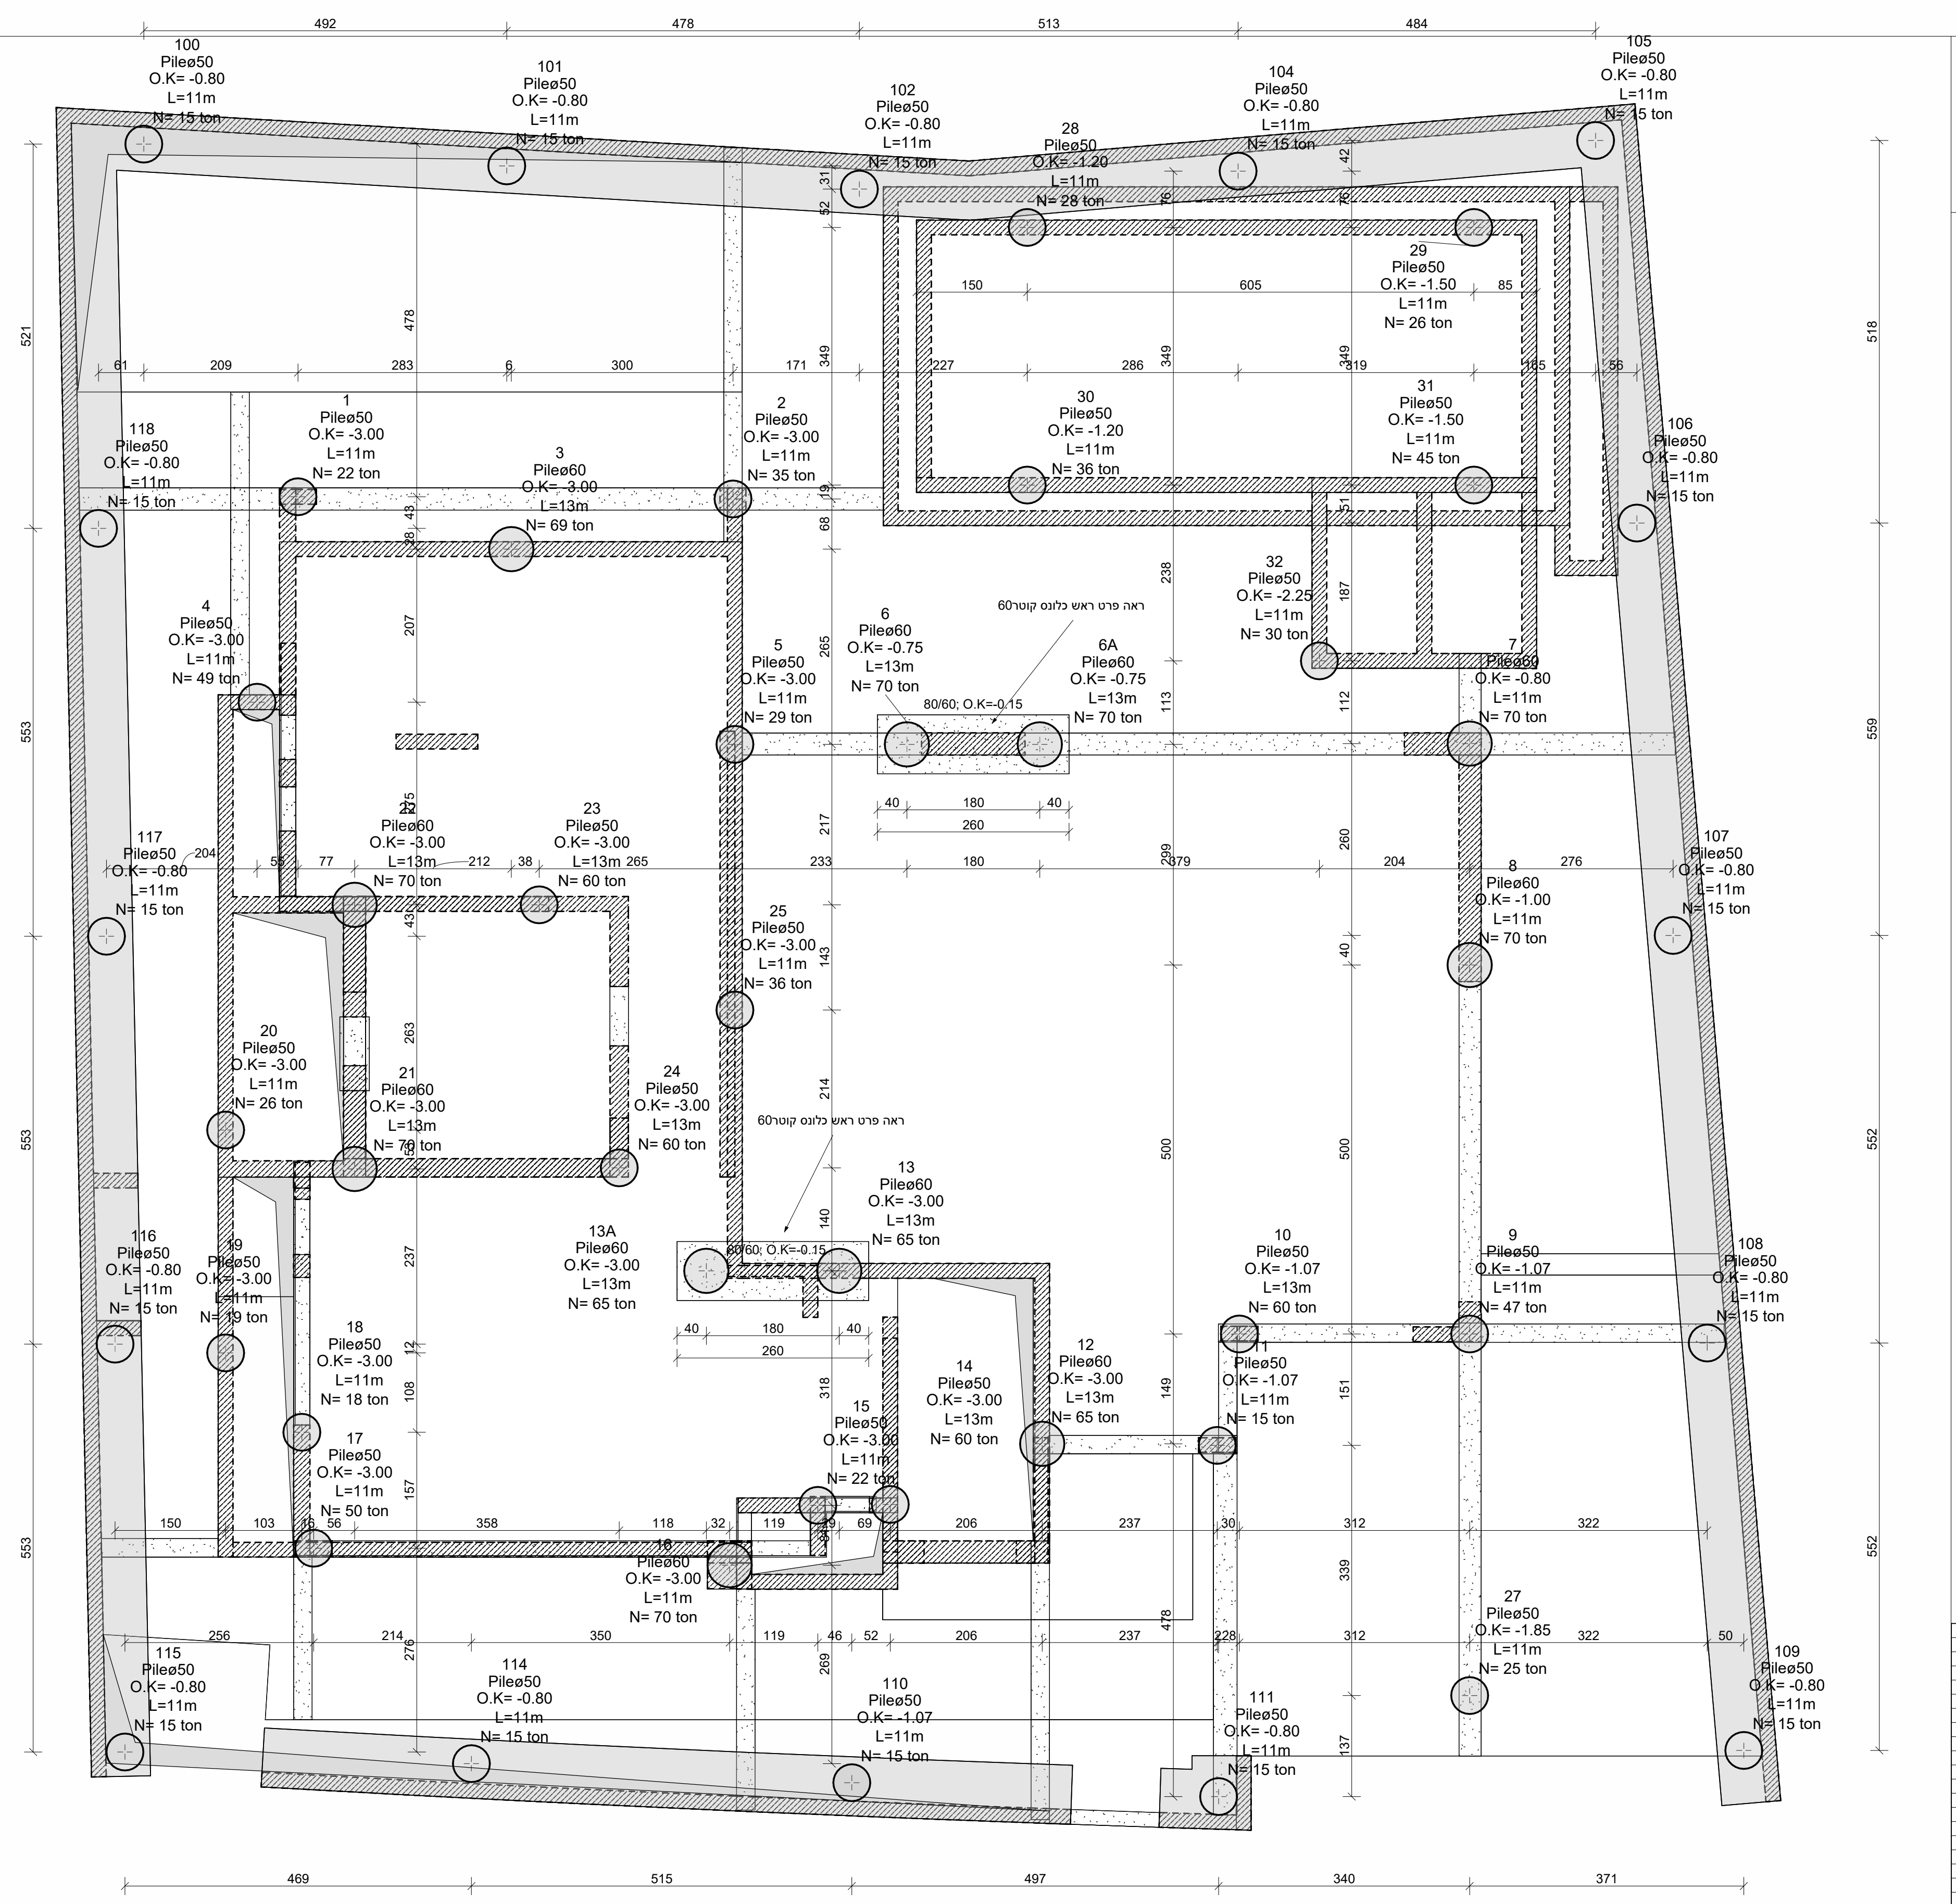

תוכנית יסודות

1 : 50

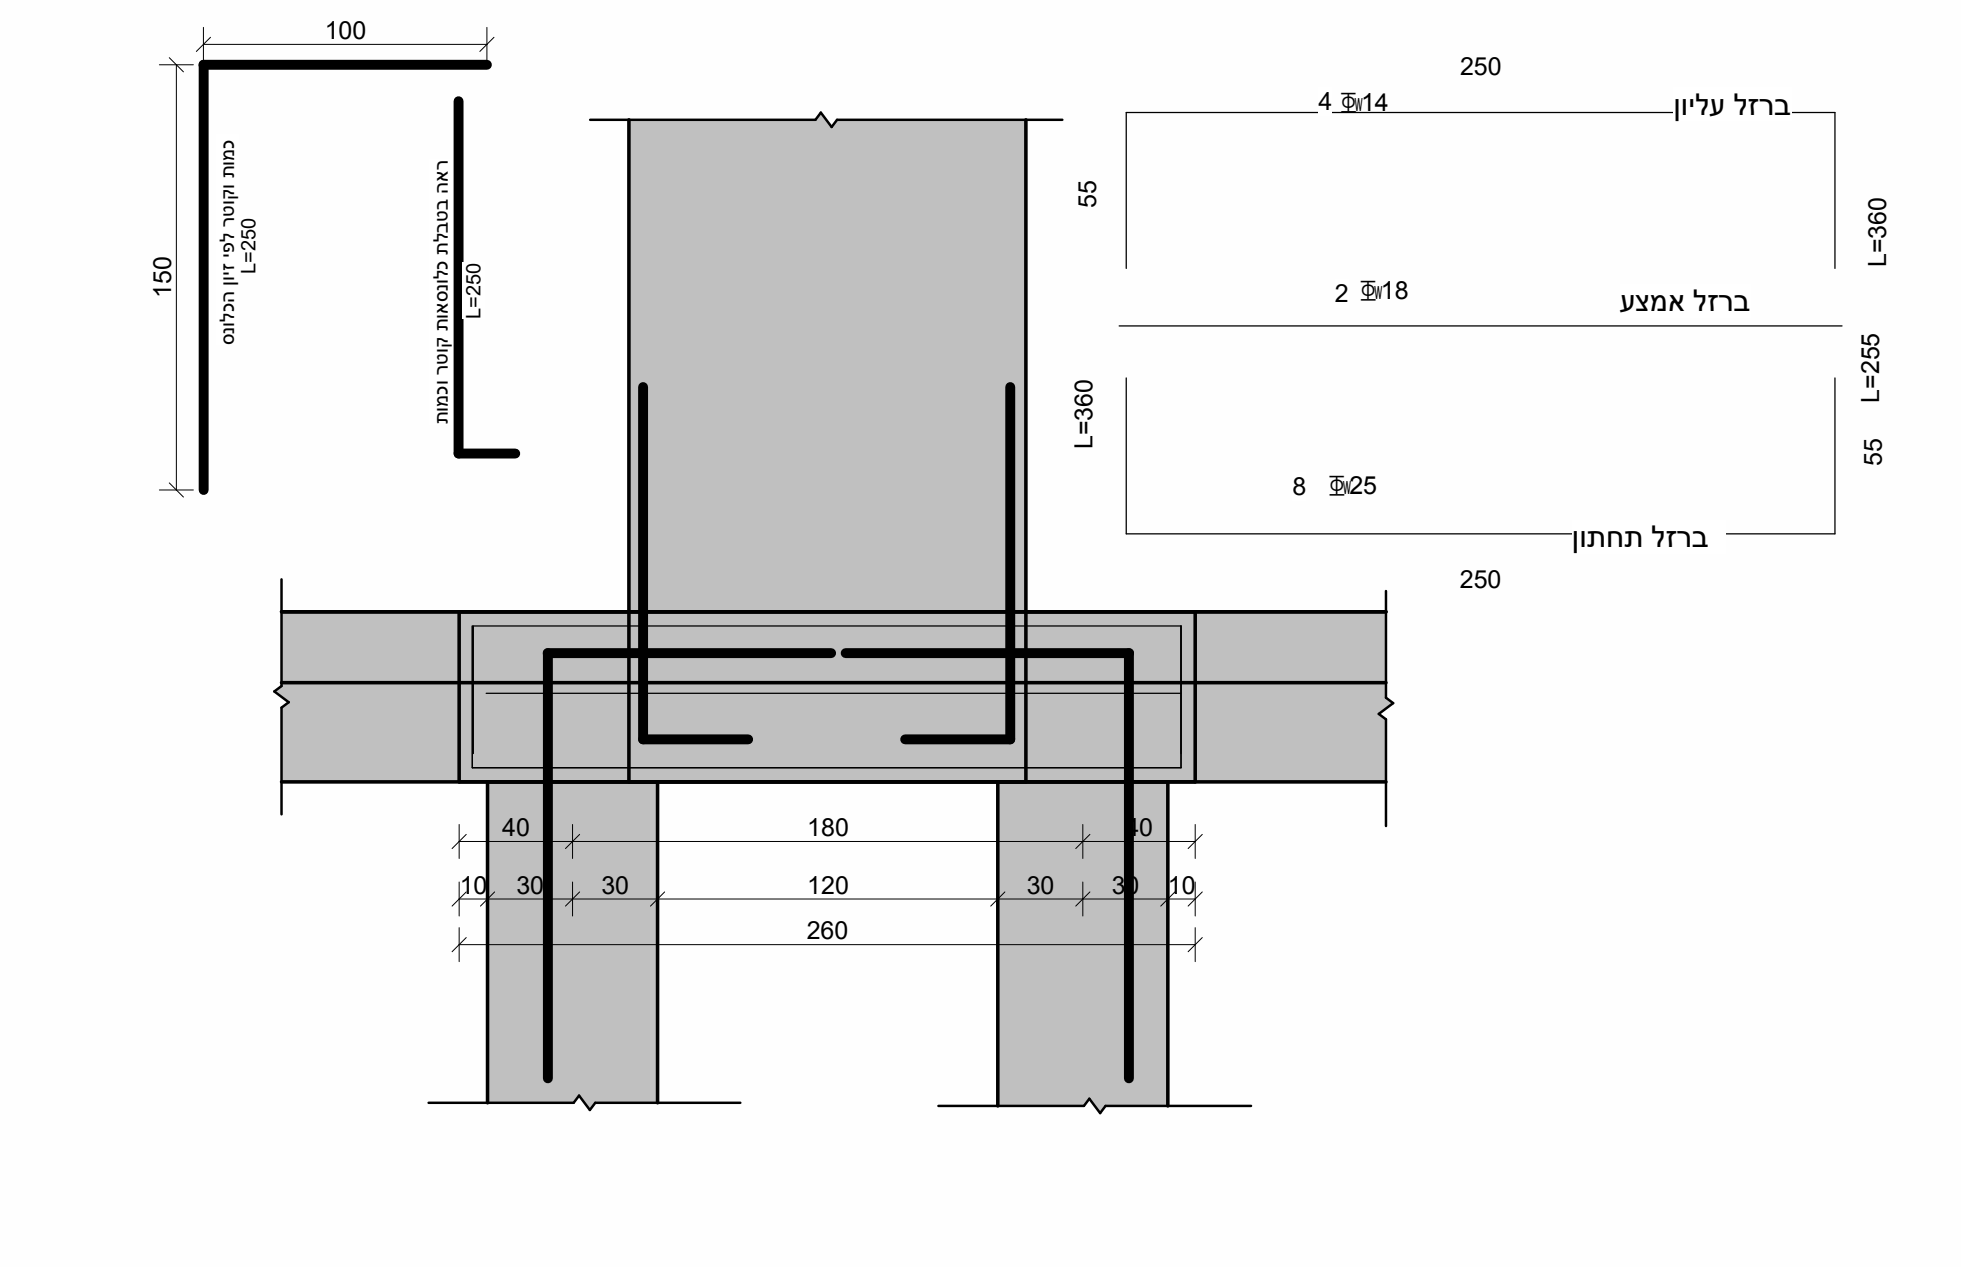

פרט ראש כלונס כפול קוטר60-1

1 : 25

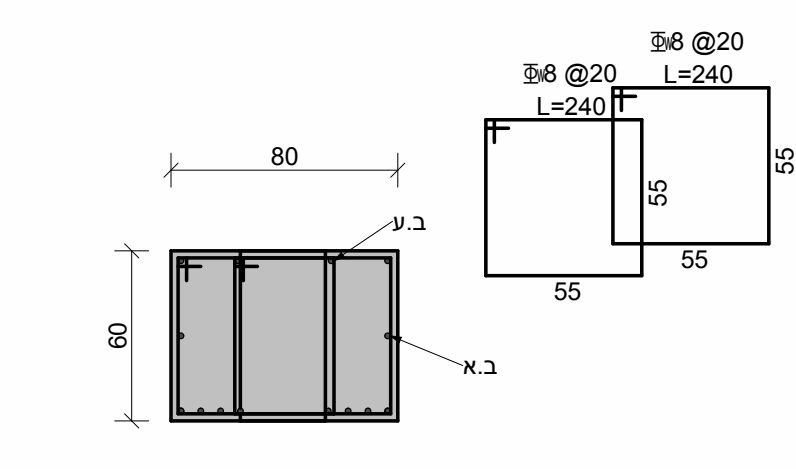

פרט ראש כלונס כפול קוטר60-2

1 : 25

6.4 קוטר הכלונסאות ייקבע בהתאם לעומסים המתוכננים כדלקמן:

קוטר (ס"מ)	אורך כלונסאות (מ')	עומס מותר בלחיצה (טון)	עומס מותר בשליפה (טון)
50 60	11	50 60	20 25
50 60	13	60 70	25 30

-כלל הנחיות יהיו ע" פ דוח קרקע214140/5187 של אגסי רימון מהנדסים, אלא אם נאמר אחרת!

-יש לבצע ניסיון קידוח בשיטה היבשה כנדרש בדוח הביסוס

- יש לבצע בדיקות סוניות בכל הכלונסאות לאחר7 ימים !

- יש לפלס את השטח ולבצע את כל עבודות המילוי הנדרשות מתחת לשלד המבנה לפני סימון הכלונסאות . הכלונסאות יסומנו על גבי מישור אופקי ומפולס בלבד!!

-באחריות הקבלן לבדוק התאמה לשיפוע ולהתאים את גובה החנייה לאבני השפה.

*****באחריות הקבלן לבדוק את מיקום הניפל ,לא לקדוח בתוכו ולא לצקת בתוכו!**

הערות

1. [illegible] תכנית חשמל אינסטלציה ואיטום.
2. [illegible] א .אישור האדריכל
3. [illegible] בתוכנית זו.
3. תוכנית זאת תבוצע רק לאחר חתימת האדריכל והמודד עליה המאשרים כי [illegible] התקנים מבחינת העמדת המבנים במגרש
4. [illegible] האדריכל.
6. מצע סוג א 'מהודק בשכבות יש לבצע לפי הנחיות יועץ הקרקע.
5. עובי כיסוי הבטון יהיה2.5o " מ בכל האלמנטים מלבד אלה שבאים במגע
7. [illegible] 4o "מ.
8. [illegible]
9. [illegible] אישור מהמהנדס המתכנן.
10. [illegible] ומרכזיותם בתחילת הקדיחה ובגמר המטר הראשון.
9. [illegible] קוטר הכלונס המתוכנן . סטייה גדולה מהנ"ל תחייב תוספת זיון ויש לדווח עליה למהנדס.
10. יש לבצע התאמה בין תכניות האדריכליות ושאר היועצים לבין תכנית זו -
11. [illegible] נס תהיה רצופה ותבוצע ביום הקדיחה . היציקה תבוצע באמצעות משפך וצינור פי.וי. סי באורך6מ'.
11. אין להעמיס את המרפסות הן לפני הבנייה , והן אחרי הבנייה בעומס הגדול
12. [illegible] מרכז הקידוח. בהחדרת הכלוב ויש להשתמש בשומרי מרחק")ספייסרים (" במידה7o " מ בהתאם לקוטר הכלונס לעומת קוטר
12. [illegible] יהיה - אך ורק באישור בכתב ממתכנן הקונסטרוקציה.
13. כל היציקות יבוצעו בעזרת משאבה בלבד.
14. יש לבצע בדיקת AS MADE
15. בכל הכלונסאות באישור מהנדס.

▨	עמוד / קיר-צומח
▭	עמוד / קיר-מפסיק

*סוגי בטון ראה ברשימת כמויות

מס 'עידכון	מהות העידכון	ע"י	תאריך
P0	תוכניות לביצוע		5.10.26

עומסים

עומס קבוע נוסף	500 =ק"ג /מ"ר
עומס שימושי	150 =ק"ג /מ"ר
עומס מרפסות	350=ק"ג /מ"ר

גובה מפלס)אדריכלות): +0.00

מפלס פני בטון: -0.15

P0 מעודכן לתאריך: 5.10.26

לעיון	לאישור	למכרז	לביצוע
○	○	○	●

שם הפרויקט:

וילה ליאור ואביחי אטואן

תאור השרטוט:

תכנית יסודות1090

מס 'השרטוט:

K-400_1090

מס 'פרויקט: WORK-167

קנ"מ:

דוא" ל: tal@yarin-eng.co.il

גודל גליון: 1738 X 910

מהנדס אחראי: טל שי אטיאס

מהנדס: רותם מאיר

ירין הנדסה
טל אטיאס: 050-444-4730
tal@yarin-eng.co.il

YARIN
תכנון | ניהול | פיקוח מבנים

01/11/2026 10:16:50
C:\Users\LENOVO P 340\Desktop\תוכניות עבודה\תמר\work
167-וילה ליאור ואביחי אטואן\const\קובץ פתיחת תיקיה רוויט\מודל רוויט
התחלתי.rvt