שכונת הרקפות
באר שבע

1.3

תכניות חזיתות וחתכים
טיפוס 2A

תאריך: 03.05.2022
קנ"מ: 1:200
מהדורה: 108

אין התנגדות -
9/08/22

עיריית באר שבע
אולגה חריטונוב
אגף הנדסה
מנהלת מחלקת
תיאום תשתיות דרכים ופיתוח

6/3/24
אדר' מור ש[illegible]צר
צוות אדריכל העיר
עיריית באר שבע

ועדה מקומית באר-שבע
אישור תוכנית מס' תמל 1016 (2)
הועדה המקומית החליטה לאשר את התוכנית
בישיבה מס' 20220012 מיום 30/6/24

שלומי נומה
סגן ומ"מ ראש העיר
יו"ר ועדה לתכנון ובנייה
עיריית באר שבע

באר שבע
בירת ההזדמנויות של ישראל

מנהלת הסכם הגג
באר שבע

מקרא :

—	גבול מגרש
- · - · -	קו בניין
⬚	חצר אפקטיבית
▩	חצר פרטית
▦	ריצוף/שביל
▣	אשפה
-0.20	מפלס עקרוני בשטחים ציבוריים
+0.00	מפלס קומה
1 ▼	מס' חזית וסימונה
▨	שטח השהיה
▩	שביל כניסה ראשית

אדר' הגר פוריה שרביט
מהנדסת העיר
באר שבע
02-05-2024

27 -11- 2022
187-2022

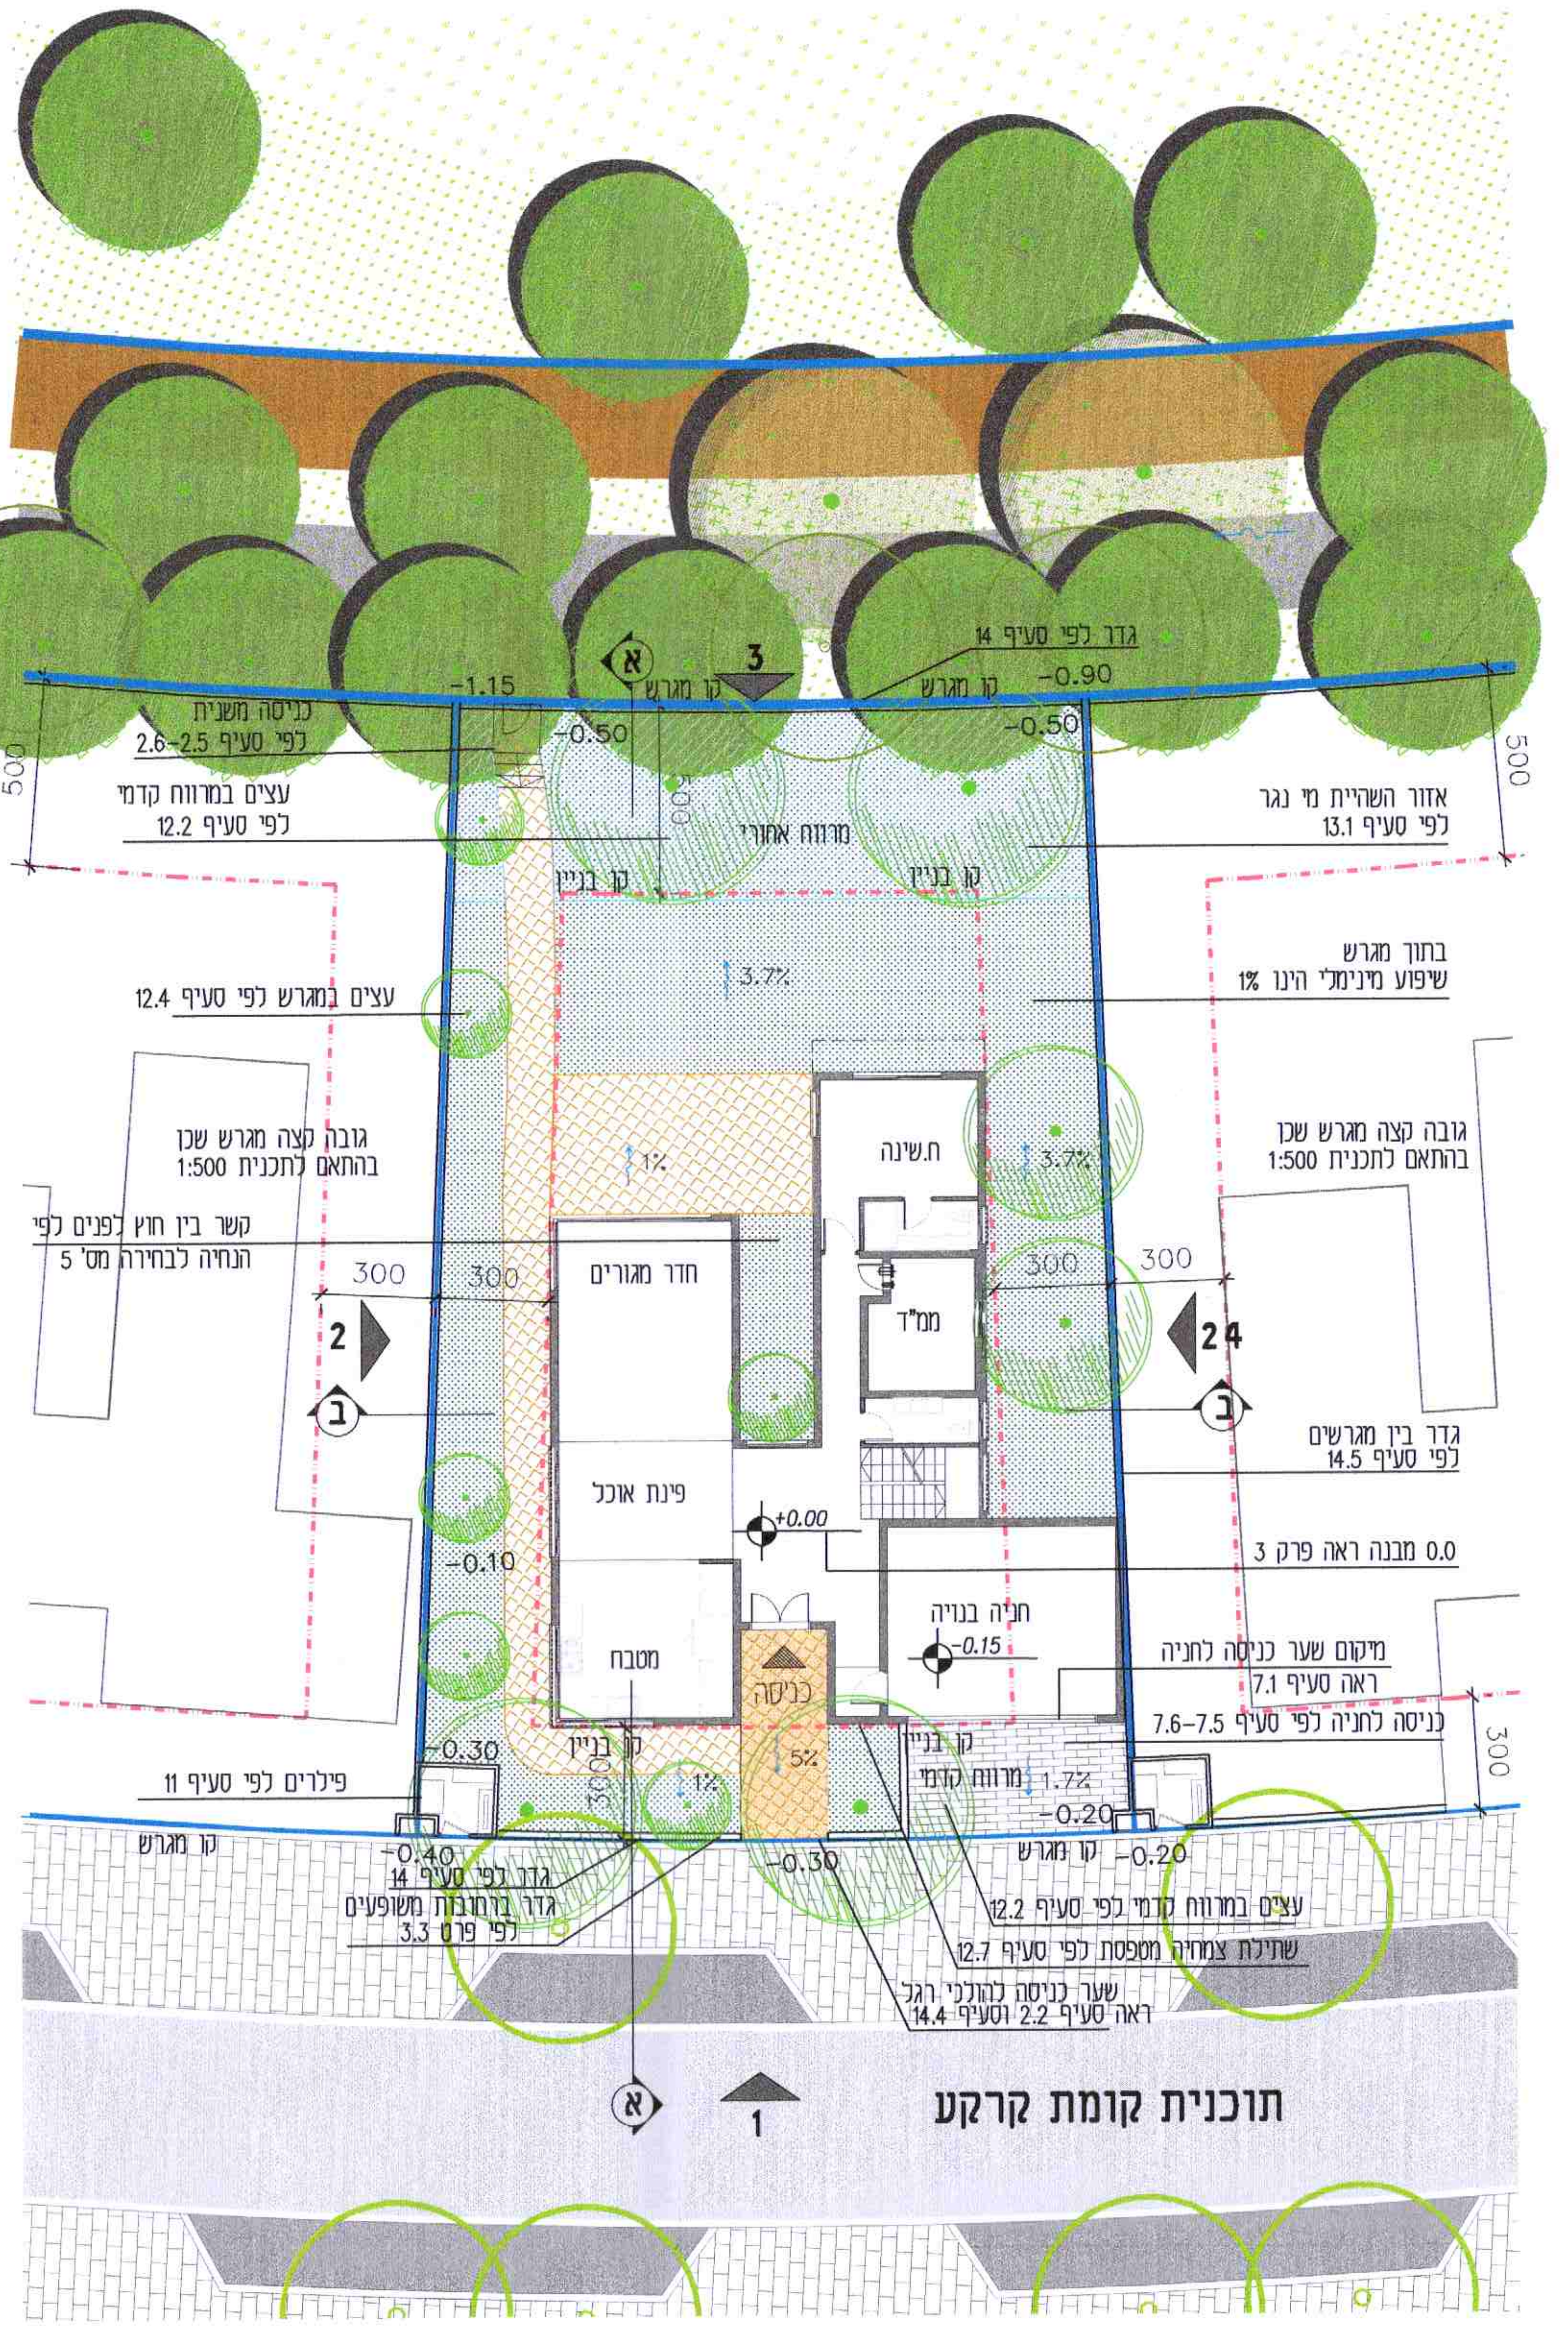

גדר לפי סעיף 14
-0.90
-1.15
קו מגרש
-0.50
כניסה משנית לפי סעיף 2.5-2.6
עצים במרווח קדמי לפי סעיף 12.2
מרווח אחורי
אזור השהיית מי נגר לפי סעיף 13.1
500
קו בניין
3.7%
בתוך מגרש שיפוע מינימלי הינו 1%
עצים במגרש לפי סעיף 12.4
1%
ח.שינה
גובה קצה מגרש שכן בהתאם לתכנית 1:500
קשר בין חוץ לפנים לפי הנחיה לבחירה מס' 5
300
חדר מגורים
ממ"ד
2
24
ב
גדר בין מגרשים לפי סעיף 14.5
פינת אוכל
+0.00
0.0 מבנה ראה פרק 3
-0.10
חניה בנויה
-0.15
מטבח
כניסה
מיקום שער כניסה לחניה ראה סעיף 7.1
כניסה לחניה לפי סעיף 7.5-7.6
5%
מרווח קדמי
1.7%
-0.20
-0.30
פילרים לפי סעיף 11
-0.40
גדר לפי סעיף 14
גדר ברחובות משופעים לפי פרט 3.3
עצים במרווח קדמי לפי סעיף 12.2
שתילת צמחיה מטפסת לפי סעיף 12.7
שער כניסה להולכי רגל ראה סעיף 2.2 וסעיף 14.4
א
1

תוכנית קומת קרקע

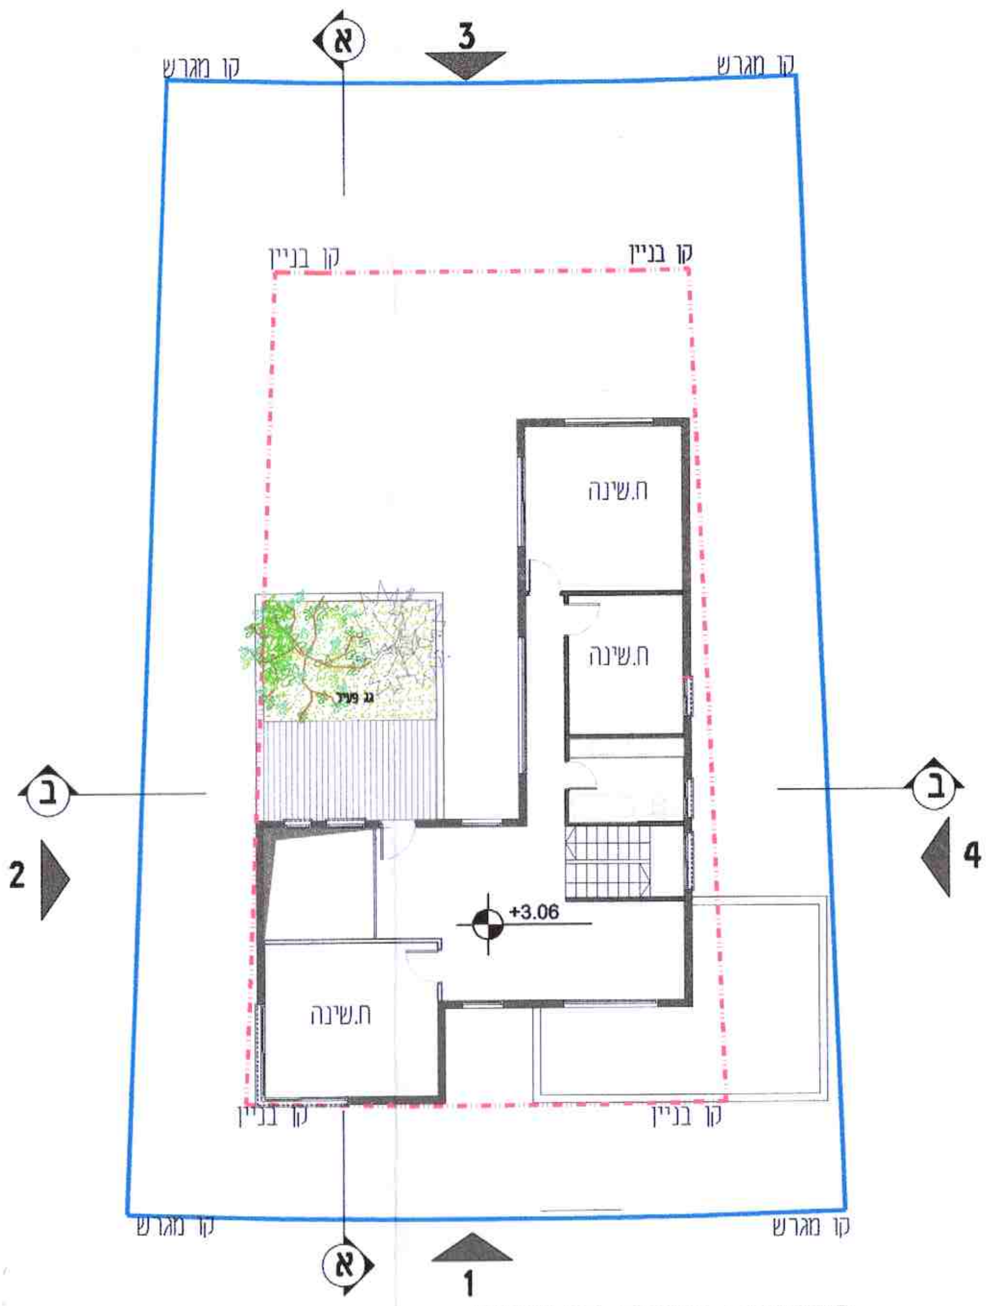

תוכנית קומה ראשונה

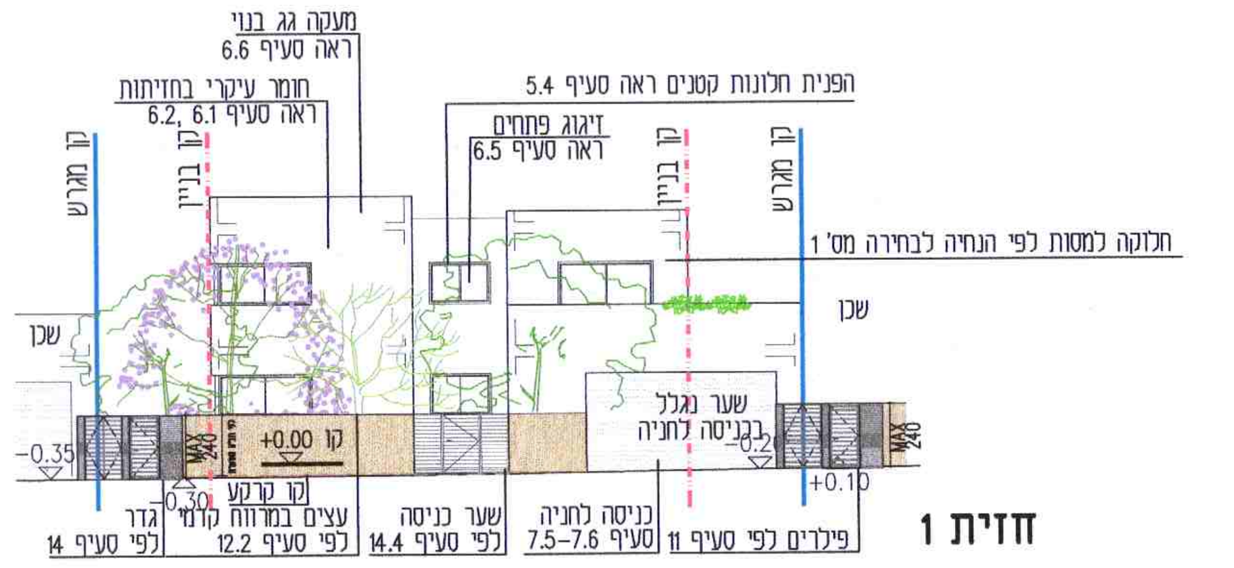

חזית 1

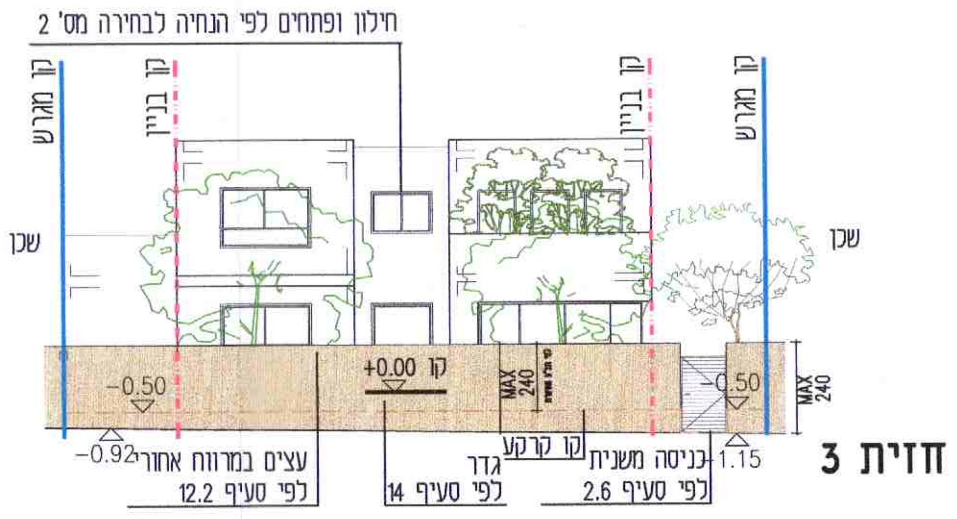

חזית 3

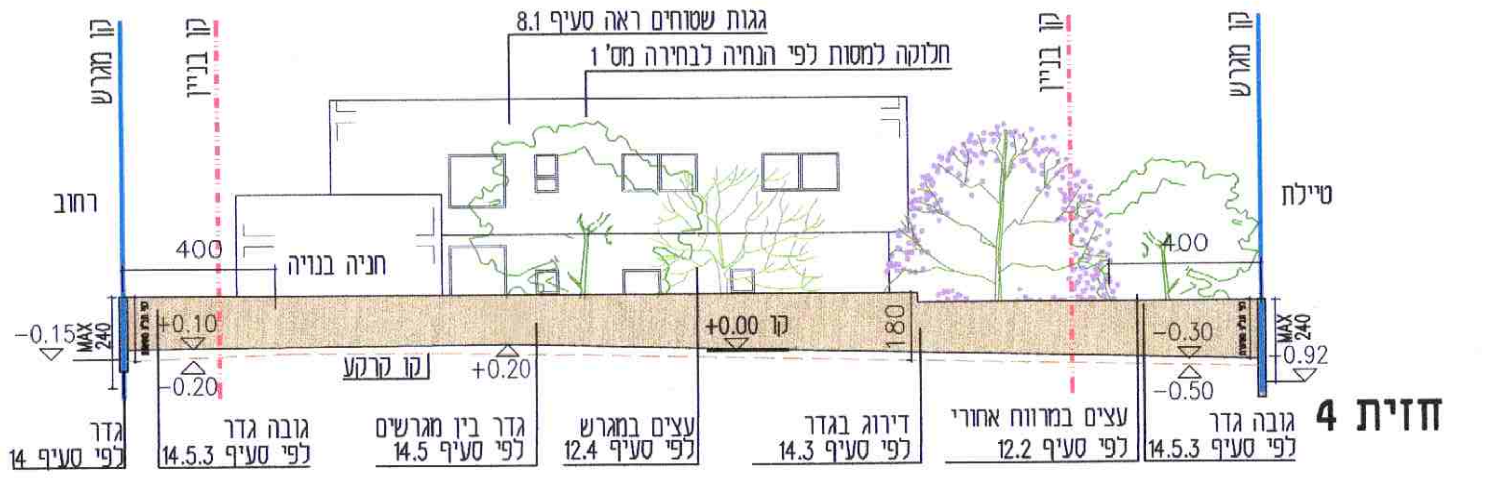

חזית 4

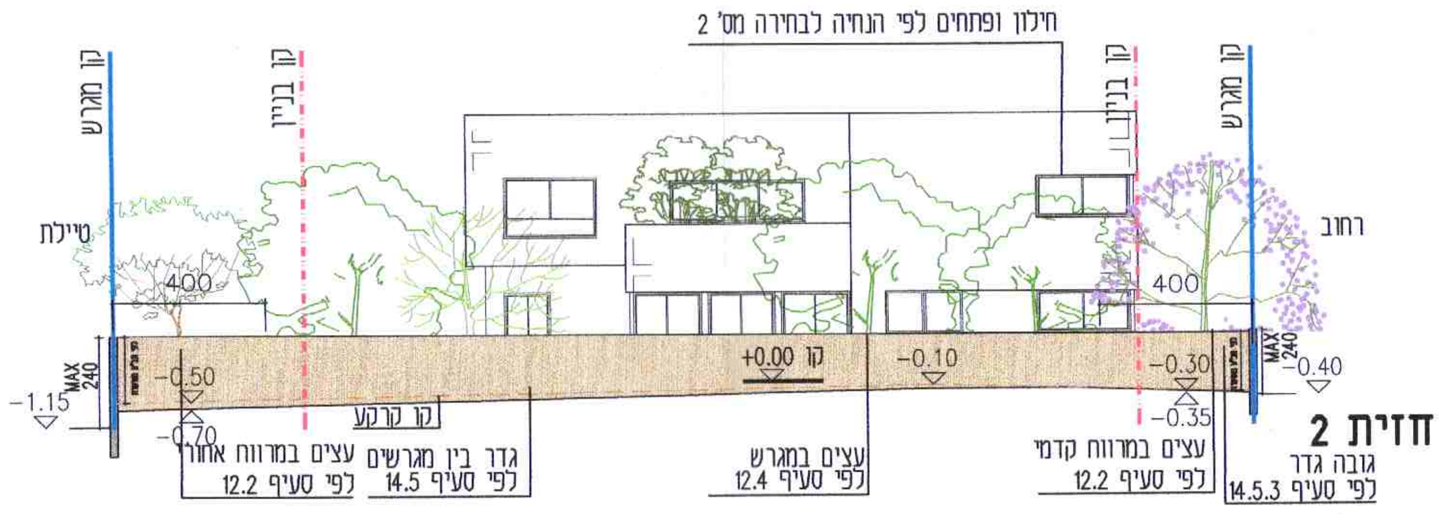

חזית 2

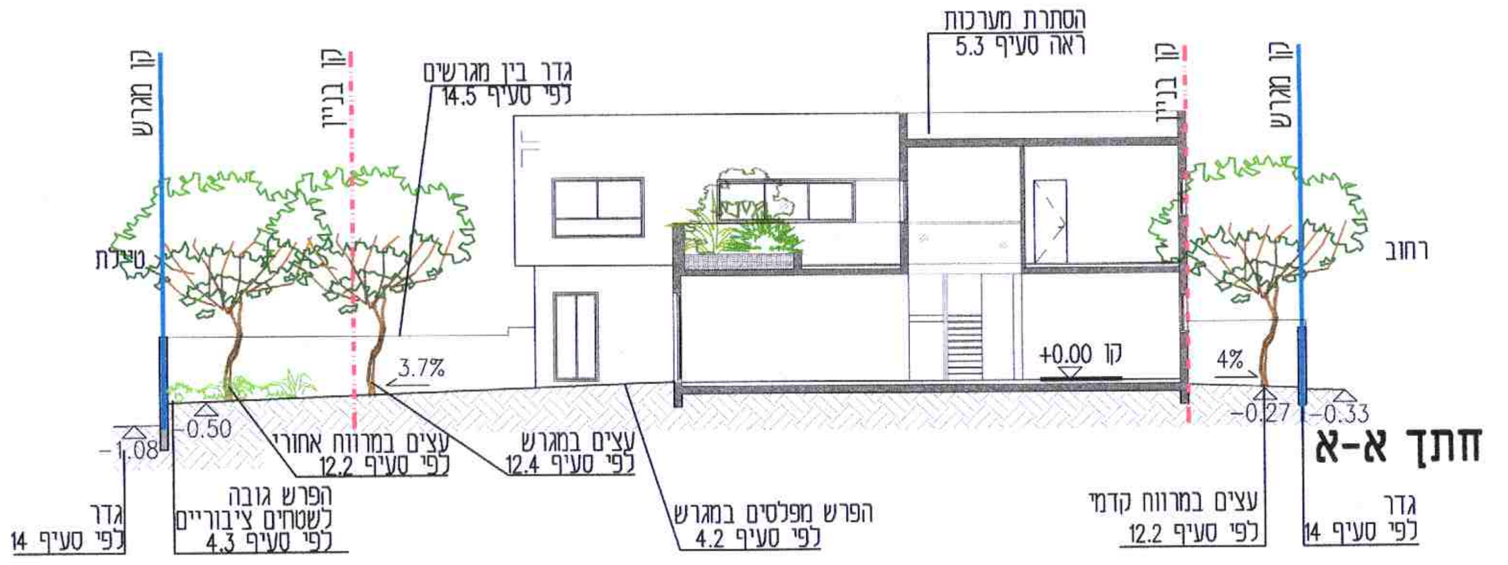

הסתרת מערכות ראה סעיף 5.3
גדר בין מגרשים לפי סעיף 14.5
קו מגרש
קו בניין
טיילת
רחוב
3.7%
4%
קו +0.00
-1.08
-0.50
-0.27
-0.33
עצים במרווח אחורי לפי סעיף 12.2
עצים במגרש לפי סעיף 12.4
גדר לפי סעיף 14
הפרש גובה לשטחים ציבוריים לפי סעיף 4.3
הפרש מפלסים במגרש לפי סעיף 4.2
עצים במרווח קדמי לפי סעיף 12.2
גדר לפי סעיף 14

חתך א-א

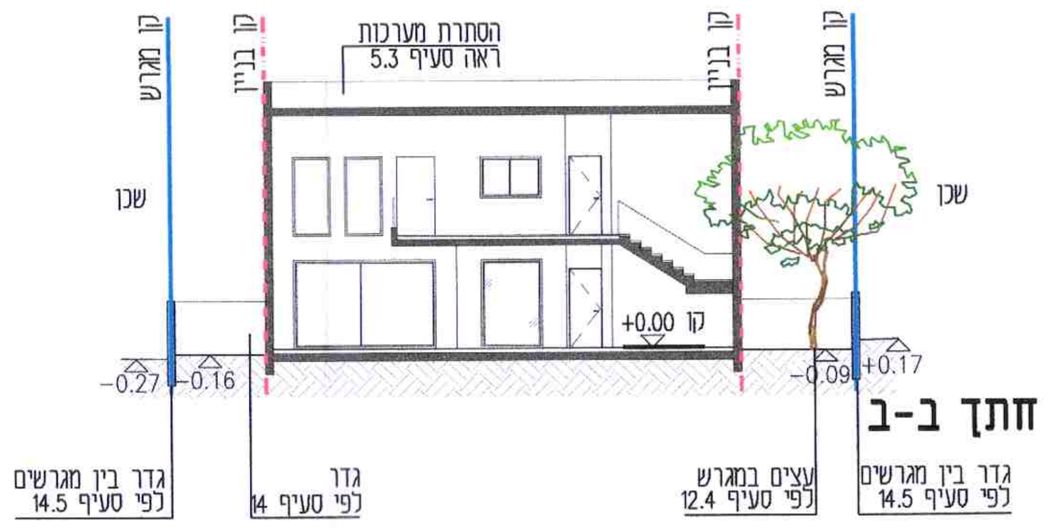

חתך ב-ב