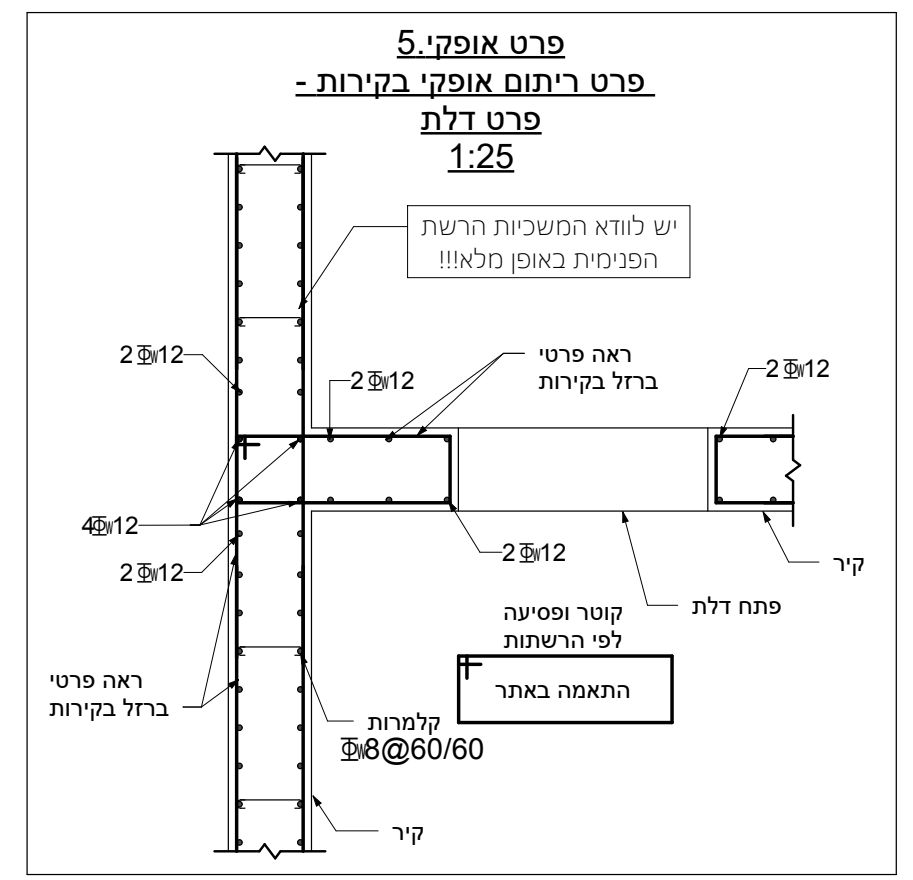
פרט אופקי.5
פרט ריתום אופקי בקירות - פרט דלת
1:25
יש לוודא המשכיות הרשת הפנימית באופן מלא!!!
2Φ12
4Φ12
ראה פרטי ברזל בקירות
פתח דלת
קיר
קוטר ופסיעה לפי הרשתות
התאמה באתר
קלמרות Φ8@60/60

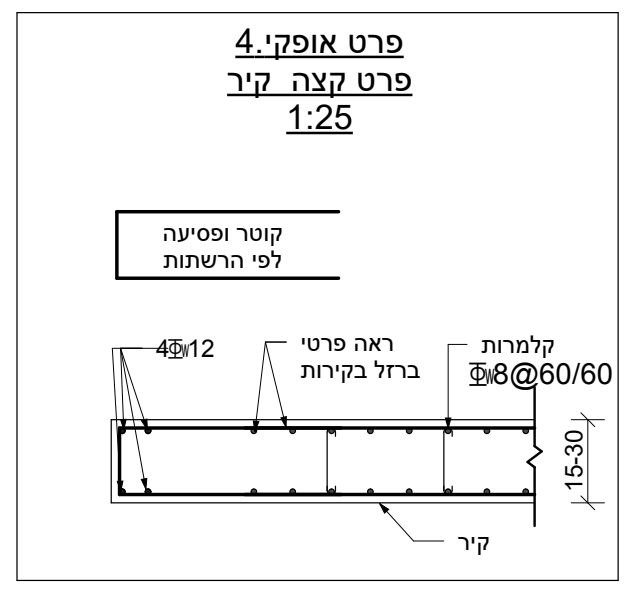
פרט אופקי.4
פרט קצה קיר
1:25
קוטר ופסיעה לפי הרשתות
4Φ12
ראה פרטי ברזל בקירות
קלמרות Φ8@60/60
15-30
קיר

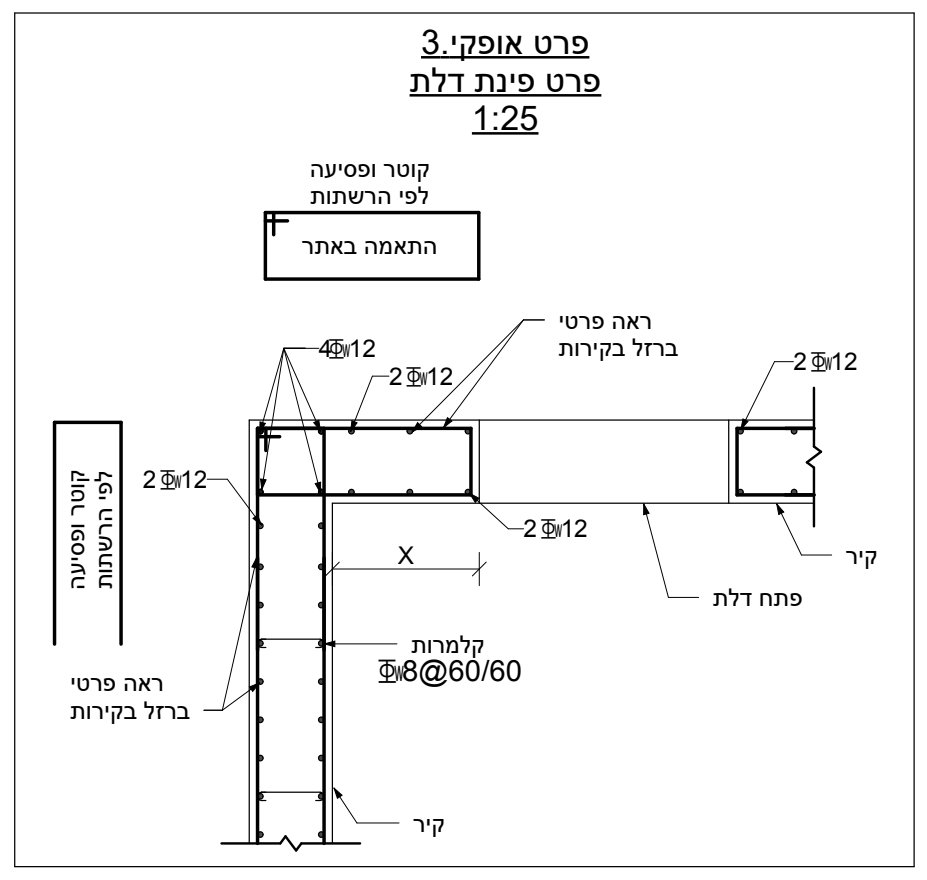
פרט אופקי.3
פרט פינת דלת
1:25
קוטר ופסיעה לפי הרשתות
התאמה באתר
4Φ12
2Φ12
ראה פרטי ברזל בקירות
X
פתח דלת
קיר
קלמרות Φ8@60/60

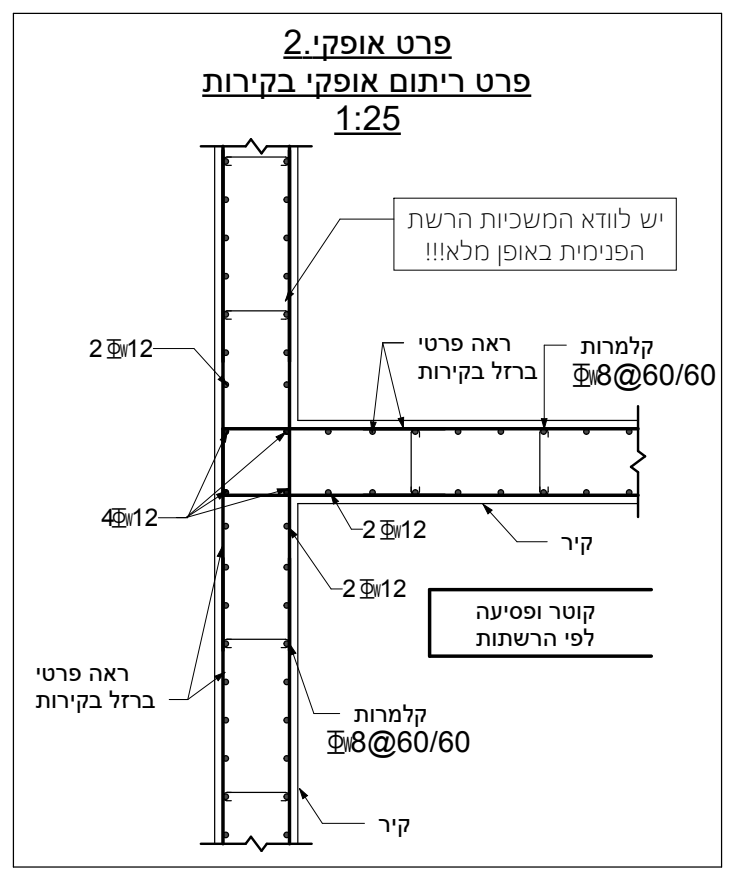
פרט אופקי.2
פרט ריתום אופקי בקירות
1:25
יש לוודא המשכיות הרשת הפנימית באופן מלא!!!
2Φ12
4Φ12
ראה פרטי ברזל בקירות
קלמרות Φ8@60/60
קוטר ופסיעה לפי הרשתות
קיר

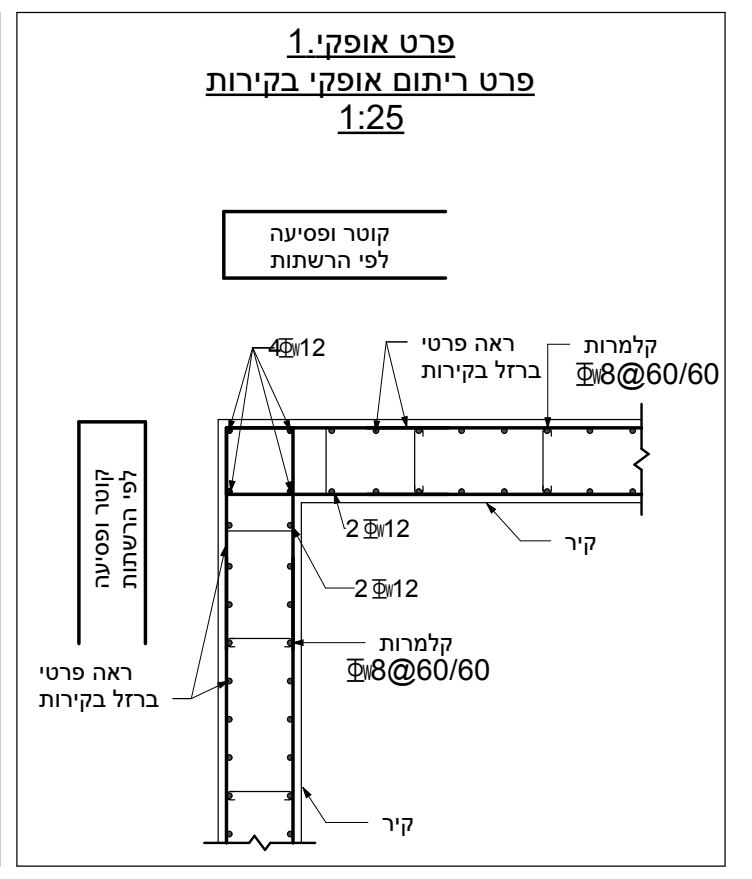
פרט אופקי.1
פרט ריתום אופקי בקירות
1:25
קוטר ופסיעה לפי הרשתות
4Φ12
ראה פרטי ברזל בקירות
קלמרות Φ8@60/60
2Φ12
קיר

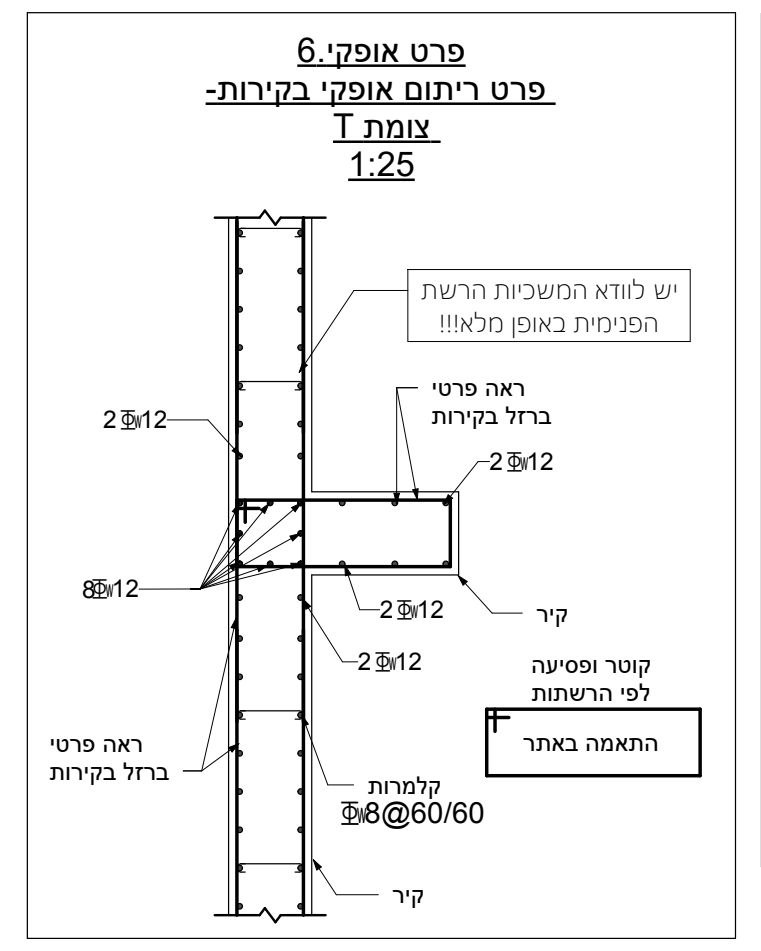
פרט אופקי.6
פרט ריתום אופקי בקירות- צומת T
1:25
יש לוודא המשכיות הרשת הפנימית באופן מלא!!!
2Φ12
ראה פרטי ברזל בקירות
קוטר ופסיעה לפי הרשתות
התאמה באתר
קלמרות Φ8@60/60
קיר

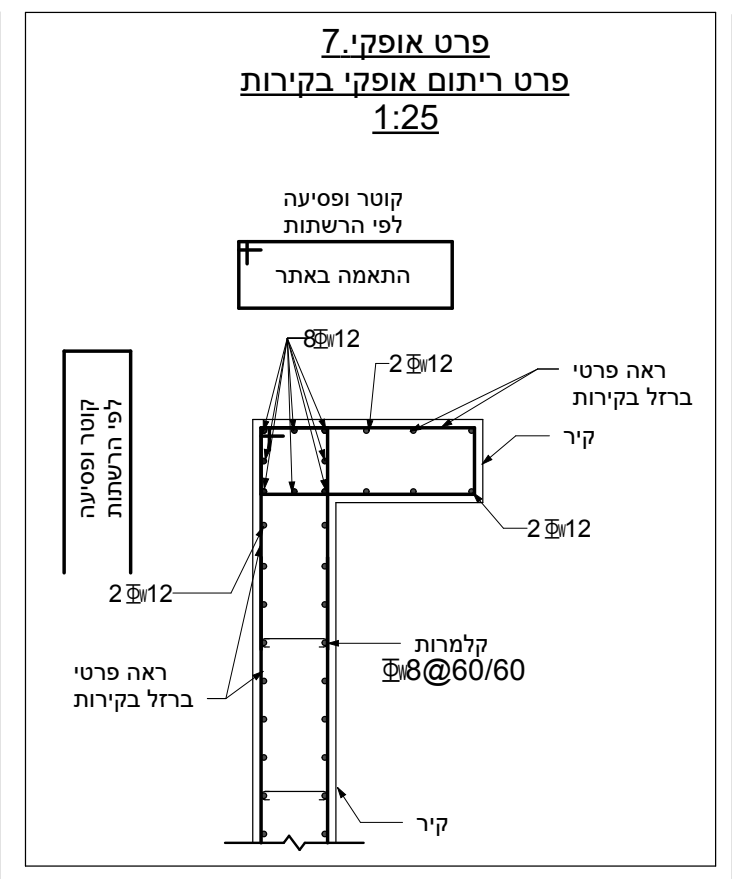
פרט אופקי.7
פרט ריתום אופקי בקירות
1:25
קוטר ופסיעה לפי הרשתות
התאמה באתר
8Φ12
2Φ12
ראה פרטי ברזל בקירות
קיר
קלמרות Φ8@60/60

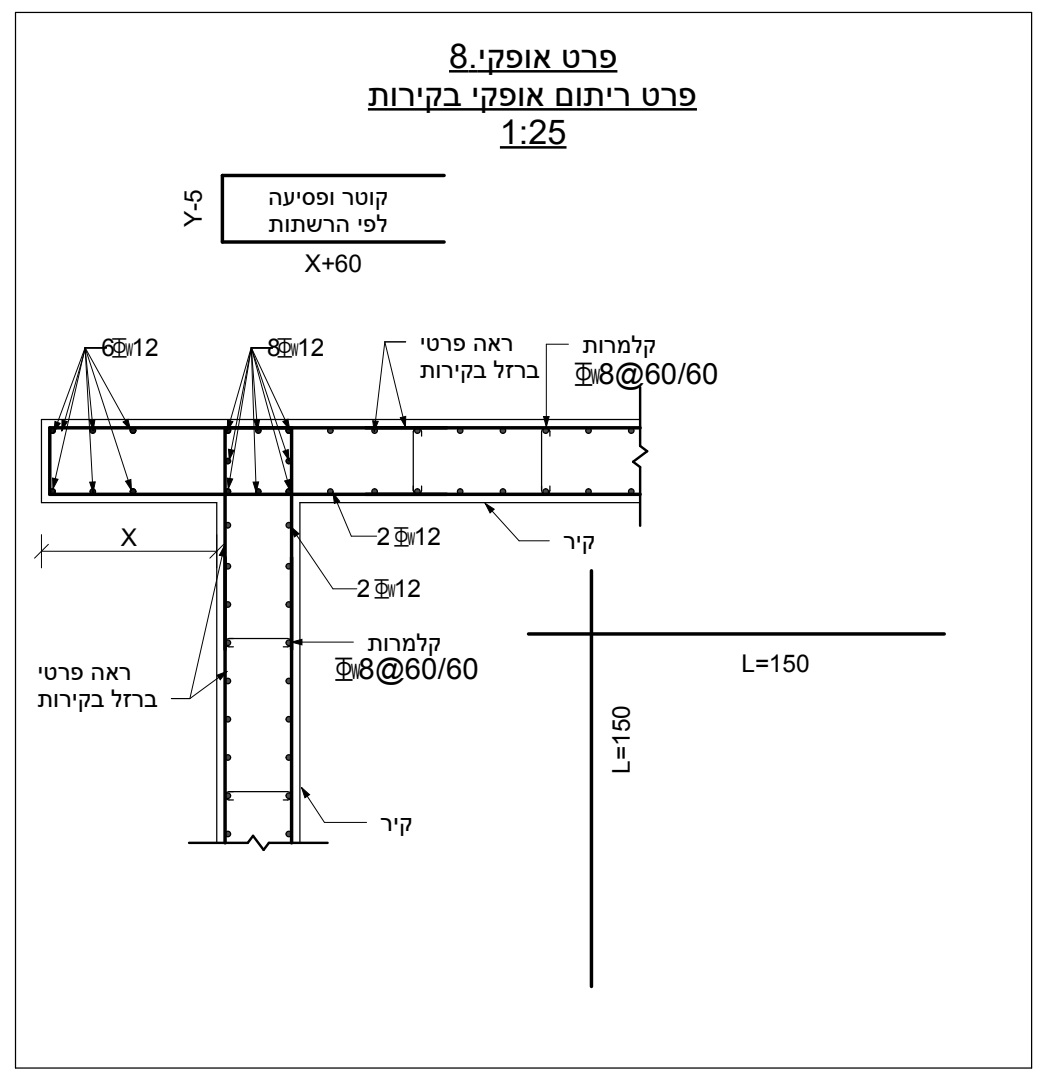
פרט אופקי.8
פרט ריתום אופקי בקירות
1:25
Y-5
קוטר ופסיעה לפי הרשתות
X+60
6Φ12
8Φ12
ראה פרטי ברזל בקירות
קלמרות Φ8@60/60
X
L=150

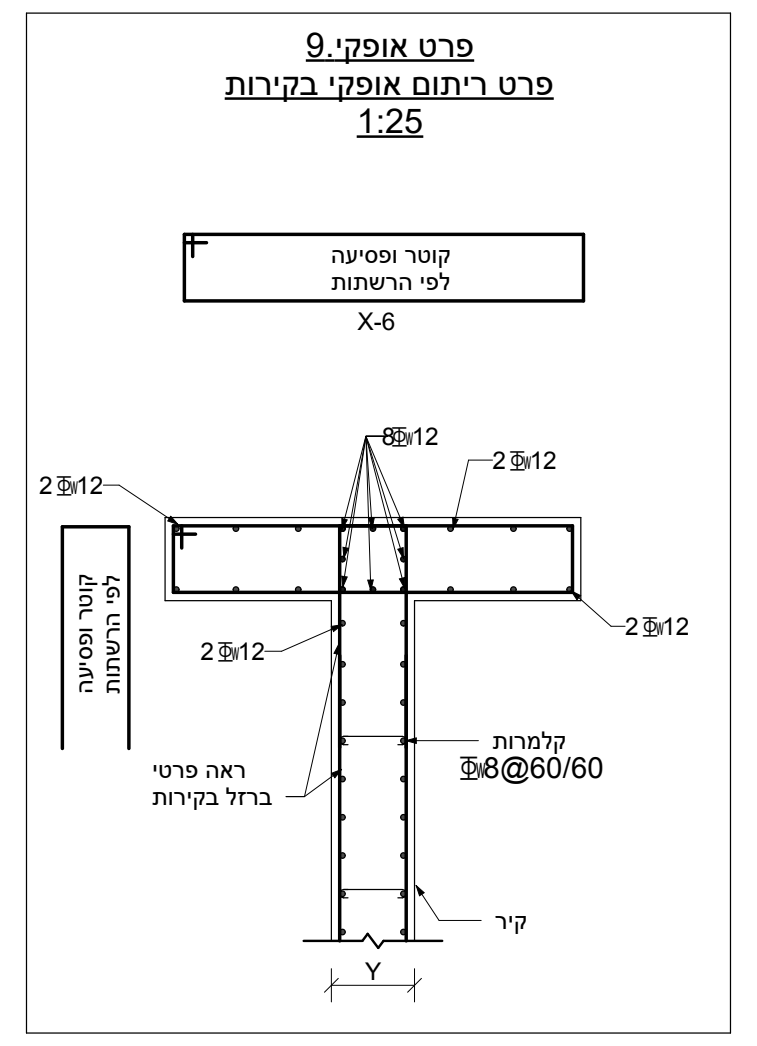
פרט אופקי.9
פרט ריתום אופקי בקירות
1:25
קוטר ופסיעה לפי הרשתות
X-6
8Φ12
2Φ12
Y

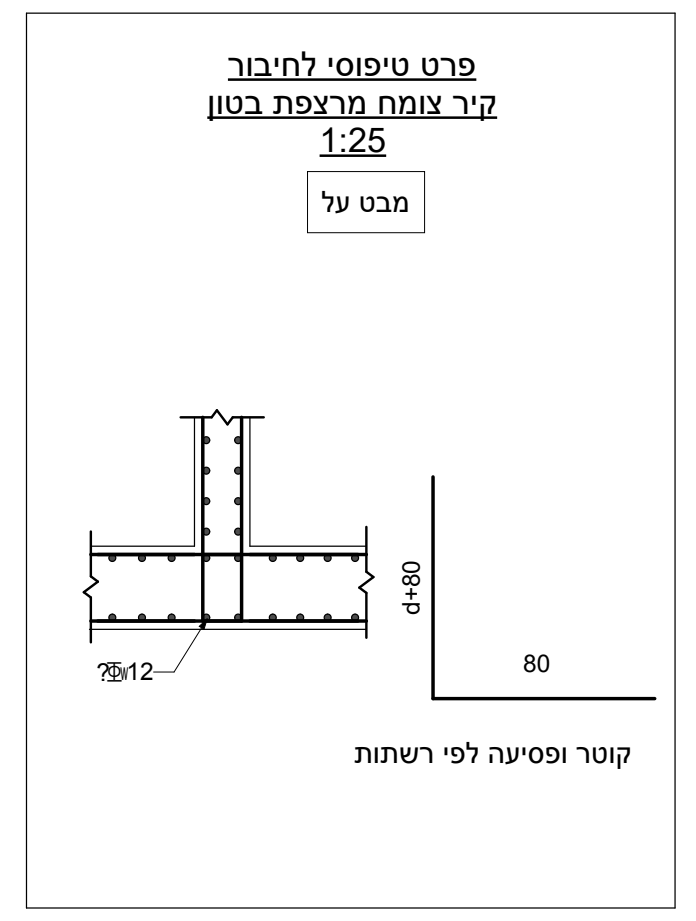
פרט טיפוסי לחיבור
קיר צומח מרצפת בטון
1:25
מבט על
80
קוטר ופסיעה לפי רשתות

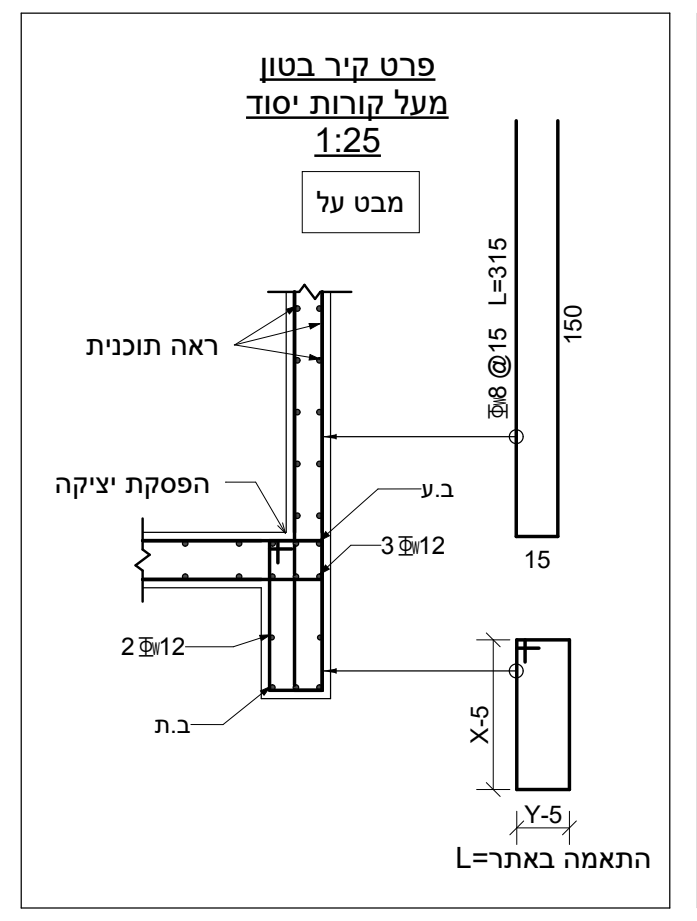
פרט קיר בטון
מעל קורות יסוד
1:25
מבט על
ראה תוכנית
הפסקת יציקה
ב.ע
ב.ת
Φ8 @15 L=315
150
X-5
Y-5
התאמה באתר=L

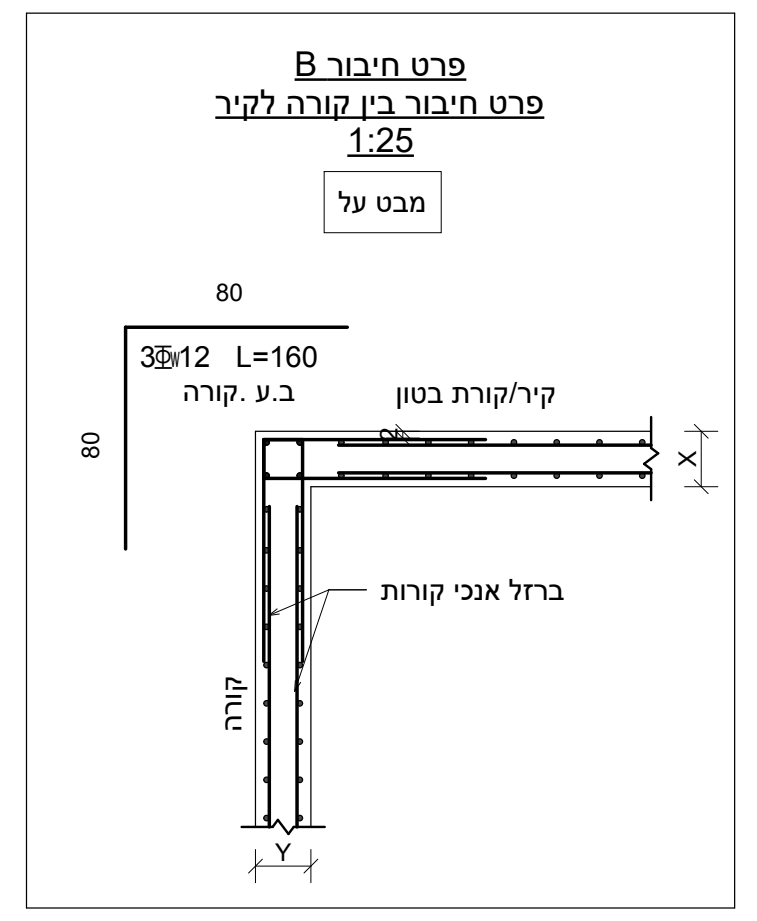
פרט חיבור B
פרט חיבור בין קורה לקיר
1:25
מבט על
80
3Φ12 L=160
ב.ע .קורה
קיר/קורת בטון
ברזל אנכי קורות
קורה
X
Y

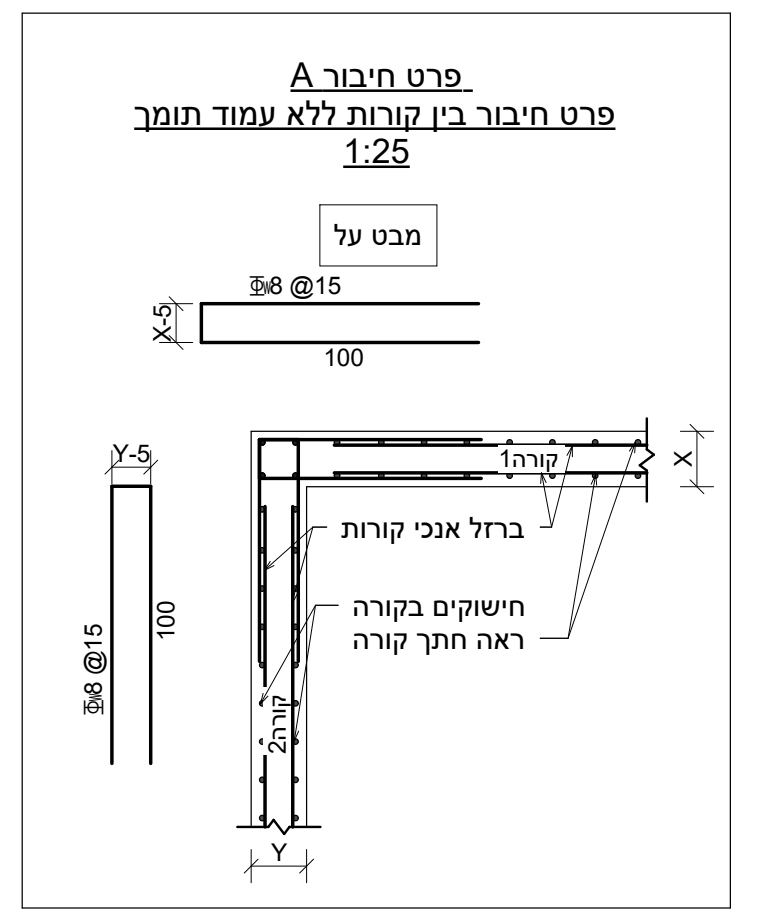
פרט חיבור A
פרט חיבור בין קורות ללא עמוד תומך
1:25
מבט על
Φ8 @15
X-5
100
Y-5
קורה1
קורה2
ברזל אנכי קורות
חישוקים בקורה ראה חתך קורה
X
Y

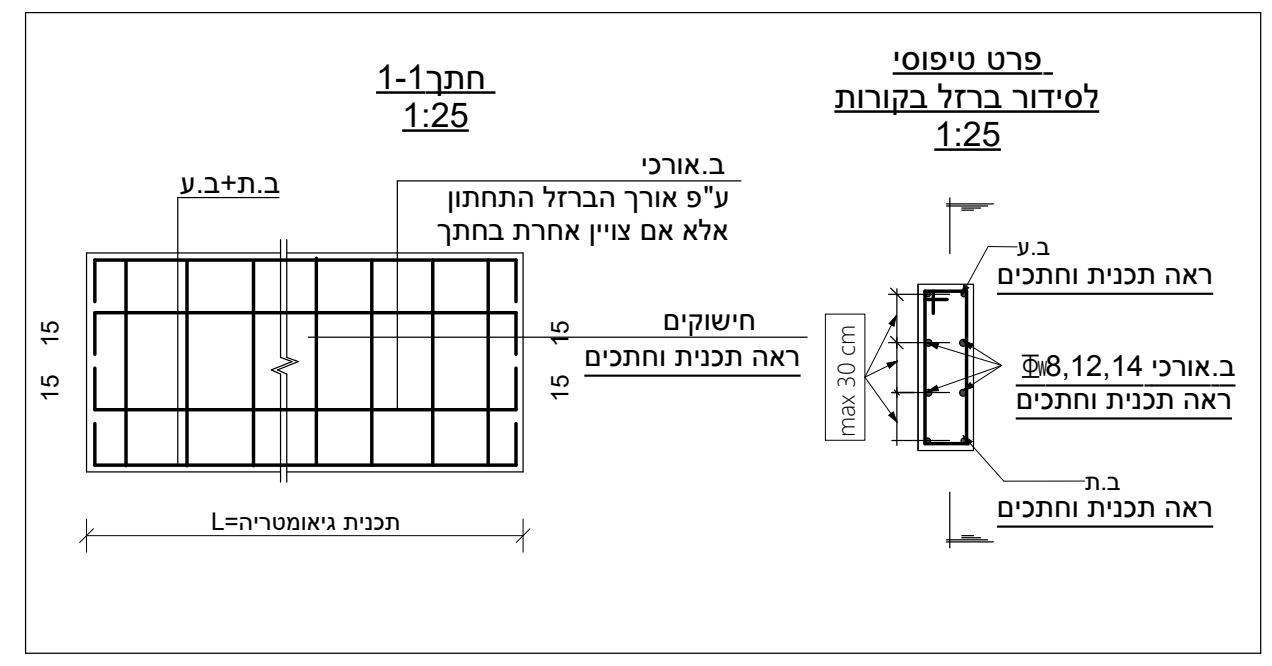
חתך1-1
1:25

פרט טיפוסי
לסידור ברזל בקורות
1:25
ב.ת+ב.ע
ב.אורכי
ע"פ אורך הברזל התחתון אלא אם צויין אחרת בחתך
חישוקים ראה תכנית וחתכים
15
תכנית גיאומטריה=L
ב.ע
ראה תכנית וחתכים
max 30 cm
ב.אורכי Φ8,12,14
ב.ת

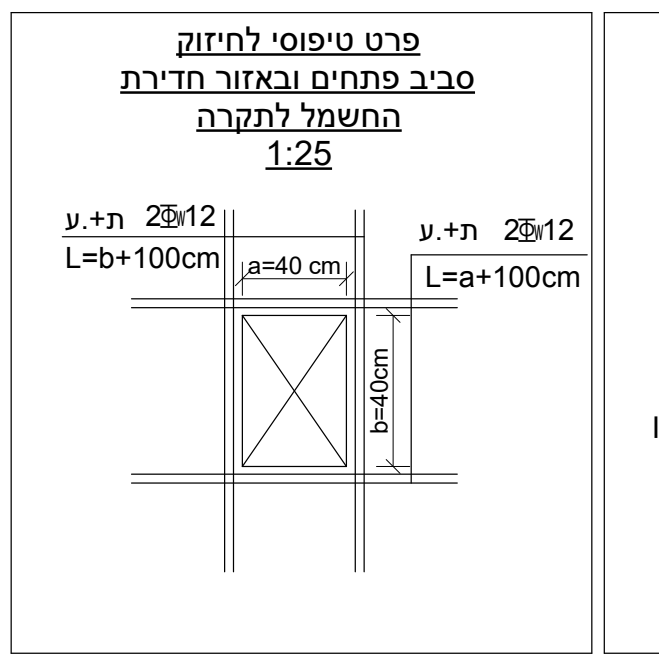
פרט טיפוסי לחיזוק
סביב פתחים ובאזור חדירת החשמל לתקרה
1:25
ת+.ע 2Φ12
L=b+100cm
a=40 cm
L=a+100cm
b=40cm

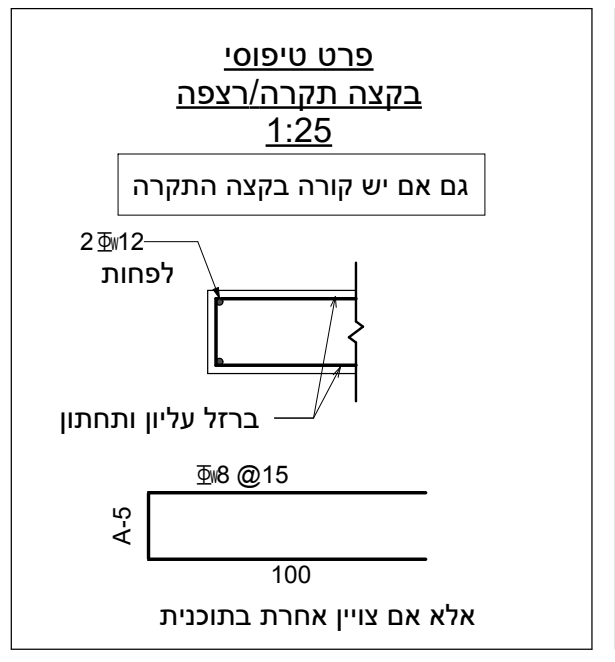
פרט טיפוסי
בקצה תקרה/רצפה
1:25
גם אם יש קורה בקצה התקרה
2Φ12 לפחות
ברזל עליון ותחתון
Φ8 @15
A-5
100
אלא אם צויין אחרת בתוכנית

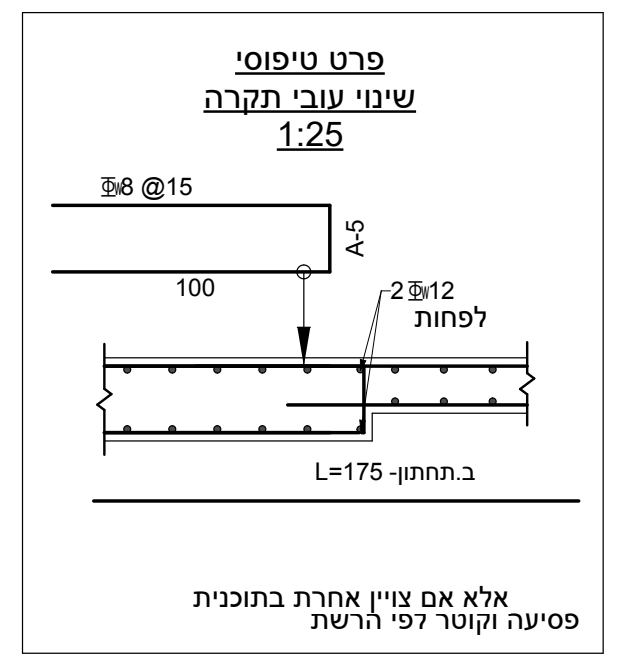
פרט טיפוסי
שינוי עובי תקרה
1:25
Φ8 @15
100
A-5
2Φ12 לפחות
ב.תחתון- L=175
אלא אם צויין אחרת בתוכנית
פסיעה וקוטר לפי הרשת

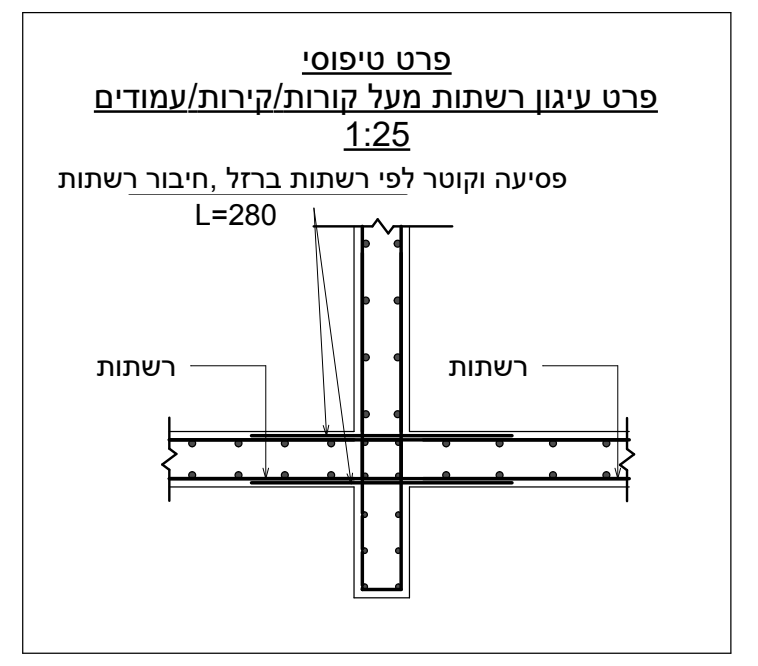
פרט טיפוסי
פרט עיגון רשתות מעל קורות/קירות/עמודים
1:25
פסיעה וקוטר לפי רשתות ברזל ,חיבור רשתות
L=280
רשתות

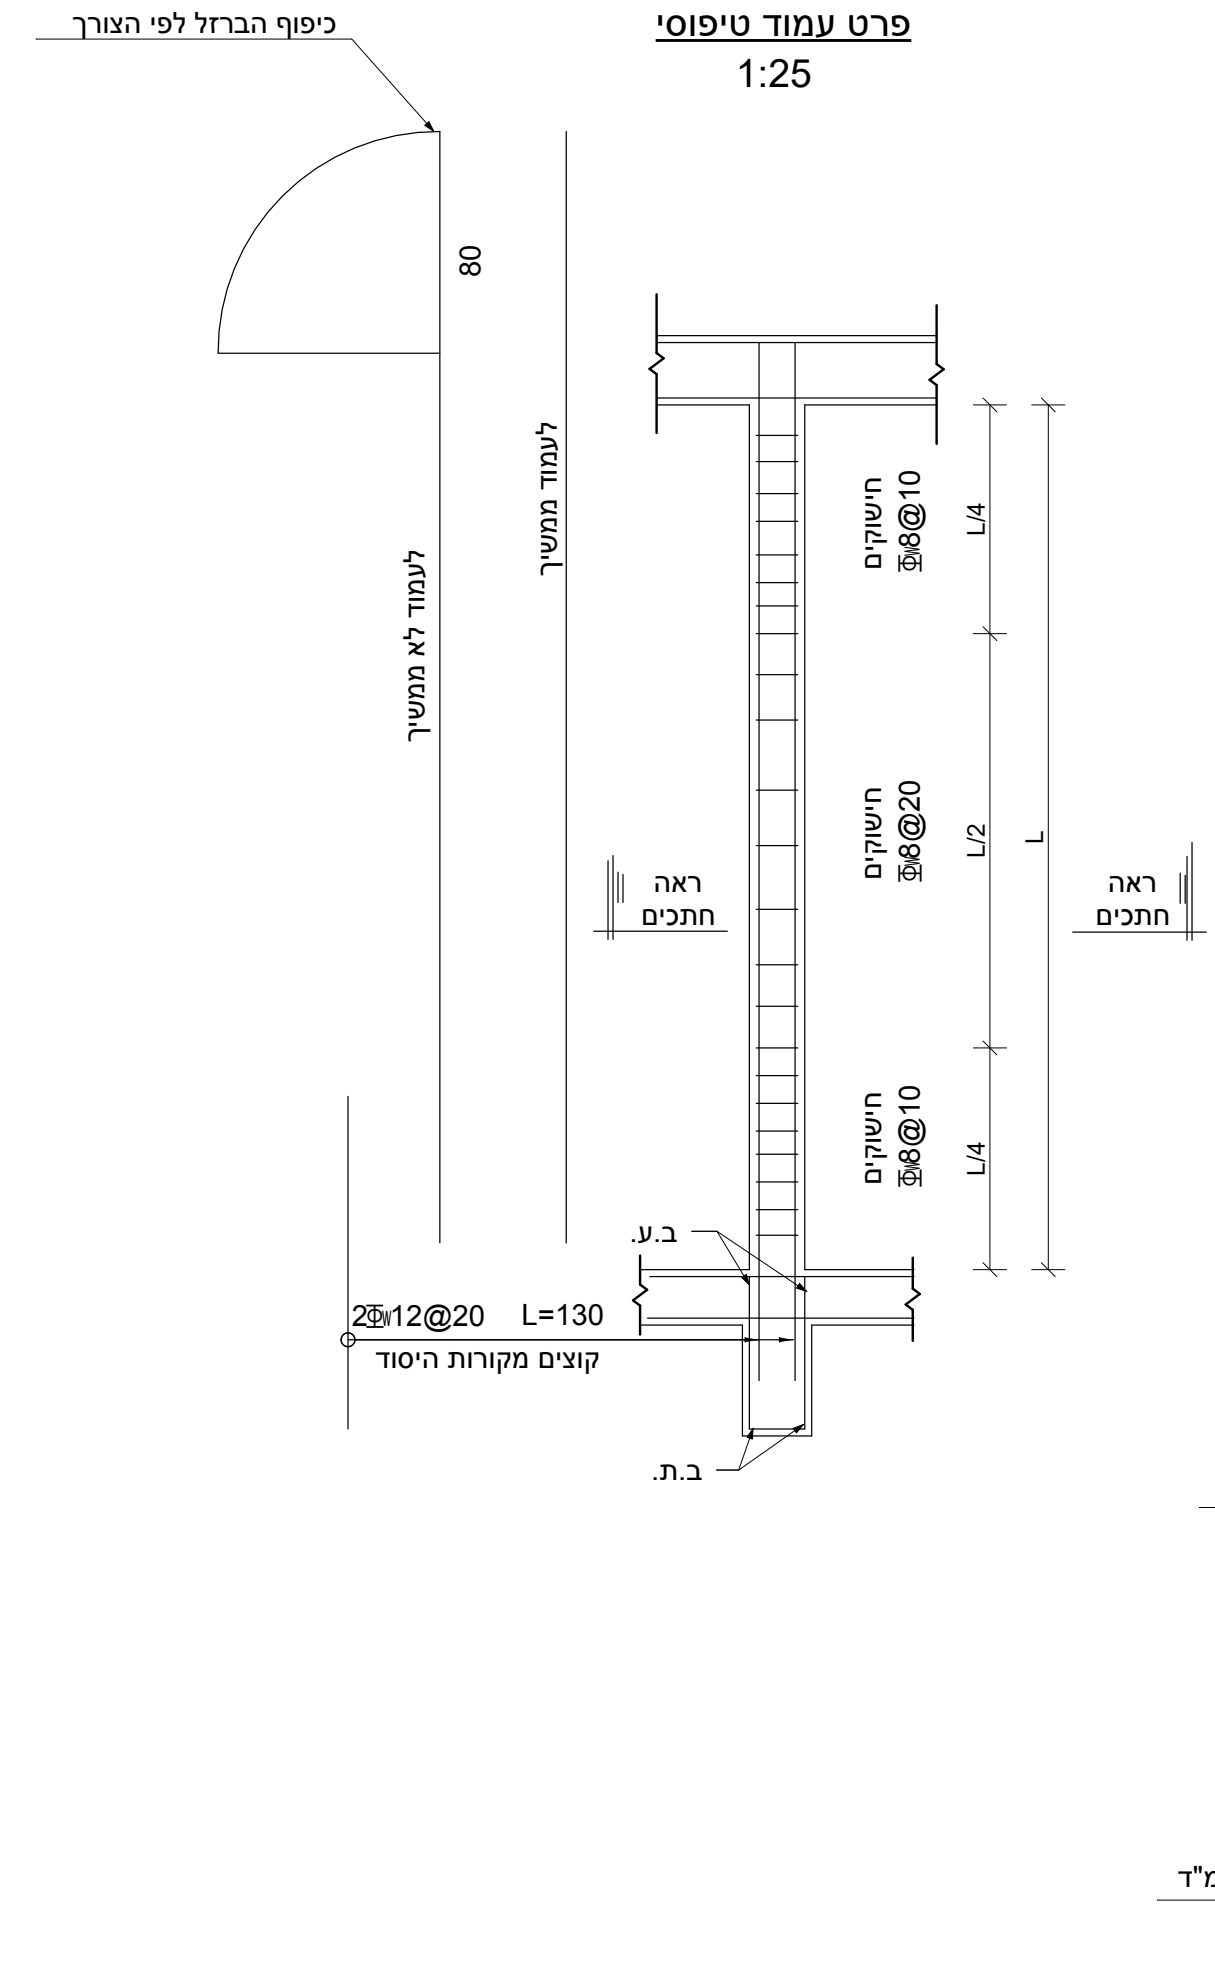
פרט עמוד טיפוסי
1:25
כיפוף הברזל לפי הצורך
80
לעמוד לא ממשיך
לעמוד ממשיך
חישוקים Φ8@10
חישוקים Φ8@20
L/4
L/2
L
ראה חתכים
ב.ע
2Φ12@20 L=130
קוצים מקורות היסוד
ב.ת

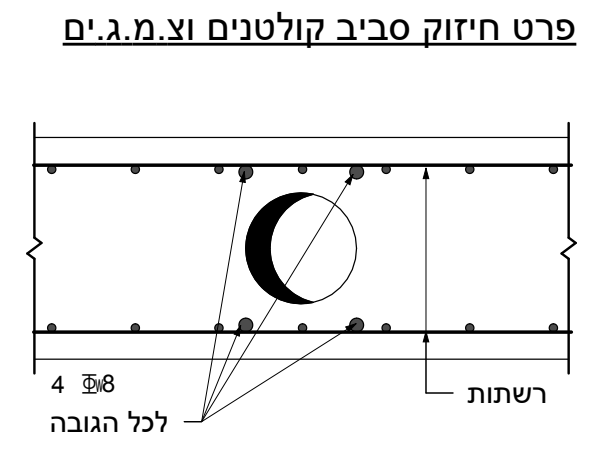
פרט חיזוק סביב קולטנים וצ.מ.ג.ים
4 Φ8
לכל הגובה
רשתות

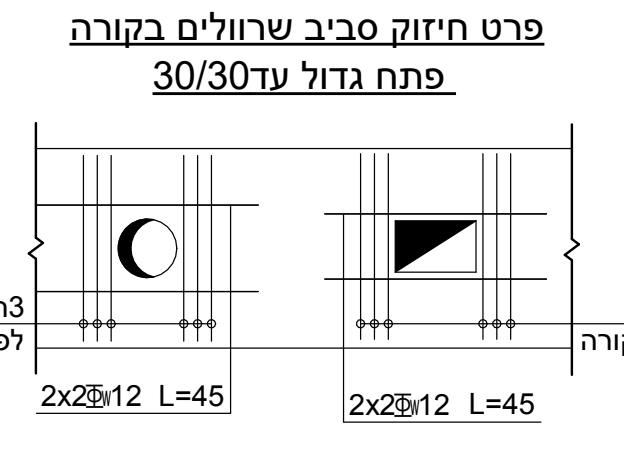
פרט חיזוק סביב שרוולים בקורה
פתח גדול עד30/30
3חישוקים לפי חתך הקורה
2x2Φ12 L=45

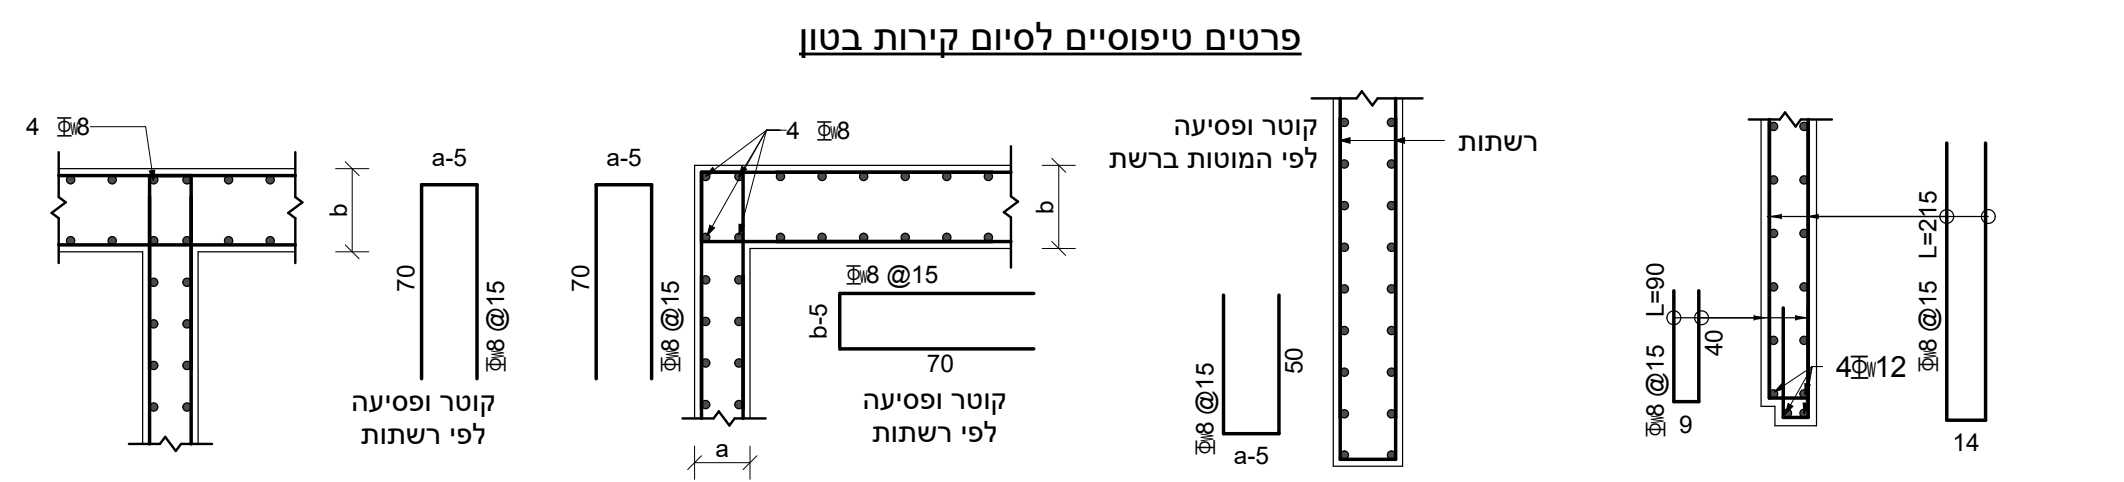
פרטים טיפוסיים לסיום קירות בטון
4 Φ8
a-5
b
70
Φ8 @15
קוטר ופסיעה לפי רשתות
a
b-5
קוטר ופסיעה לפי המוטות ברשת
רשתות
50
L=90
L=215
40
4Φ12
9
14

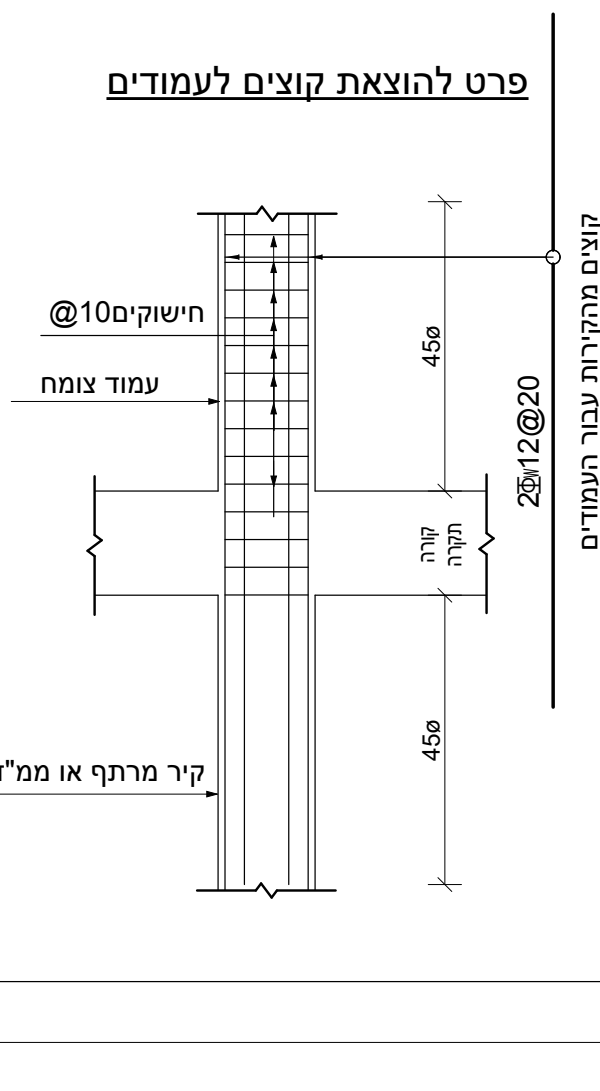
פרט להוצאת קוצים לעמודים
חישוקים@10
עמוד צומח
45ø
2Φ12@20
קוצים מהקירות עבור העמוד
קיר מרתף או ממ"ד

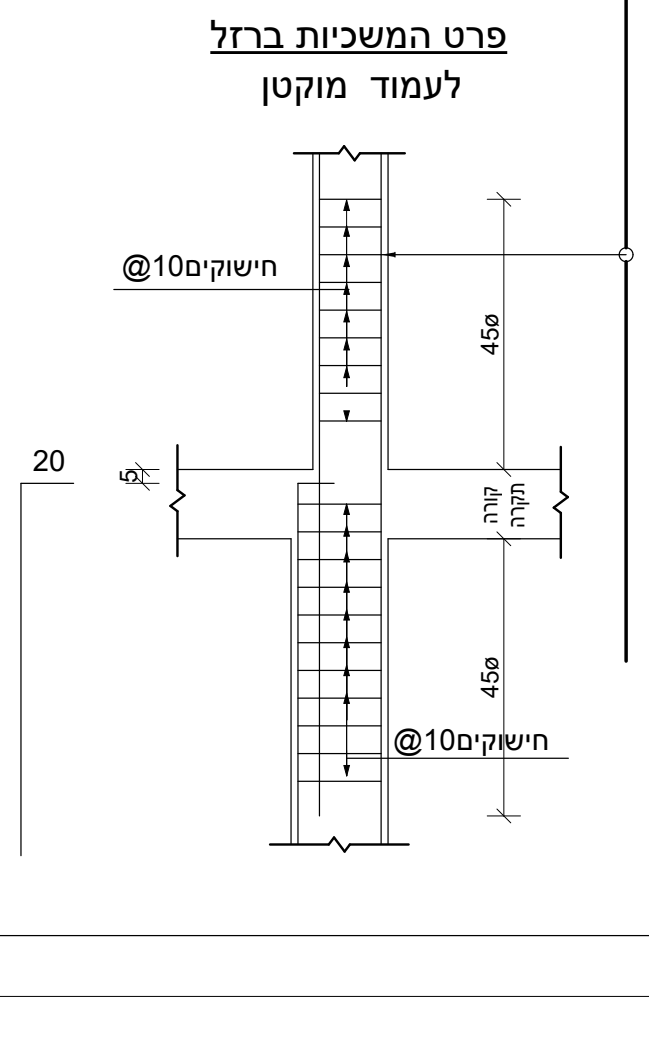
פרט המשכיות ברזל
לעמוד מוקטן
חישוקים@10
45ø
20

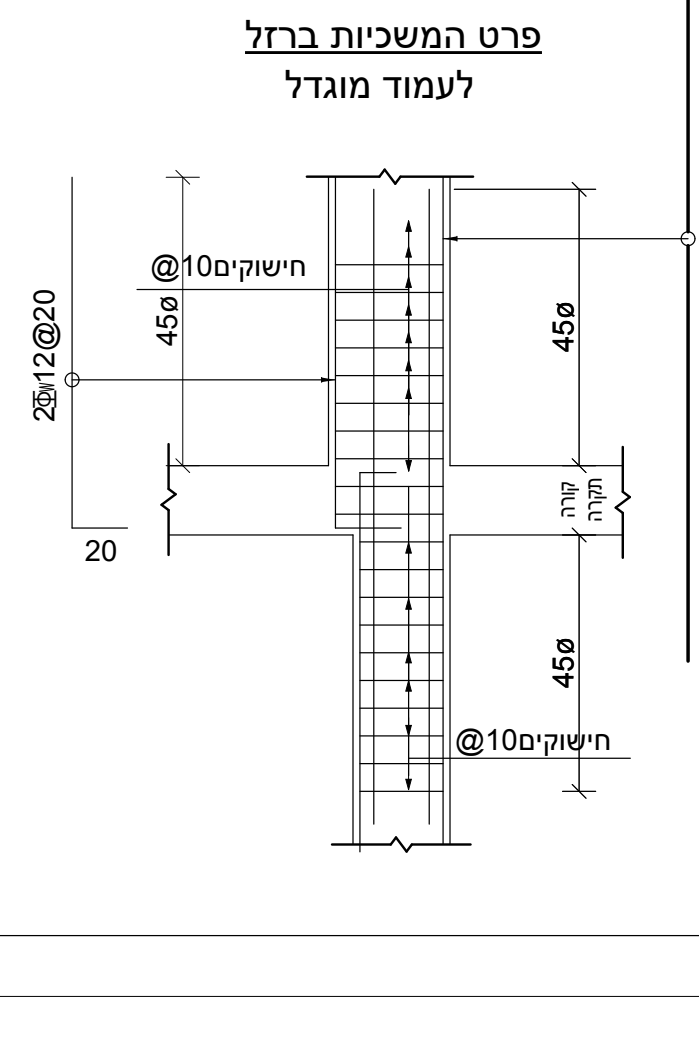
פרט המשכיות ברזל
לעמוד מוגדל
חישוקים@10
2Φ12@20
45ø
20

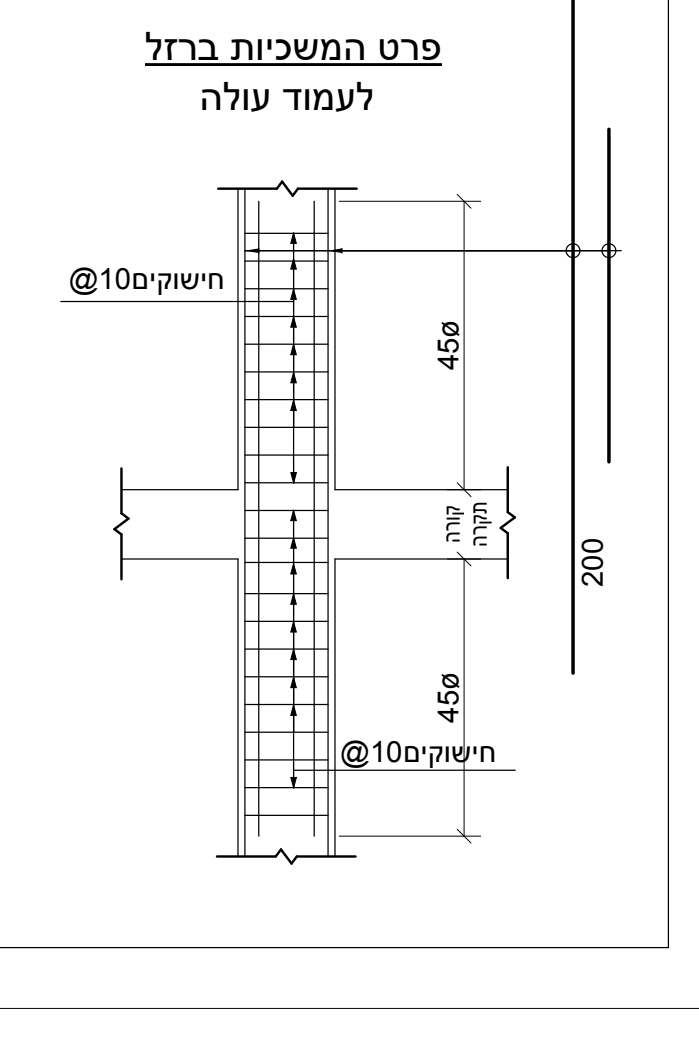
פרט המשכיות ברזל
לעמוד עולה
חישוקים@10
45ø
200

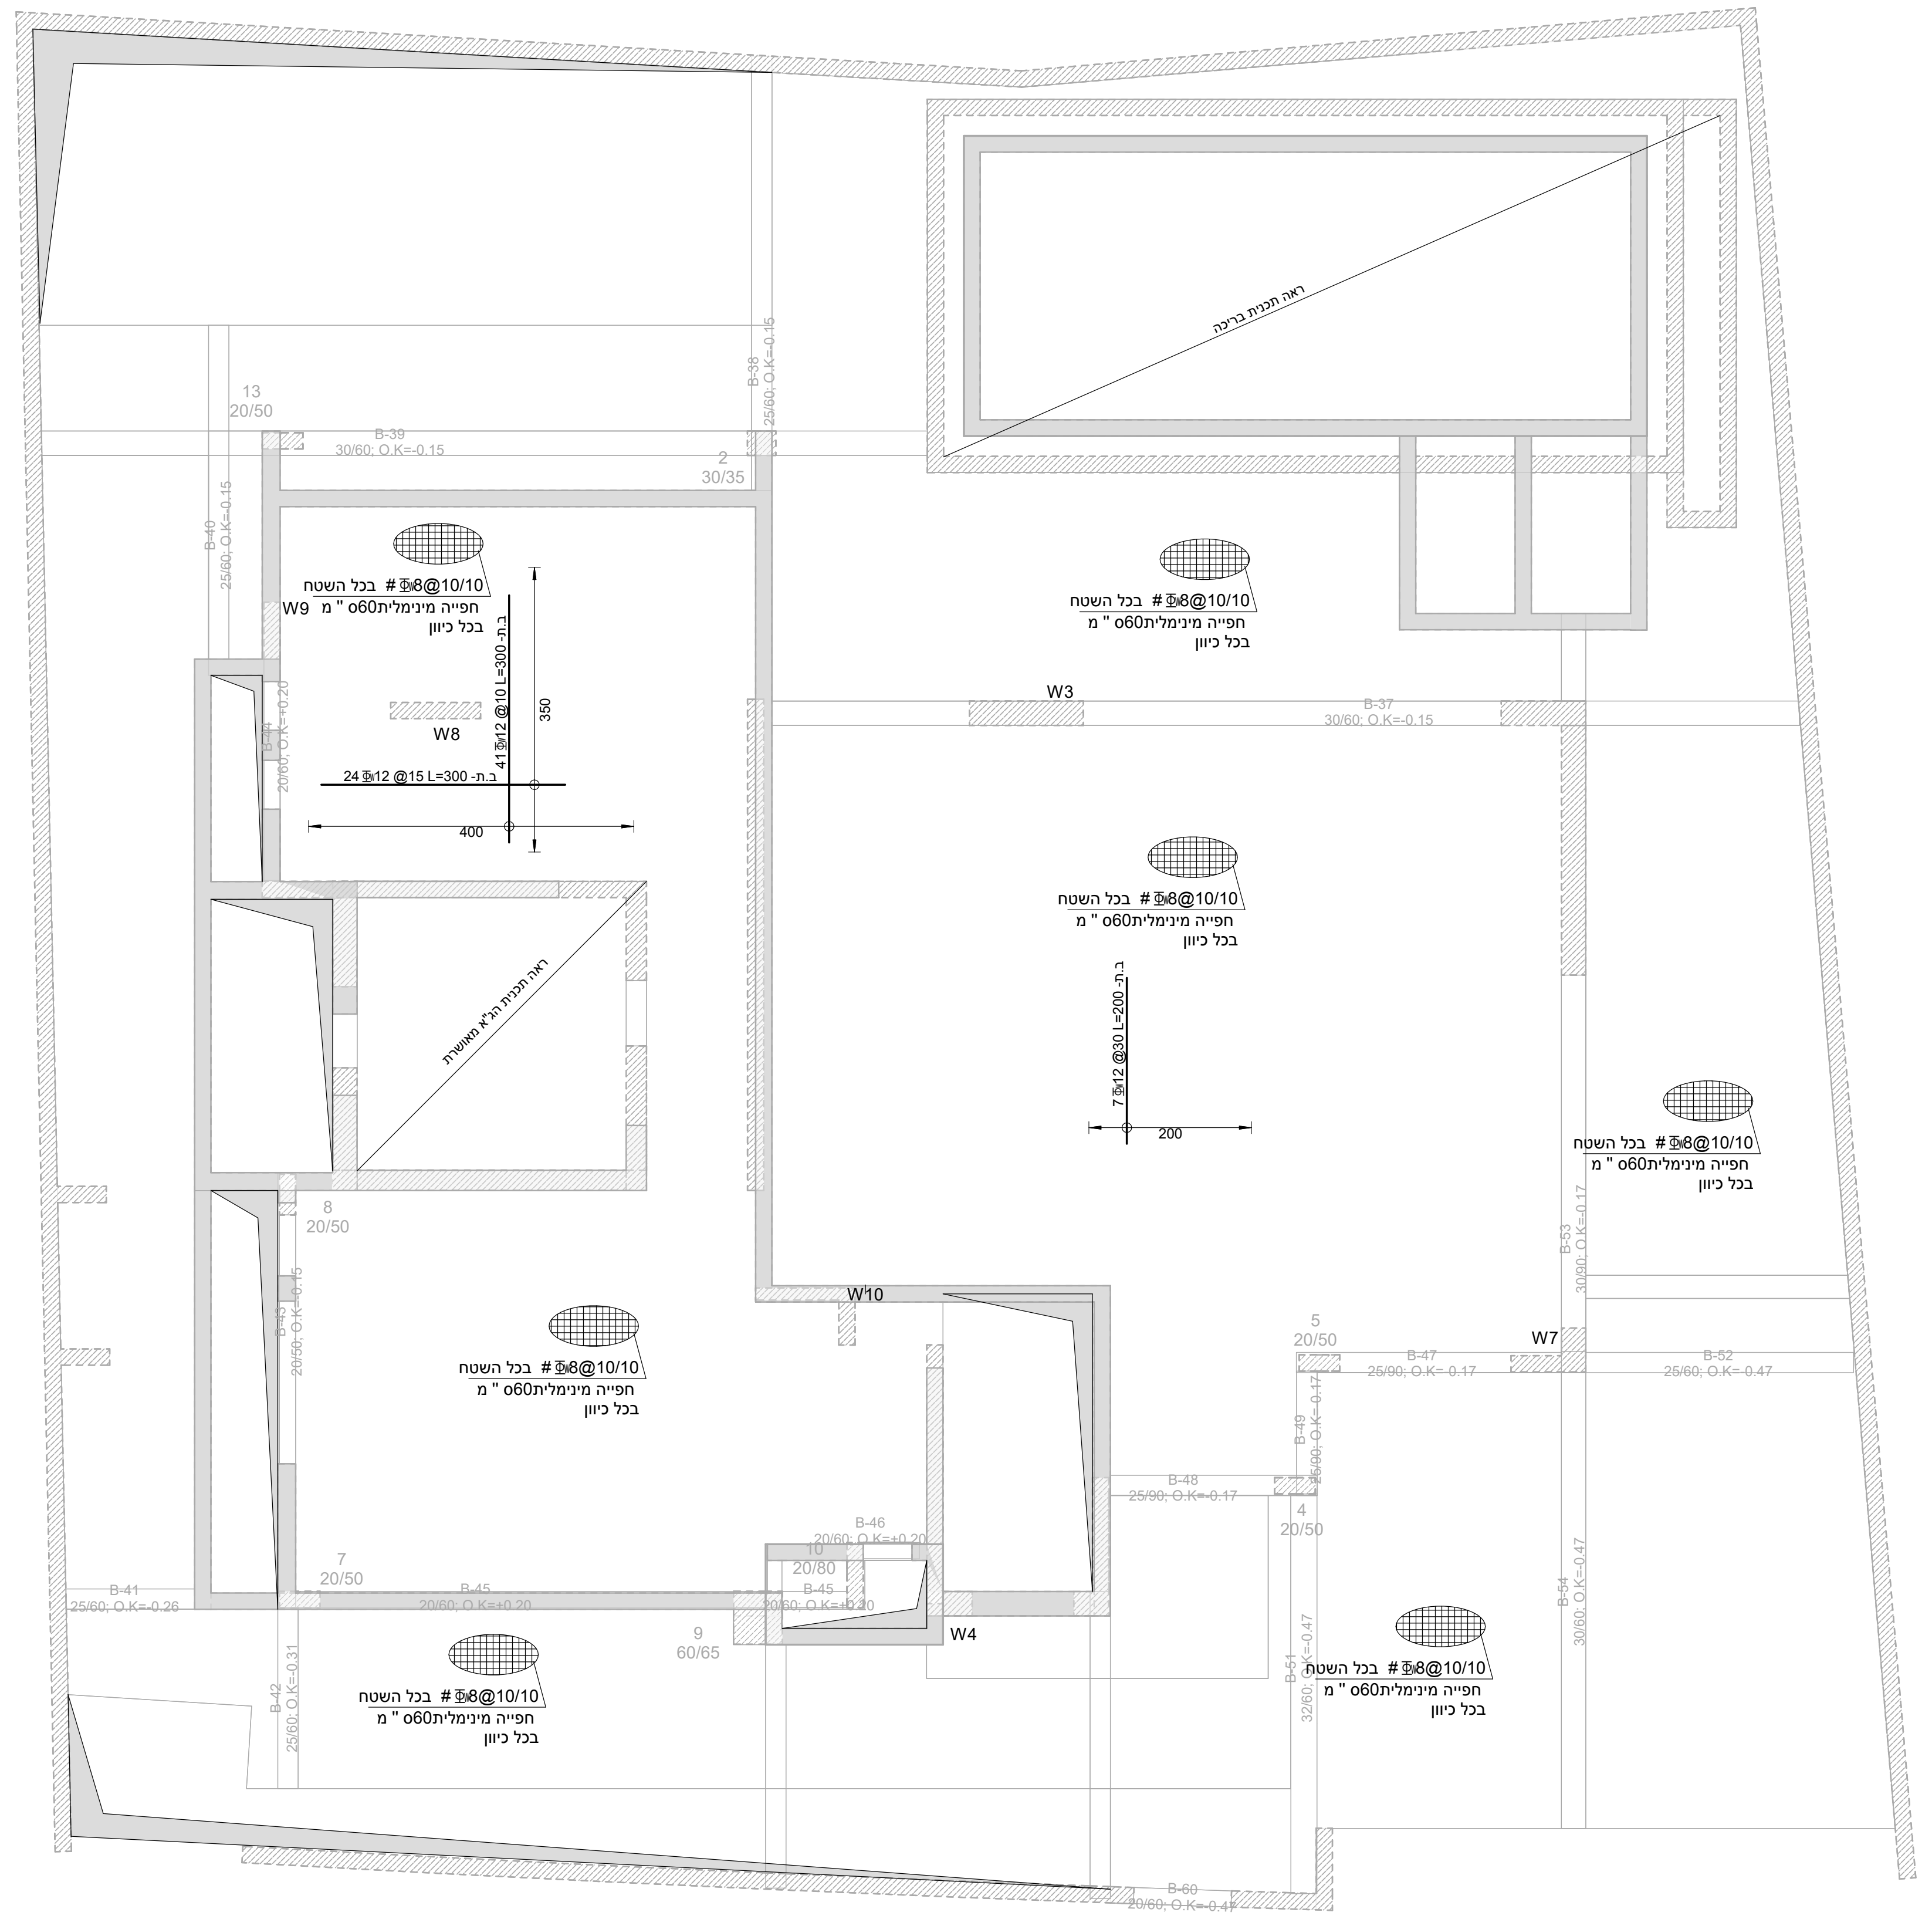
ברזל תחתון
1 : 50
W9
W8
W3
W10
W7
W4
Φ8@10/10 # בכל השטח
חפייה מינימלית60 "מ בכל כיוון

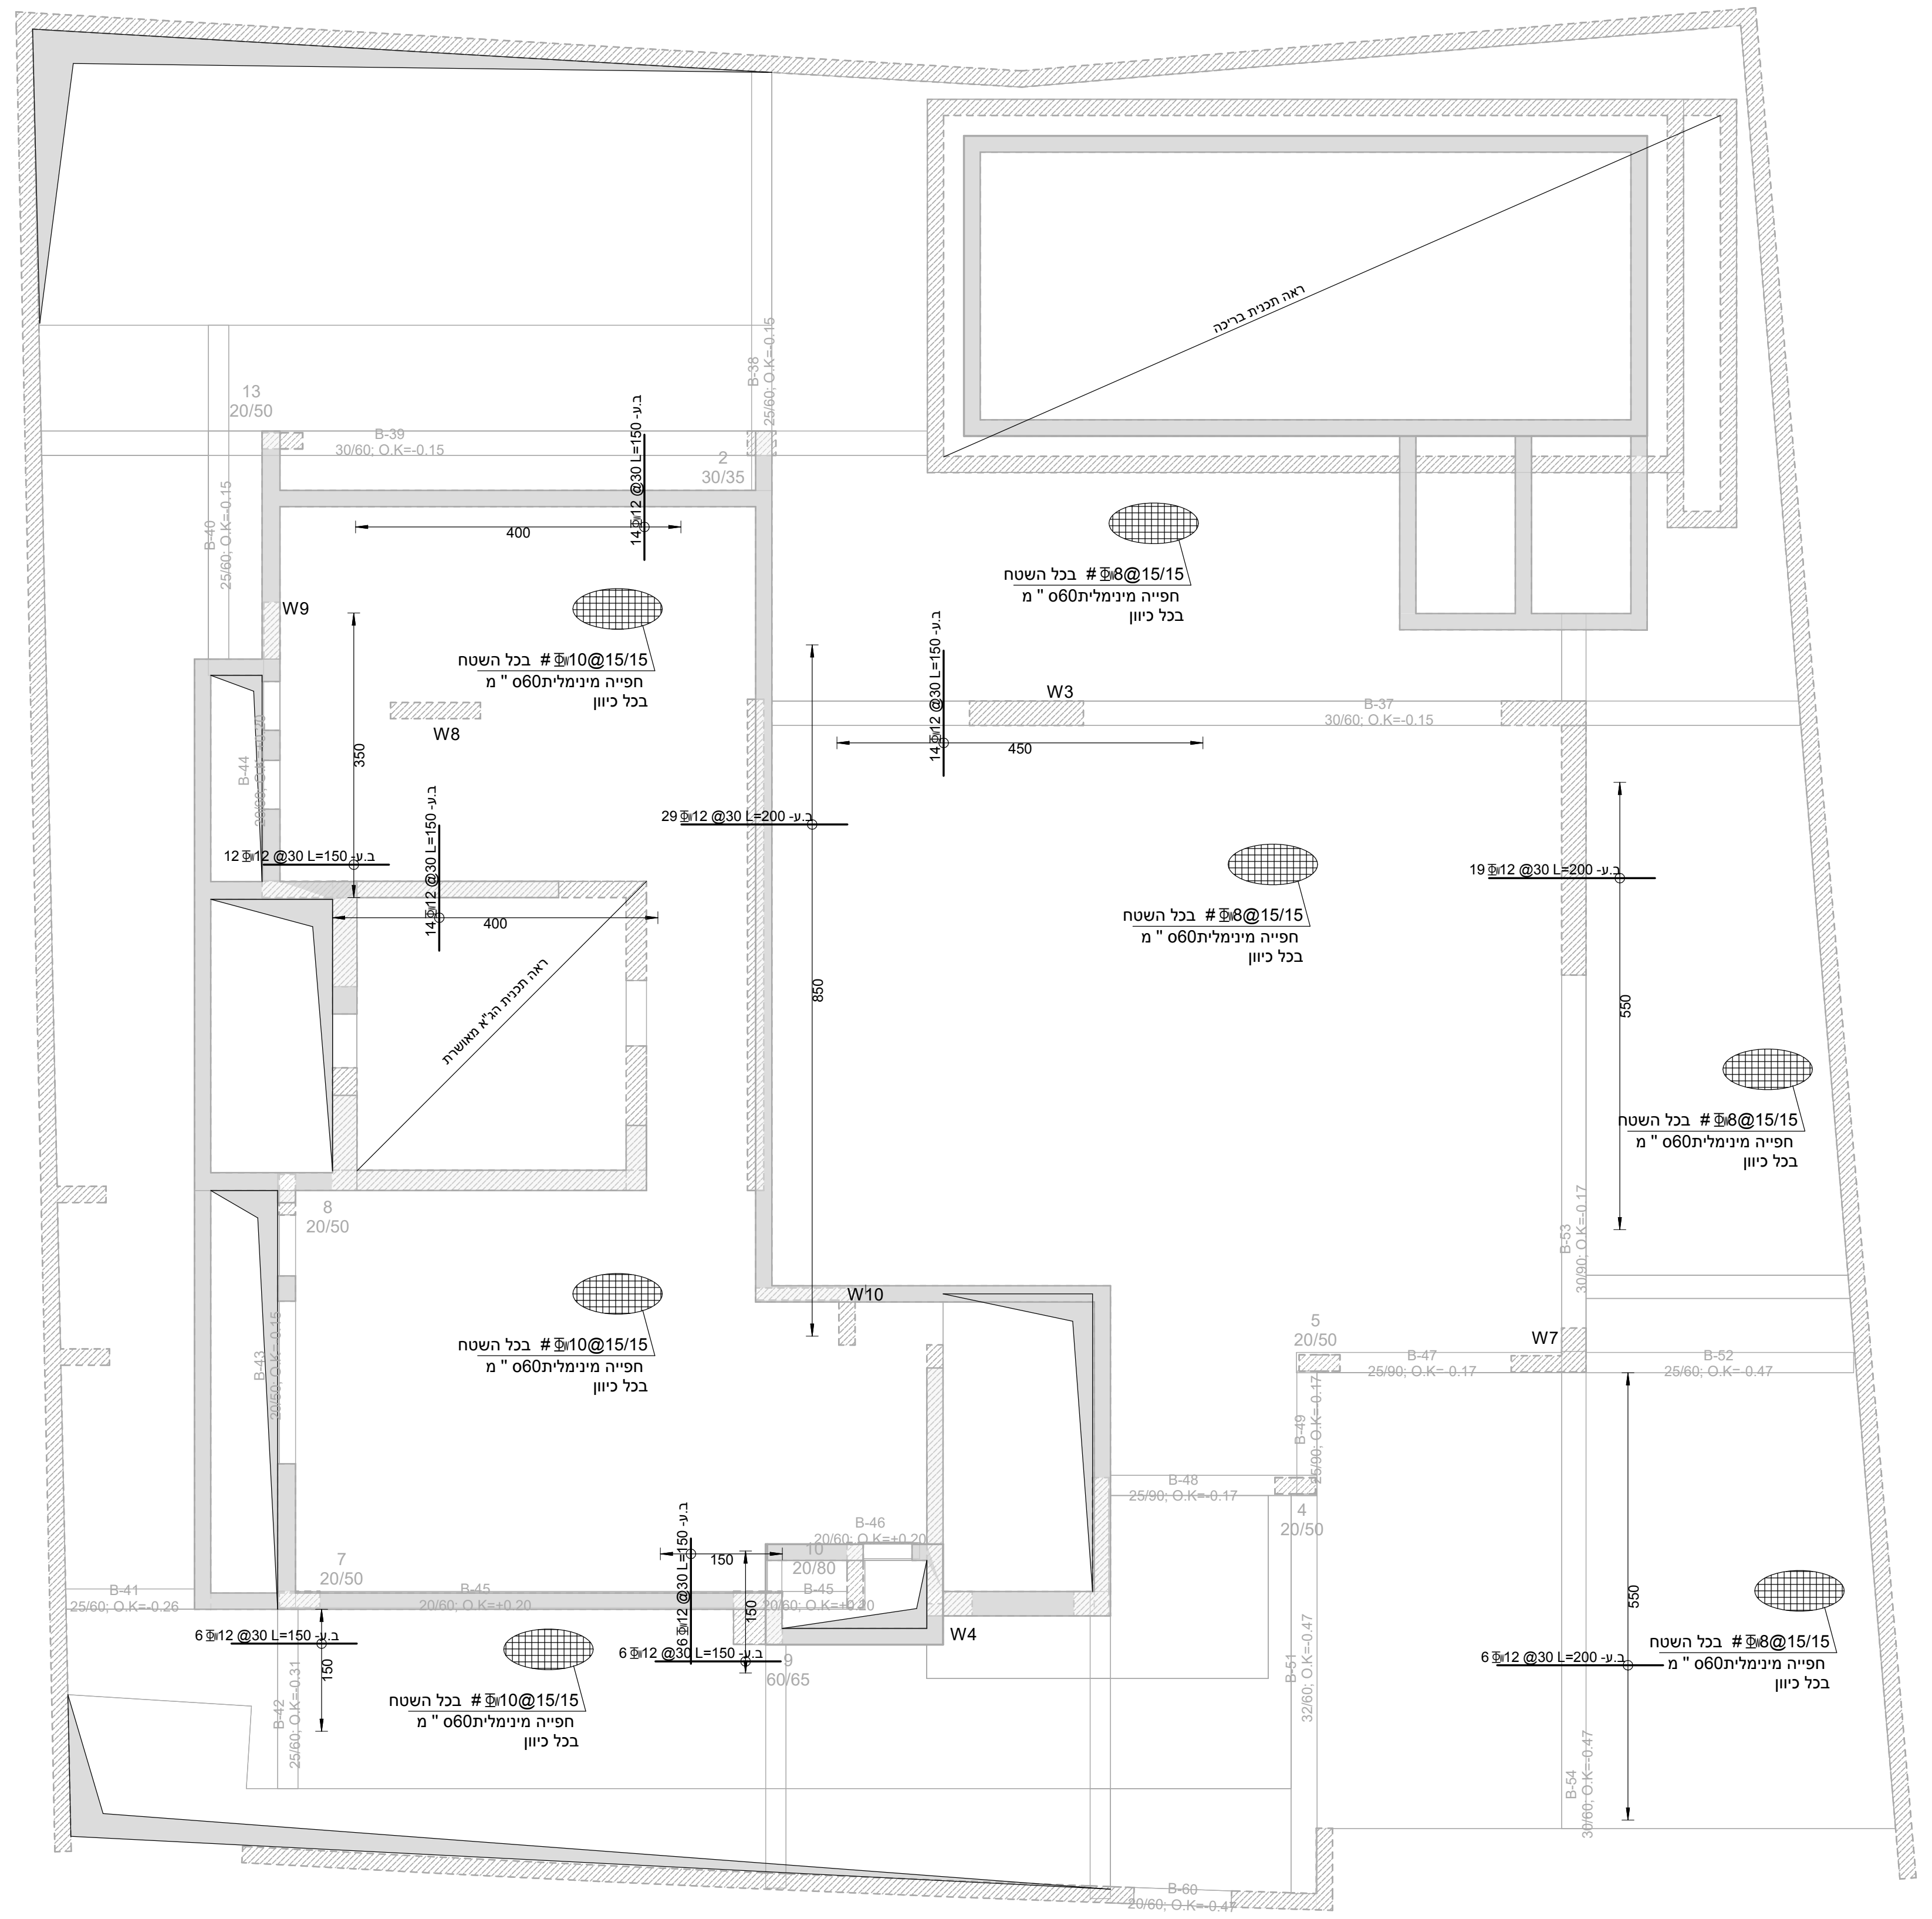
ברזל עליון
1 : 50
W9
W8
W3
W10
W7
W4
Φ8@15/15 # בכל השטח
Φ10@15/15 # בכל השטח
חפייה מינימלית60 "מ בכל כיוון

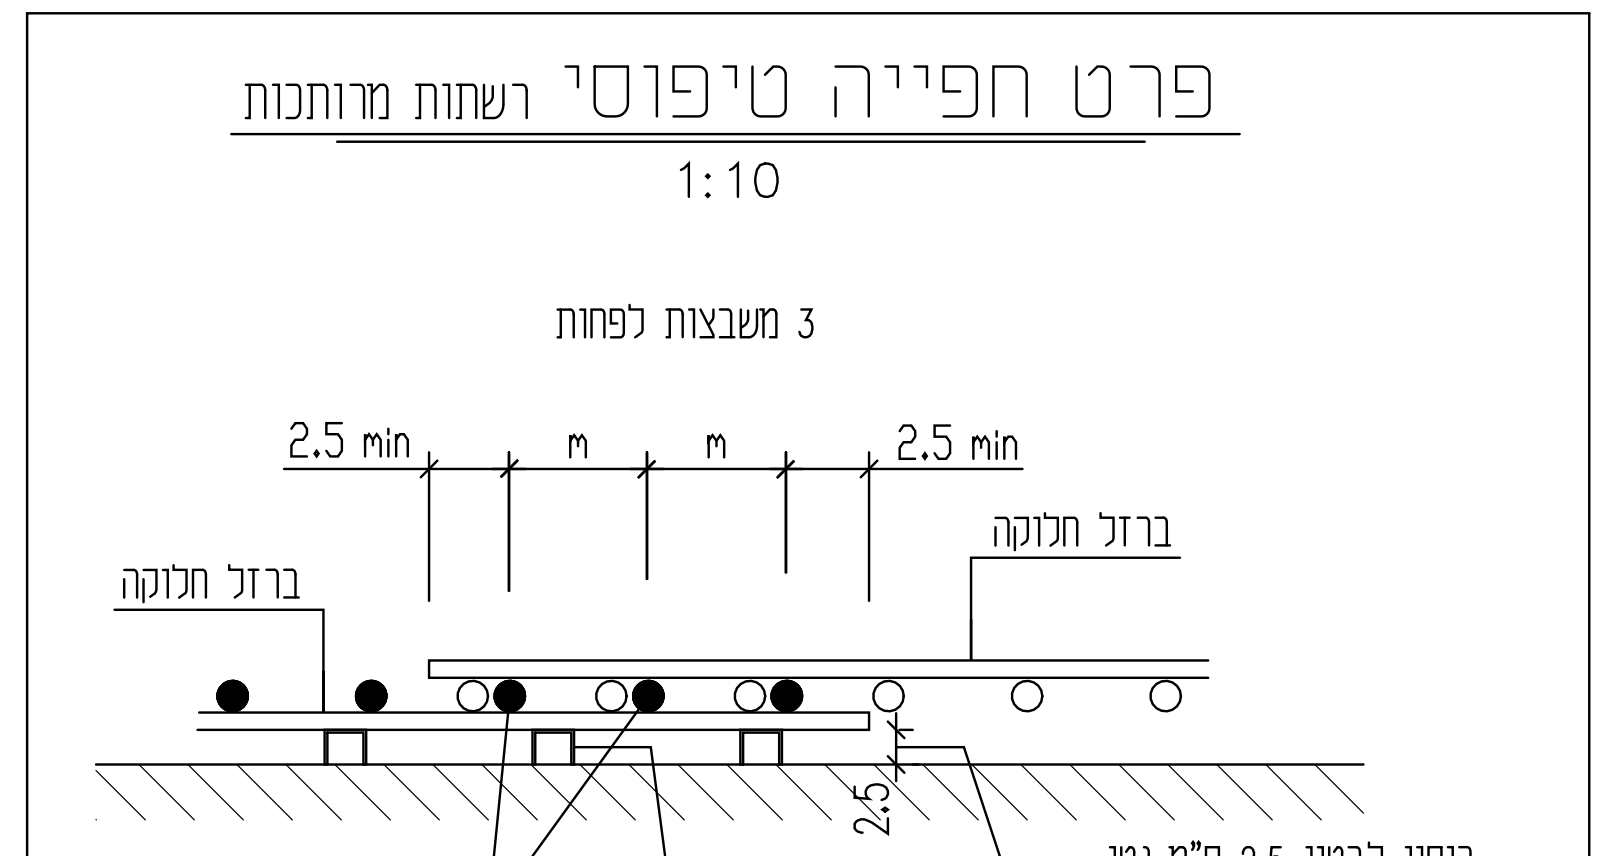
פרט חפייה טיפוסי רשתות מרותכות
1:10
3 משבצות לפחות
2.5 min
m
m
2.5 min
ברזל חלוקה
ברזל חלוקה
2.5
ברזל ראשי
שומרי מרחק
כיסוי לבטון 2.5 ס"מ נטו

הערות

1. יש לקרוא תוכנית זו יחד עם תוכנית חשמל אינסטלציה ואיטום.
2. תכנית זאת מיועדת לביצוע רק במידה ומולאו שני תנאים בסיסיים:
   א .אישור האדריכל
   ב . התוכנית מתאימה להיתר הבניה)באישור המהנדס האחראי על הביצוע)
3. תוכנית זאת תבוצע רק לאחר חתימת האדריכל והמודד עליה המאשרים כי היא מתאימה להיתר בניה והתקנים מבחינת העמדת המבנים במגרש
4. מיקום המבנה ביחס למגרש יקבע ע" י המודד בהתאם לתוכנית העמדה של האדריכל.
5. עובי כיסוי הבטון יהיה2.5ס " מ בכל האלמנטים מלבד אלה שבאים במגע עם הקרקע - שם עובי הכיסוי יהיה4ס "מ.
6. הארקת יסוד -יש לעיין בתכנית יועץ חשמל.
7. אין להעביר צינורות בקוטר גדול מ-50מ "מ ללא אישור מהמהנדס המתכנן.
8. דוח קרקע הינו חלק בלתי נפרד מתכנית זו.
9 סוג בטון ב-30 דרגת חשיפה 3.
10. יש לבצע התאמה בין תכניות האדריכליות ושאר היועצים לבין תכנית זו - לפני ביצוע.
11. אין להעמיס את המרפסות הן לפני הבנייה , והן אחרי הבנייה בעומס הגדול מהמצויין בתכנית!
12. פירוק טפסות בכל שלב יהיה - אך ורק באישור בכתב ממתכנן הקונסטרוקציה.

▨	עמוד / קיר-צומח
■	עמוד / קיר-מפסיק

*סוגי בטון ראה ברשימת כמויות

מס 'עידכון	מהות העידכון	ע"י	תאריך
P1	W8 הזזת עמוד		1.11.26
P0	תוכניות לביצוע		5.10.26

עומסים

עומס קבוע נוסף	500 =ק"ג /מ"ר
עומס שימושי	150 =ק"ג /מ"ר
עומס מרפסות	350=ק"ג /מ"ר

גובה מפלס)אדריכלות): +0.00
מפלס פני בטון: -0.15

P1 מעודכן לתאריך: 1.11.26

לעיון	לאישור	למכרז	לביצוע
○	○	○	●

שם הפרויקט:
וילה ליאור ואביחי אטואן

תאור השרטוט:
קומה קרקע -פריסת ברזל

מס 'השרטוט:
K-23

מס 'פרויקט: WORK-167
קנ"מ:
דוא" ל: tal@yarin-eng.co.il
גודל גליון: 1850 X 900
מהנדס אחראי: טל שיי אטיאס
מהנדס: רותם מאיר

ירין הנדסה
טל אטיאס: 050-444-4730
tal@yarin-eng.co.il
YARIN
תכנון | ניהול | פיקוח מבנים

01/11/2026 10:16:20
C:\Users\LENOVO P340\Desktop\עבודה\תכניות רותם\work 167-רויטו\מודל רויט\קובץ\cons\פתיחת תיקיה ריטאביחי אטואן\ התחלתי.rvt