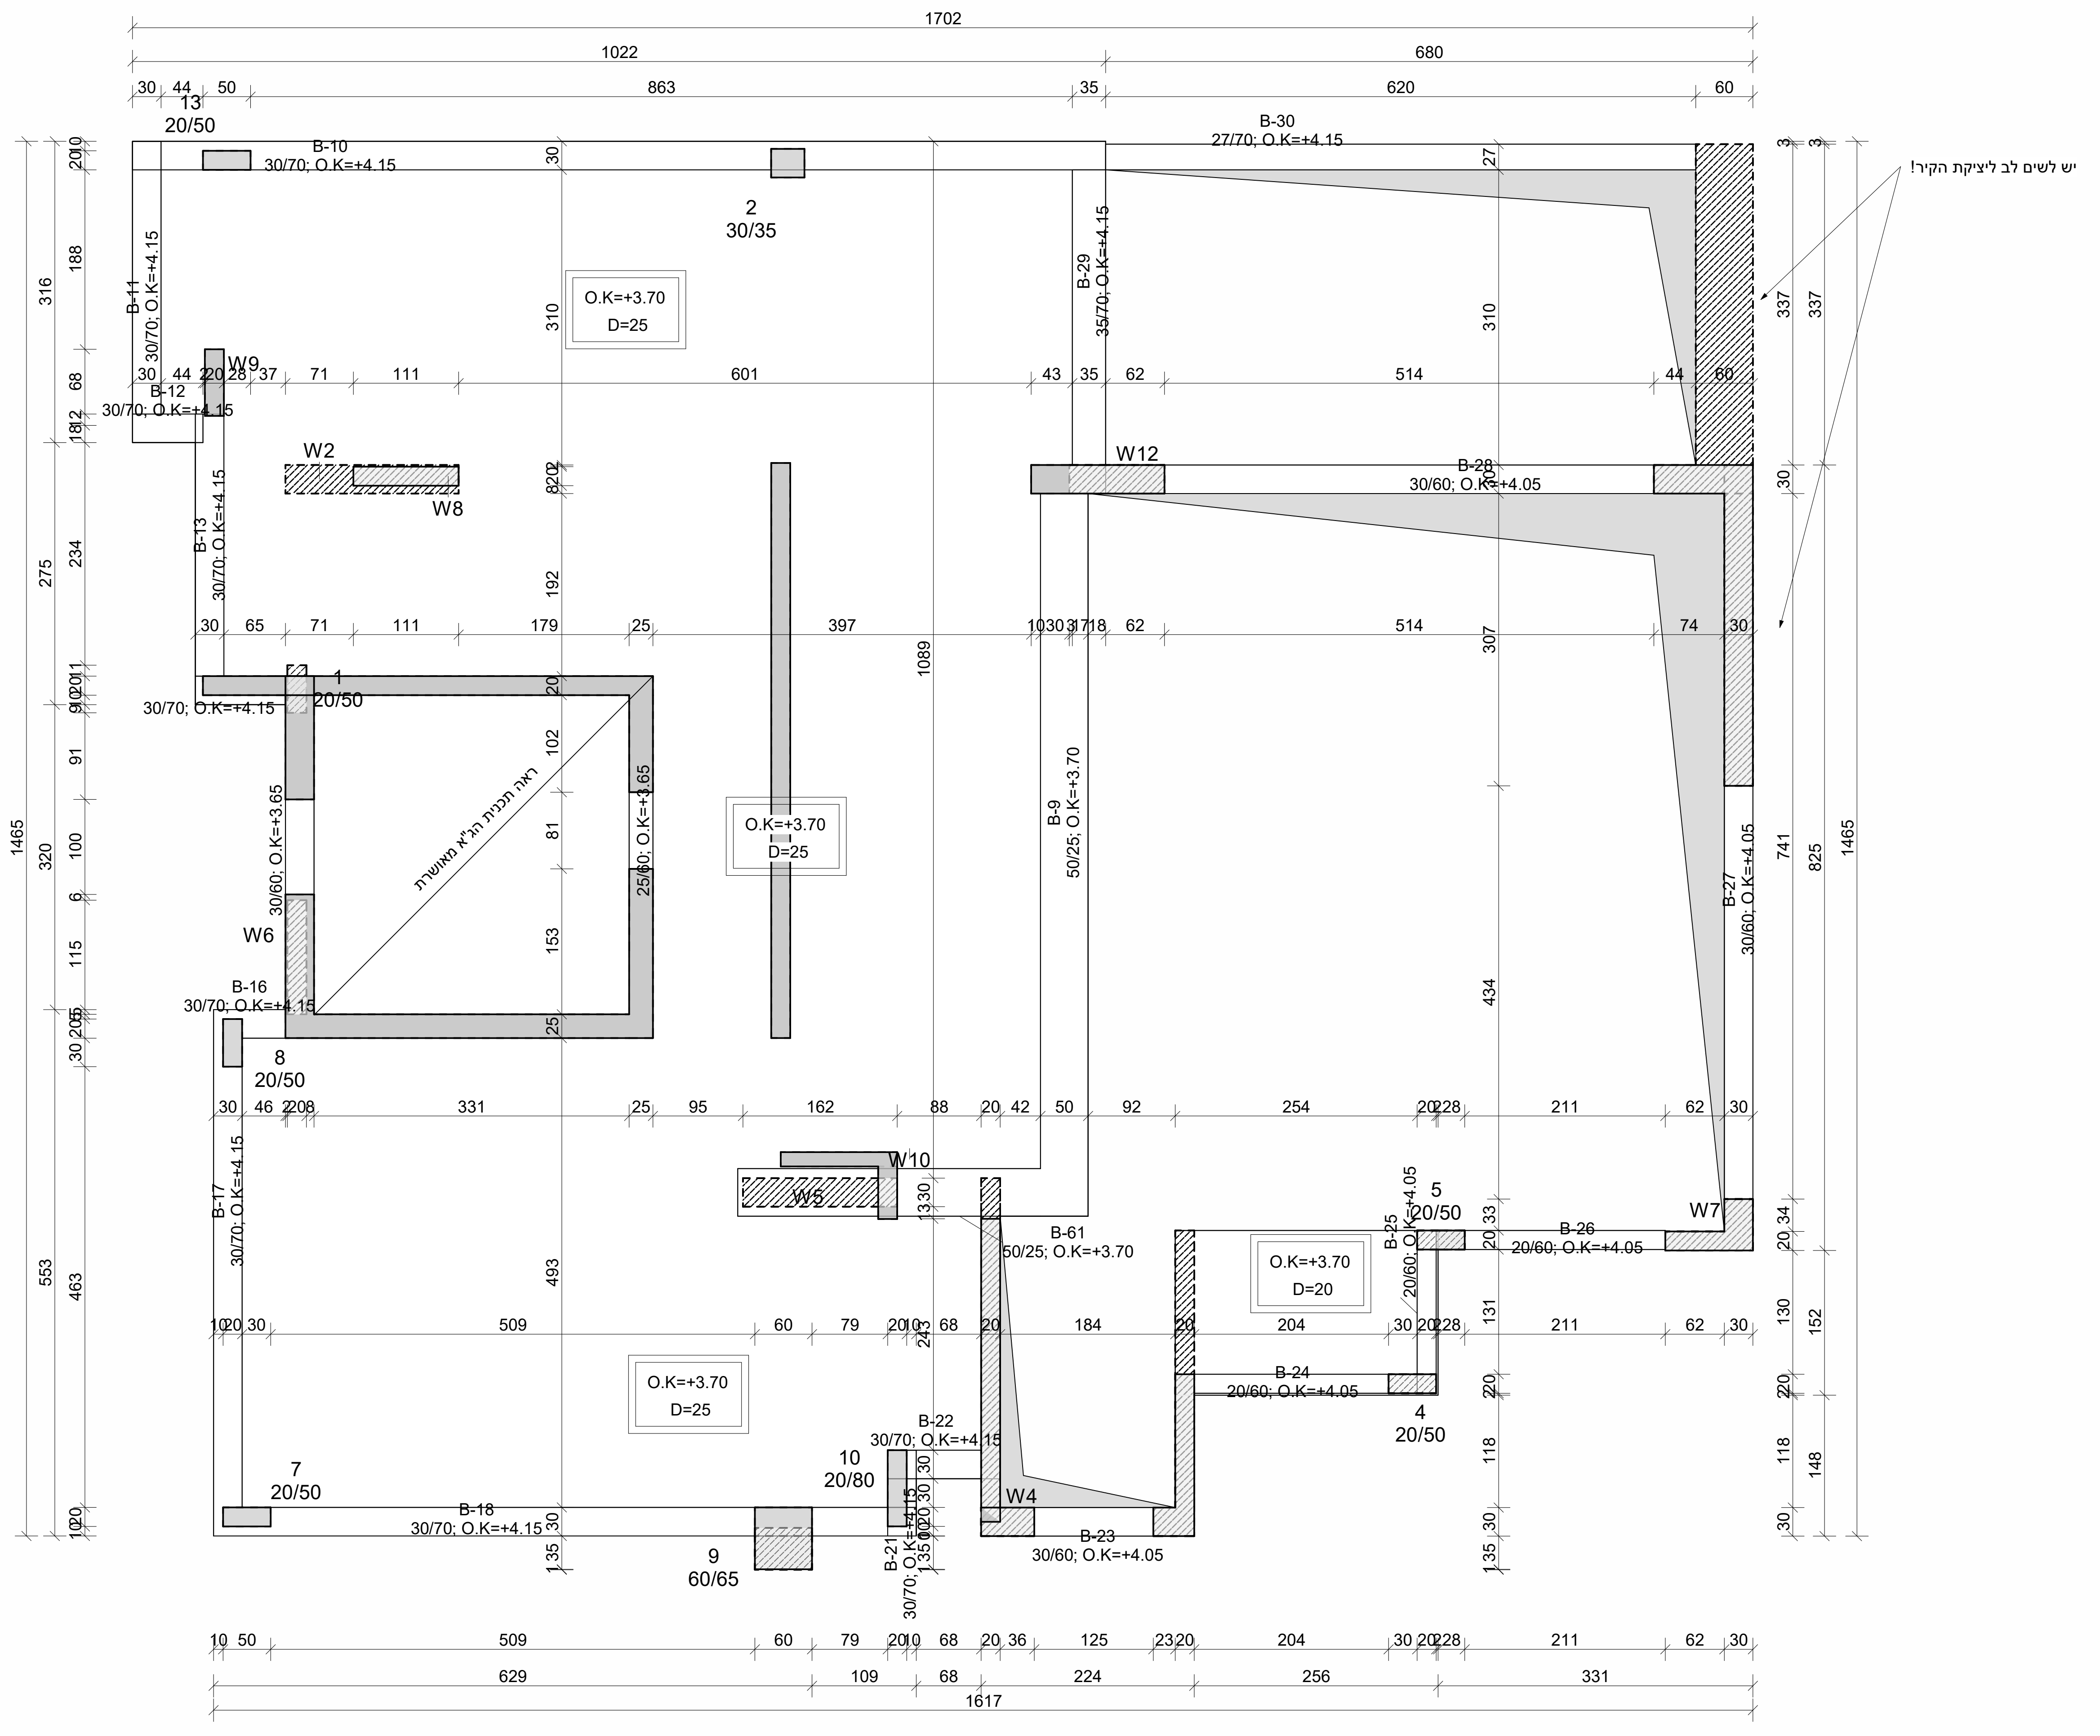
1702
1022
680
863
620
13
20/50
B-10
30/70; O.K=+4.15
2
30/35
B-30
27/70; O.K=+4.15
O.K=+3.70
D=25
B-11
30/70; O.K=+4.15
B-12
30/70; O.K=+4.15
W9
B-29
35/70; O.K=+4.15
W2
W8
W12
B-28
30/60; O.K=+4.05
B-13
30/70; O.K=+4.15
1
20/50
ראה תכנית הג"א מאושרת
30/60; O.K=+3.65
25/60; O.K=+3.65
W6
B-16
30/70; O.K=+4.15
8
20/50
B-9
50/25; O.K=+3.70
B-27
30/60; O.K=+4.05
יש לשים לב ליציקת הקיר!
W10
W5
B-17
30/70; O.K=+4.15
B-61
50/25; O.K=+3.70
5
20/50
B-25
20/60; O.K=+4.05
B-26
20/60; O.K=+4.05
W7
O.K=+3.70
D=20
B-24
20/60; O.K=+4.05
4
20/50
B-22
30/70; O.K=+4.15
10
20/80
7
20/50
B-18
30/70; O.K=+4.15
9
60/65
B-21
30/70; O.K=+4.15
W4
B-23
30/60; O.K=+4.05
1089
1465
1617

תוכנית בקומה ב

1 : 50

הערות

1. יש לקרוא תוכנית זו יחד עם תוכנית חשמל אינסטלציה ואיטום.
2. תכנית זאת מיועדת לביצוע רק במידה ומולאו שני תנאים בסיסיים:
   א .אישור האדריכל
   ב . התוכנית מתאימה להיתר הבניה)באישור המהנדס האחראי על הביצוע)
3. תוכנית זאת תבוצע רק לאחר חתימת האדריכל והמודד עליה המאשרים כי היא מתאימה להיתר בניה והתקנים מבחינת העמדת המבנים במגרש
4. מיקום המבנה ביחס למגרש יקבע ע" י המודד בהתאם לתוכנית העמדה של האדריכל.
5. עובי כיסוי הבטון יהיה2.5o " מ בכל האלמנטים מלבד אלה שבאים במגע עם הקרקע - שם עובי הכיסוי יהיה4o "מ.
6. הארקת יסוד -יש לעיין בתכנית יועץ חשמל.
7. אין להעביר צינורות בקוטר גדול מ-50מ "מ ללא אישור מהמהנדס המתכנן.
8. דוח קרקע הינו חלק בלתי נפרד מתכנית זו.
9. סוג בטון ב-30 דרגת חשיפה 3.
10. יש לבצע התאמה בין תכניות האדריכליות ושאר היועצים לבין תכנית זו - לפני ביצוע.
11. אין להעמיס את המרפסות הן לפני הבנייה , והן אחרי הבנייה בעומס הגדול מהמצויין בתכנית!
12. פירוק טפסות בכל שלב יהיה - אך ורק באישור בכתב ממתכנן הקונסטרוקציה.

עמוד / קיר-צומח ▨

עמוד / קיר-מפסיק ▩

*סוגי בטון ראה ברשימת כמויות

פרט הגבהת בטון ביציאה למרפסת

1:25

רולקה,סף שיש ,מריחת איטום-ראה פרט יועץ איטום!

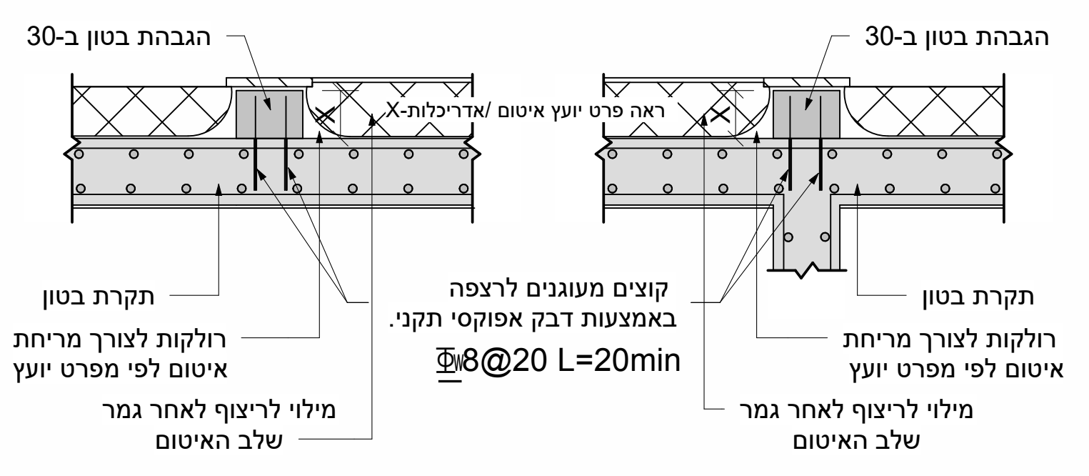
הגבהת בטון ב-30
הגבהת בטון ב-30
ראה פרט יועץ איטום /אדריכלות-X
תקרת בטון
רולקות לצורך מריחת איטום לפי מפרט יועץ
קוצים מעוגנים לרצפה באמצעות דבק אפוקסי תקני.
Φw8@20 L=20min
מילוי לריצוף לאחר גמר שלב האיטום
תקרת בטון
רולקות לצורך מריחת איטום לפי מפרט יועץ
מילוי לריצוף לאחר גמר שלב האיטום

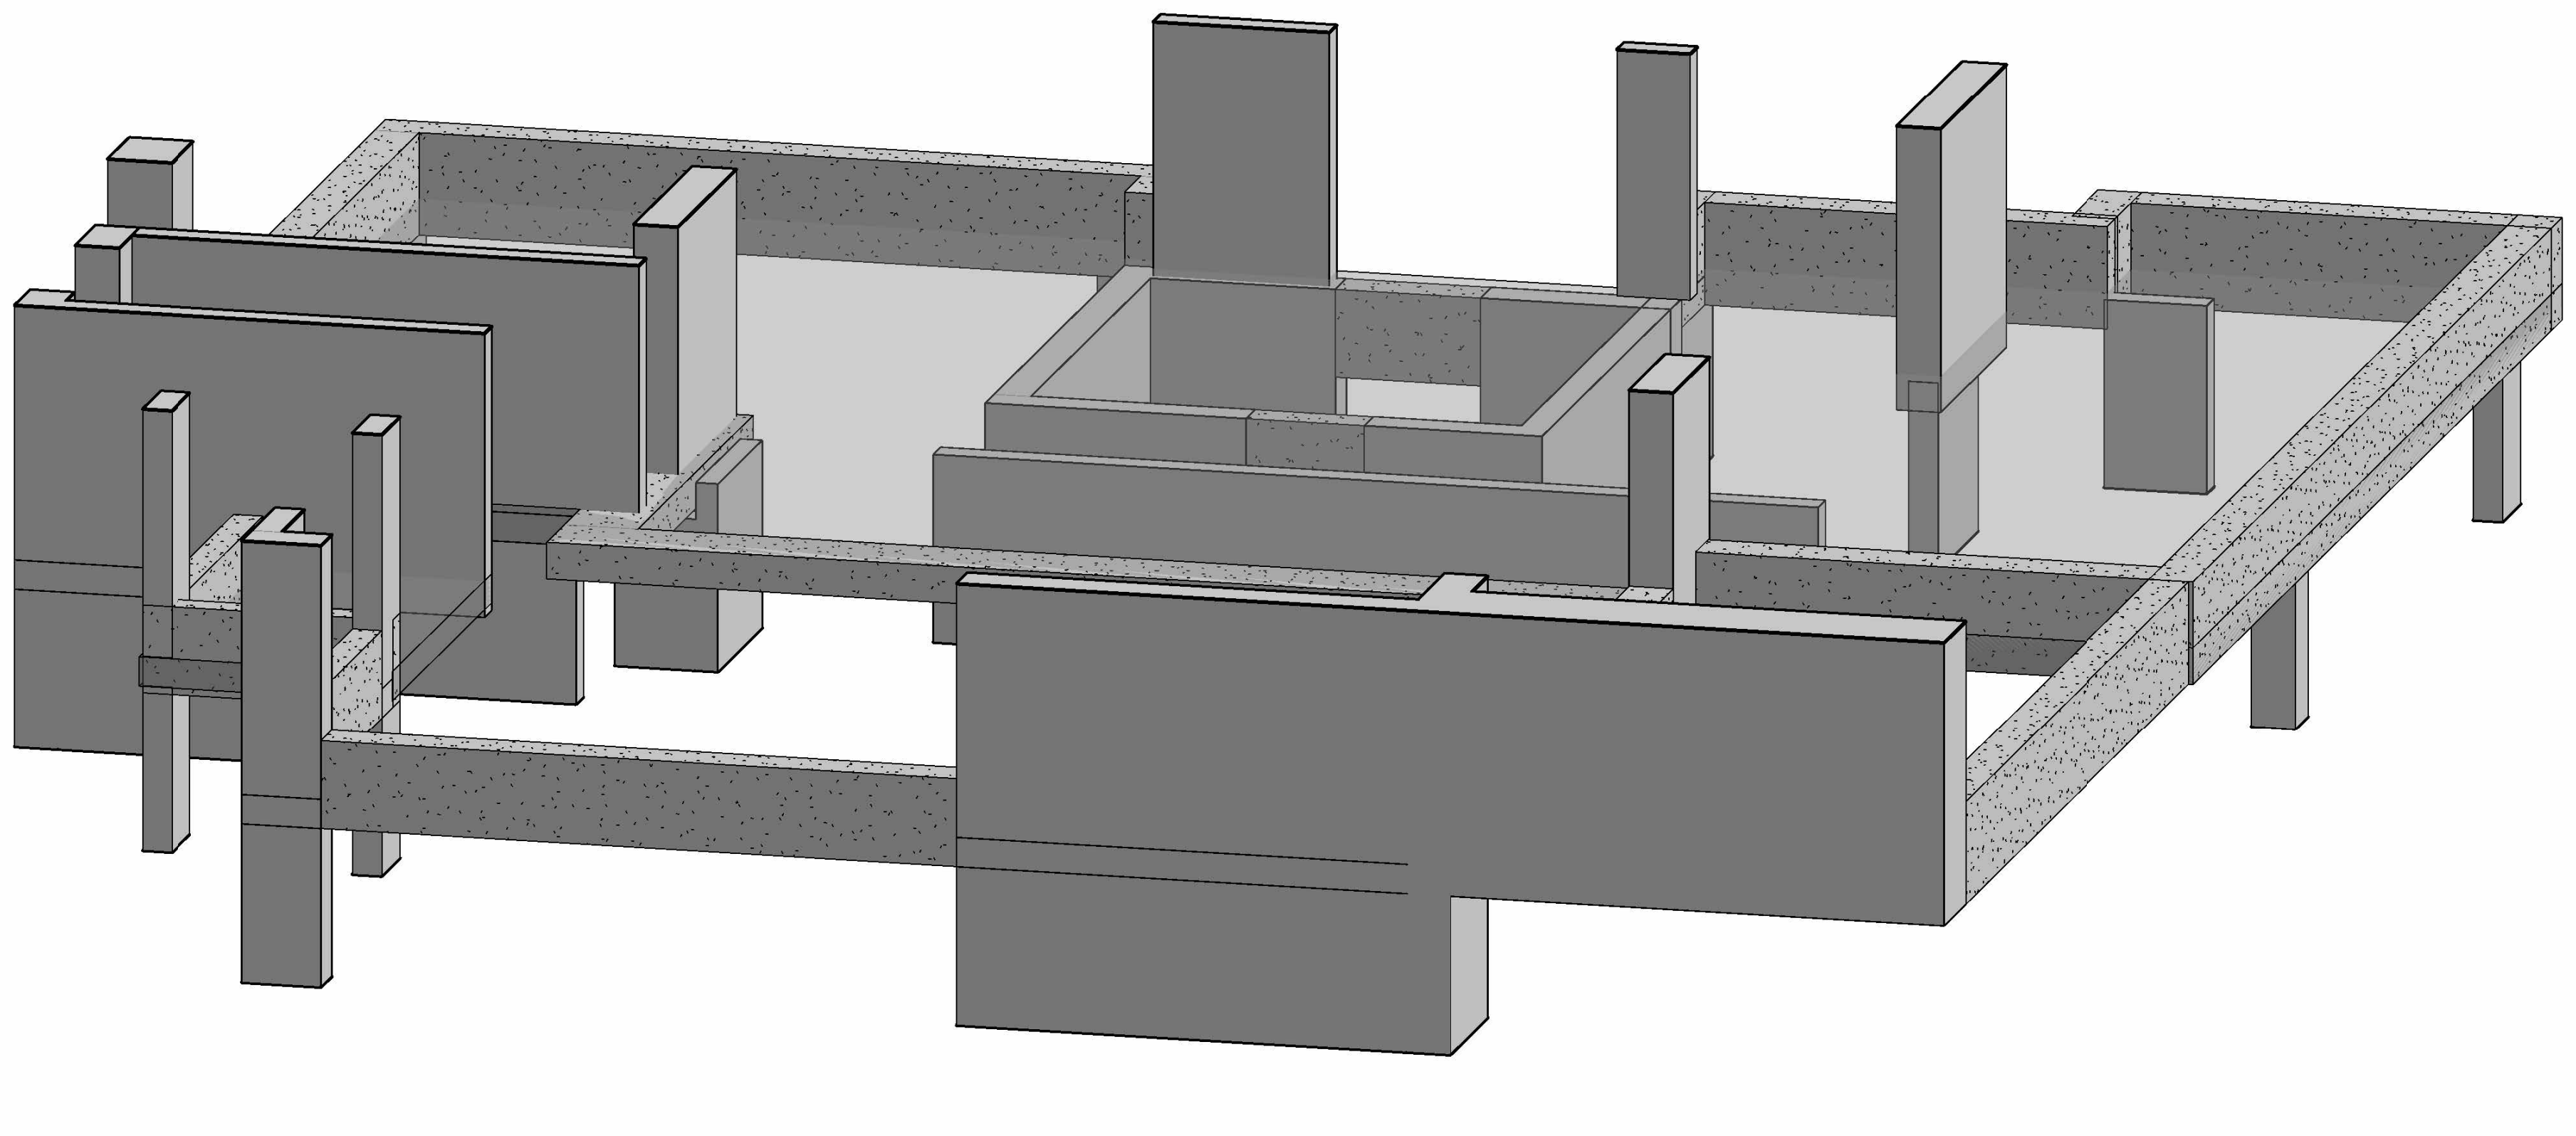

3D-K-31

תאריך	ע"י	מהות העידכון	מס 'עידכון
1.11.26		W8 הזזת עמוד	P1
5.10.26		תוכניות לביצוע	P0

עומסים

עומס קבוע נוסף 500 =ק"ג /מ"ר

עומס שימושי 150 =ק"ג /מ"ר

עומס מרפסות 350=ק"ג /מ"ר

גובה מפלס)אדריכלות): +3.85

מפלס פני בטון: +3.70

P1 מעודכן לתאריך: 1.11.26

לעיון	לאישור	למכרז	לביצוע
○	○	○	●

שם הפרויקט:

וילה ליאור ואביחי אטואן

תאור השרטוט:

תוכנית קומה א ' -גיאומטריה

מס 'השרטוט:

K-31

מס 'פרויקט: WORK-167

קנ"מ:

דוא" ל: tal@yarin-eng.co.il

גודל גליון: 844 X 840

מהנדס אחראי: טל שיי אטיאס

מהנדס: רותם מאיר

ירין הנדסה
טל אטיאס: 050-444-4730
tal@yarin-eng.co.il

YARIN
תכנון | ניהול | פיקוח מבנים

01/11/2026 10:16:27
C:\Users\LENOVO P340\Desktop\עבודה\תוכניות עבודה\רותם\work
167-רוויטו מודל רוויט\קובץ\cons\פתיחת תיקייה רויטאביחי אטואן
התחלתי.rvt