6009118-47

מינהל התכנון
9.11.16
לאשר את התוכנית

## חוק התכנון והבנייה, התשכ"ה - 1965
## תכנית מפורטת

## מס' תמל\1016

# -
# שכונת הרקפות
# באר-שבע

| | |
|---|---|
| נספח נופי | גליון 1 מתוך 1 |
| מחוז | דרום |
| מרחב תכנון מקומי | באר שבע |
| רשות מקומית | באר שבע |
| ישוב | באר שבע |
| תאריך | 27-11-2016 |
| מהדורה | 10 |
| קנ"מ | 1:200 1:5000 |

| | | |
|---|---|---|
| מגיש התוכנית | שם: רשות מקרקעי ישראל<br>תאגיד: | חתימה: |
| עורך התכנית | שם: נעמה מליס<br>תאגיד: | חתימה: |
| יזם התוכנית | שם: רשות מקרקעי ישראל<br>תאגיד: | חתימה: |
| מודד | שם: חץ הצפון<br>תאגיד: | חתימה: |
| בעלים | תאגיד: מדינת ישראל | חתימה: |

## מקרא

| | |
|---|---|
| ━ | גבול התוכנית |
| 🟩 | גינה שכונתית |
| 🟩 | גינה שכונתית משולבת באזורים אקסטנסיביים מטופלים |
| 🟩 | שטחים אקסטנסיביים מטופלים |
| 🟨 | אזורי אל-געת |
| 🟫 | נוף פתוח |
| ━ | סימטאות הולכי רגל |
| ━ | שבילים לאורך רחובות |
| ━ | טיילת נופית |
| ┅ | המשך טיילת בשצ"פ |
| - - - | קישוריות אל הנוף |
| ✱ | נקודות ענין נופיות בשולי התוכנית |
| 🟧 | כיכר עירונית |
| 🟥 | מגרש למבנה ציבור |
| ▭ | מגרש מסחרי |
| ━ | כביש |
| ▨ | רחוב משולב |
| - - - | ציר נחל |
| ♣ | עץ לשימור |
| ♣ | עץ להעתקה |
| ♣ | עץ לעקירה |
| + | נקי ענין מסקר טבע עירוני |
| × | אתר ארכיאולוגי |

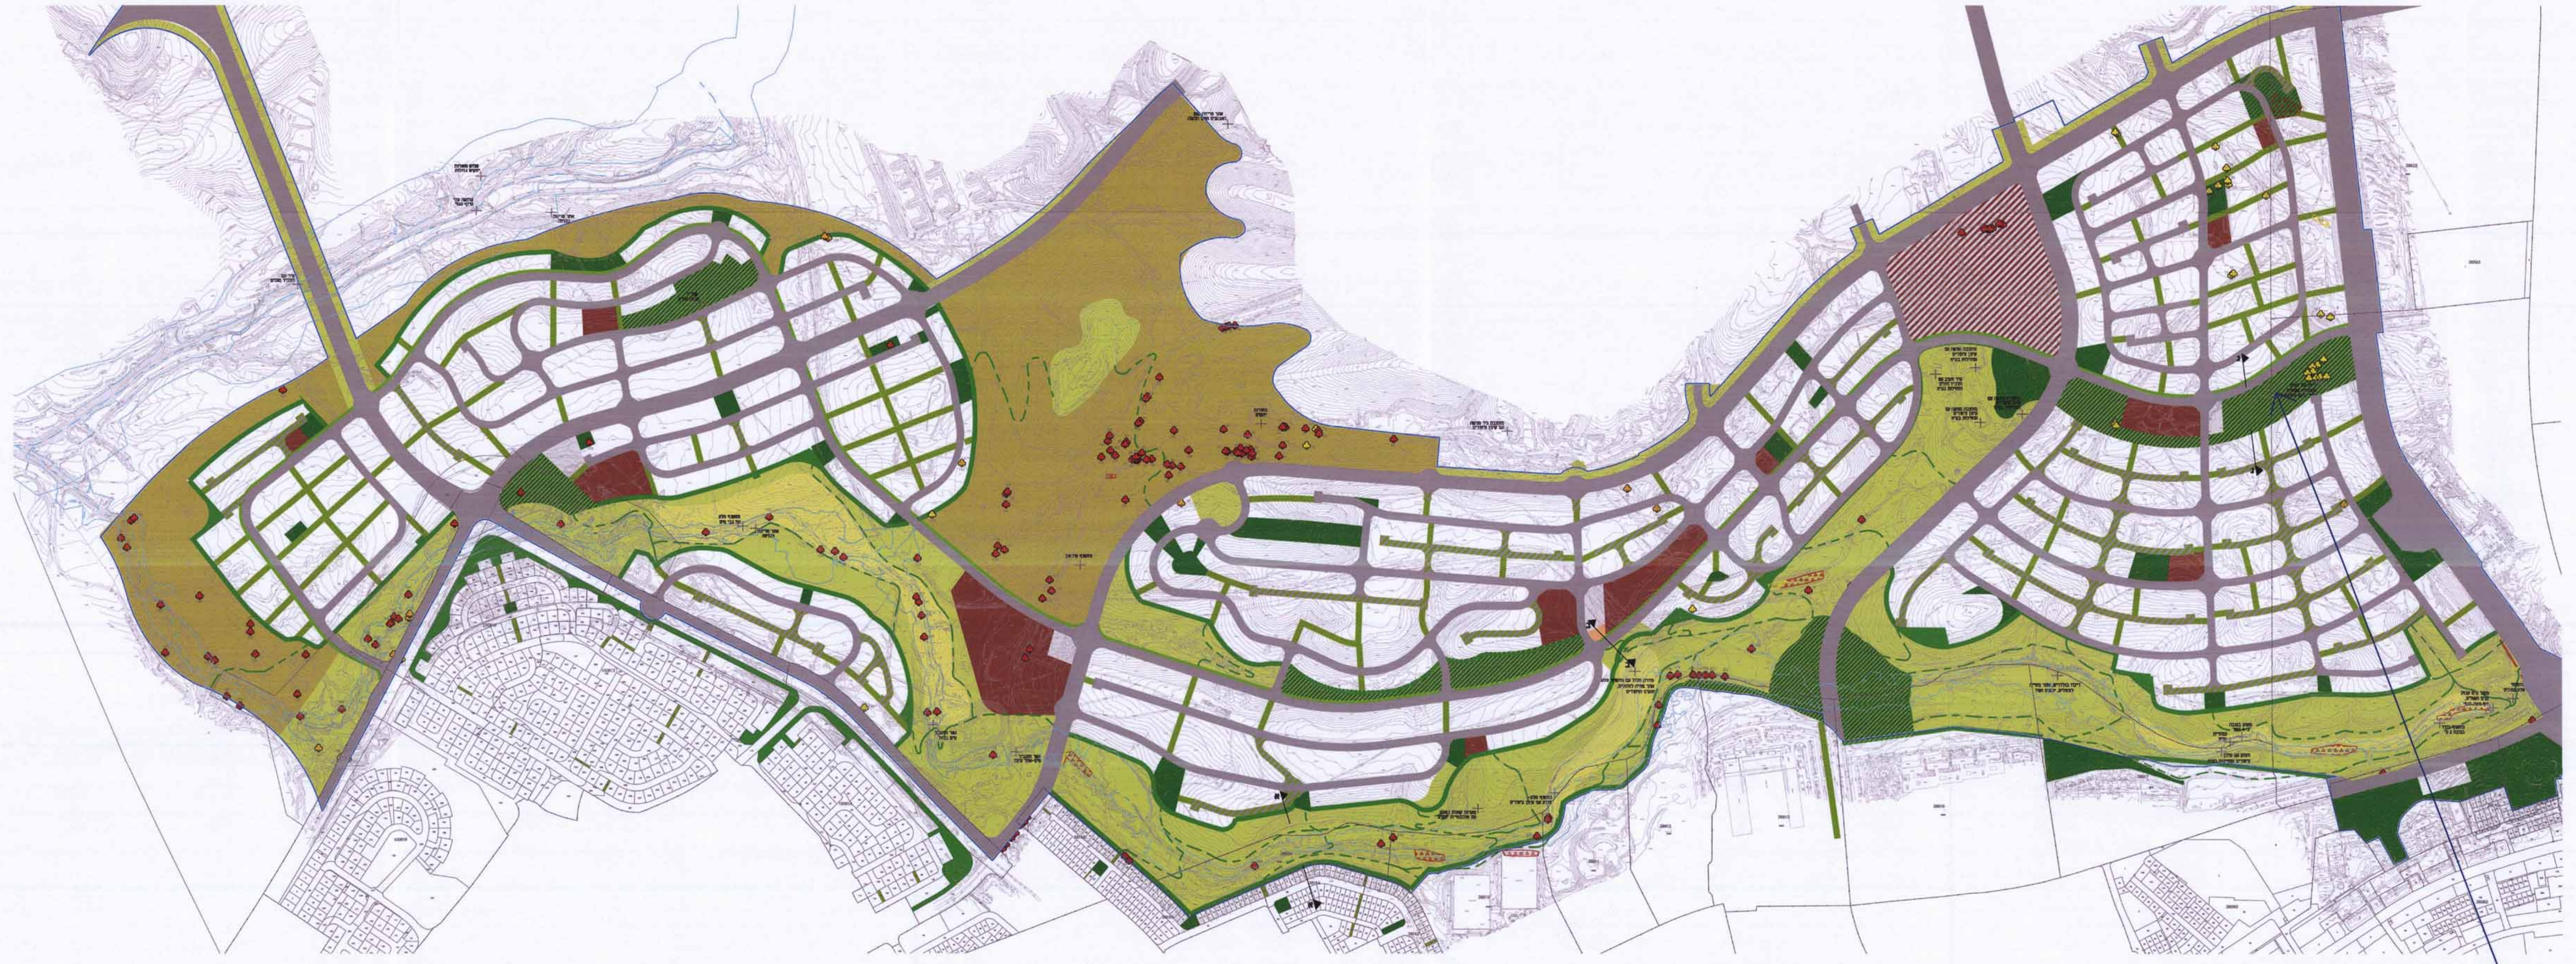

השלד הירוק קנ"מ 1:2500

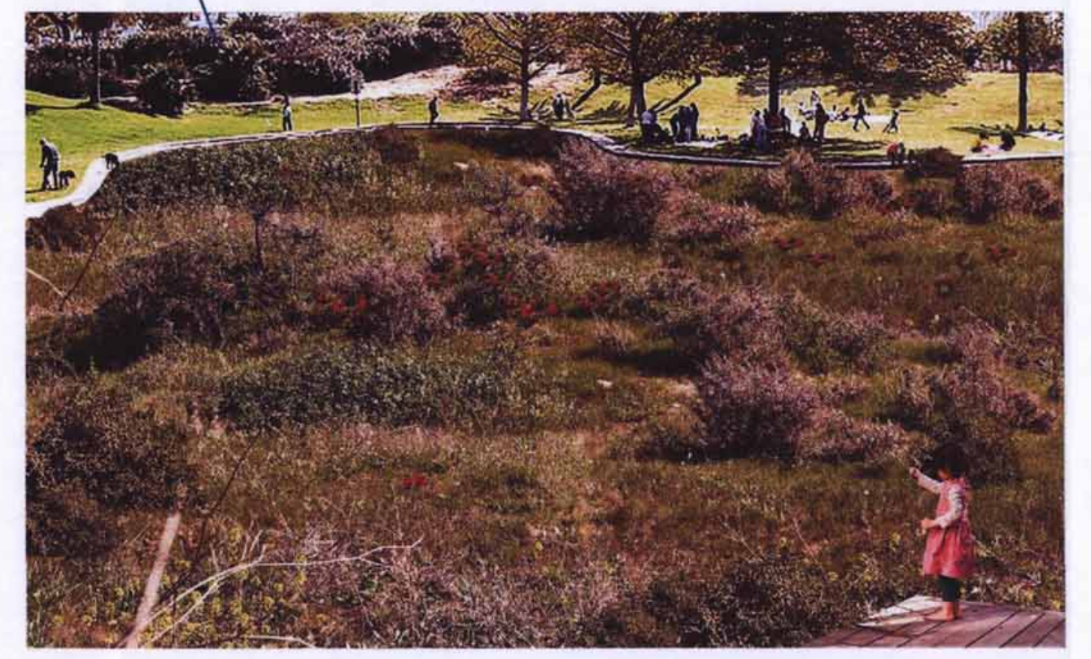

גינות שכונתיות משולבות
באזורים אקסטנסיביים מטופלים

### עקרונות התכנון הנופי

שימור שטחי טבע בלתי מופרים, בהתאם לערכי הטבע הקיימים בשטח ועל פי סקרים שנערכו במקום.

שימור הנחלים בתוואי הטבעי שלהם כרצועת טבע עירוני.

שימור ראשי הגבעות כנכס ציבורי - שמירה על מבטים רחוקים אל הנוף הסובב.

העתקת צמחים ייחודיים הנמצאים בשטחים המיועדים לבינוי.

שילוב והשקה בין שטחים אינטנסיביים לשטחים האקסטנסיביים.

הצמדת מוסדות הציבור למערכת הירוקה.

יצירת מערכת ירוקה המשכית של משעולים, רחובות, גנים שכונתיים וטיילת, תוך שמירה על צירי מבט ונקודות תצפית בממשק עם הנוף הפתוח שבשולי התוכנית.

אזור אל-געת מזרחי

אזור אל-געת מרכזי

אזור אל-געת מערבי

מרבדי פריחה
בנחל כובשים

יש לשמור על מידות מינימליות של בתי גידול, כמפורט להלן, בכל שטחי המתחם. ככל הניתן יהיו בתי הגידול נמוכים ממפלס הקרקע מסביבם וינקזו מי נגר. יש לשאוף לבתי גידול רציפים ככל הניתן, ללא מחיצות.

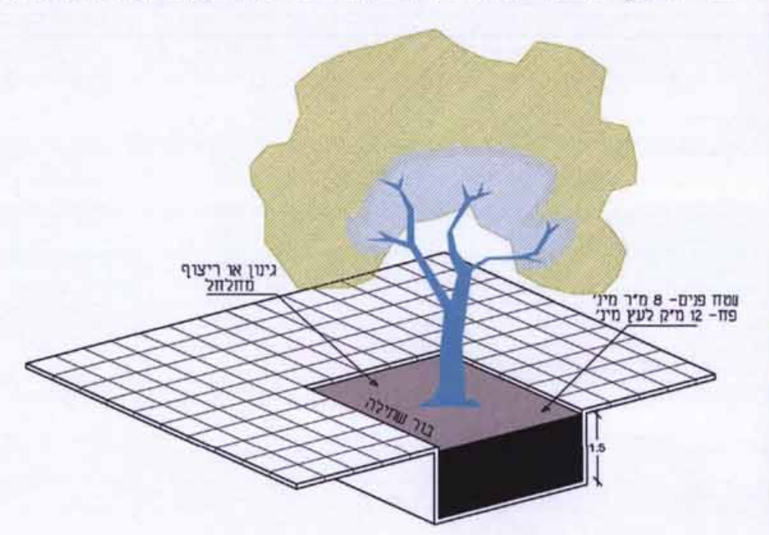

בור שתילה בודד

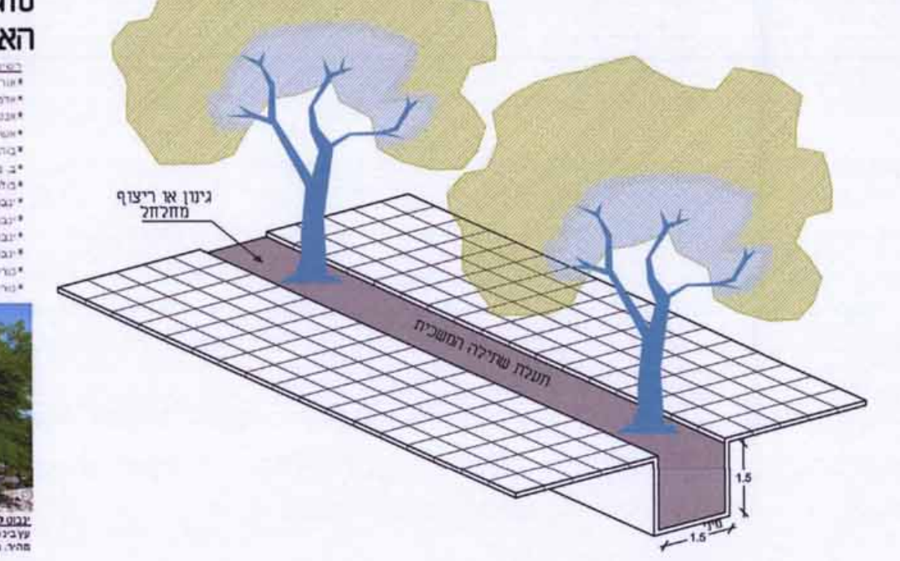

תעלת שתילה המשכית

לנטיעות ברחובות ייבחרו עצים נותני צל, מותאמי אקלים וחסכניים במים. מומלץ להשתמש בעצים מהירי צמיחה.
סוג עצי הרחוב ייקבע מתוך רשימת עצי הרחוב המופיעה ב"תוכנית האסטרטגית למרחב הציבורי" של באר שבע:

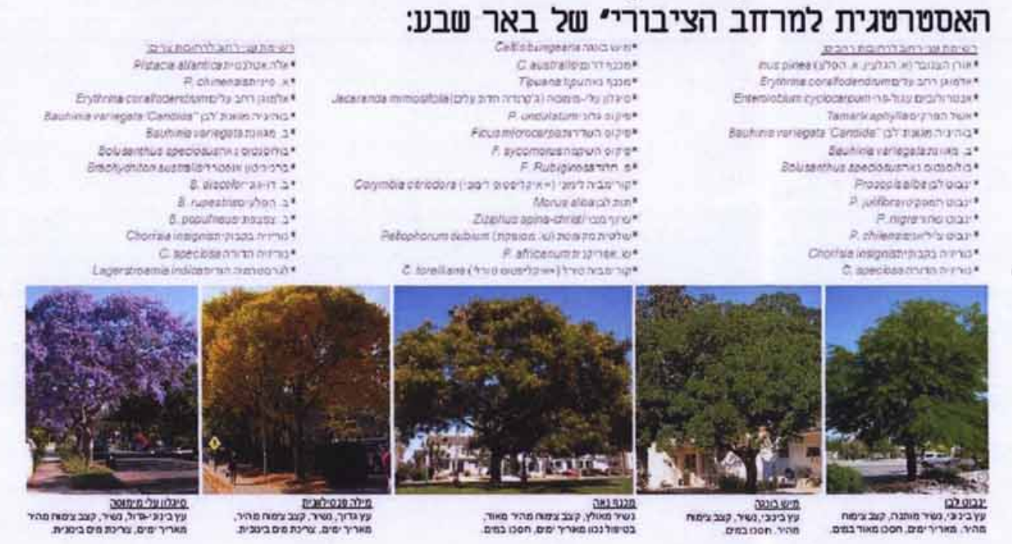

עצי רחוב מומלצים

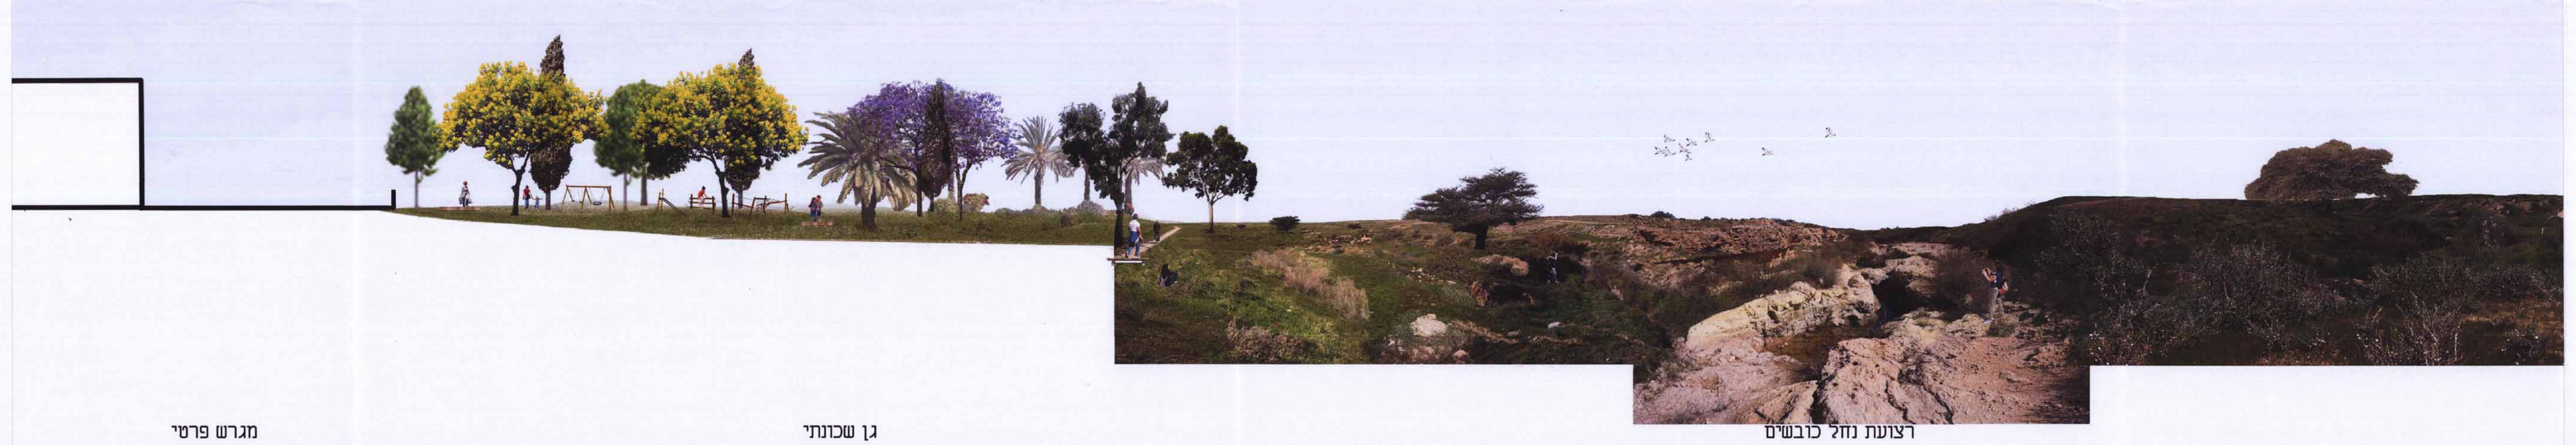

ממשק אופייני בין שטחי הטבע לשטחים המפותחים

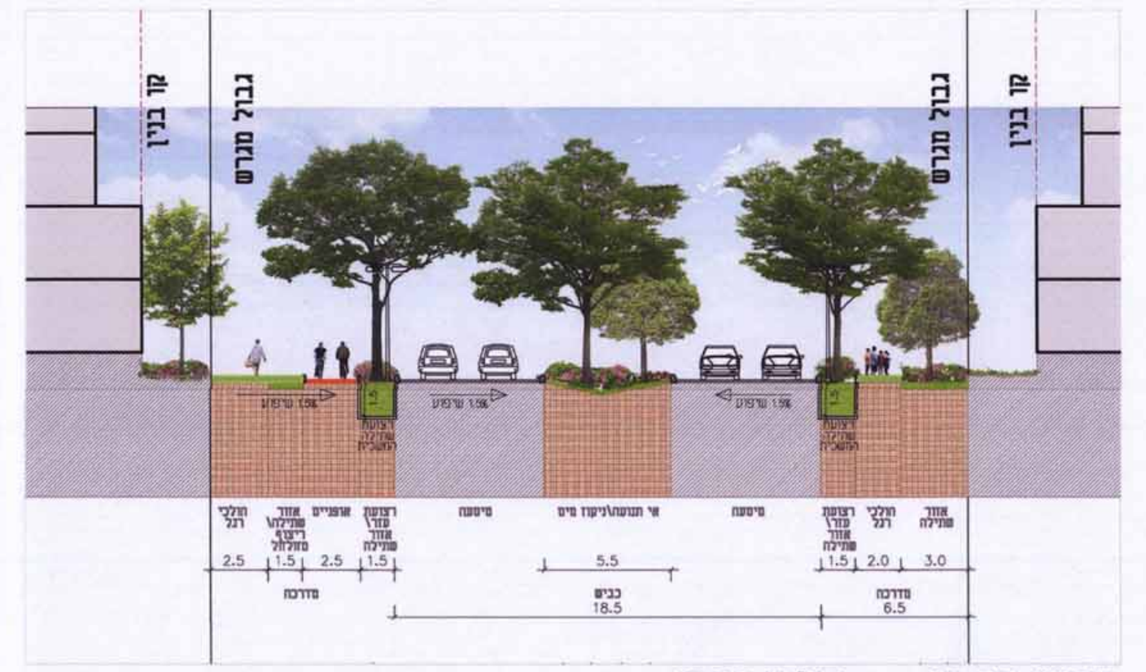

כביש 60,50 קנ"מ 1:200

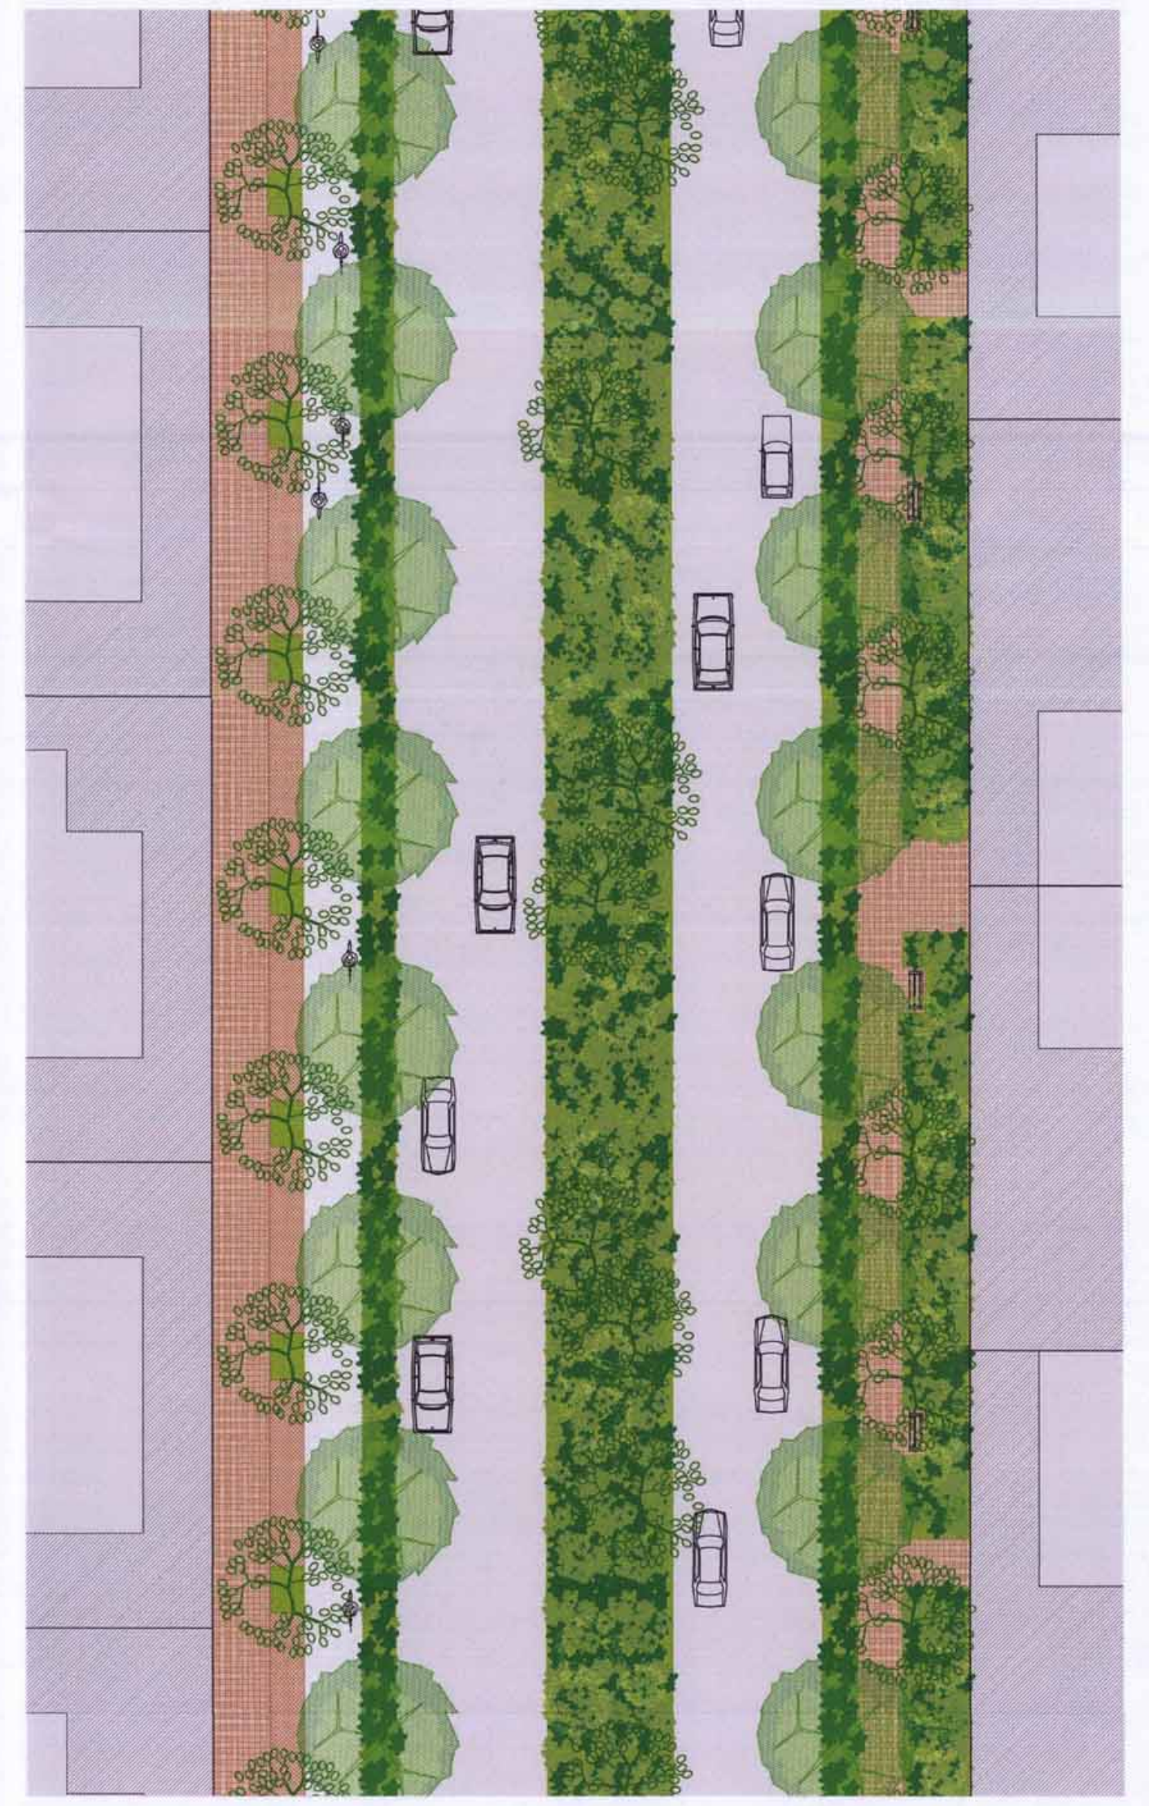

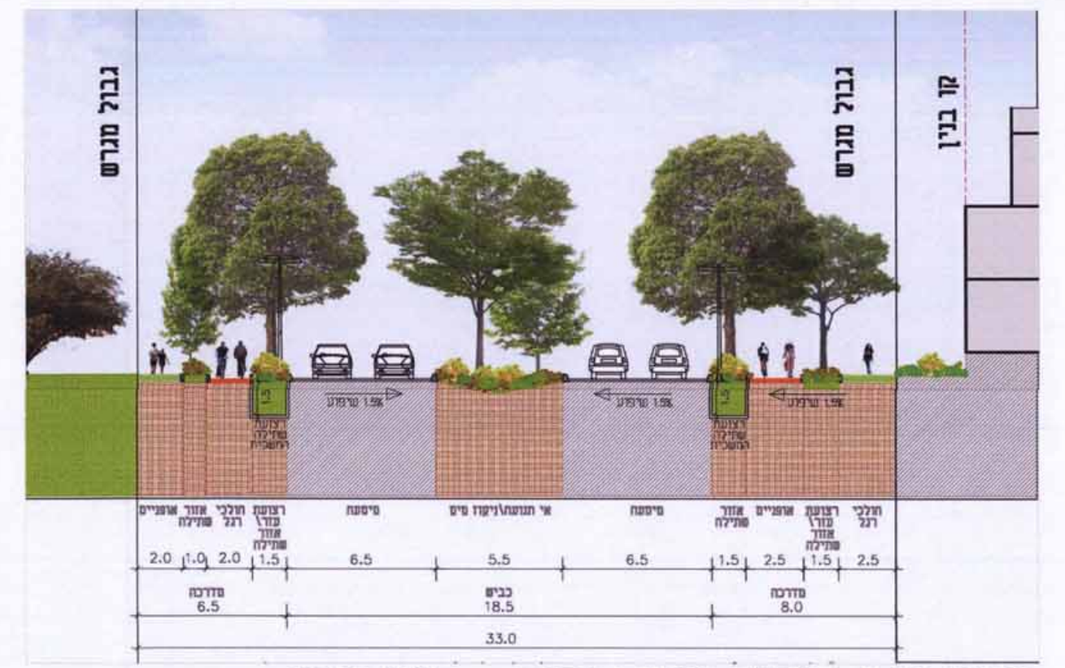

כביש 8,40 בצמוד לשטח פתוח קנ"מ 1:200

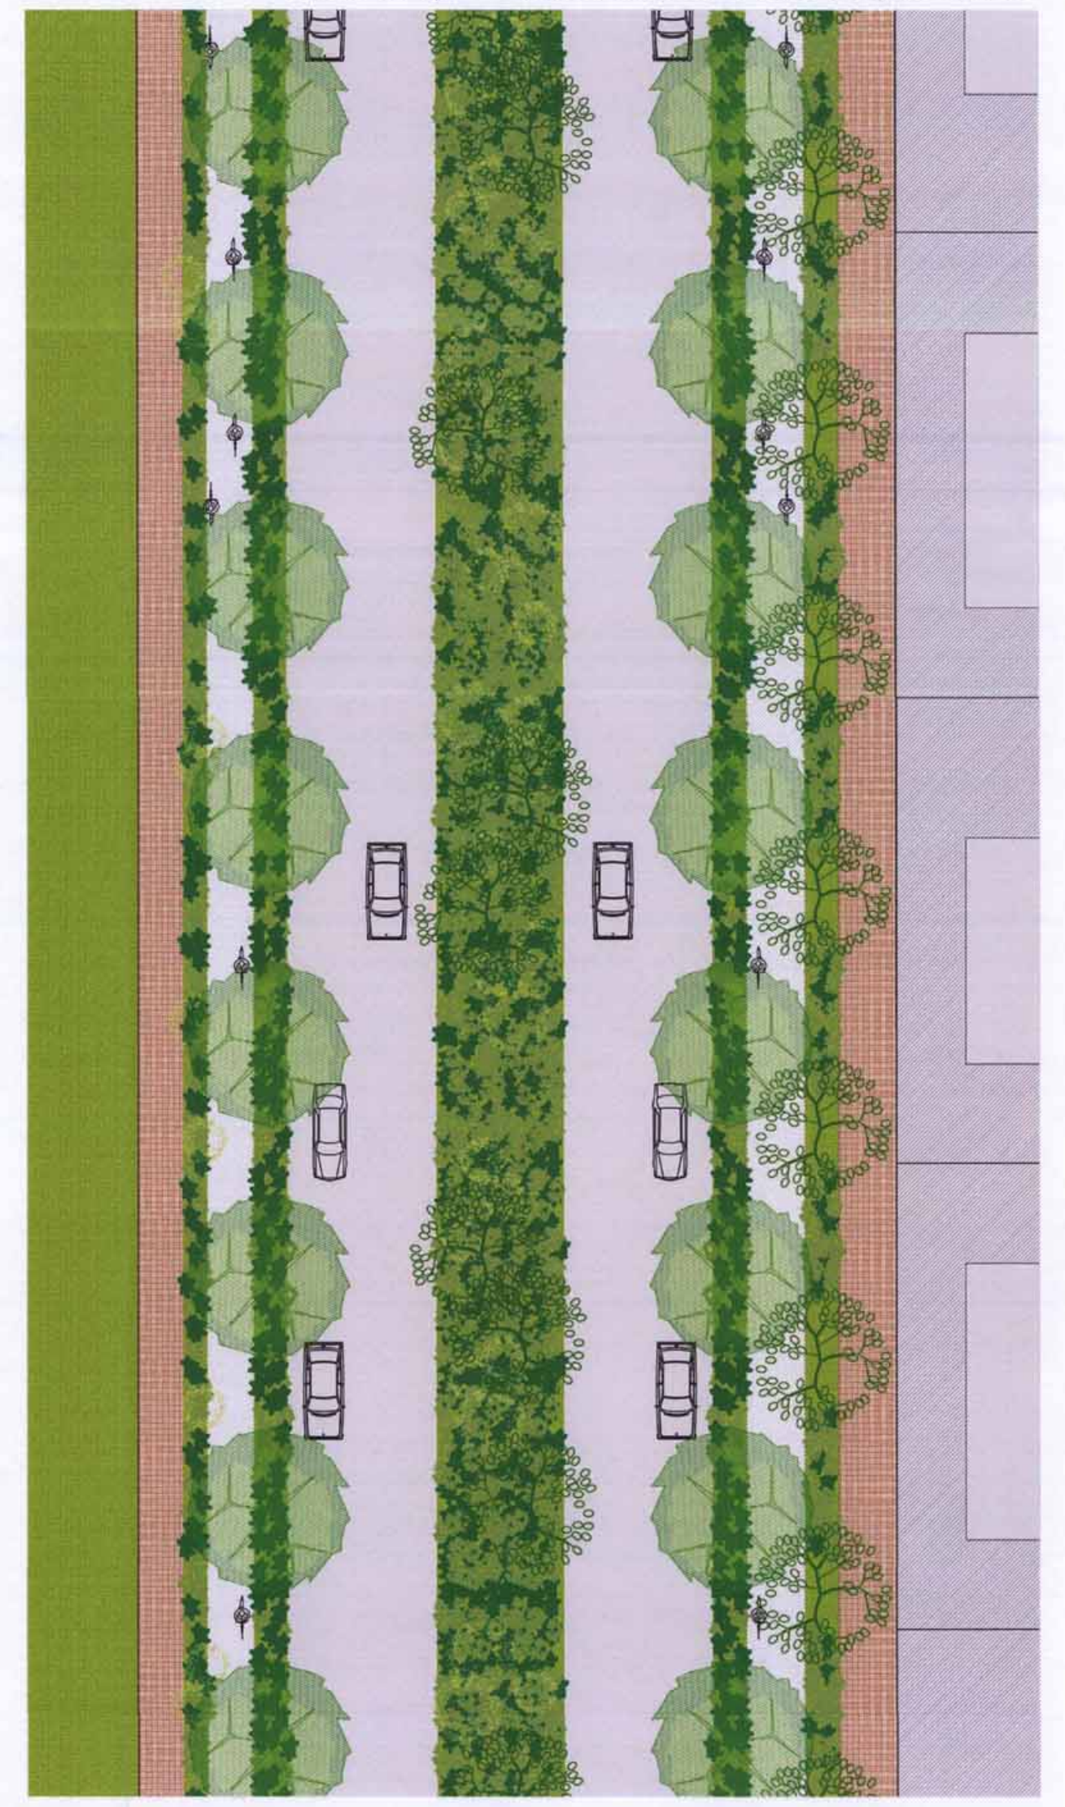

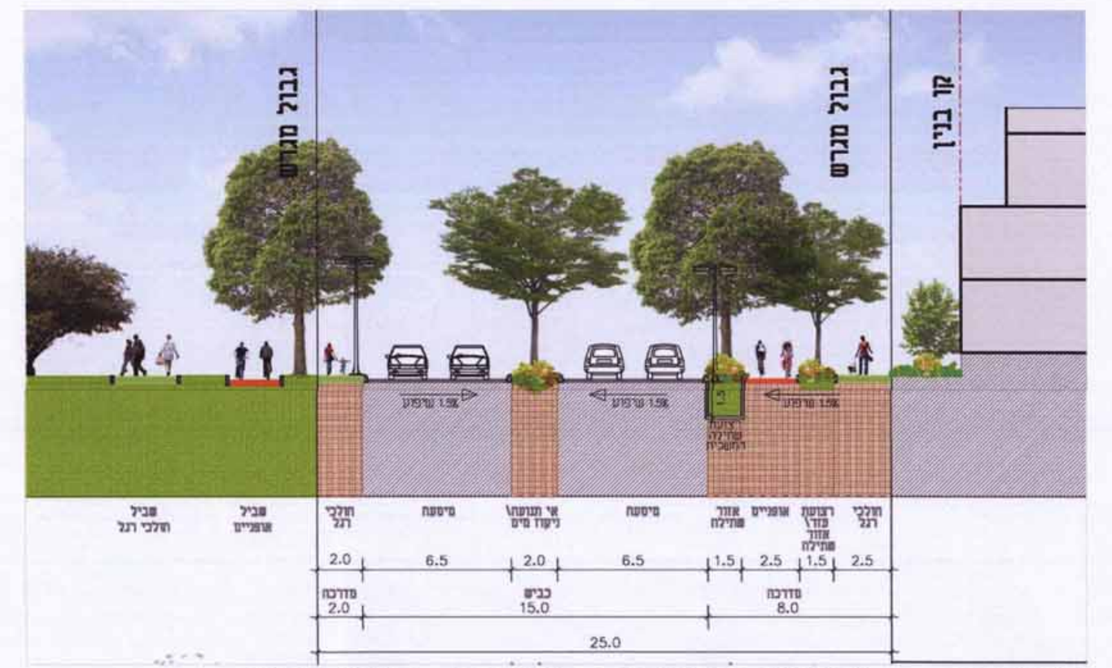

כביש 40 (בצמוד לשטחי תמ"א 22) קנ"מ 1:200

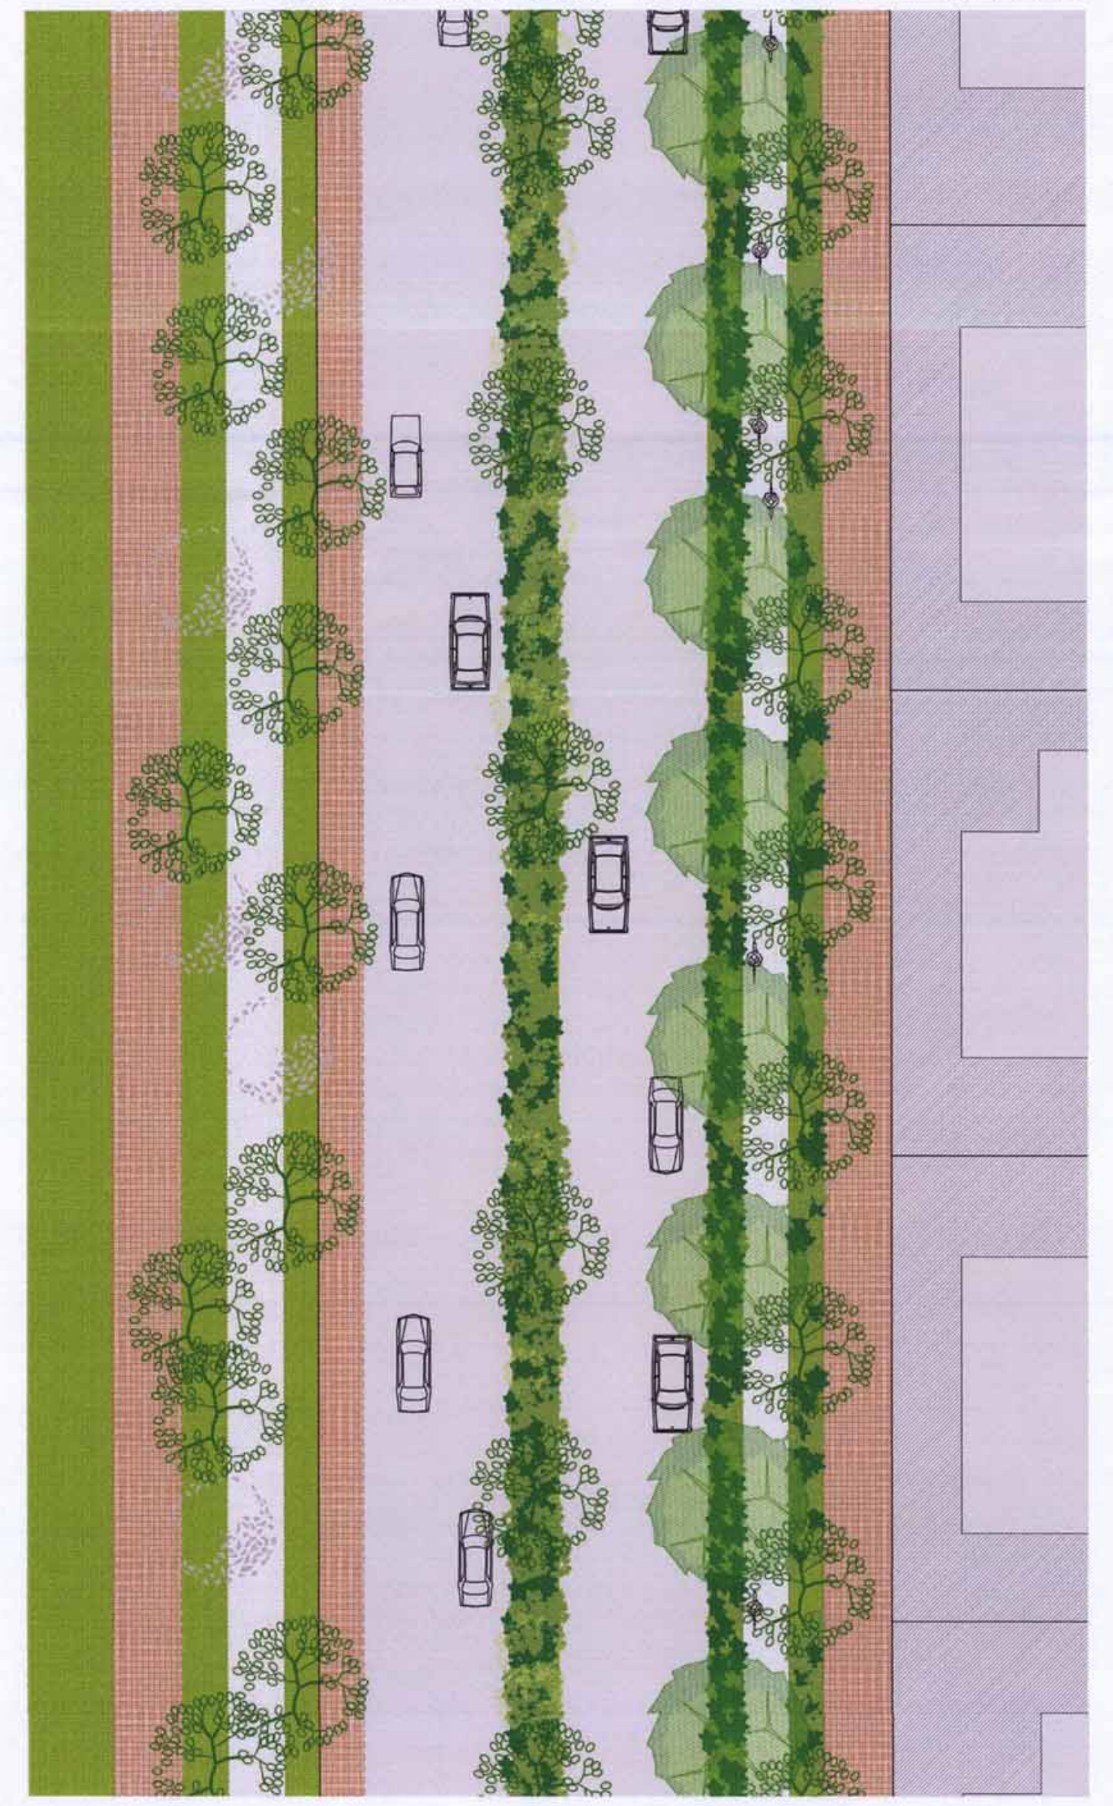

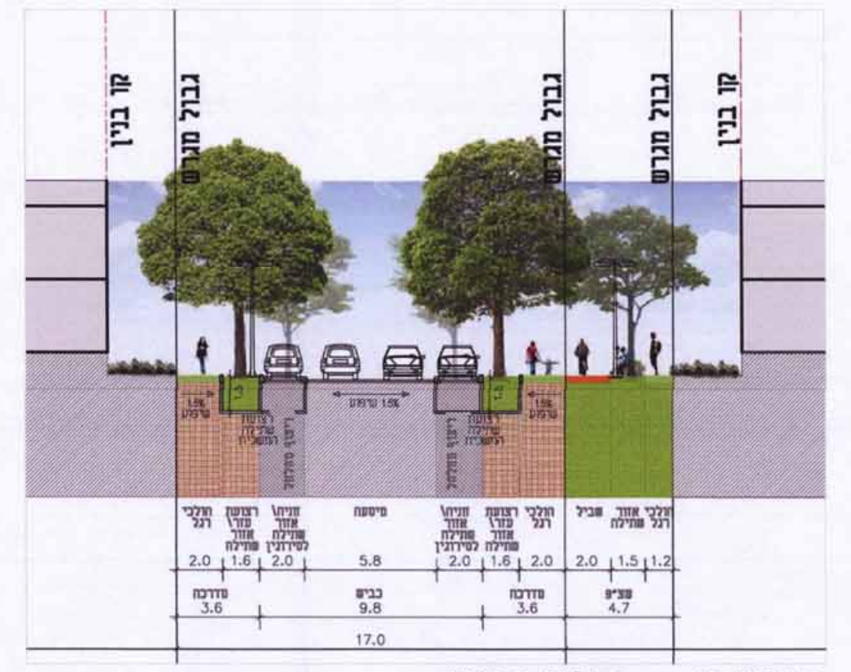

כביש 10 קנ"מ 1:200

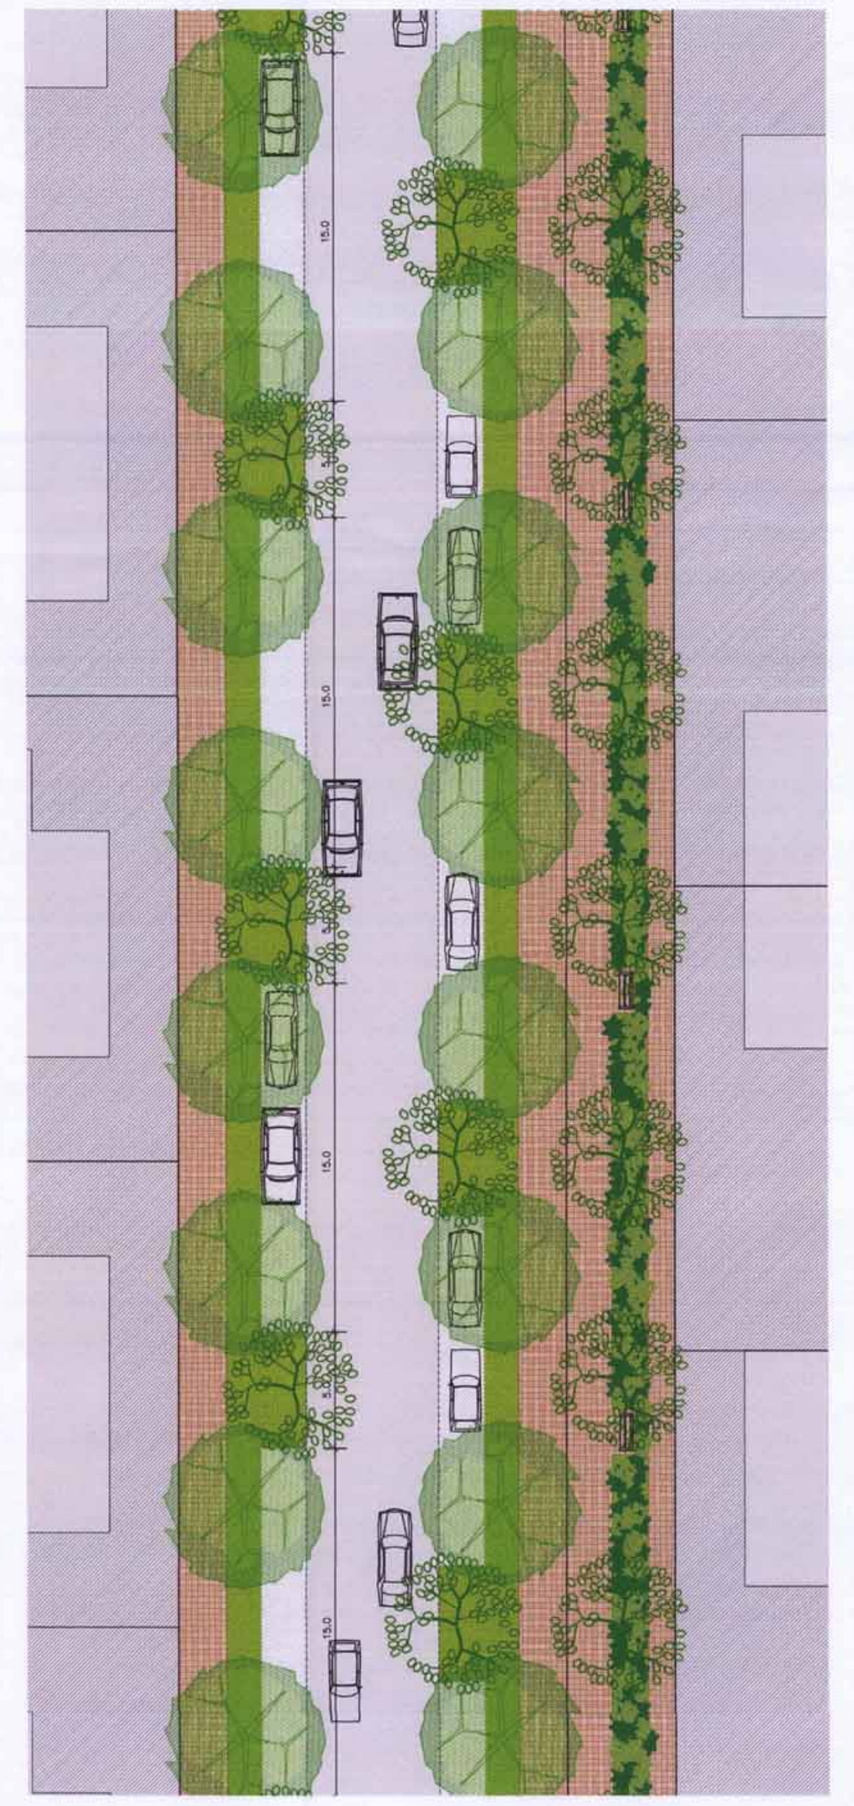

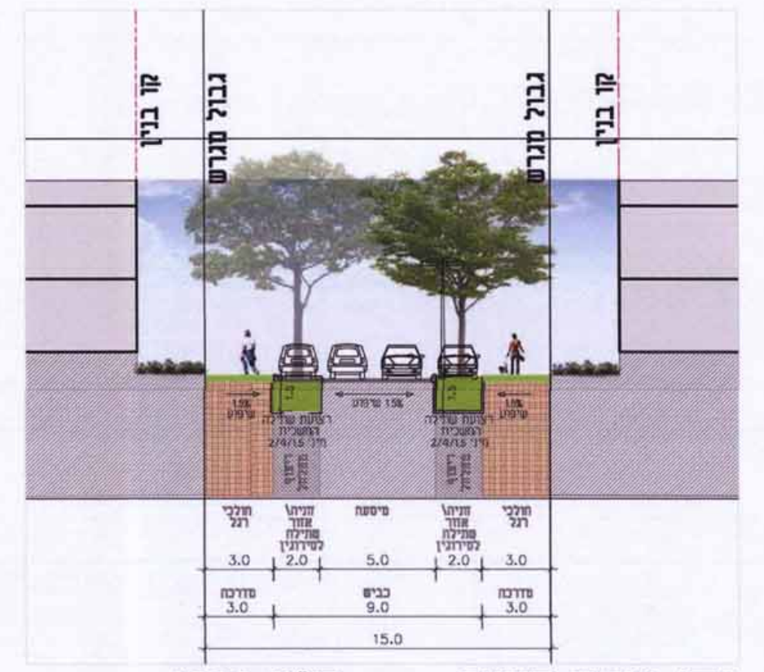

רח' מיתון תנועה קנ"מ 1:200

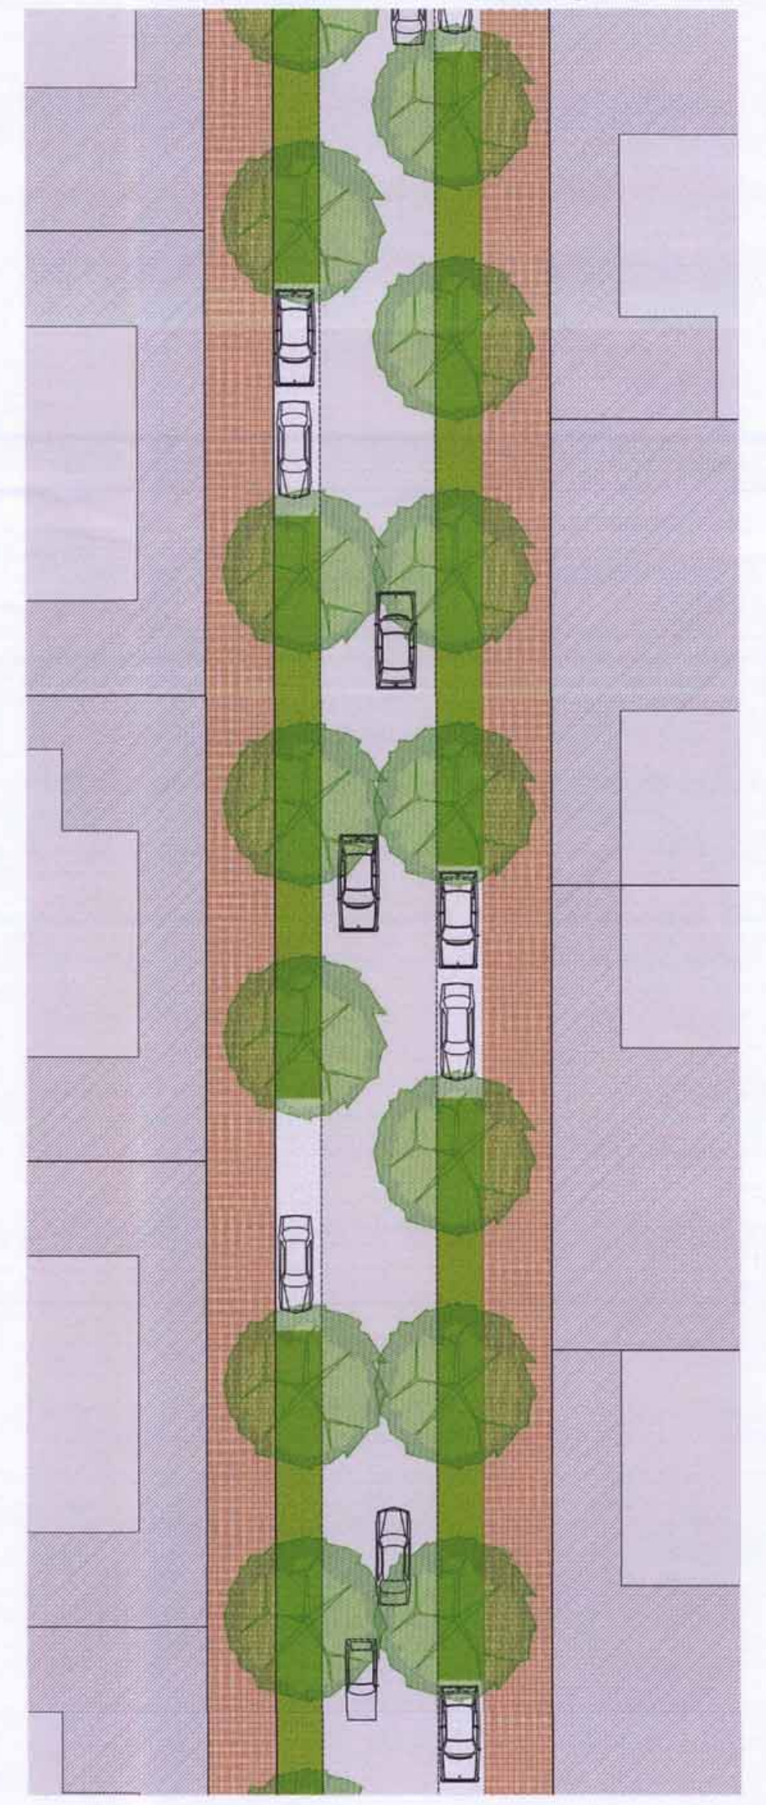

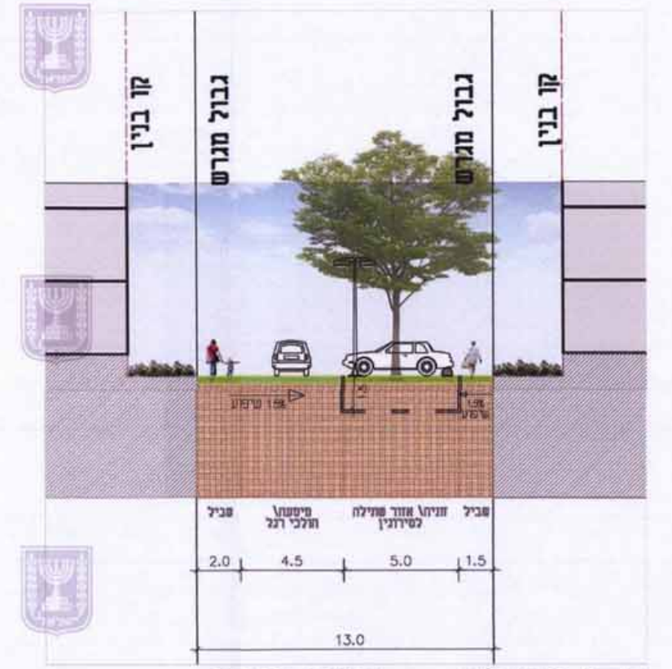

רח' משולב קנ"מ 1:200

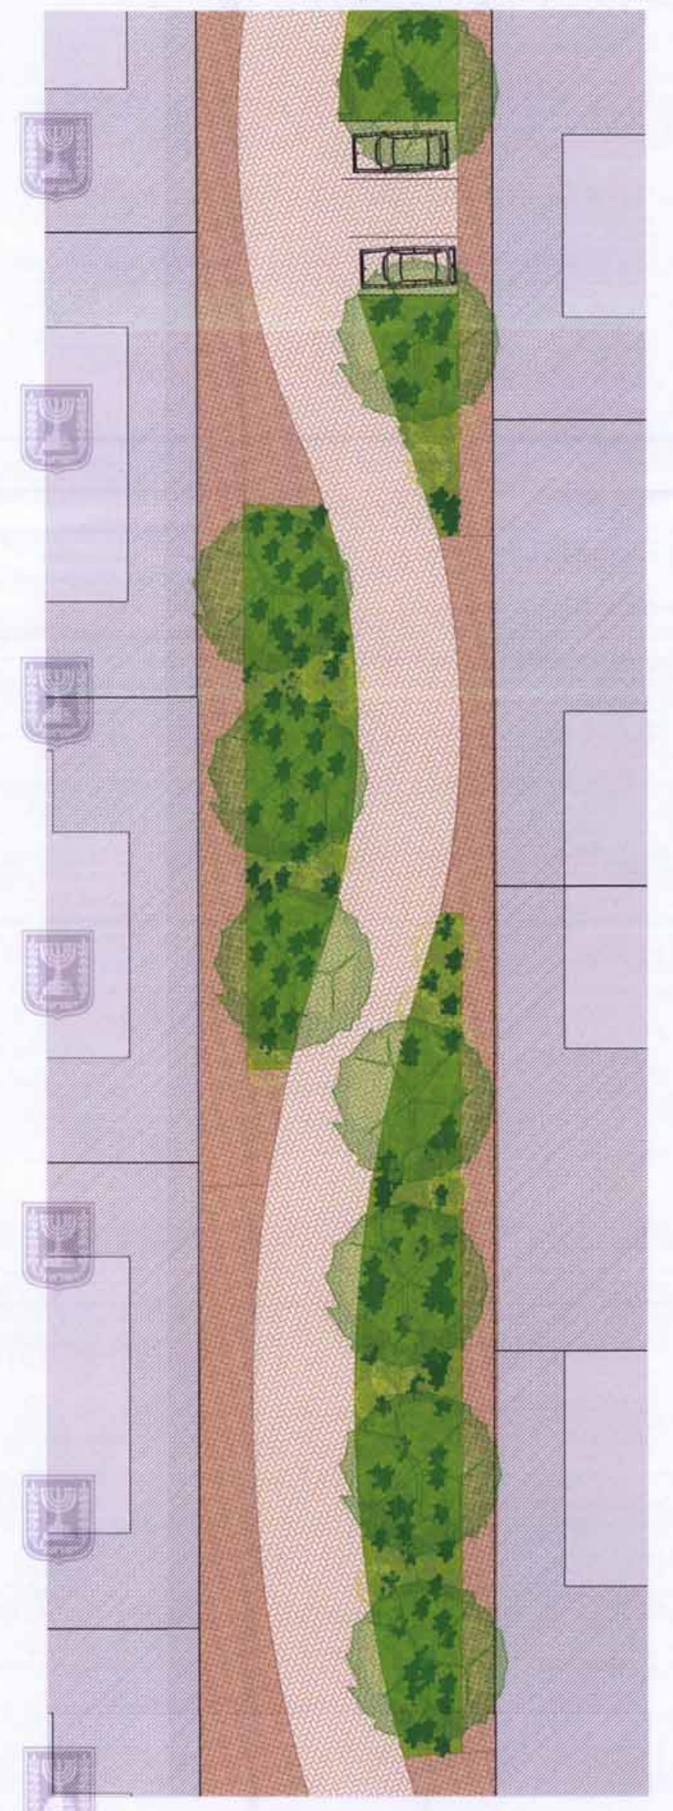

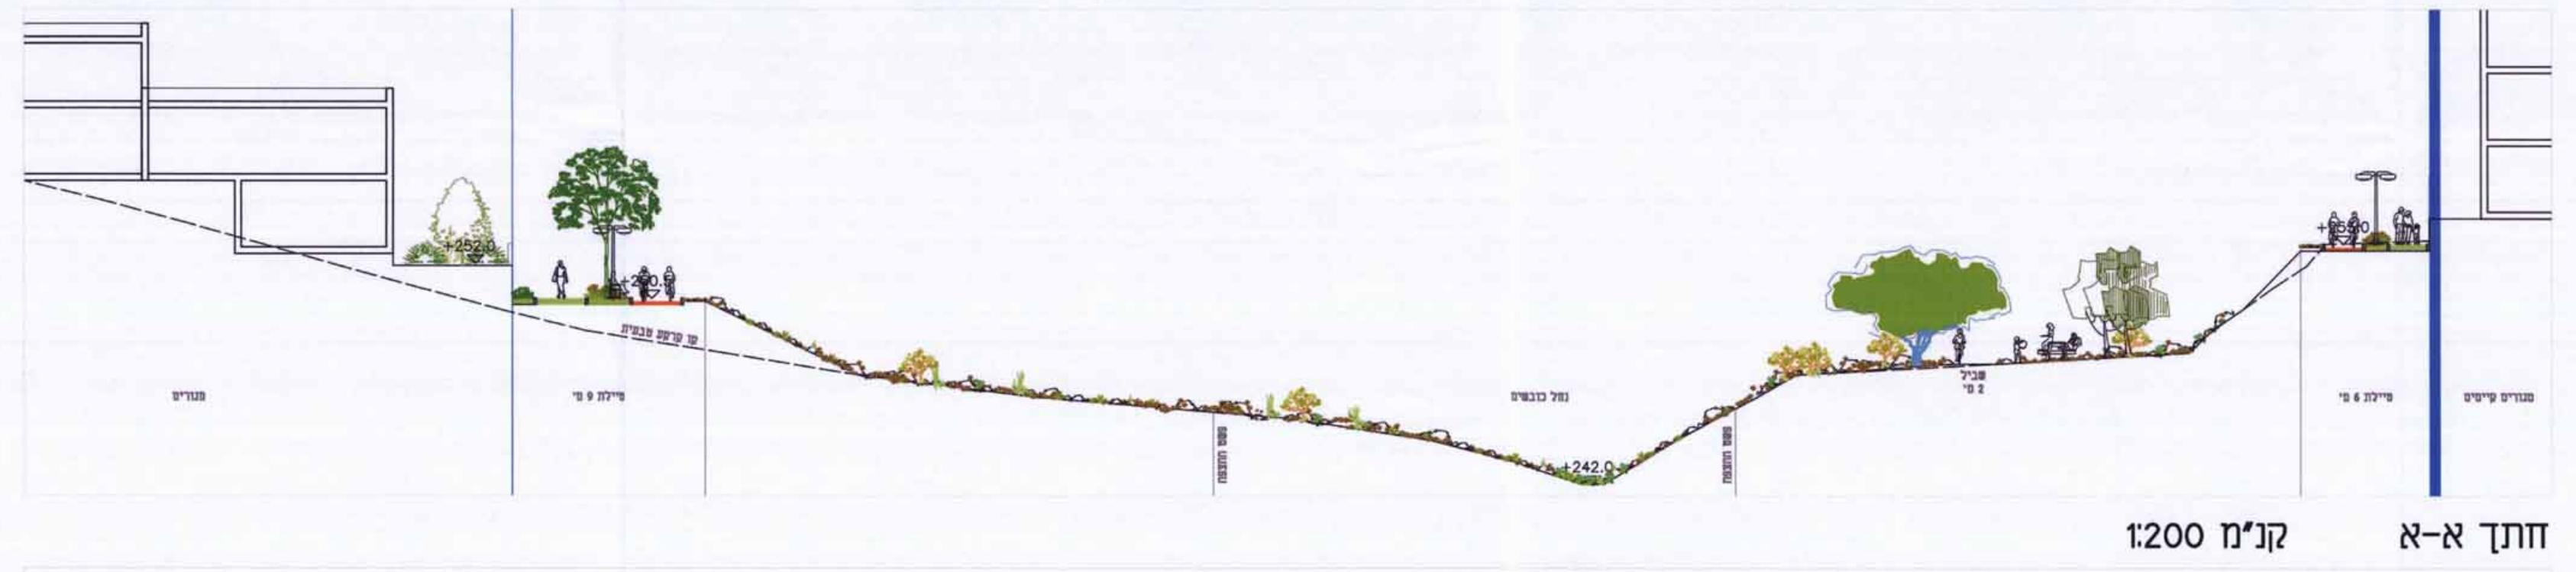

חתך א-א קנ"מ 1:200

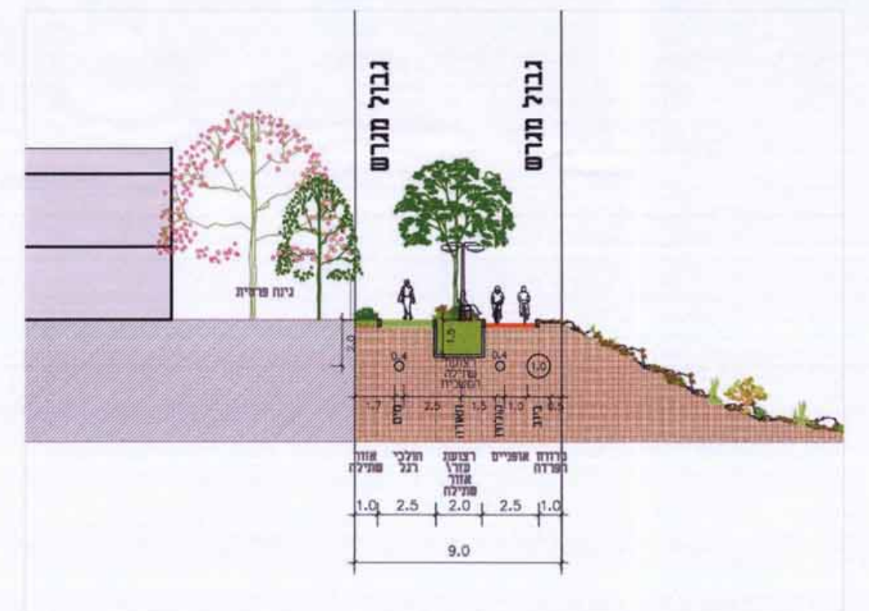

טיילת קנ"מ 1:200

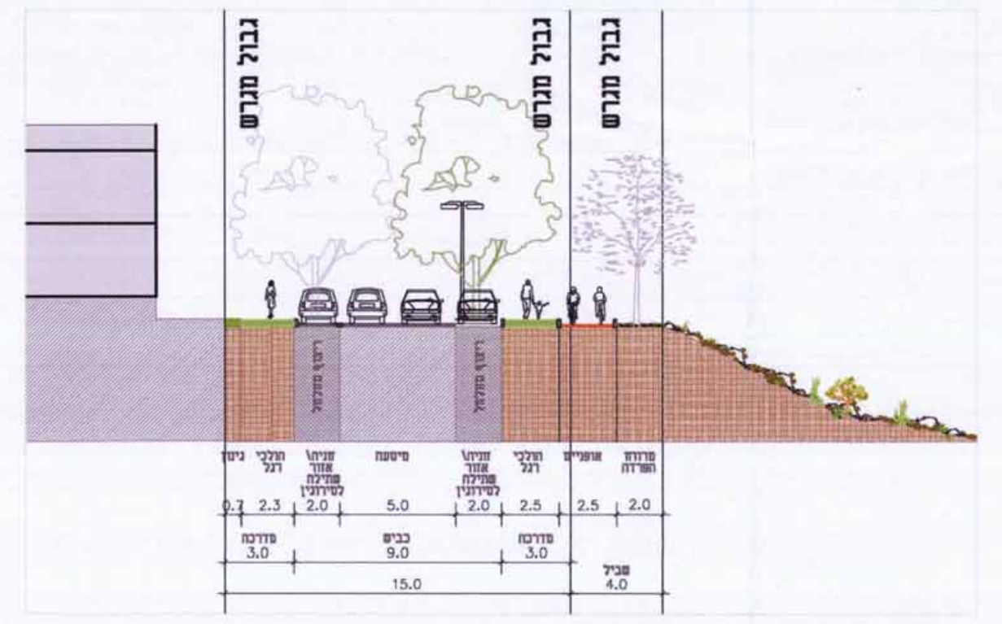

טיילת בצמוד לרח' מיתון תנועה קנ"מ 1:200

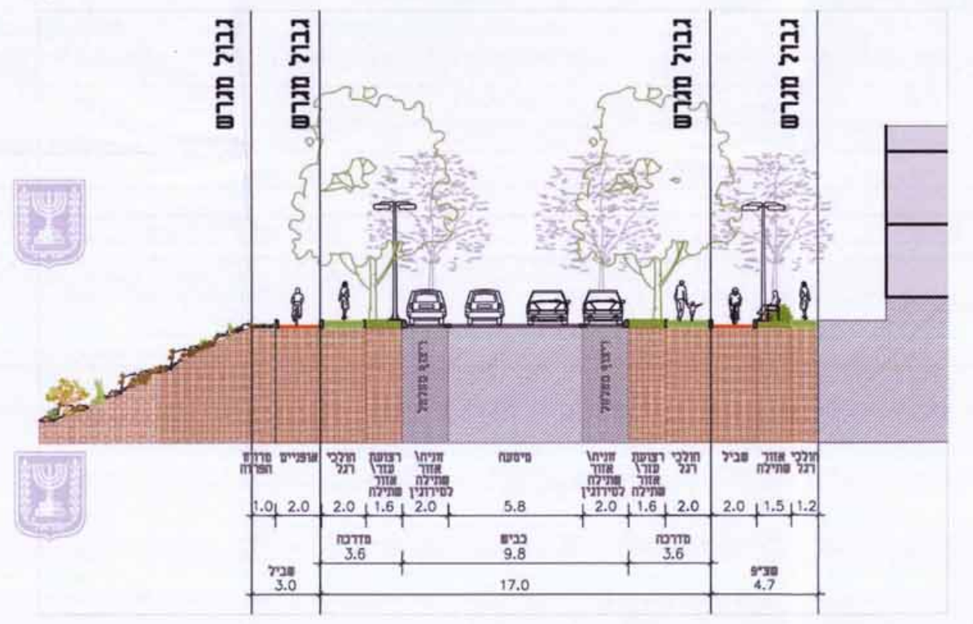

טיילת בצמוד לכביש 10 קנ"מ 1:200

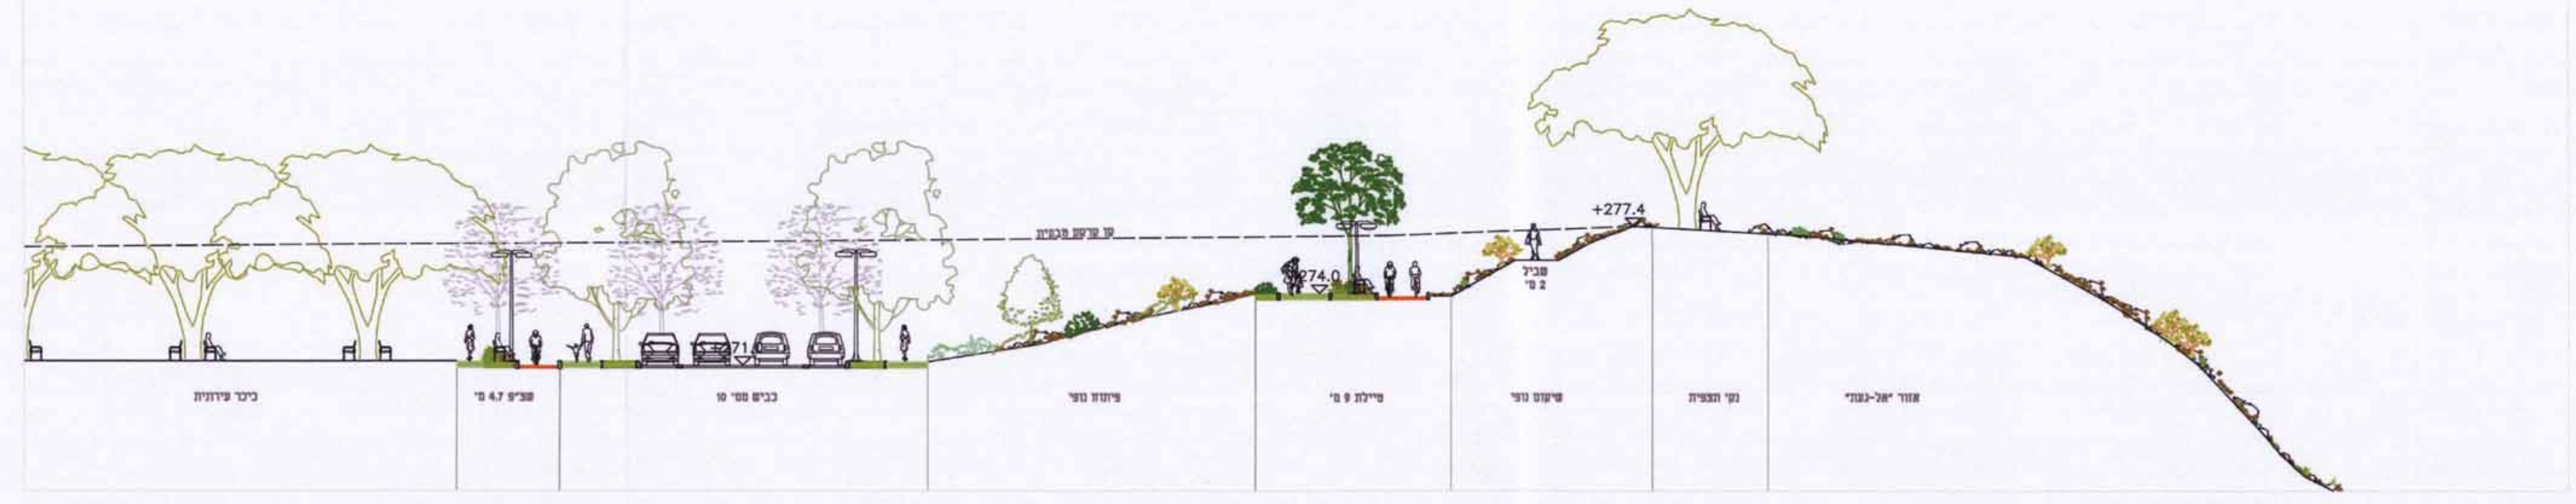

חתך ב-ב קנ"מ 1:200

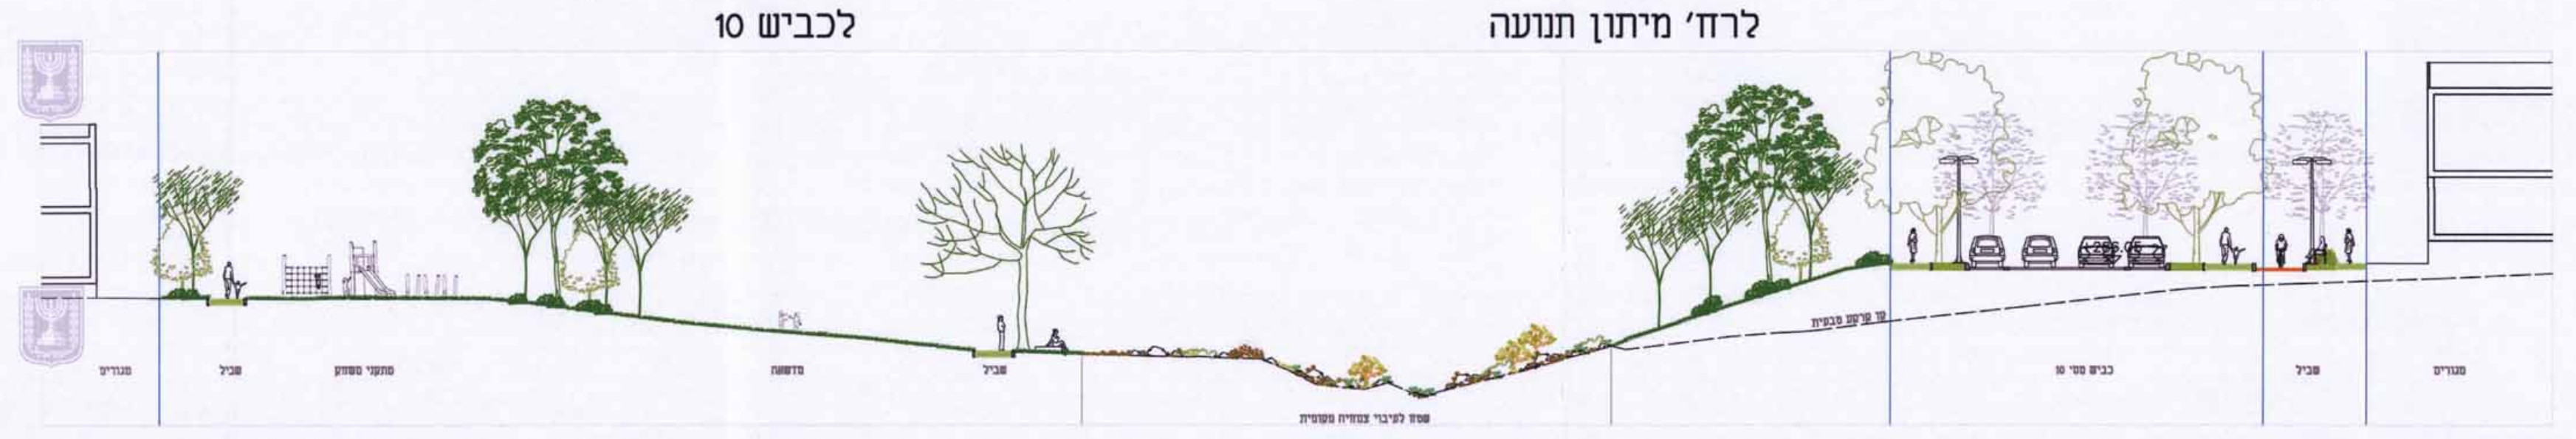

חתך ג-ג קנ"מ 1:200