7.3	שכונת הרקפות באר שבע

נספחים
פרטי פיתוח
רחובות טיפוסיים

תאריך: 21.01.2019 קנ"מ: משתנה
מהדורה: 003

Xapuc –
21/01/2019
עיריית באר-שבע
אולגה חריטונוב
אגף הנדסה
מנהלת מחלקת
תיאום תשתיות דרכים ופיתוח

באר שבע
עיר ההזדמנויות של ישראל

מנהלת הסכם הגג
באר שבע

אדר' תמר פרית שרביט
מהנדסת העיר
באר שבע

0 2 -05- 2024

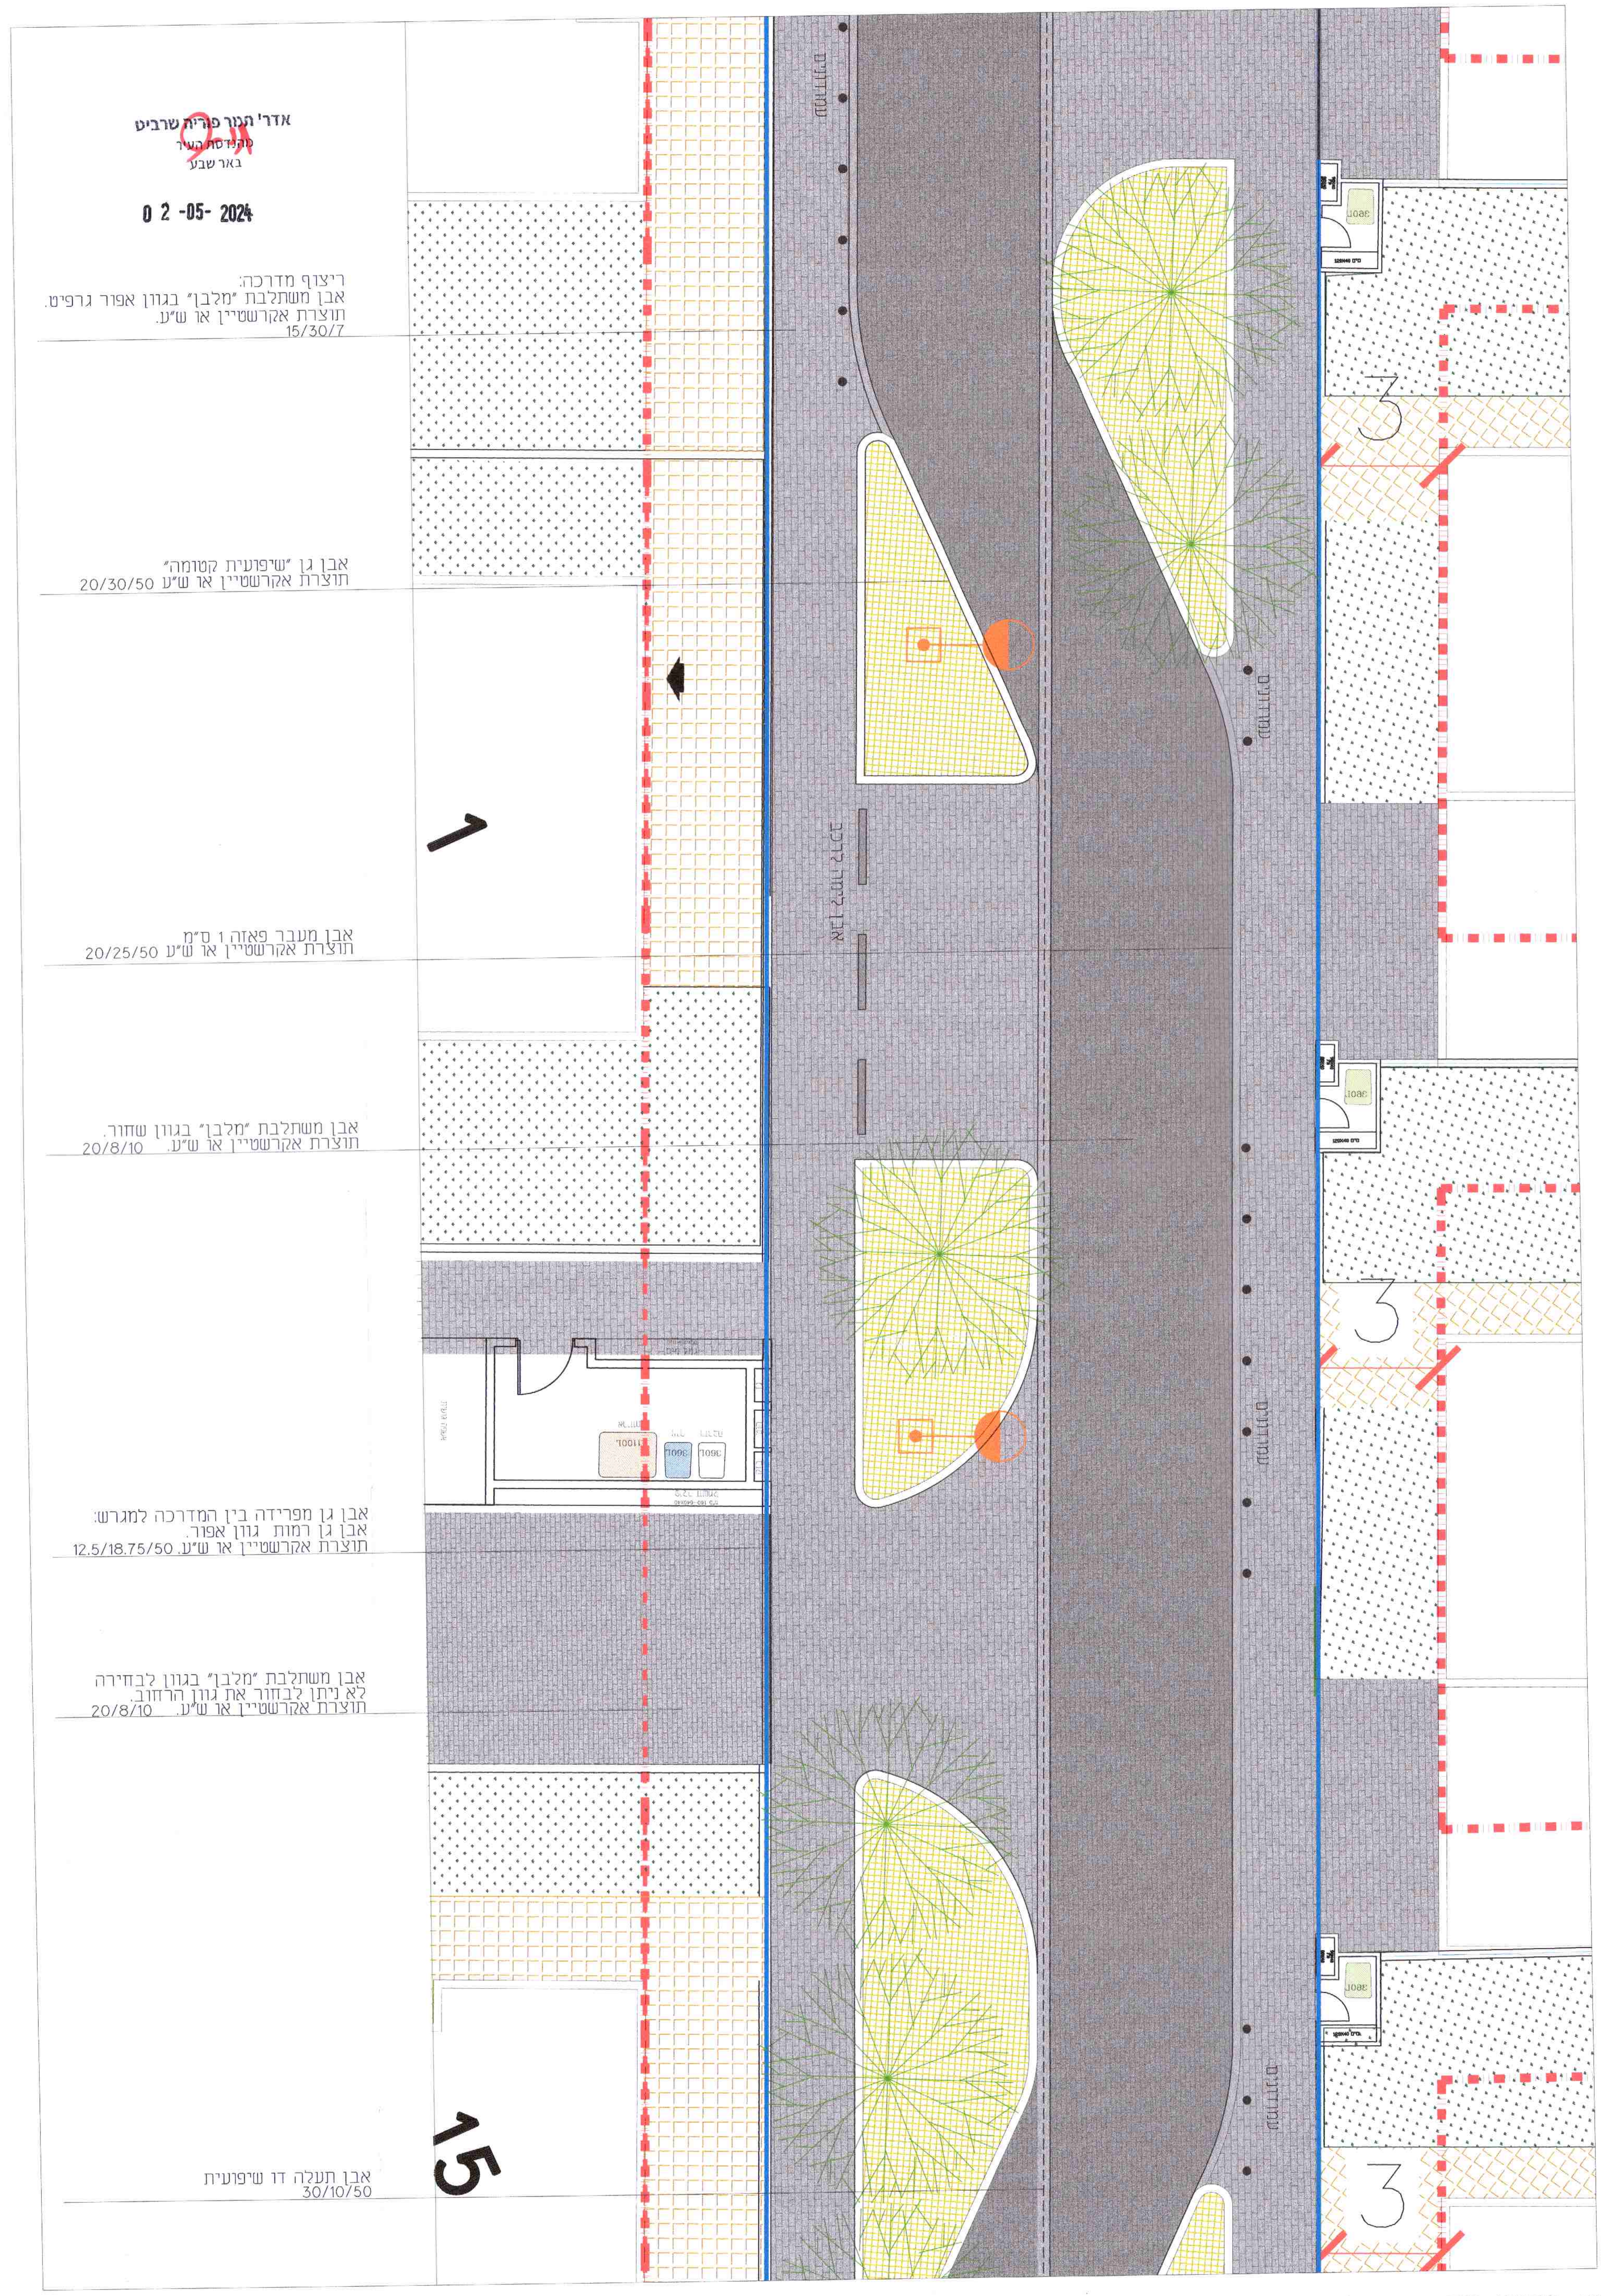

ריצוף מדרכה:
אבן משתלבת "מלבן" בגוון אפור גרפיט.
תוצרת אקרשטיין או ש"ע.
15/30/7
אבן גן "שיפועית קטומה"
תוצרת אקרשטיין או ש"ע 20/30/50
אבן מעבר פאזה 1 ס"מ
תוצרת אקרשטיין או ש"ע 20/25/50
אבן משתלבת "מלבן" בגוון שחור.
תוצרת אקרשטיין או ש"ע. 20/8/10
אבן גן מפרידה בין המדרכה למגרש:
אבן גן רמות גוון אפור.
תוצרת אקרשטיין או ש"ע. 12.5/18.75/50
אבן משתלבת "מלבן" בגוון לבחירה
לא ניתן לבחור את גוון הרחוב.
תוצרת אקרשטיין או ש"ע. 20/8/10
אבן תעלה דו שיפועית
30/10/50
1
15
3

14. מקטע רחוב משולב - תכנית טיפוסית 1:100

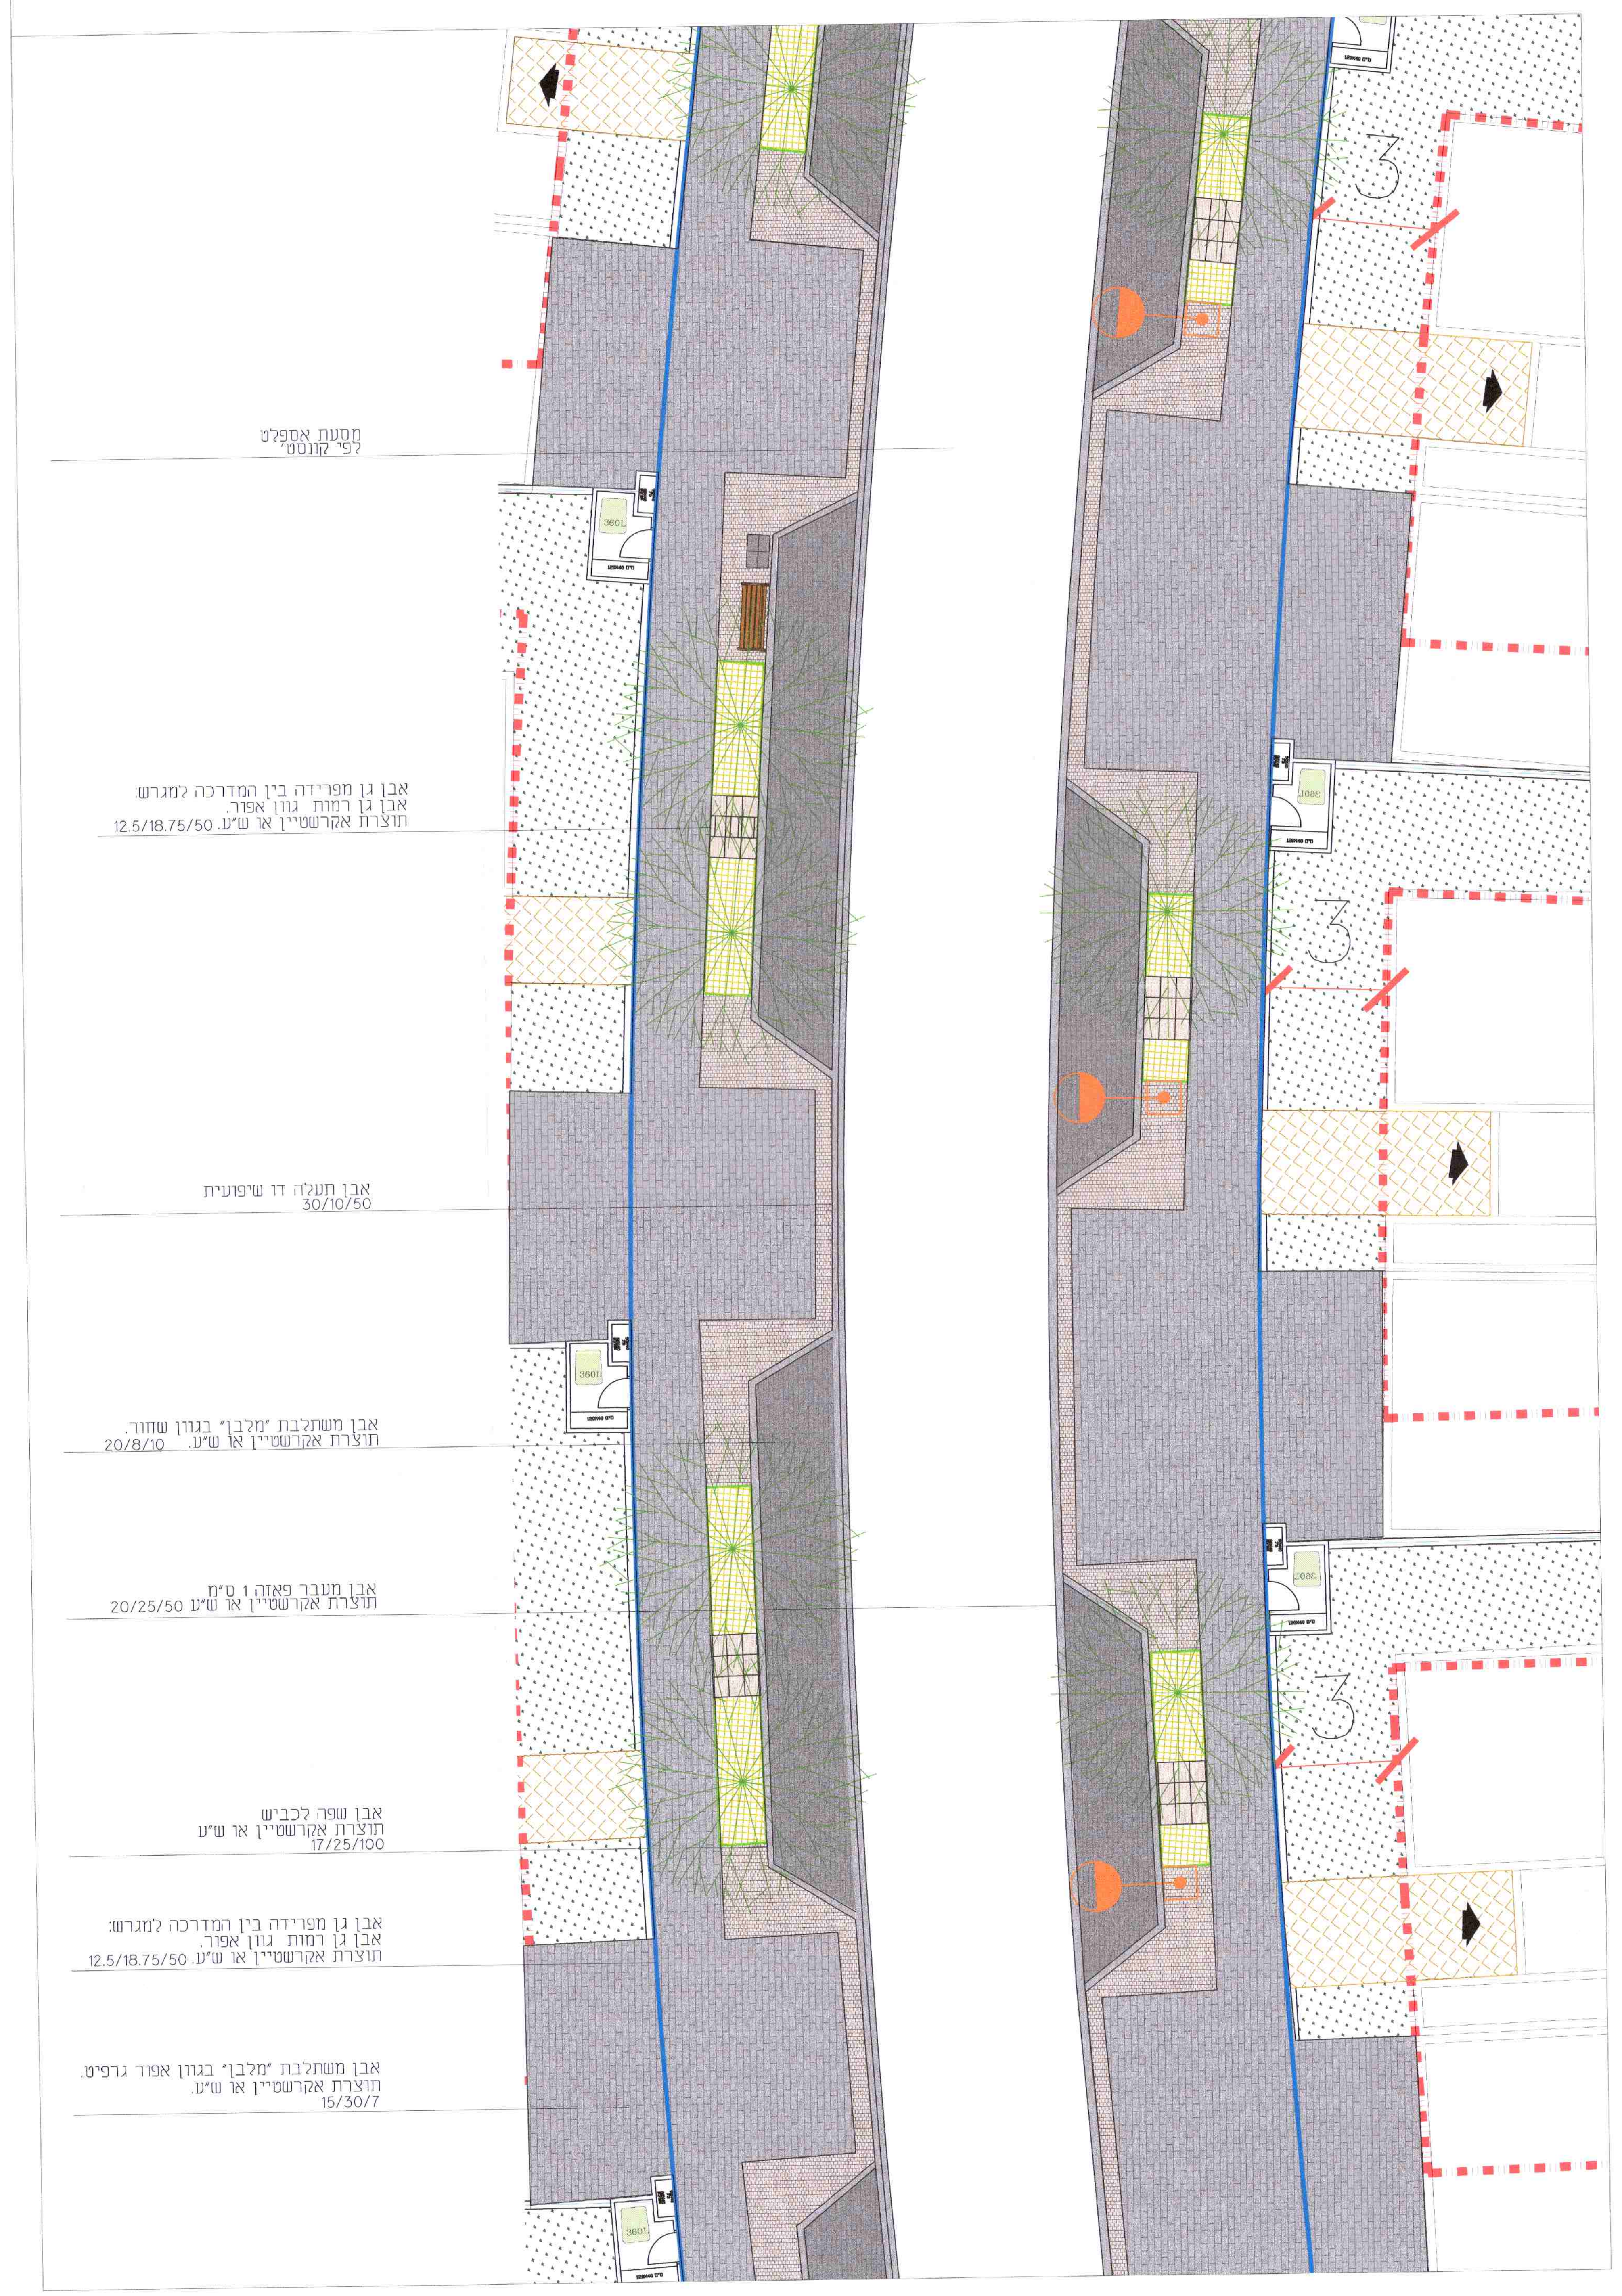

מסעת אספלט
לפי קונסט'
אבן גן מפרידה בין המדרכה למגרש:
אבן גן רמות גוון אפור.
תוצרת אקרשטיין או ש"ע. 12.5/18.75/50
אבן תעלה דו שיפועית
30/10/50
אבן משתלבת "מלבן" בגוון שחור.
תוצרת אקרשטיין או ש"ע. 20/8/10
אבן מעבר פאזה 1 ס"מ
תוצרת אקרשטיין או ש"ע 20/25/50
אבן שפה לכביש
תוצרת אקרשטיין או ש"ע
17/25/100
אבן גן מפרידה בין המדרכה למגרש:
אבן גן רמות גוון אפור.
תוצרת אקרשטיין או ש"ע. 12.5/18.75/50
אבן משתלבת "מלבן" בגוון אפור גרפיט.
תוצרת אקרשטיין או ש"ע.
15/30/7
3

13. מקטע כביש - תכנית טיפוסית 1:100

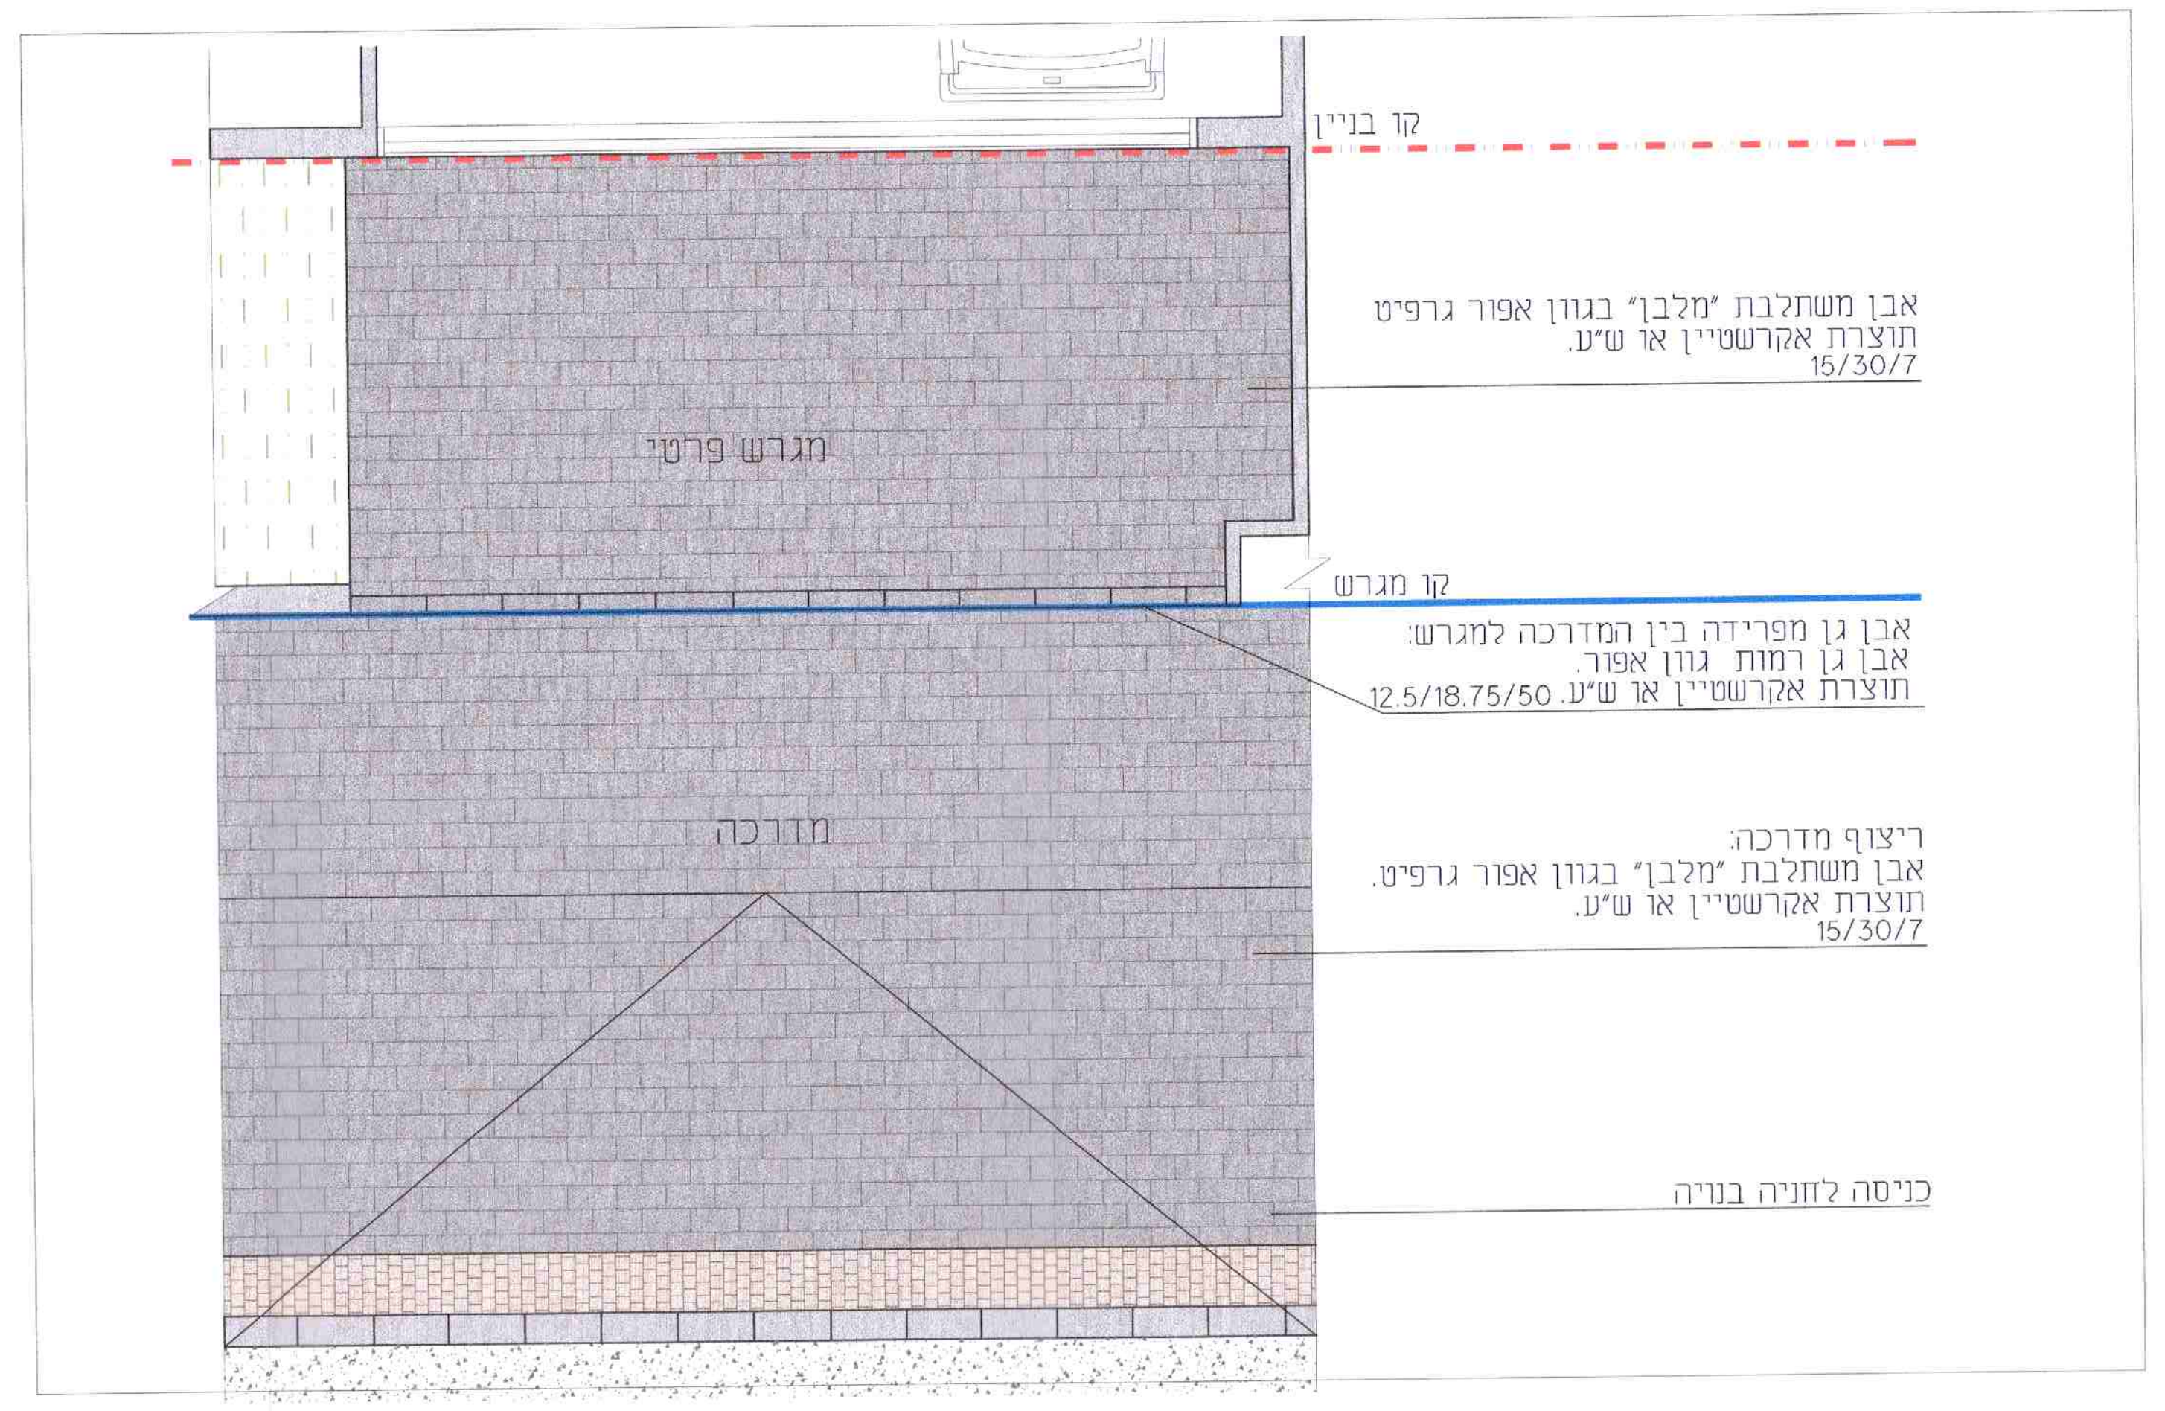

10. ריצוף בכניסות לחניות, מגרשי 'בנה ביתך' 1:50

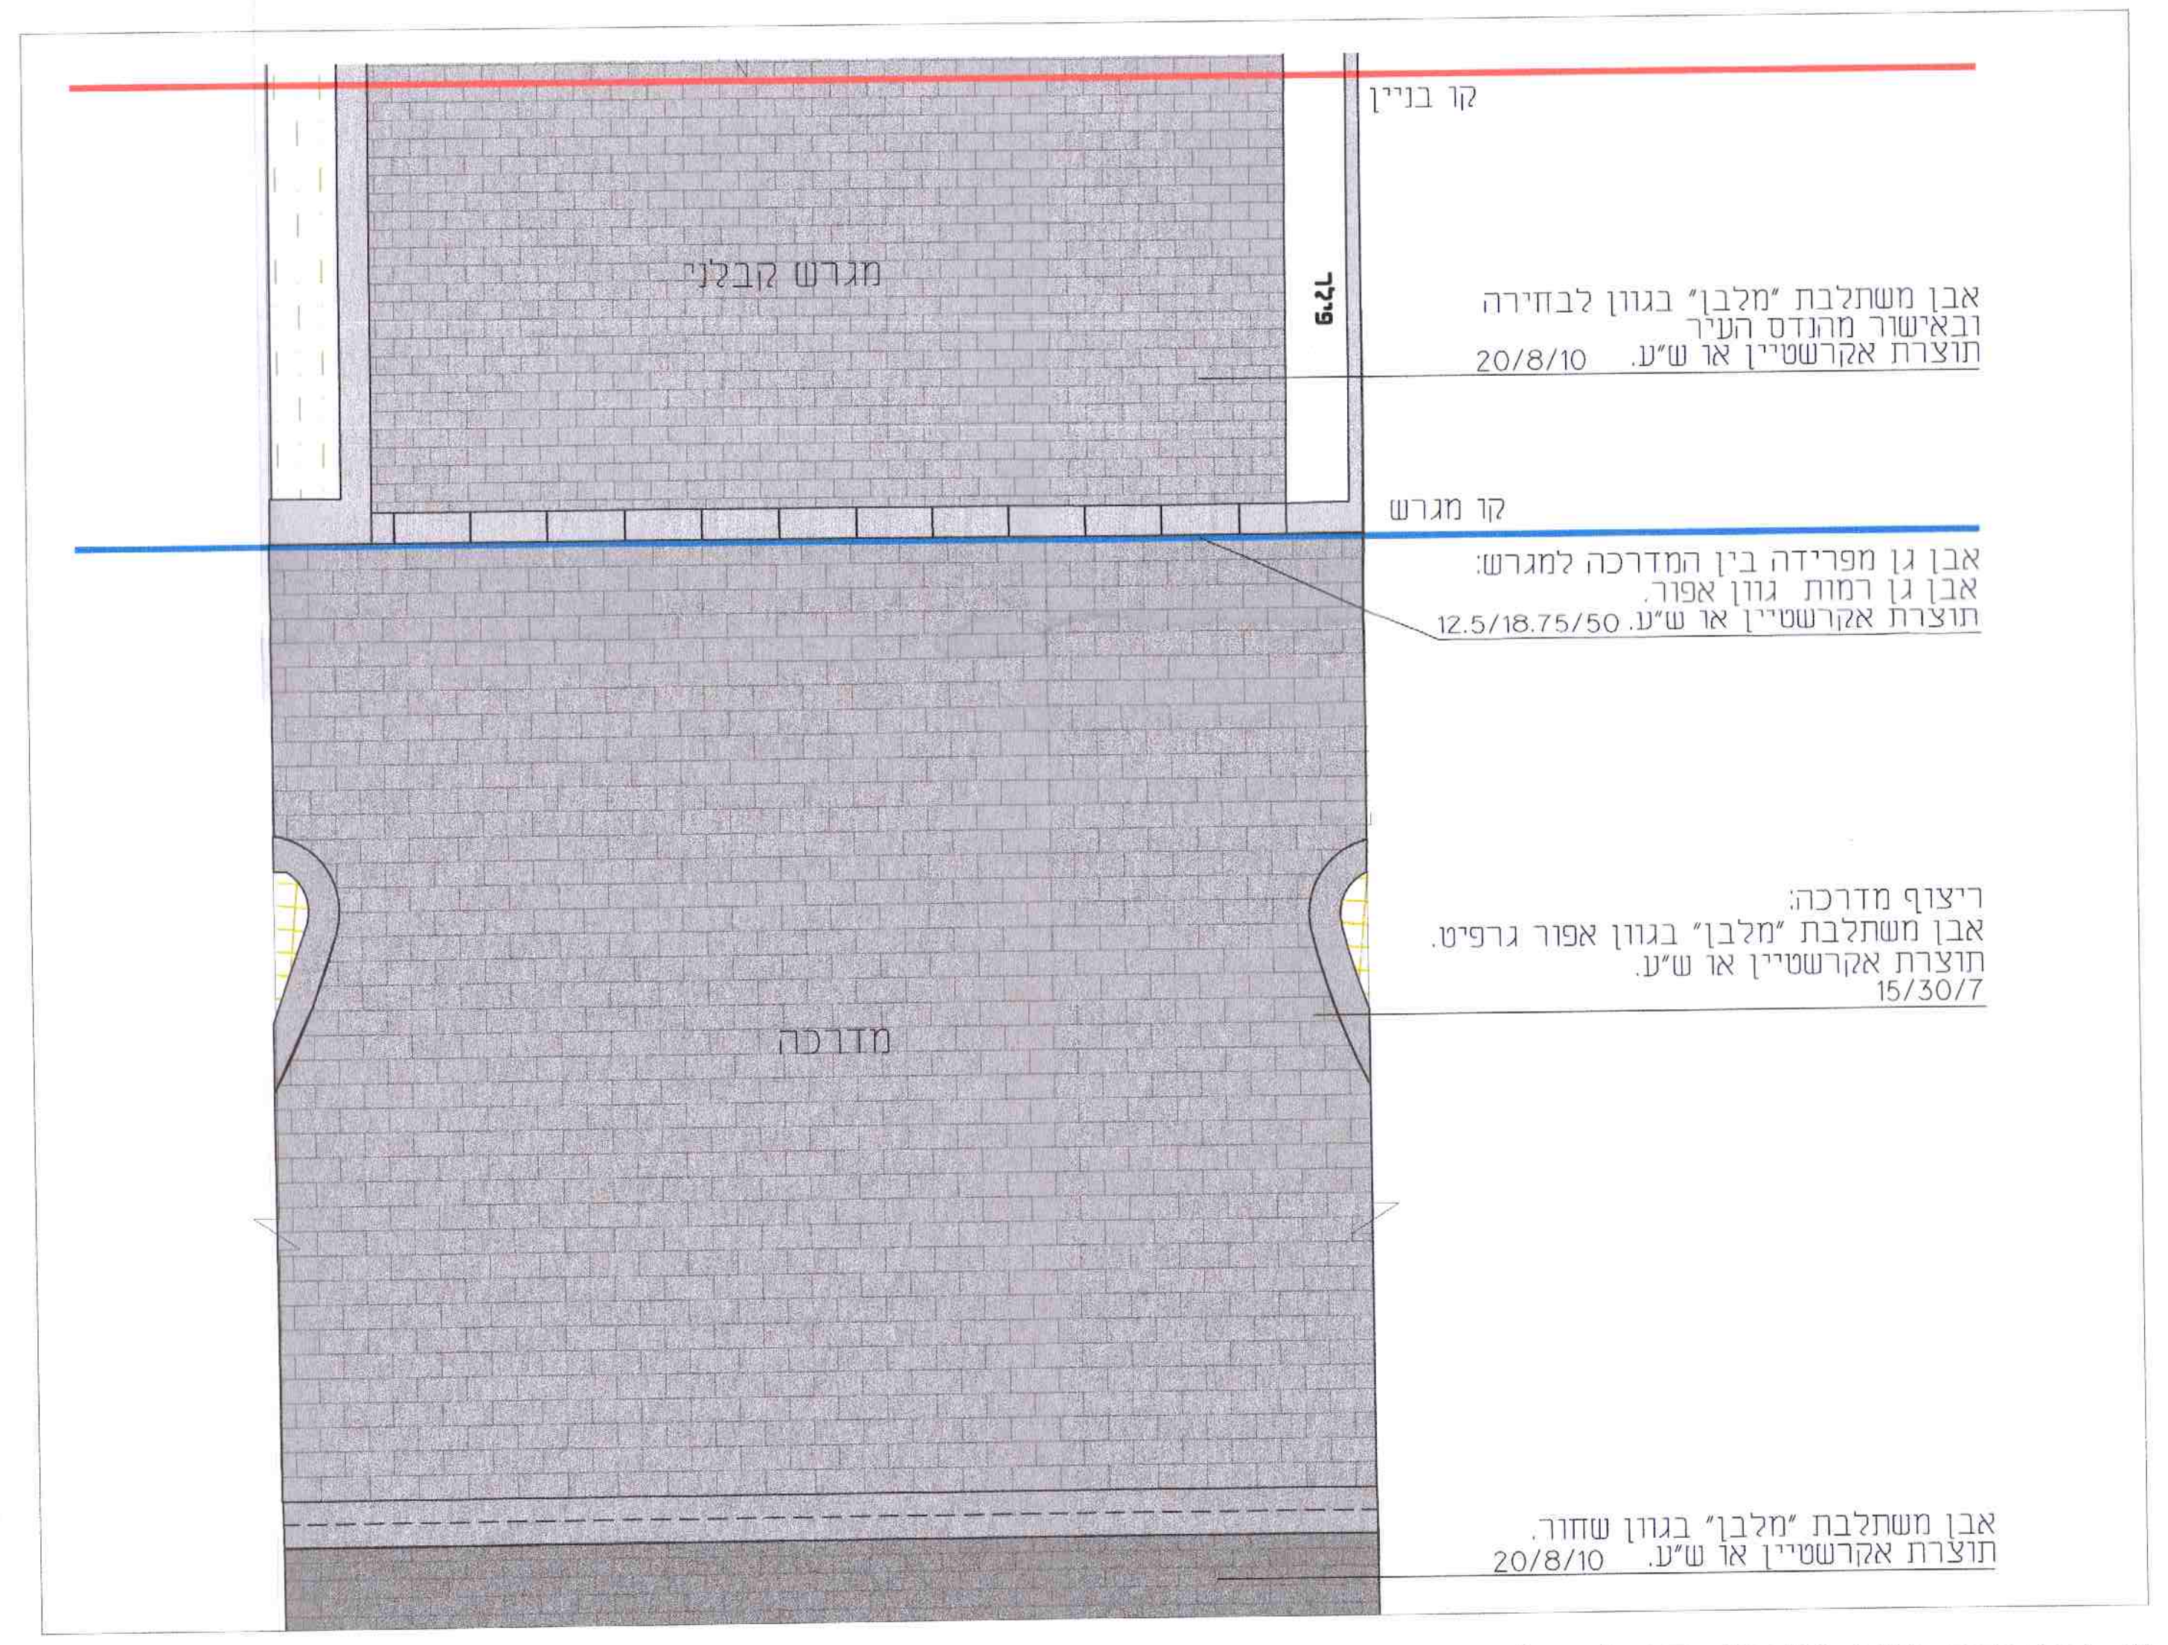

קו בניין
מגרש קבלני
אבן משתלבת "מלבן" בגוון לבחירה
ובאישור מהנדס העיר
תוצרת אקרשטיין או ש"ע. 20/8/10
קו מגרש
אבן גן מפרידה בין המדרכה למגרש:
אבן גן רמות גוון אפור.
תוצרת אקרשטיין או ש"ע. 12.5/18.75/50
מדרכה
ריצוף מדרכה:
אבן משתלבת "מלבן" בגוון אפור גרפיט.
תוצרת אקרשטיין או ש"ע.
15/30/7
אבן משתלבת "מלבן" בגוון שחור.
תוצרת אקרשטיין או ש"ע. 20/8/10

11. הפרדה בין מגרש קבלני לכביש 1:50

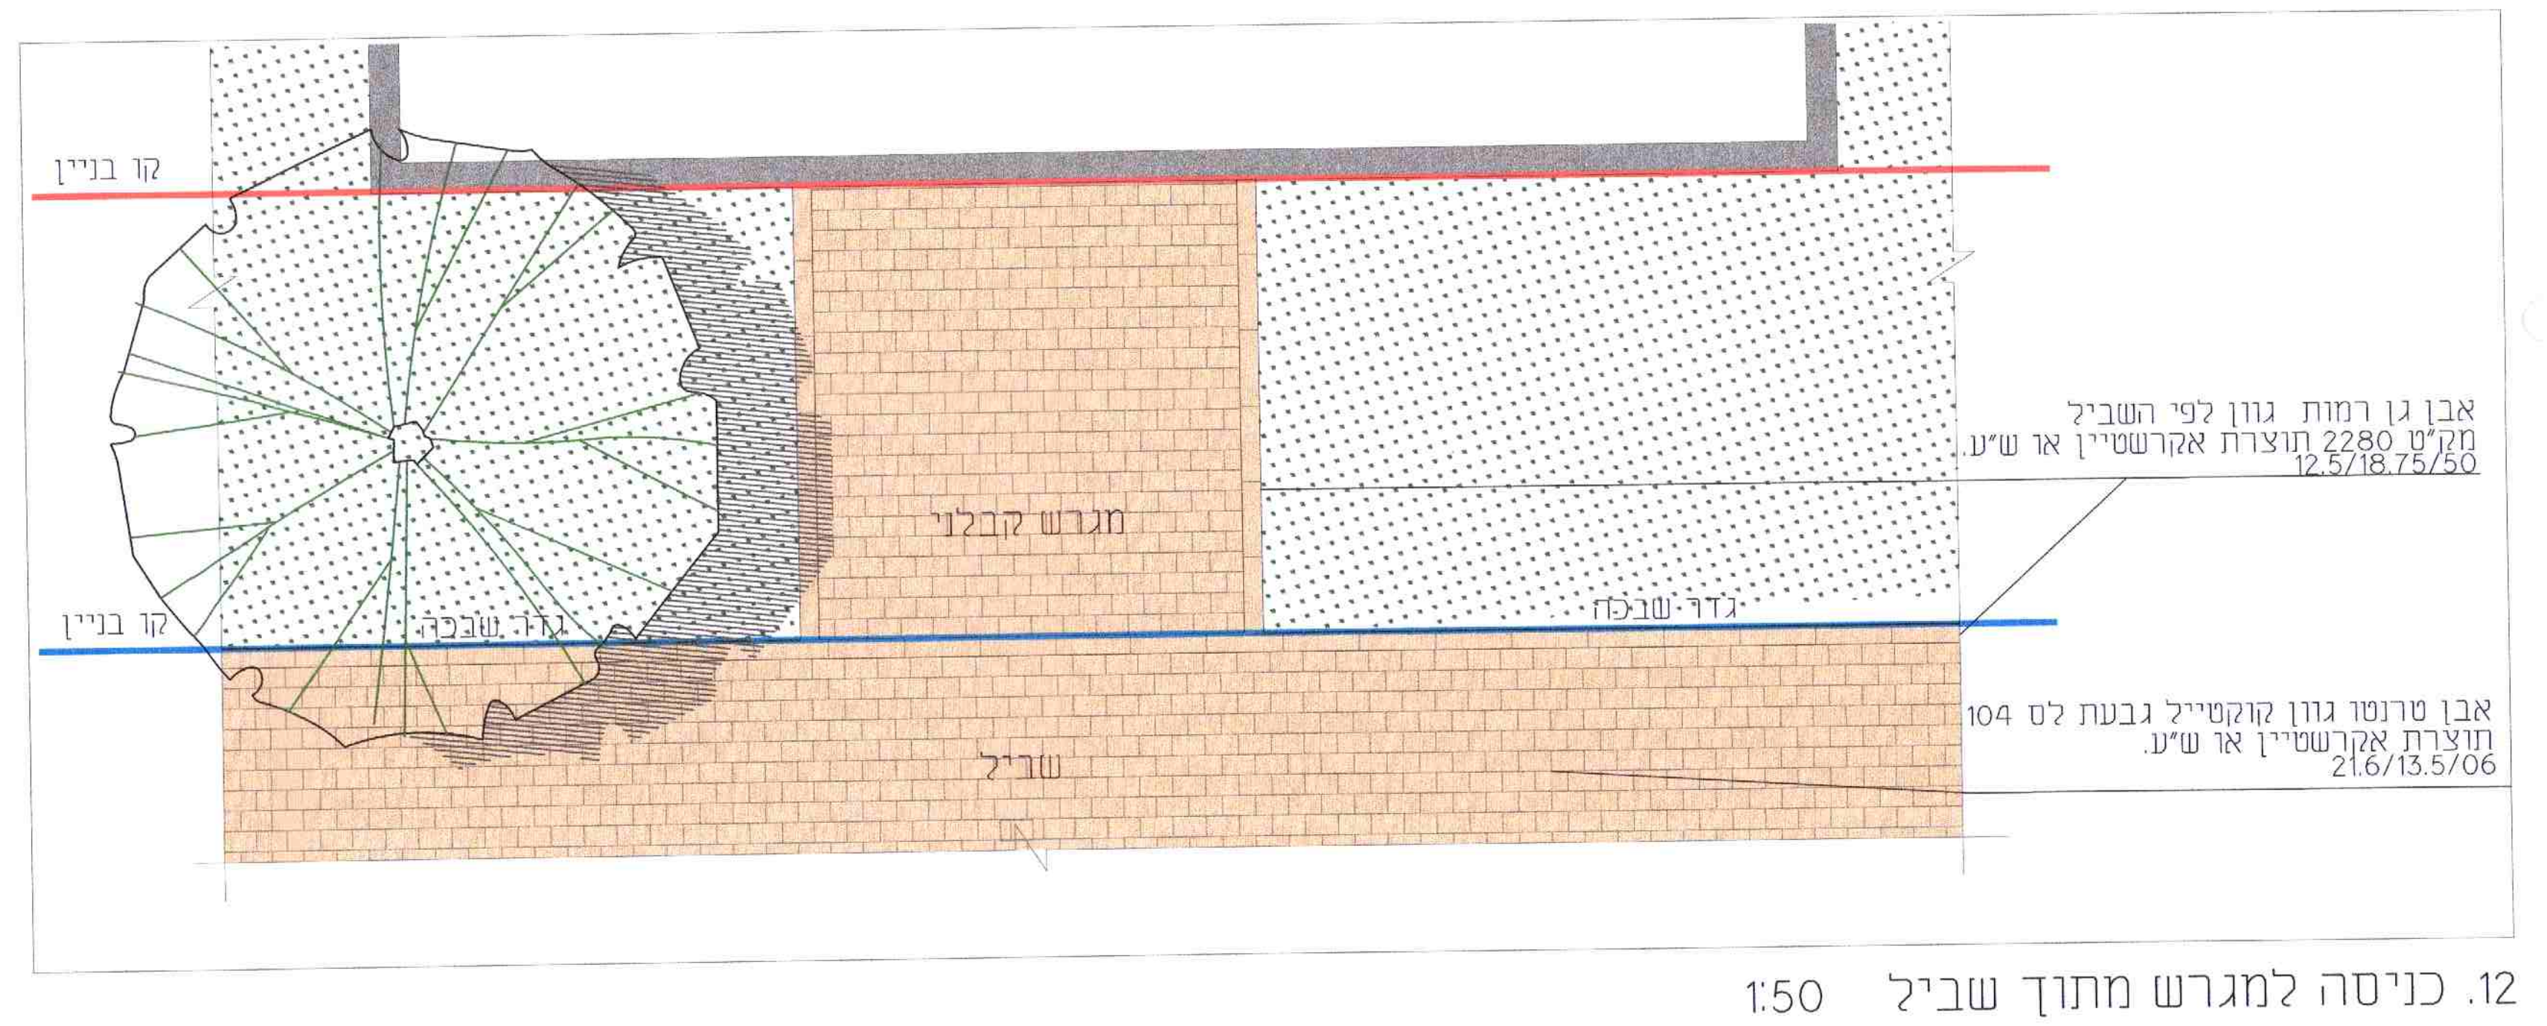

קו בניין
מגרש קבלני
גדר שבכה
קו בניין
שביל
אבן גן רמות גוון לפי השביל
מק"ט 2280 תוצרת אקרשטיין או ש"ע.
12.5/18.75/50
אבן טרנטו גוון קוקטייל גבעת לס 104
תוצרת אקרשטיין או ש"ע.
21.6/13.5/06

12. כניסה למגרש מתוך שביל 1:50