1.5

שכונת הרקפות
באר שבע

תכניות חזיתות וחתכים
טיפוס 3A

תאריך: 03.05.2022 קנ"מ: 1:200

מהדורה: 108

אין התנגדות
9/08/2022

אולגה חריטונוב
עיריית באר-שבע
אגף הנדסה
מנהלת מחלקת
תיאום תשתיות דרכים ופיתוח

6/3/24
אדר' מור שוייצר
צוות אדריכל העיר
עיריית באר שבע

ועדה מקומית באר-שבע
אישור תוכנית מס' גימל 1016 (2)
הוועדה המקומית החליטה לאשר את התוכנית
בישיבה מס' 20230012 מיום 30/6/24

שלומי נומה
סגן ומ"מ ראש העיר
יו"ר ועדה לתכנון ובנייה
עיריית באר שבע

באר7שבע
בירת ההזדמנויות של ישראל

מנהלת הסכם הגג
באר7שבע

27-11-2022
187-2022

מקרא :

גבול מגרש	—
קו בניין	- - -
חצר אפקטיבית	⬚
חצר פרטית	▨
ריצוף/שביל	▨
אשפה	■
מפלס עקרוני בשטחים ציבוריים	-0.20
מפלס קומה	+0.00
מס' חזית וסימונה	1 ▼
שטח השהייה	▨
שביל כניסה ראשית	▨

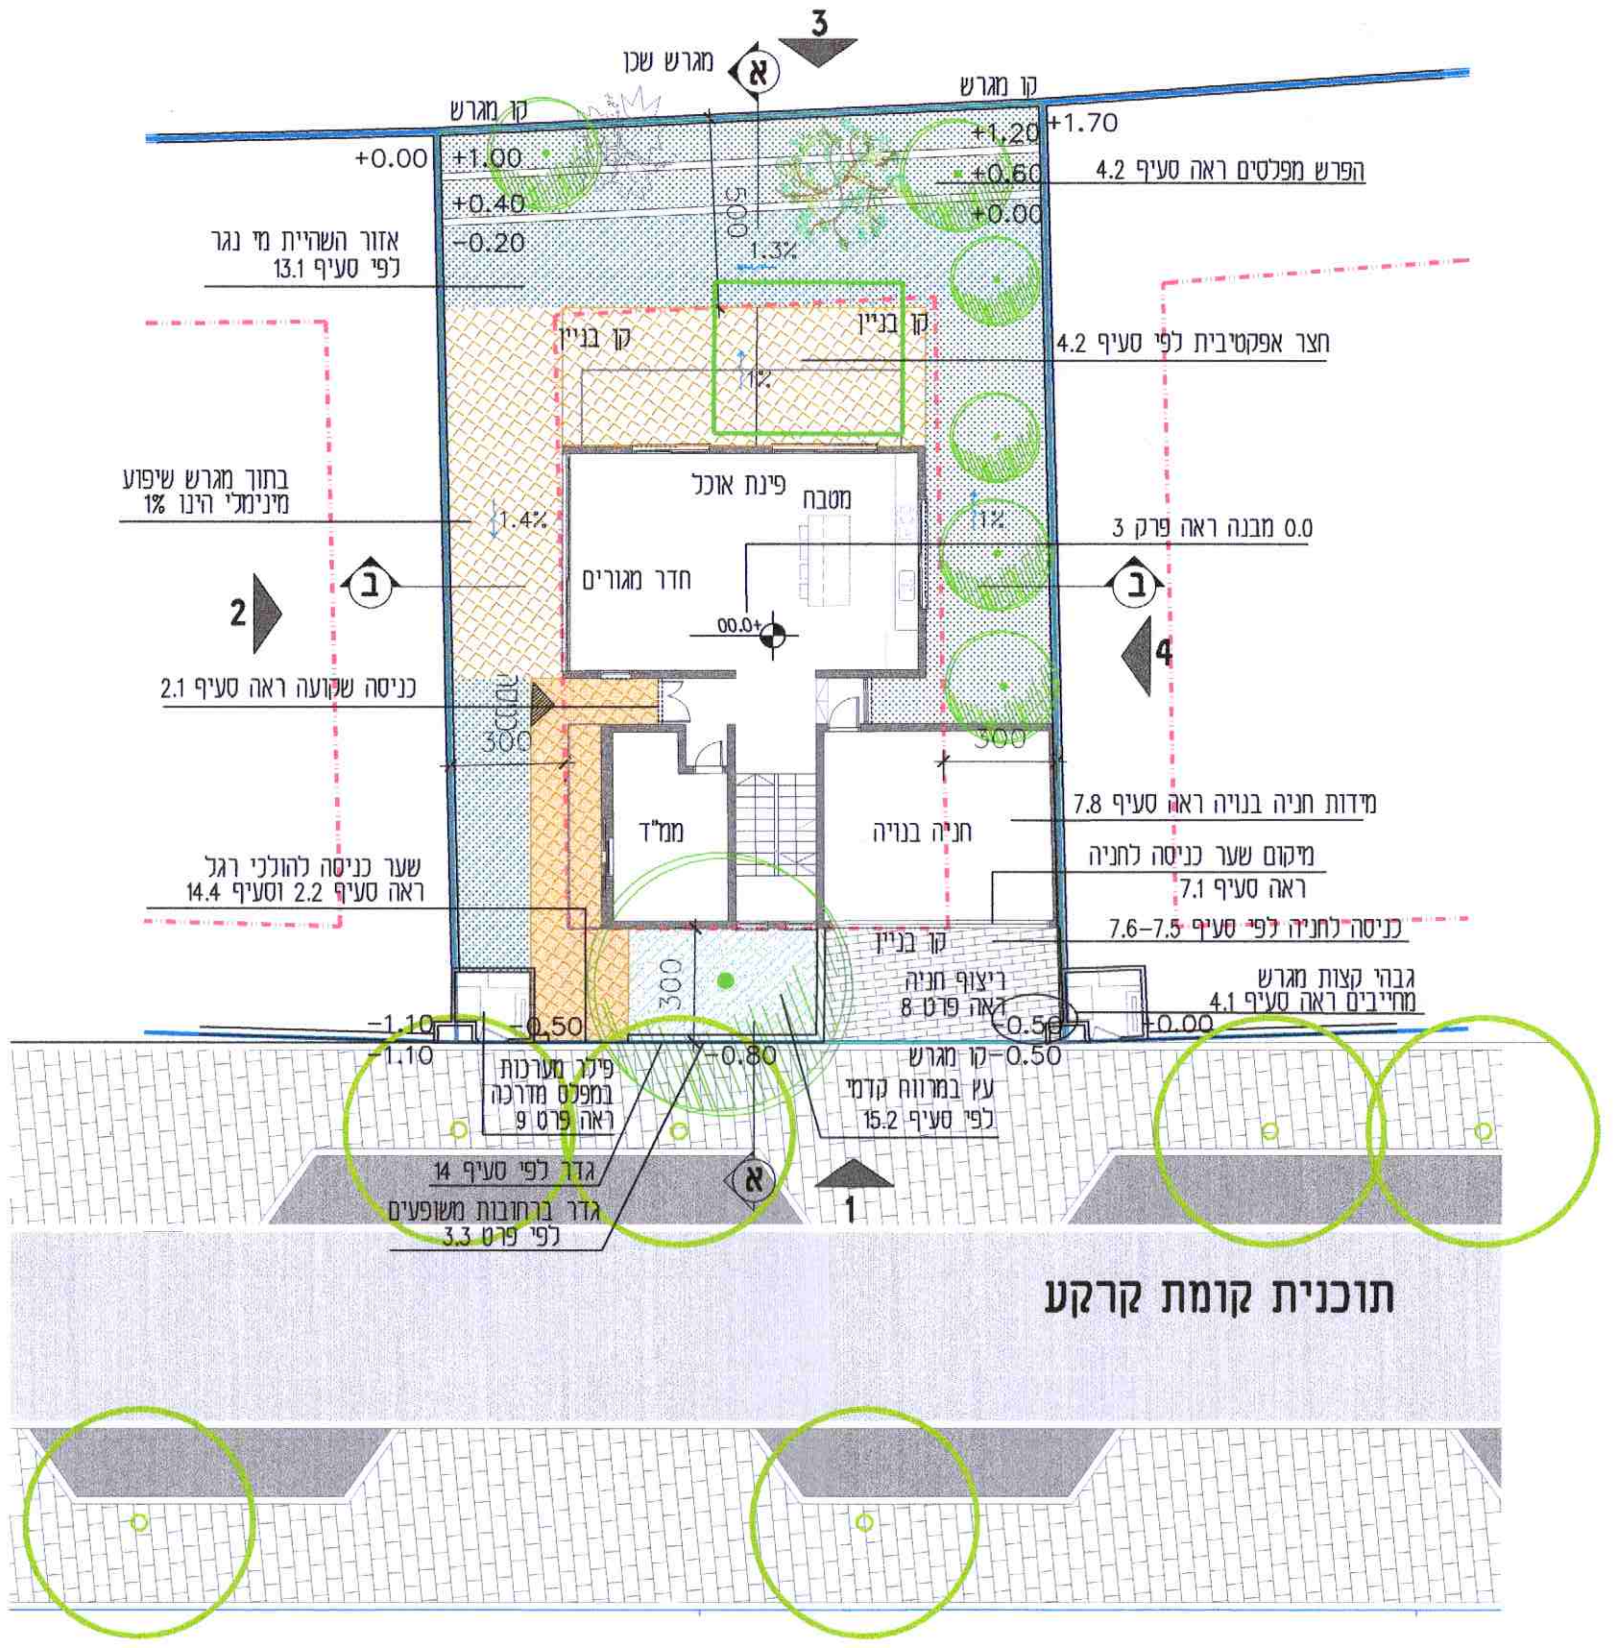
3
א
מגרש שכן
קו מגרש
קו מגרש
+0.00
+1.00
+0.40
-0.20
+1.20
+1.70
+0.60
+0.00
500
1.3%
הפרש מפלסים ראה סעיף 4.2
אזור השהיית מי נגר לפי סעיף 13.1
קו בניין
קו בניין
1%
חצר אפקטיבית לפי סעיף 4.2
בתוך מגרש שיפוע מינימלי הינו 1%
1.4%
פינת אוכל
מטבח
1%
0.0 מבנה ראה פרק 3
ב
חדר מגורים
ב
2
00.0+
4
כניסה שקועה ראה סעיף 2.1
300
300
ממ"ד
חניה בנויה
מידות חניה בנויה ראה סעיף 7.8
שער כניסה להולכי רגל ראה סעיף 2.2 וסעיף 14.4
מיקום שער כניסה לחניה ראה סעיף 7.1
כניסה לחניה לפי סעיף 7.5-7.6
קו בניין
300
ריצוף חניה ראה פרט 8
גבהי קצות מגרש מחייבים ראה סעיף 4.1
-1.10
-1.10
-0.50
-0.80
-0.50
-0.50
±0.00
קו מגרש
פילר מערכות במפלס מדרכה ראה פרט 9
עץ במרווח קדמי לפי סעיף 15.2
גדר לפי סעיף 14
גדר ברחובות משופעים לפי פרט 3.3
א
1

תוכנית קומת קרקע

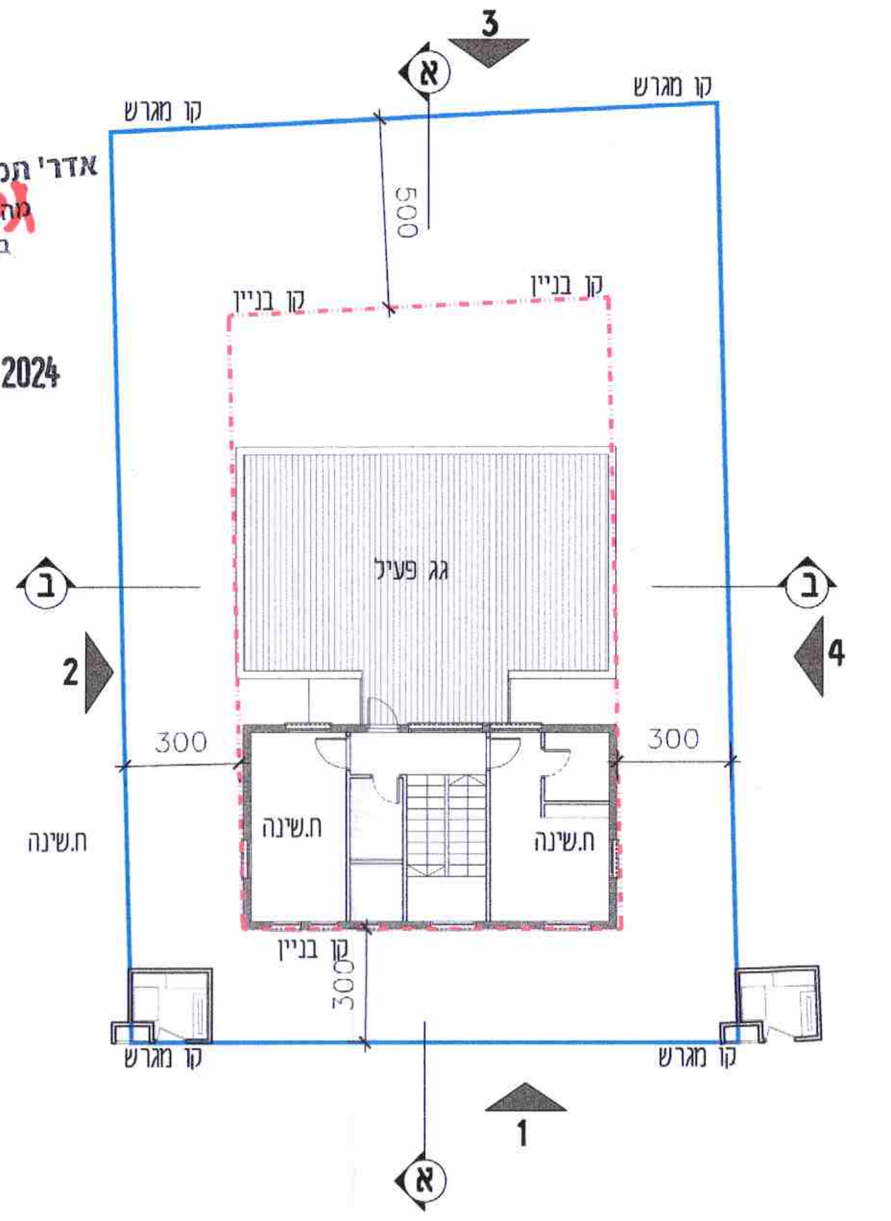

אדר' תמר פוריה שרביט
מהנדסת העיר
באר שבע

0 2 -05- 2024

תכנית קומה ראשונה

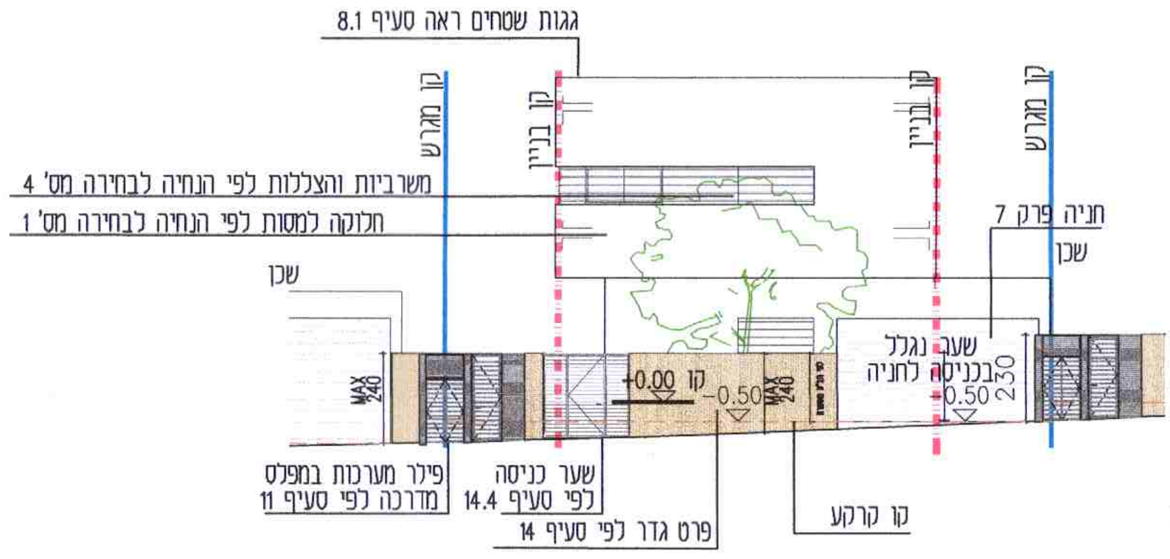

חזית 1

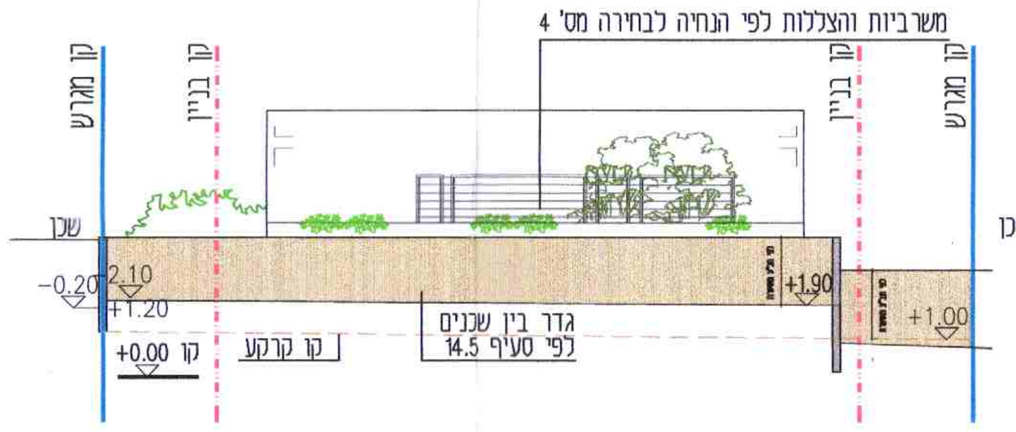

חזית 3

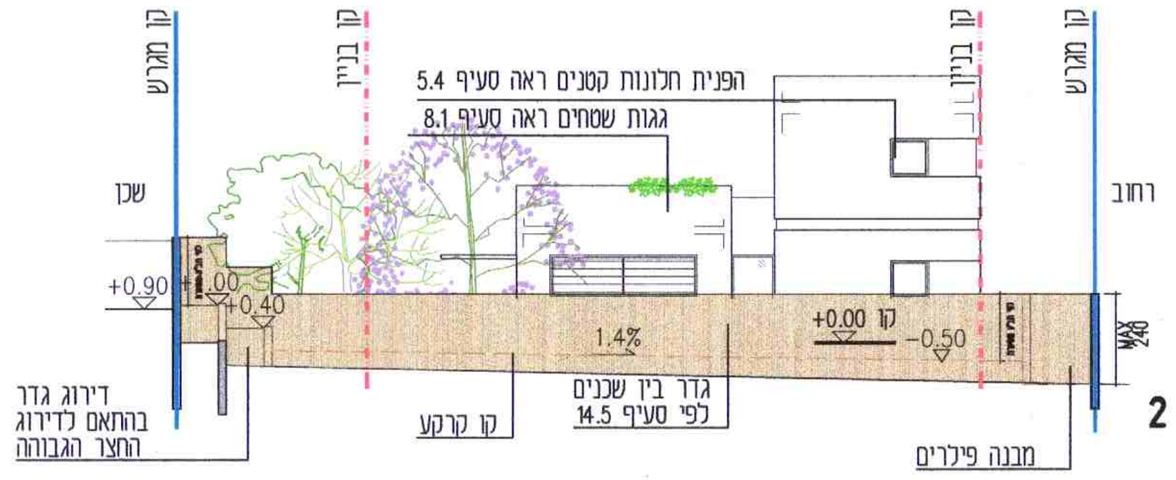

חזית 2

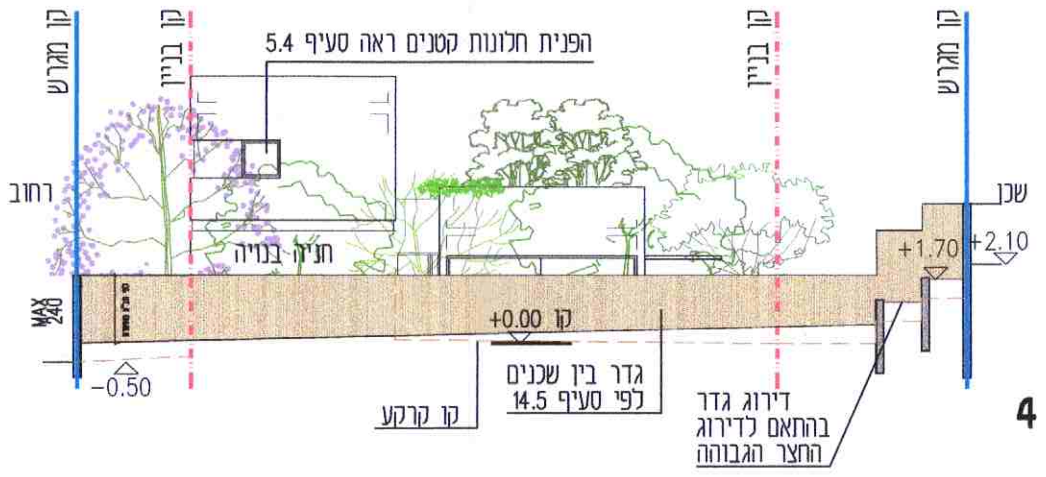
קו מגרש
קו בניין
הפנית חלונות קטנים ראה סעיף 5.4
קו בניין
קו מגרש
רחוב
שכן
חניה בנויה
+1.70
+2.10
MAX 240
+0.00 קו
-0.50
קו קרקע
גדר בין שכנים לפי סעיף 14.5
דירוג גדר בהתאם לדירוג החצר הגבוהה

חזית 4

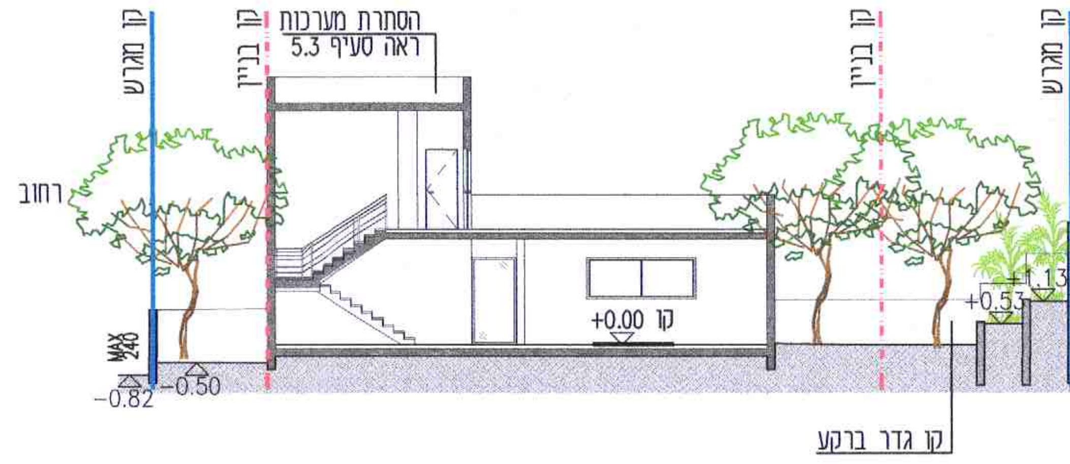

חתך א-א

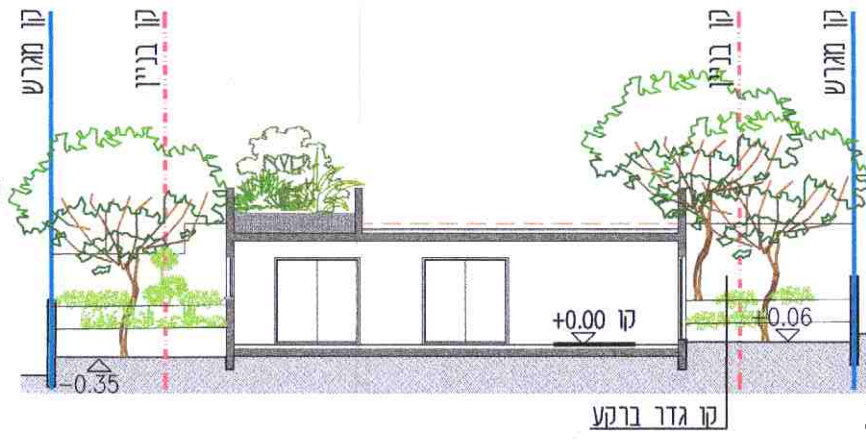

חתך ב-ב

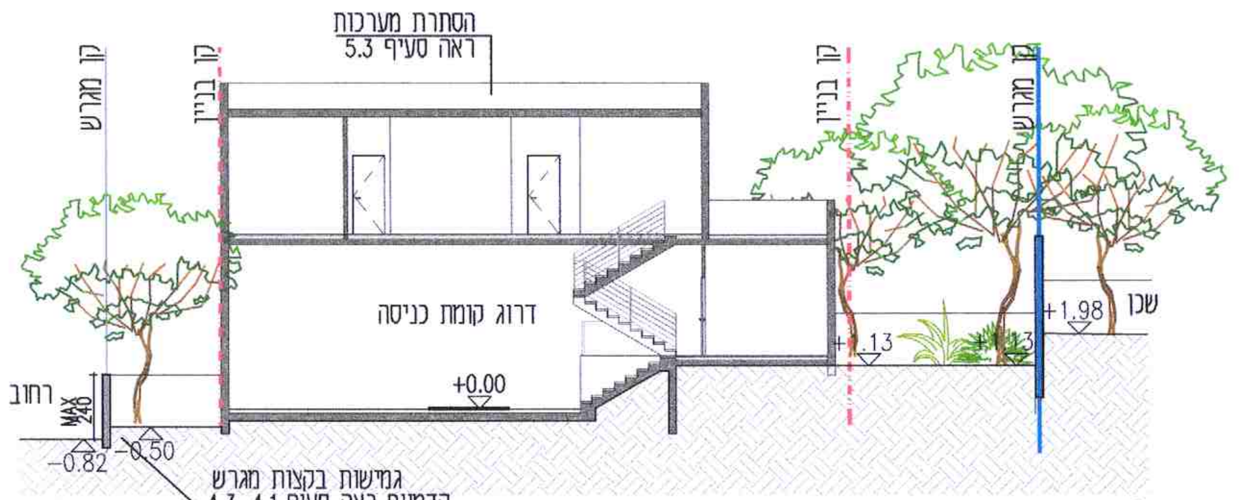

דוגמה לדרוג במבנה
חתך ג