פרט טיפוסי
פרט עיגון רשתות מעל קורות/קירות/עמודים
1:25

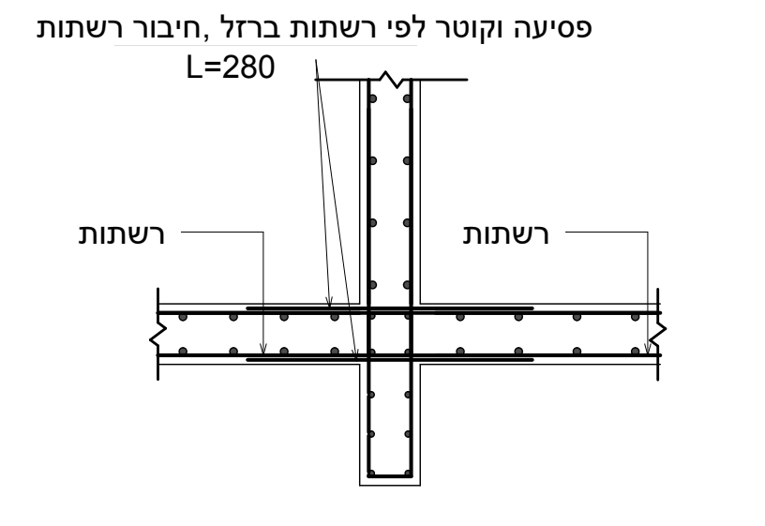

פרט טיפוסי
שינוי עובי תקרה
1:25

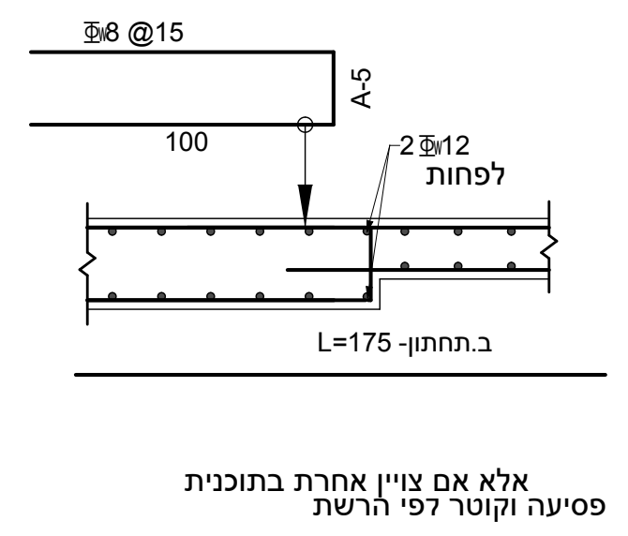

פרט טיפוסי
בקצה תקרה/רצפה
1:25

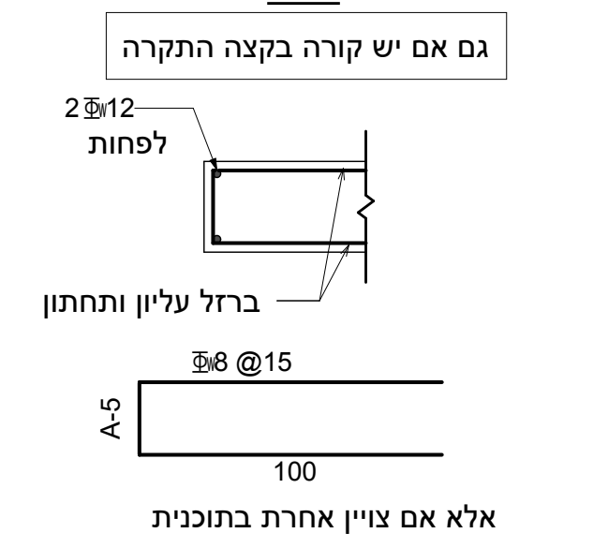

פרט טיפוסי לחיזוק
סביב פתחים ובאזור חדירת
החשמל לתקרה
1:25

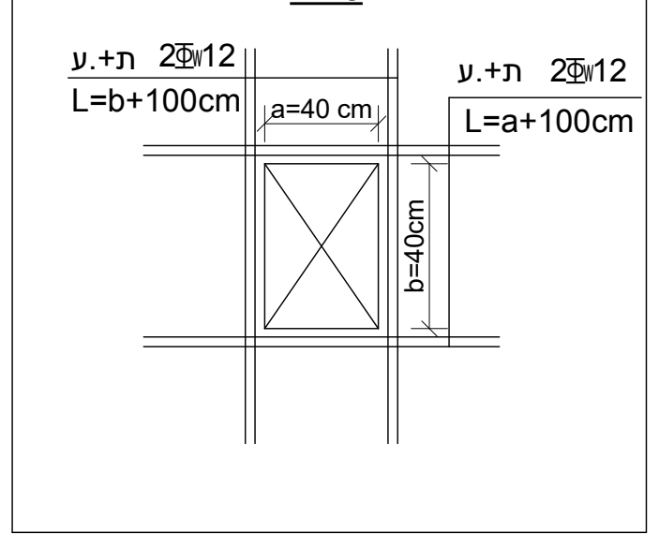

פרט טיפוסי
לסידור ברזל בקורות
1:25

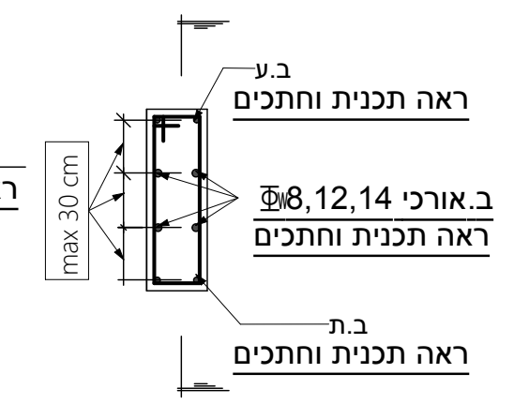

חתך1-1
1:25

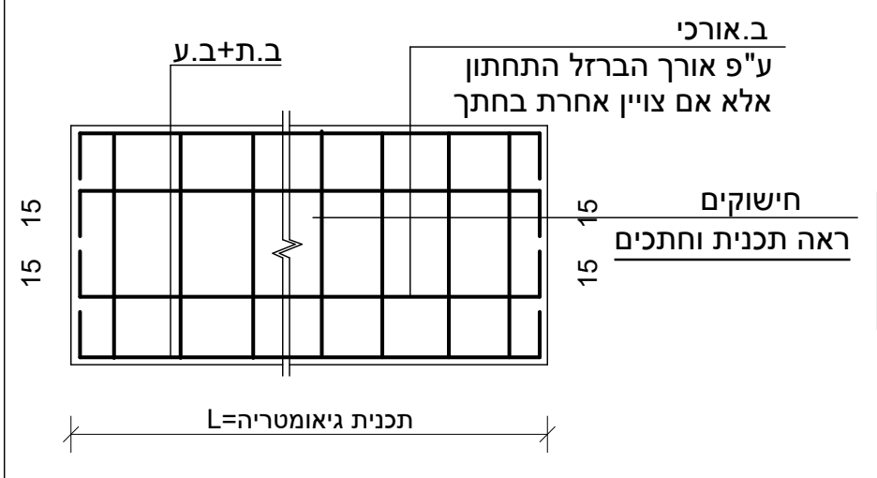

פרט אופקי.5
פרט ריתום אופקי בקירות -
פרט דלת
1:25

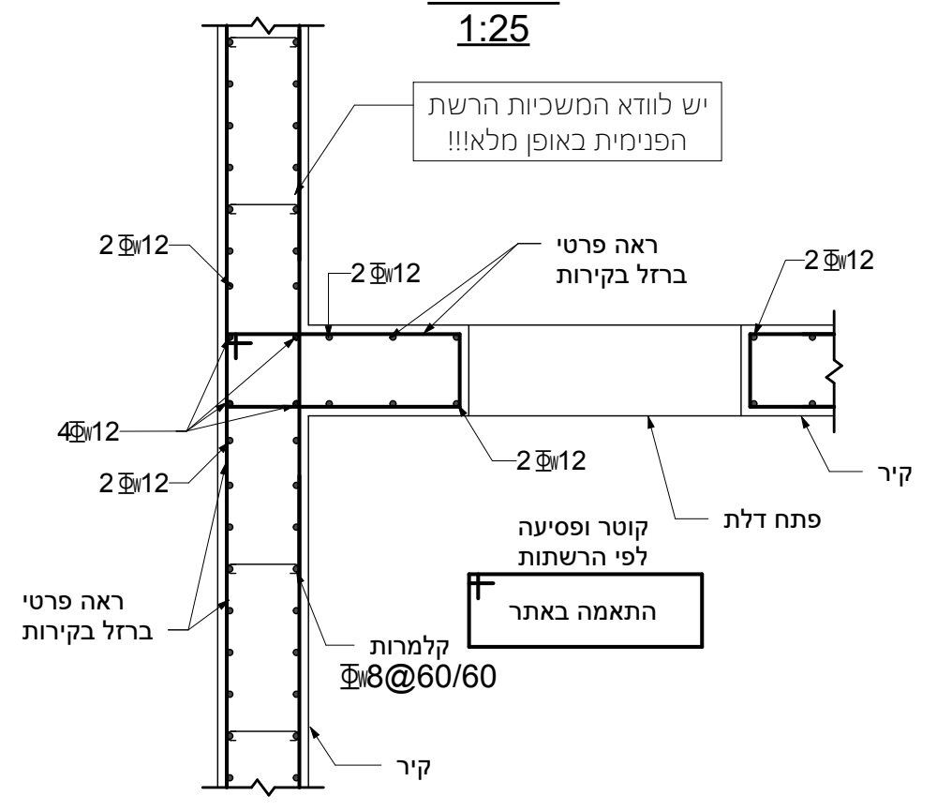

פרט אופקי.4
פרט קצה קיר
1:25

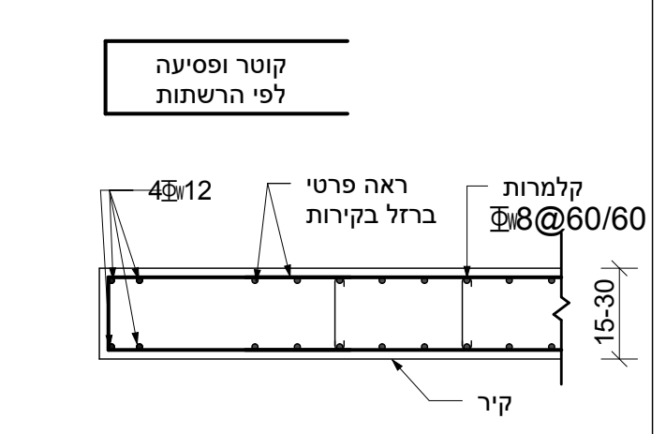

פרט אופקי.1
פרט ריתום אופקי בקירות
1:25

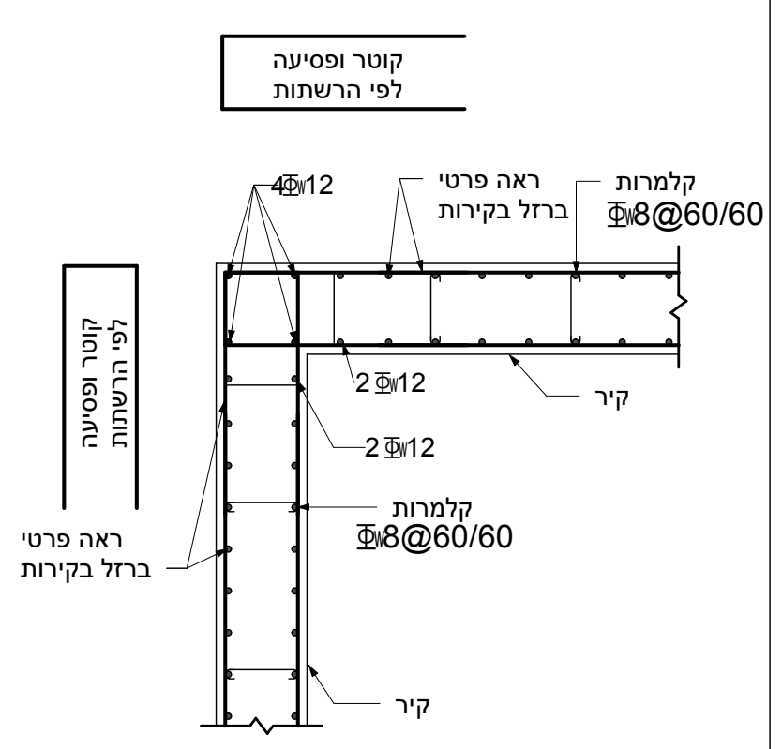

פרט אופקי.2
פרט ריתום אופקי בקירות
1:25

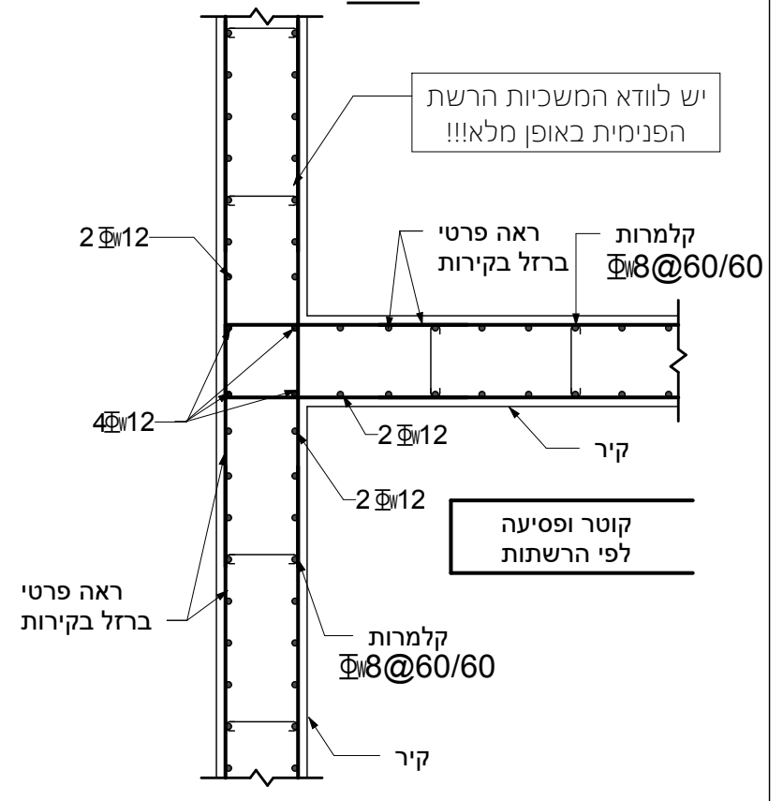

פרט אופקי.3
פרט פינת דלת
1:25

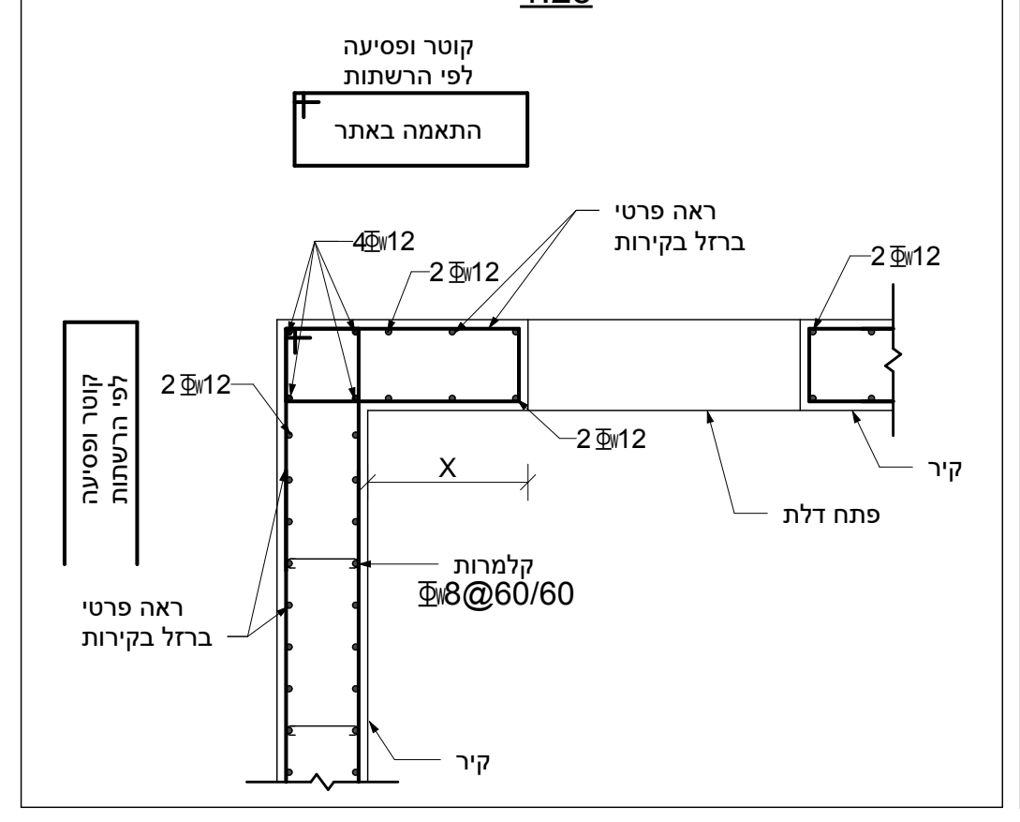

פרט אופקי.9
פרט ריתום אופקי בקירות
1:25

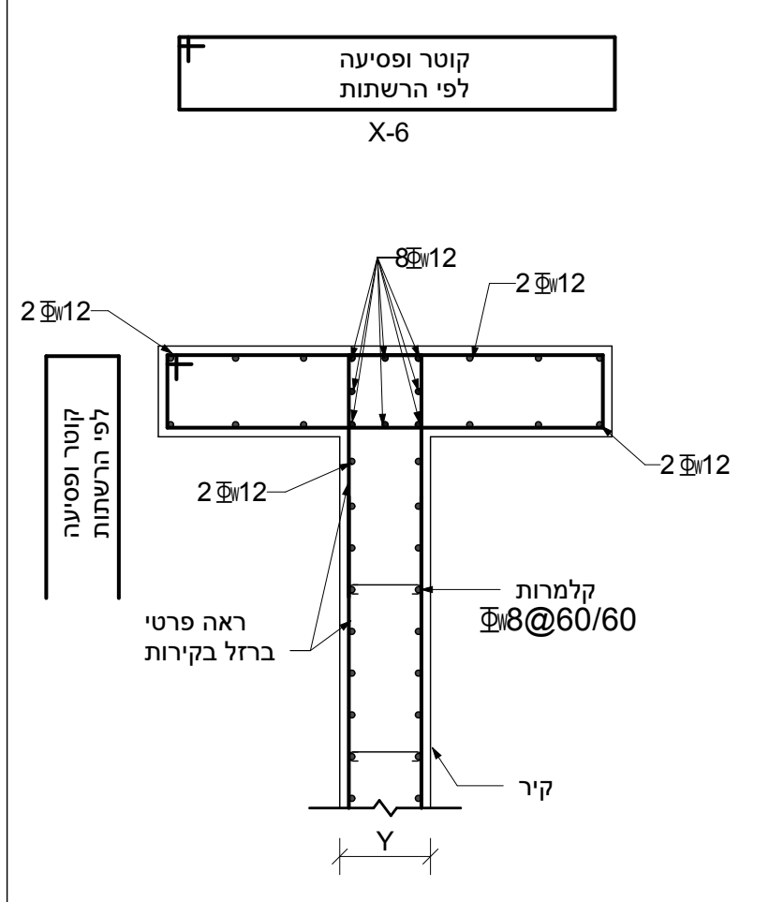

פרט אופקי.8
פרט ריתום אופקי בקירות
1:25

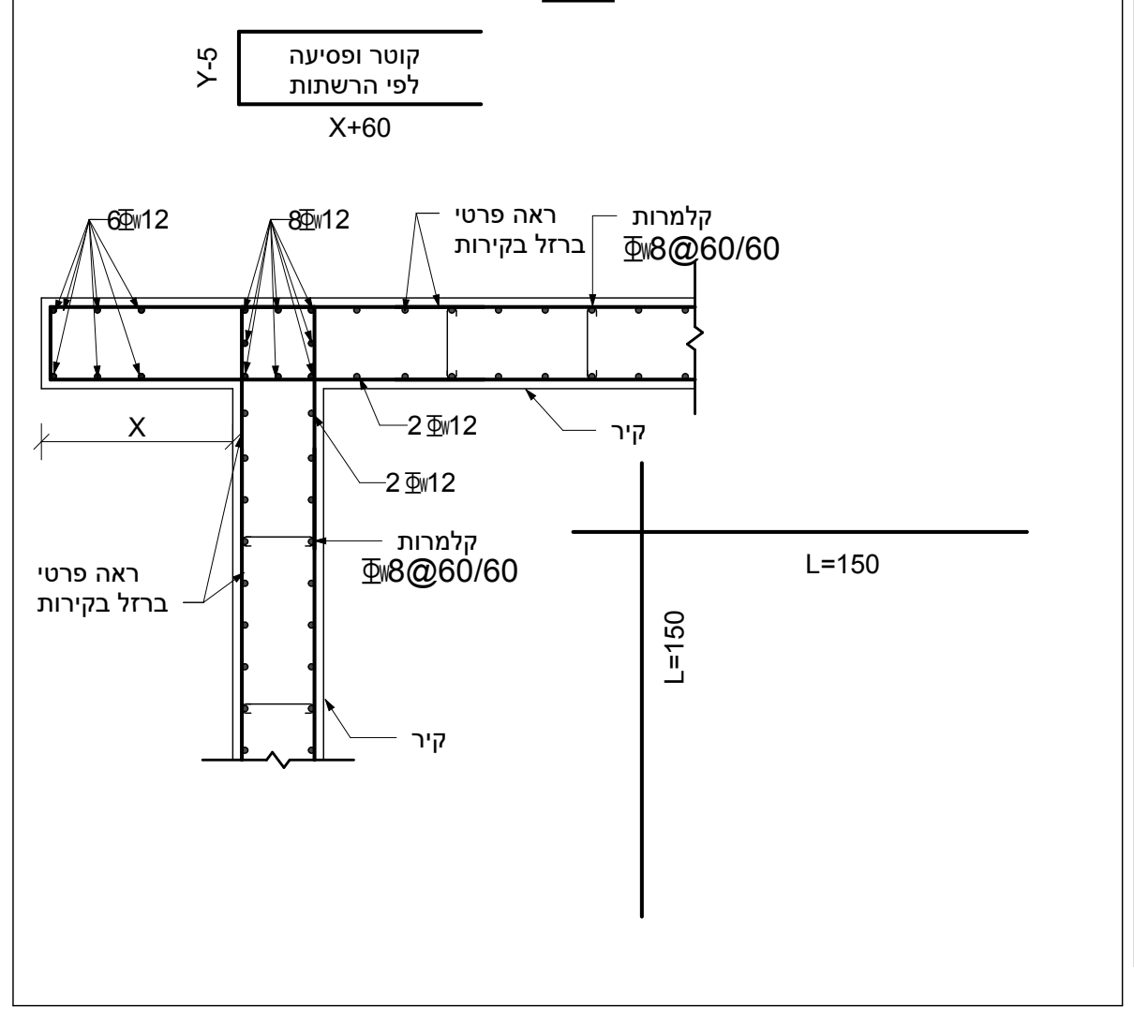

פרט אופקי.7
פרט ריתום אופקי בקירות
1:25

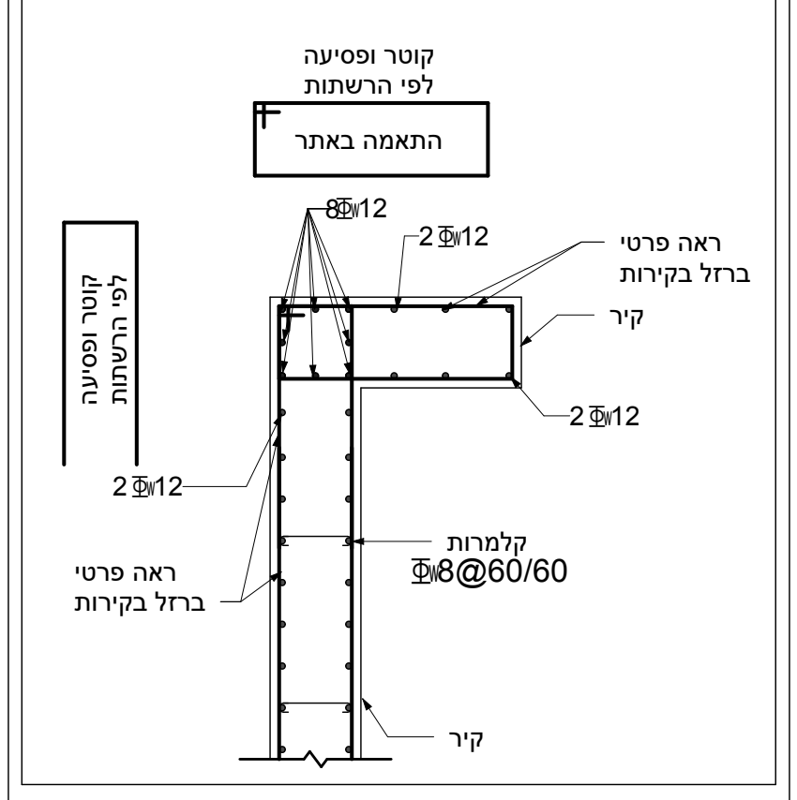

פרט אופקי.6
פרט ריתום אופקי בקירות-
צומת T
1:25

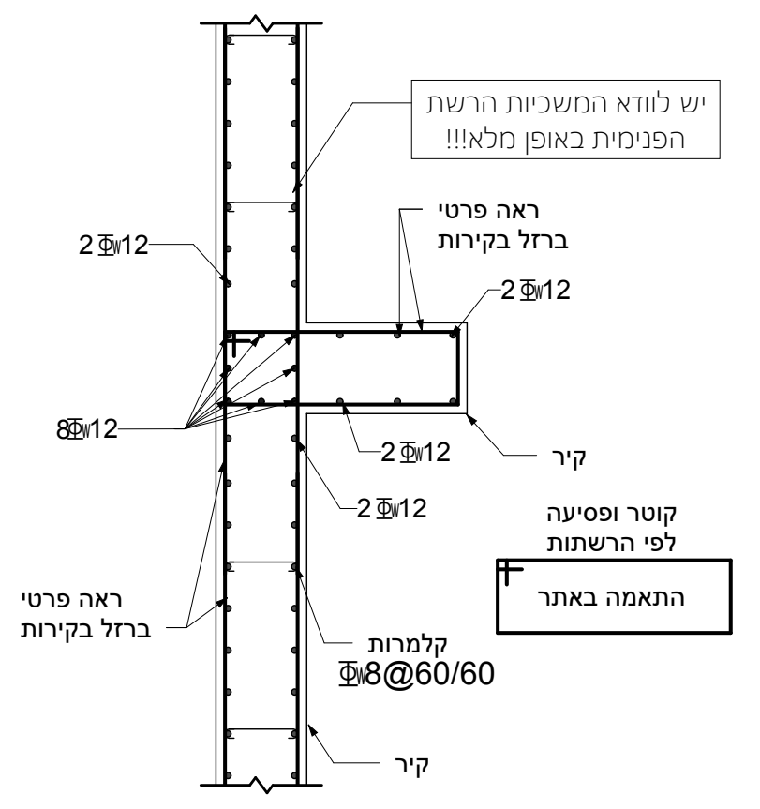

פרט חיבור A
פרט חיבור בין קורות ללא עמוד תומך
1:25

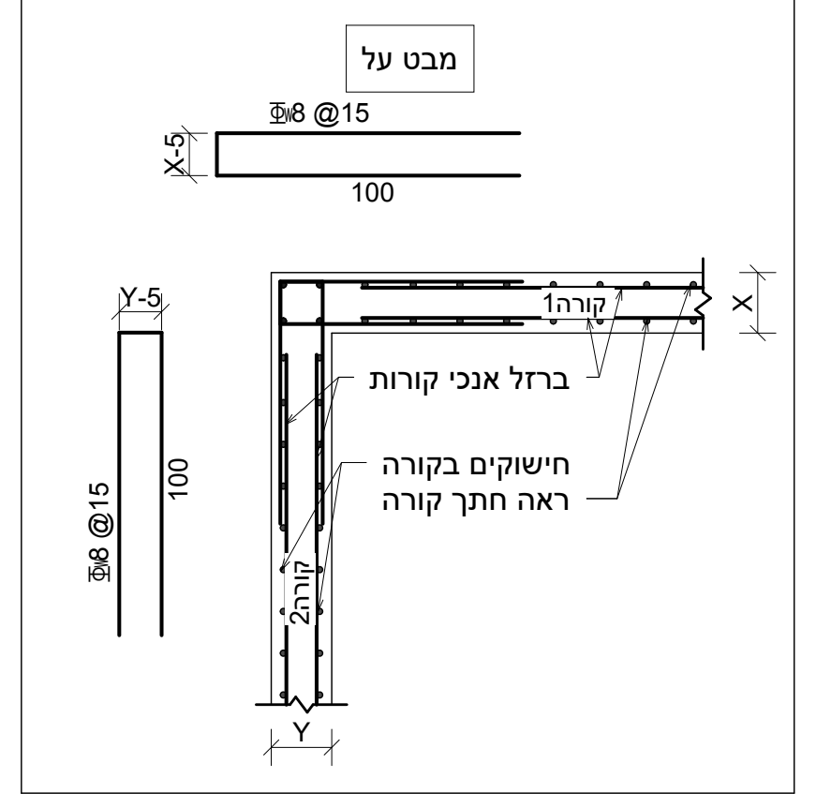

פרט חיבור B
פרט חיבור בין קורה לקיר
1:25

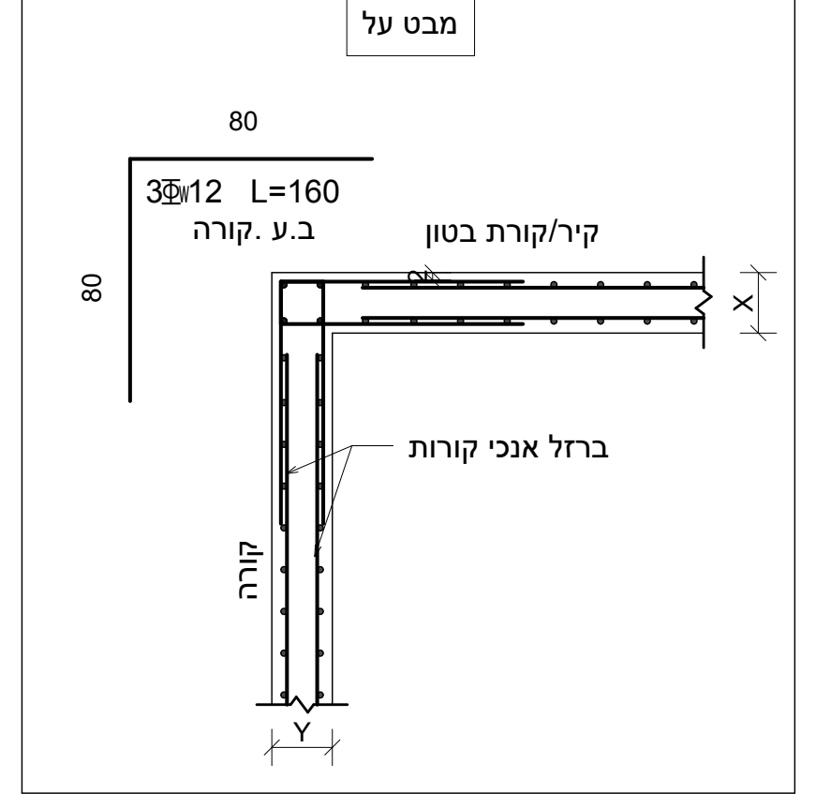

פרט קיר בטון
מעל קורות יסוד
1:25

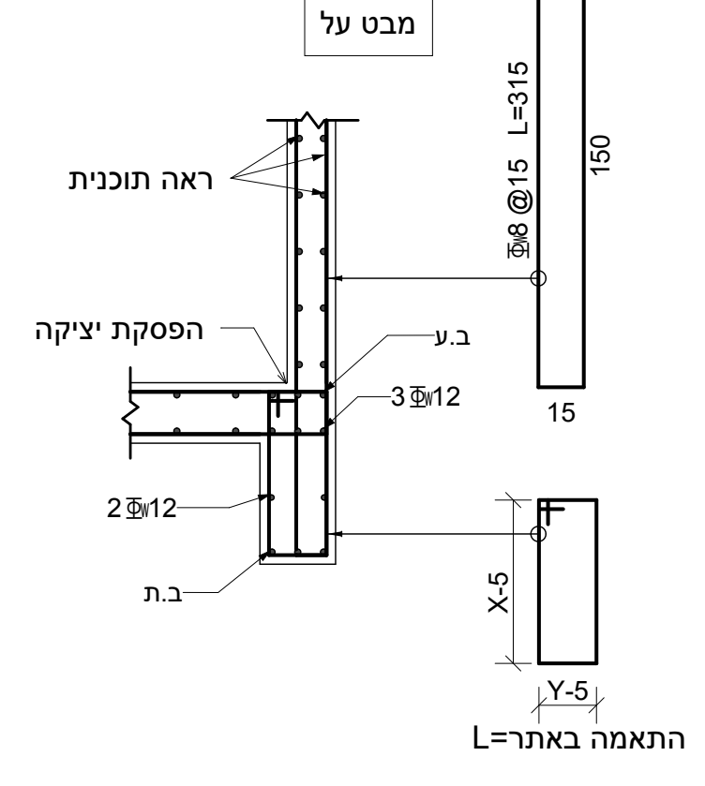

פרט טיפוסי לחיבור
קיר צומח מרצפת בטון
1:25

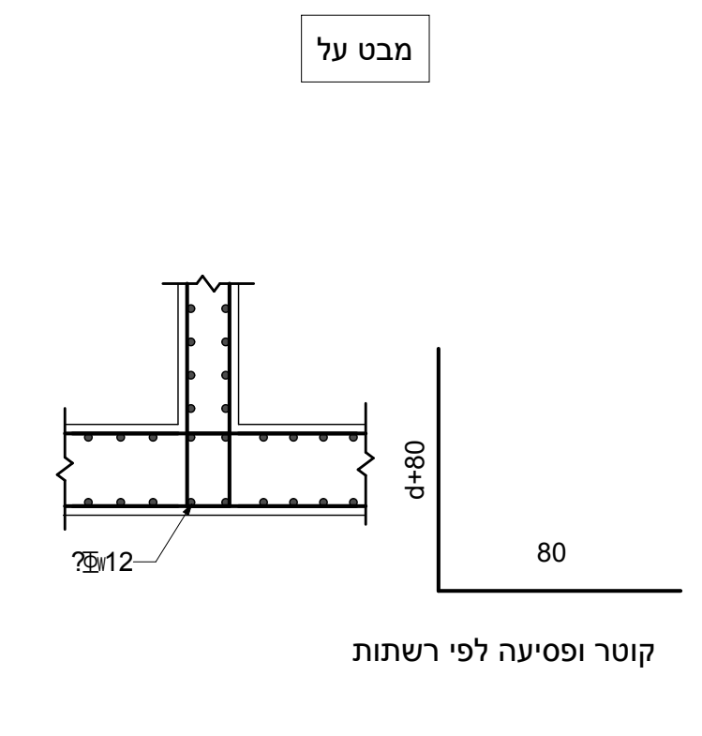

פרט חיזוק סביב שרוולים בקורה
פתח גדול עד30/30

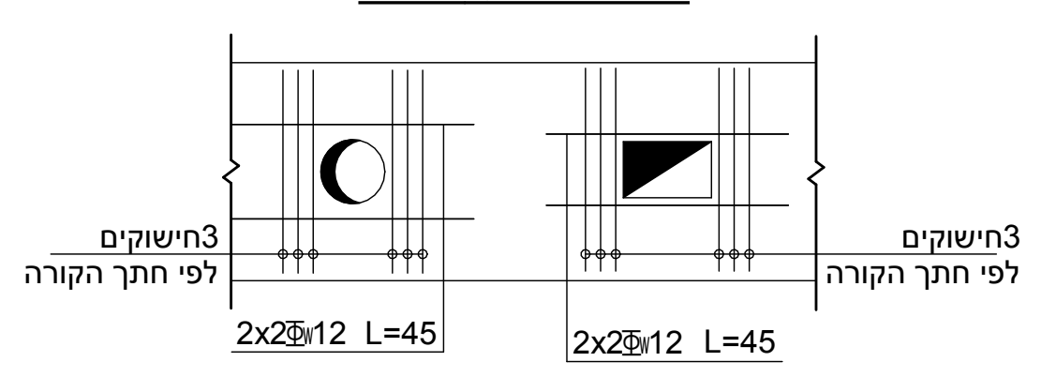

פרט חיזוק סביב קולטנים וצ.מ.ג.ים

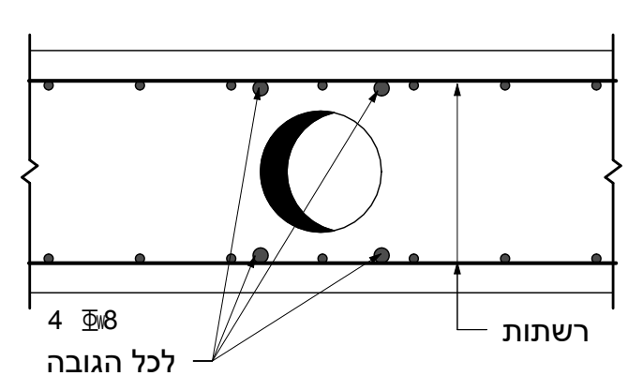

פרט עמוד טיפוסי
1:25

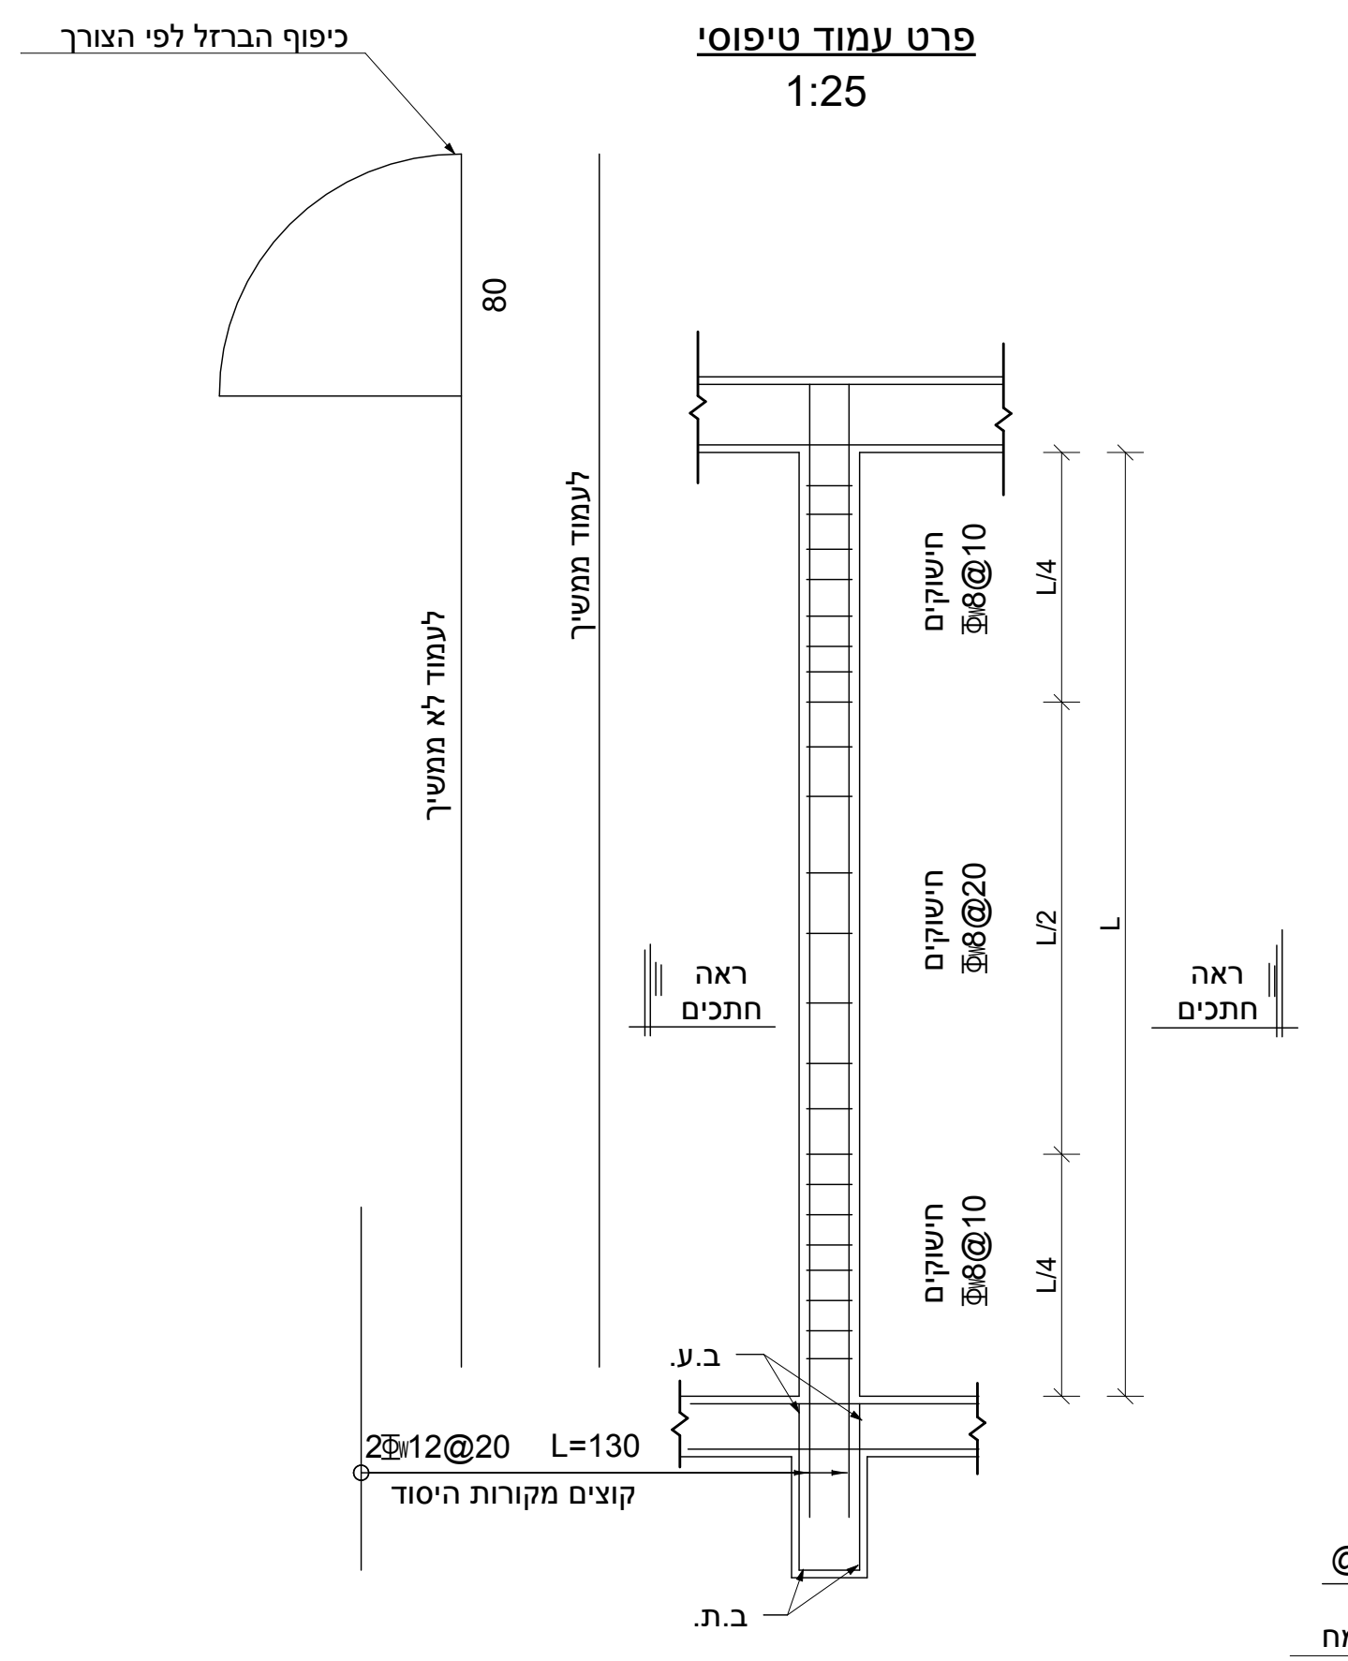

פרטים טיפוסיים לסיום קירות בטון

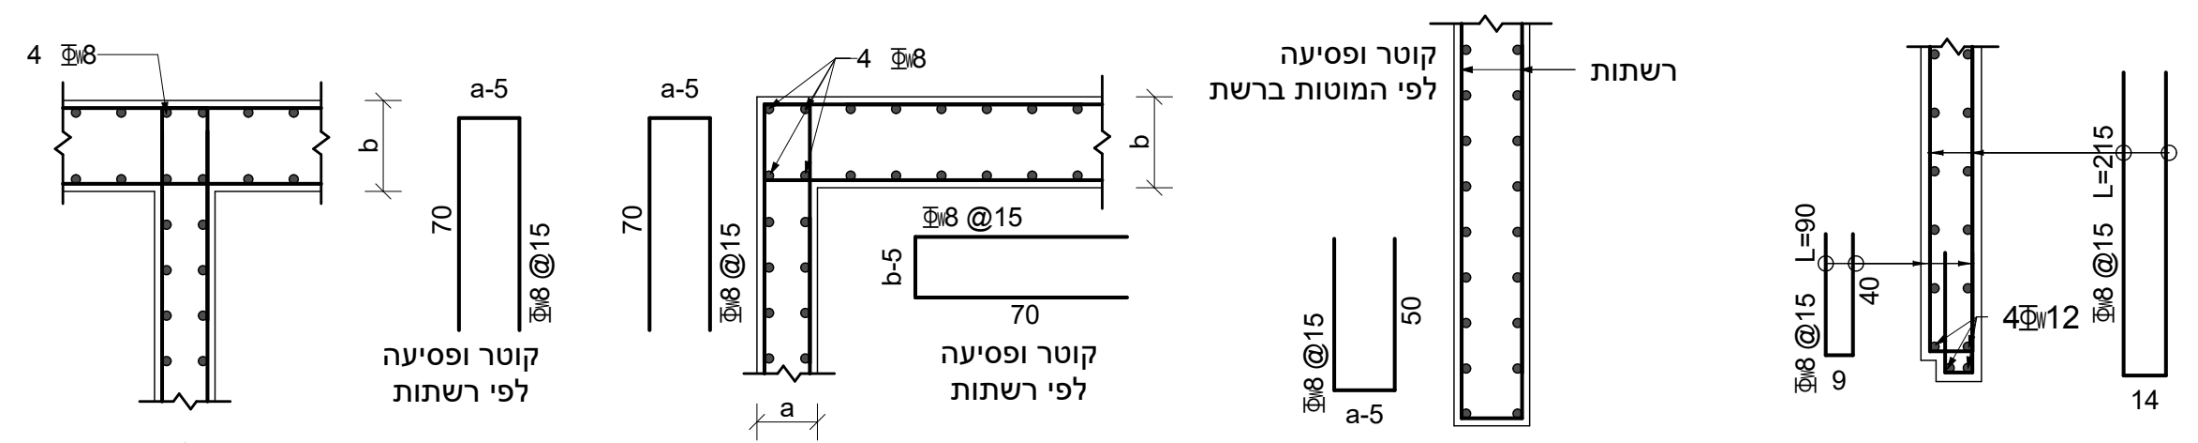

פרט המשכיות ברזל
לעמוד עולה

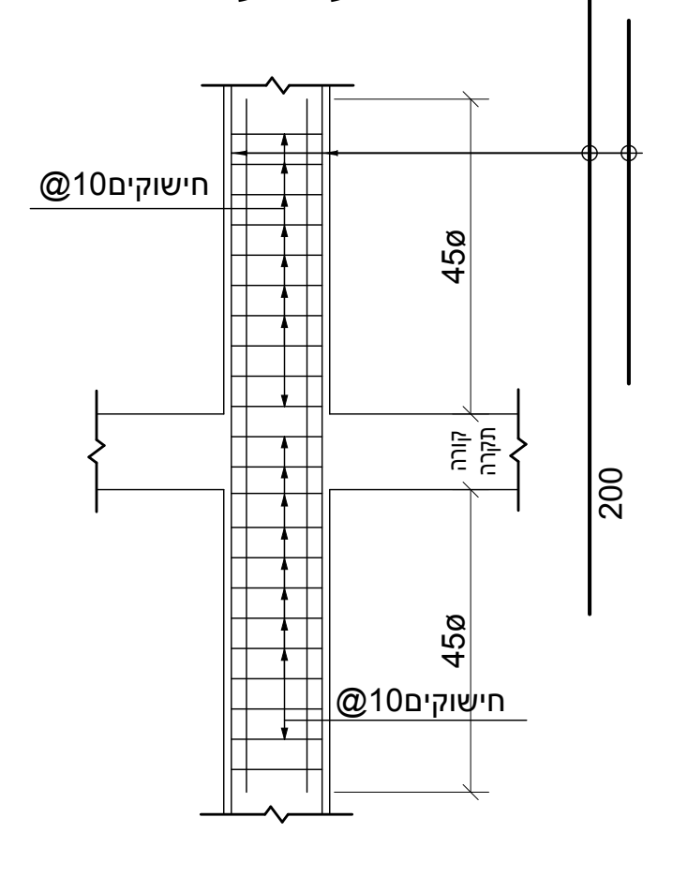

פרט המשכיות ברזל
לעמוד מוגדל

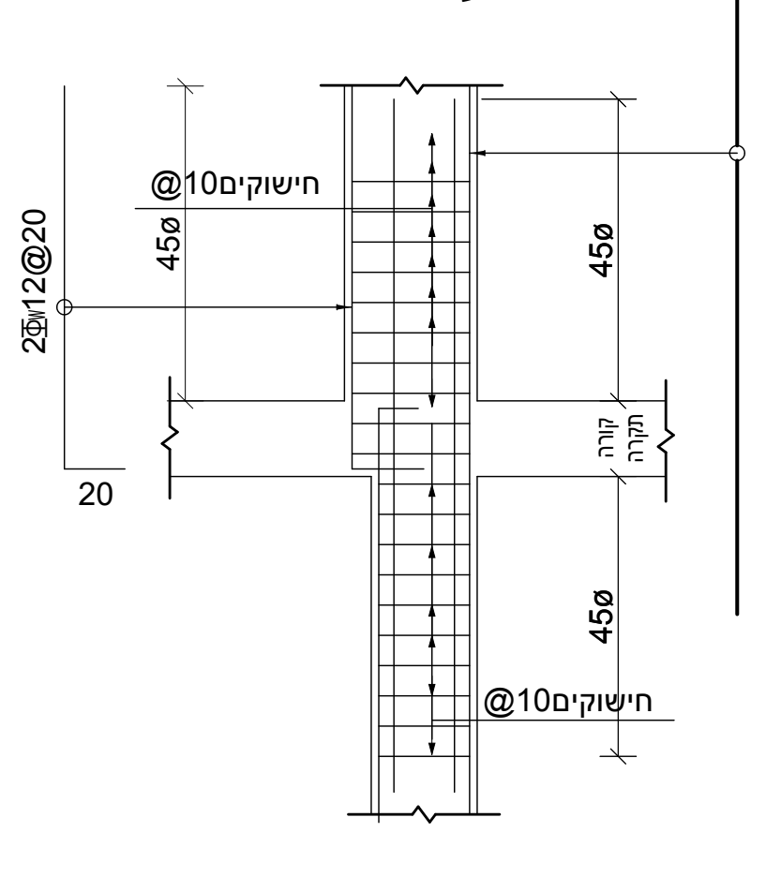

פרט המשכיות ברזל
לעמוד מוקטן

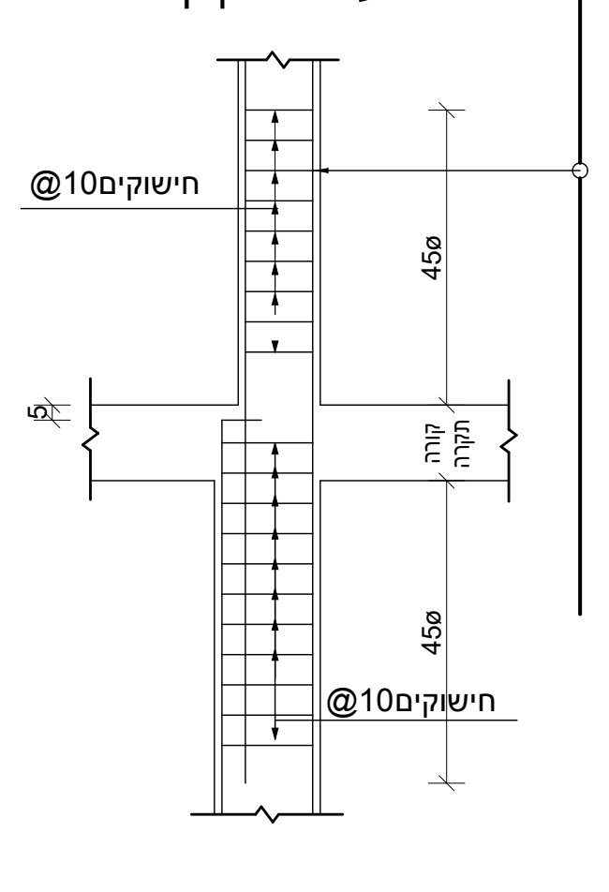

פרט להוצאת קוצים לעמודים

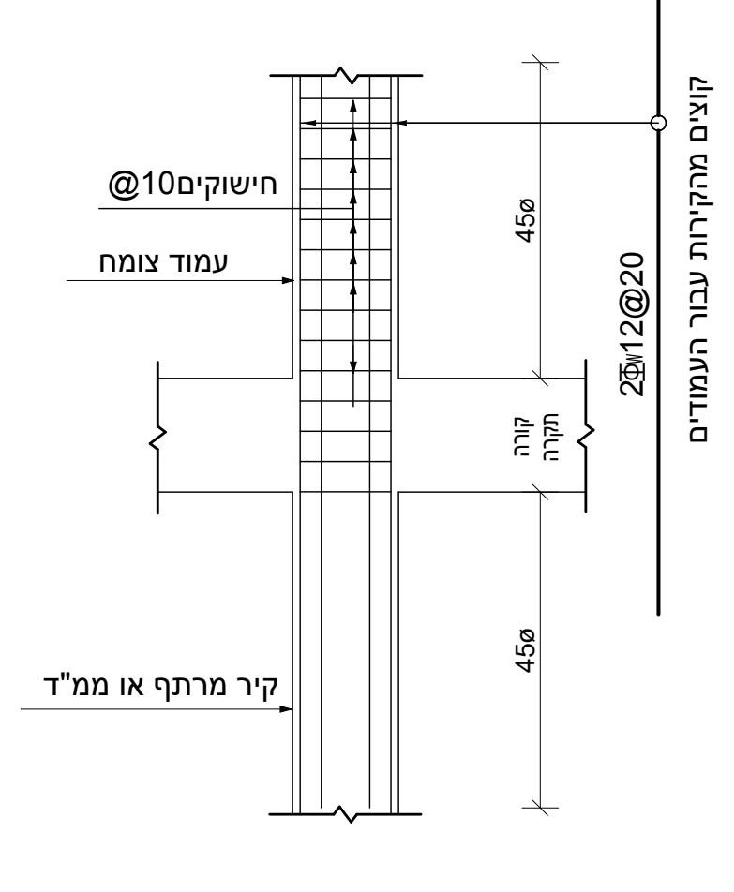

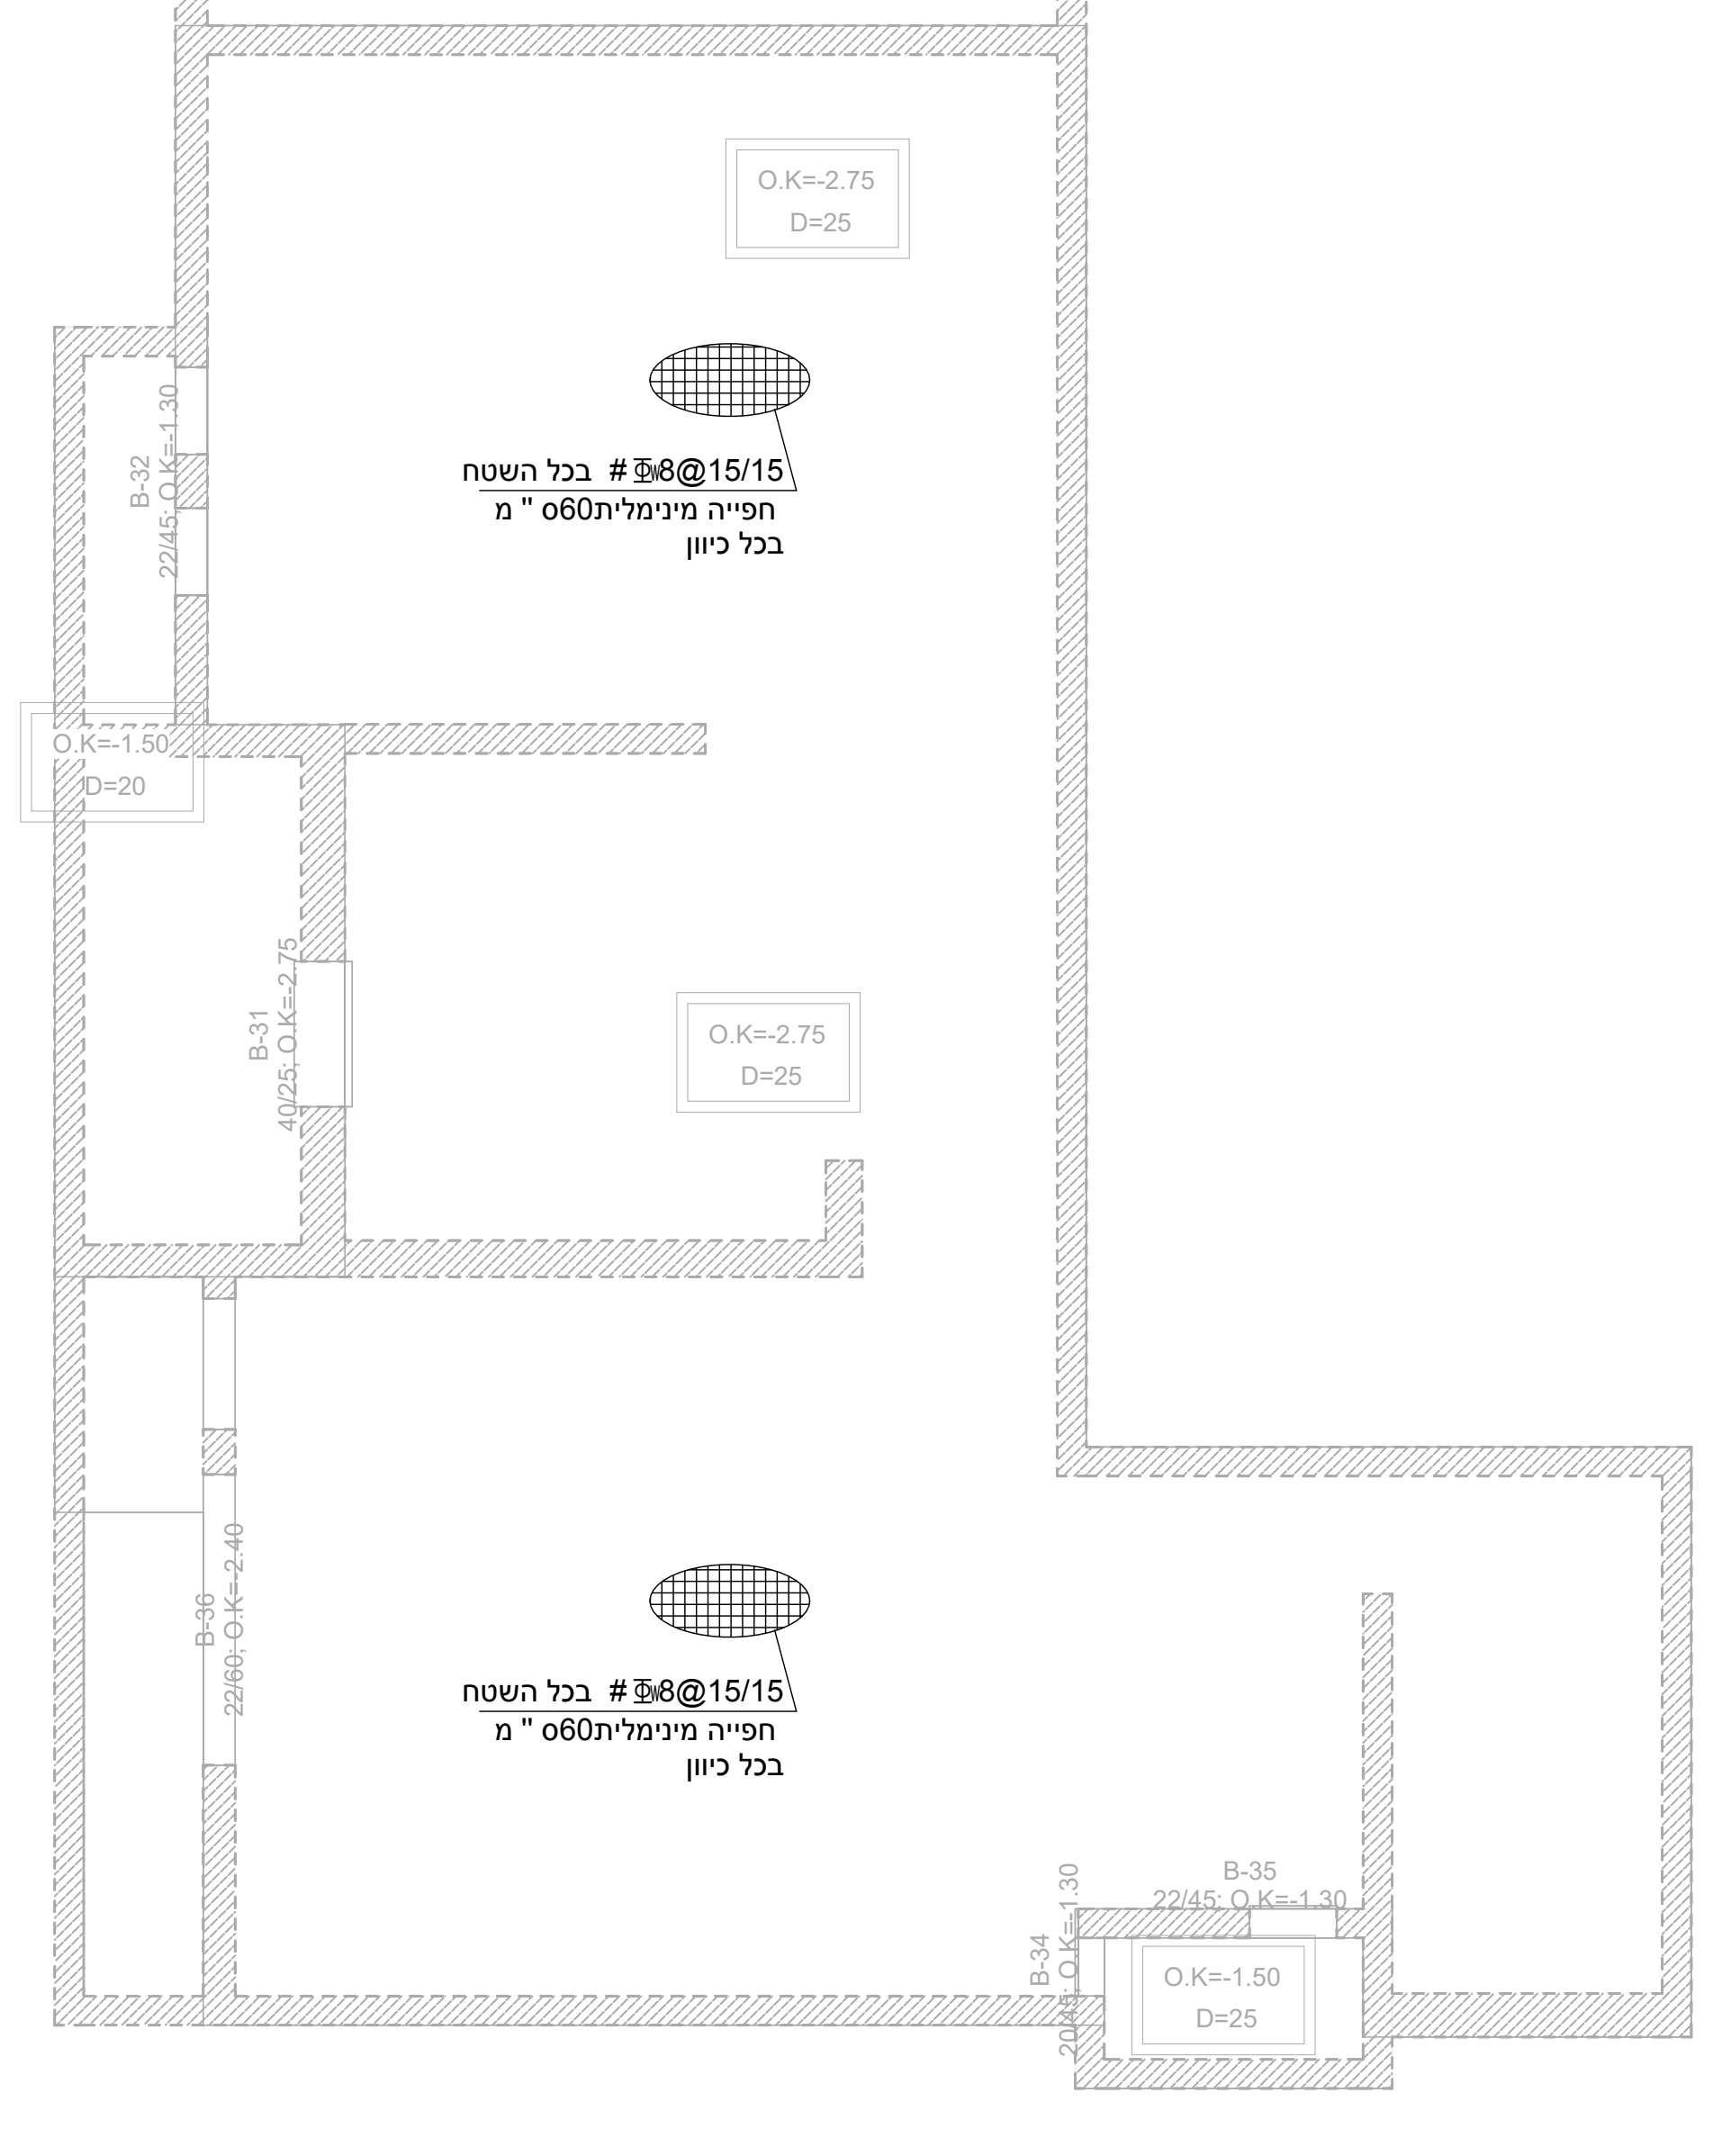

ברזל עליון
1 : 50

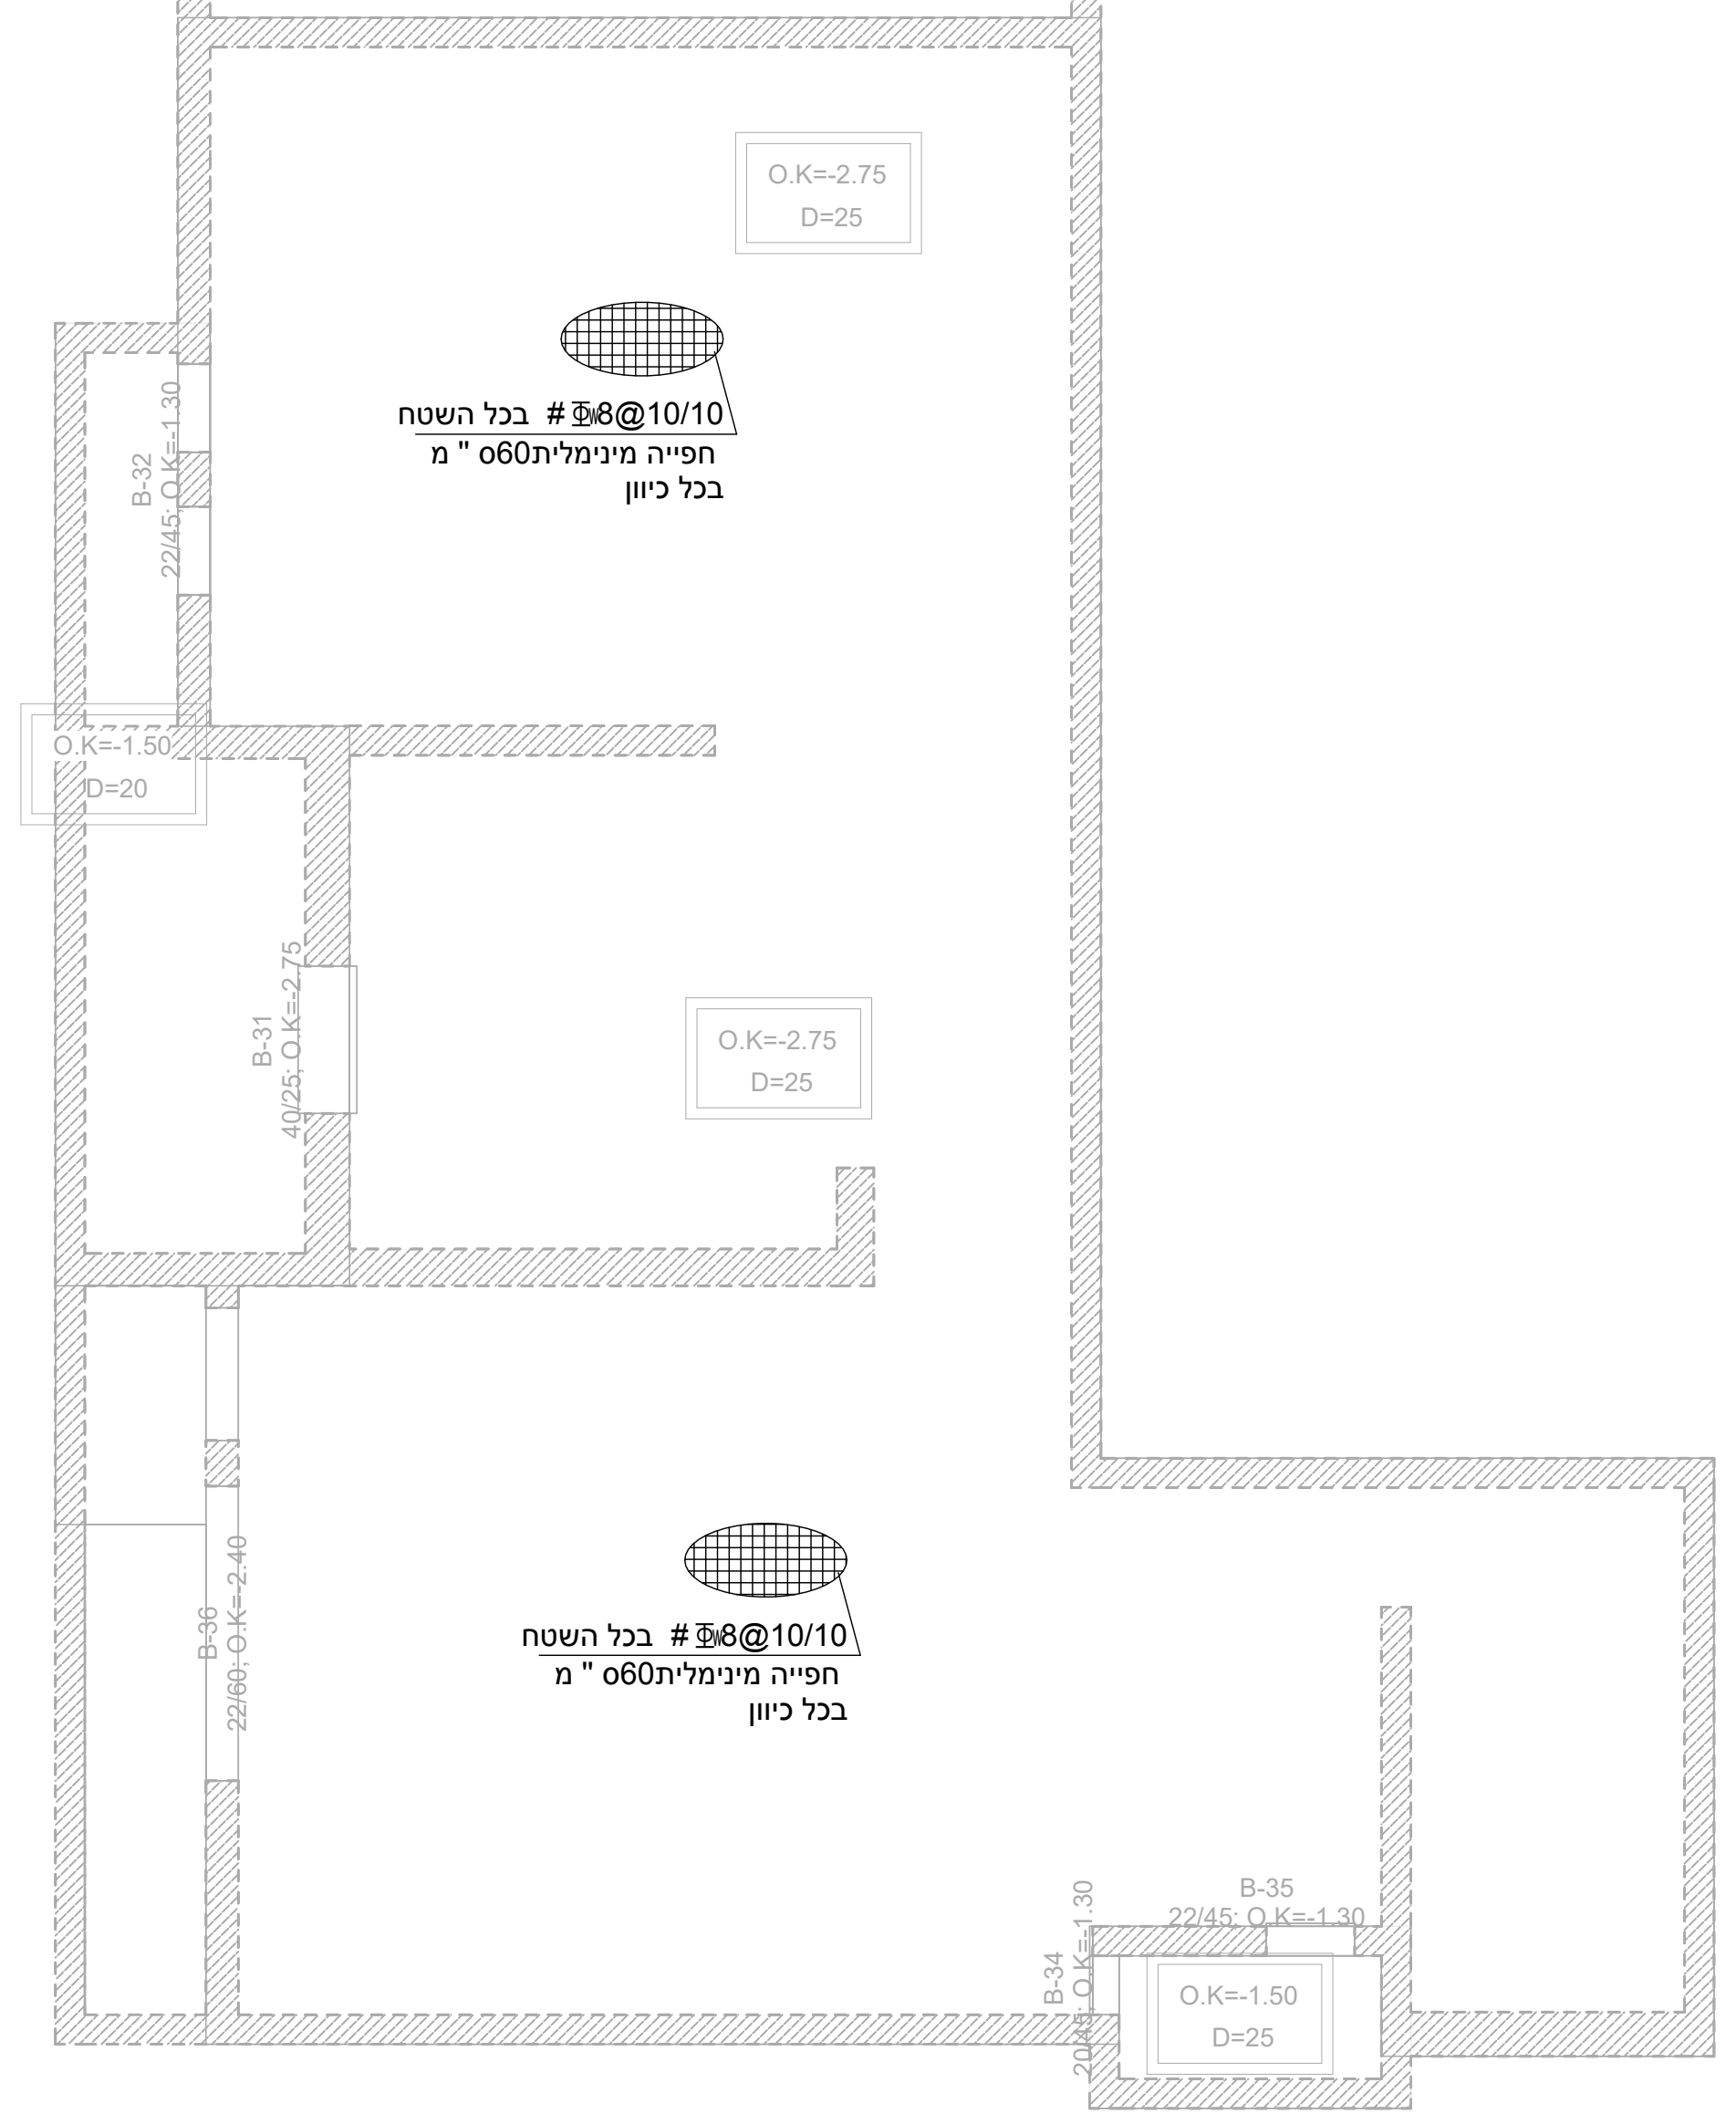

ברזל תחתון
1 : 50

פרט חפייה טיפוסי רשתות מרותכות
1:10

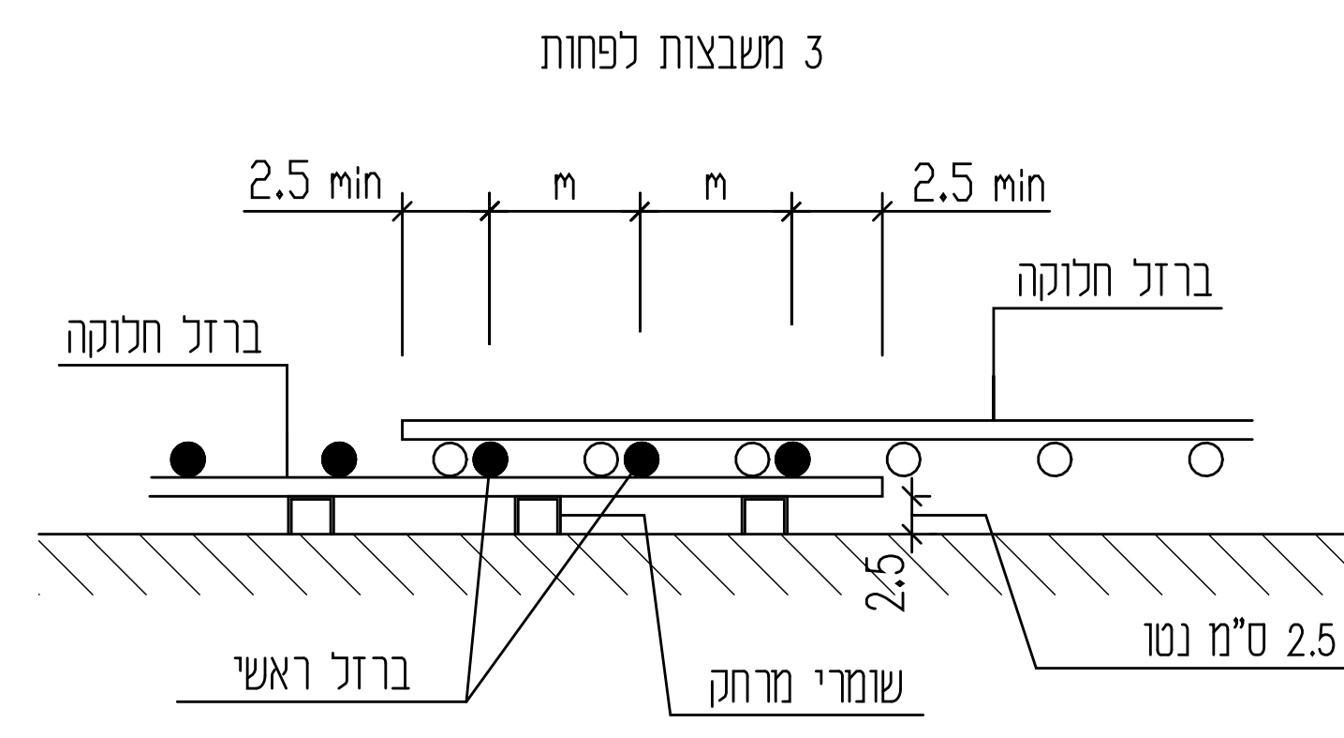

הערות

1. יש לקרוא תוכנית זו יחד עם תוכנית חשמל אינסטלציה ואיטום.
2. תכנית זאת מיועדת לביצוע רק במידה ומולאו שני תנאים בסיסיים:
   א .אישור האדריכל
   ב . התוכנית מתאימה להיתר הבניה)באישור המהנדס האחראי על הביצוע)
3. תוכנית זאת תבוצע רק לאחר חתימת האדריכל והמודד עליה המאשרים כי היא מתאימה להיתר בניה והתקנים מבחינת העמדת המבנים במגרש
4. מיקום המבנה ביחס למגרש יקבע ע" י המודד בהתאם לתוכנית העמדה של האדריכל.
5. עובי כיסוי הבטון יהיה2.5o " מ בכל האלמנטים מלבד אלה שבאים במגע עם הקרקע - שם עובי הכיסוי יהיה4o "מ.
6. הארקת יסוד -יש לעיין בתכנית יועץ חשמל.
7. אין להעביר צינורות בקוטר גדול מ-50מ "מ ללא אישור מהמהנדס המתכנן.
8. דוח קרקע הינו חלק בלתי נפרד מתכנית זו.
9. סוג בטון ב-30 דרגת חשיפה 3.
10. יש לבצע התאמה בין תכניות האדריכליות ושאר היועצים לבין תכנית זו - לפני ביצוע.
11. אין להעמיס את המרפסות הן לפני הבנייה , והן אחרי הבנייה בעומס הגדול מהמצויין בתכנית!
12. פירוק טפסות בכל שלב יהיה - אך ורק באישור בכתב ממתכנן הקונסטרוקציה.

▨ עמוד / קיר-צומח

▩ עמוד / קיר-מפסיק

*סוגי בטון ראה ברשימת כמויות

מס 'עידכון	מהות העידכון	ע"י	תאריך
P0	תוכניות לביצוע		5.10.26

עומסים

עומס קבוע נוסף 500 =ק"ג /מ"ר
עומס שימושי 150 =ק"ג /מ"ר
עומס מרפסות 350=ק"ג /מ"ר

גובה מפלס)אדריכלות): -2.60
מפלס פני בטון: -2.75

P0 מעודכן לתאריך: 5.10.26

לעיון	לאישור	למכרז	לביצוע
○	○	○	●

שם הפרויקט:
וילה ליאור ואביחי אטואן

תאור השרטוט:
קומת מרתף -פריסת ברזל

מס 'השרטוט:
K-13

מס 'פרויקט: WORK-167
קנ"מ:
דוא" ל: tal@yarin-eng.co.il
גודל גליון: 1356 X 900
מהנדס אחראי: טל שי אטיאס
מהנדס: רותם מאיר

YARIN
תכנון | ניהול | פיקוח מבנים
ירין הנדסה
טל אטיאס: 050-444-4730
tal@yarin-eng.co.il

01/11/2026 10:16:02
C:\Users\LENOVO P340\Desktop\עבודה\תוכניות קונסטרוקציה\work 167-\cons\ וילה ליאור ואביחי אטואן\תוכניות עבודה\ התחלתי.rvt