הערות

1. יש לקרוא תוכנית זו יחד עם תוכנית חשמל אינסטלציה ואיטום.
2. תכנית זאת מיועדת לביצוע רק במידה ומולאו שני תנאים בסיסיים:
   א .אישור האדריכל
   ב . התוכנית מתאימה להיתר הבניה)באישור המהנדס האחראי על הביצוע)
3. תוכנית זאת תבוצע רק לאחר חתימת האדריכל והמודד עליה המאשרים כי היא מתאימה להיתר בניה והתקנים מבחינת העמדת המבנים במגרש
4. מיקום המבנה ביחס למגרש יקבע ע" י המודד בהתאם לתוכנית העמדה של האדריכל.
5. עובי כיסוי הבטון יהיה2.5ס " מ בכל האלמנטים מלבד אלה שבאים במגע עם הקרקע - שם עובי הכיסוי יהיה4ס "מ.
6. הארקת יסוד -יש לעיין בתכנית יועץ חשמל.
7. אין להעביר צינורות בקוטר גדול מ-50מ "מ ללא אישור מהמהנדס המתכנן.
8. דוח קרקע הינו חלק בלתי נפרד מתכנית זו.
9. סוג בטון ב-30 דרגת חשיפה 3.
10. יש לבצע התאמה בין תכניות האדריכליות ושאר היועצים לבין תכנית זו - לפני ביצוע.
11. אין להעמיס את המרפסות הן לפני הבנייה , והן אחרי הבנייה בעומס הגדול מהמצויין בתכנית!
12. פירוק טפסות בכל שלב יהיה - אך ורק באישור בכתב ממתכנן הקונסטרוקציה.

▨ עמוד / קיר-צומח

■ עמוד / קיר-מפסיק

*סוגי בטון ראה ברשימת כמויות

תאריך	ע"י	מהות העידכון	מס 'עידכון
5.10.26		תוכניות לביצוע	P0

עומסים

עומס קבוע נוסף 200 =ק"ג /מ"ר

עומס שימושי 200 =ק"ג /מ"ר

עומס מרפסות -=ק"ג /מ"ר

גובה מפלס)אדריכלות): +6.9

מפלס פני בטון: +6.9

P0 מעודכן לתאריך: 5.10.26

לעיון	לאישור	למכרז	לביצוע
○	○	○	●

שם הפרויקט:

וילה ליאור ואביחי אטואן

תאור השרטוט:

קומה גג -פריסת ברזל

מס 'השרטוט:

K-43

מס 'פרויקט: WORK-167

קנ"מ:

דוא" ל: tal@yarin-eng.co.il

גודל גליון: 1624 X 900

מהנדס אחראי: טל שיי אטיאס

מהנדס: שירה גיל אסרף

ירין הנדסה
טל אטיאס: 050-444-4730
tal@yarin-eng.co.il

YARIN
תכנון | ניהול | פיקוח מבנים

01/11/2026 10:17:03
C:\Users\LENOVO P340\Desktop\עבודה\תוכניות עבודה\רותם\work\רויטל מודל רויטל\קובץ cons\פתיחת תיקייה רויטאביחי אטואן\167-התחלתי.rvt

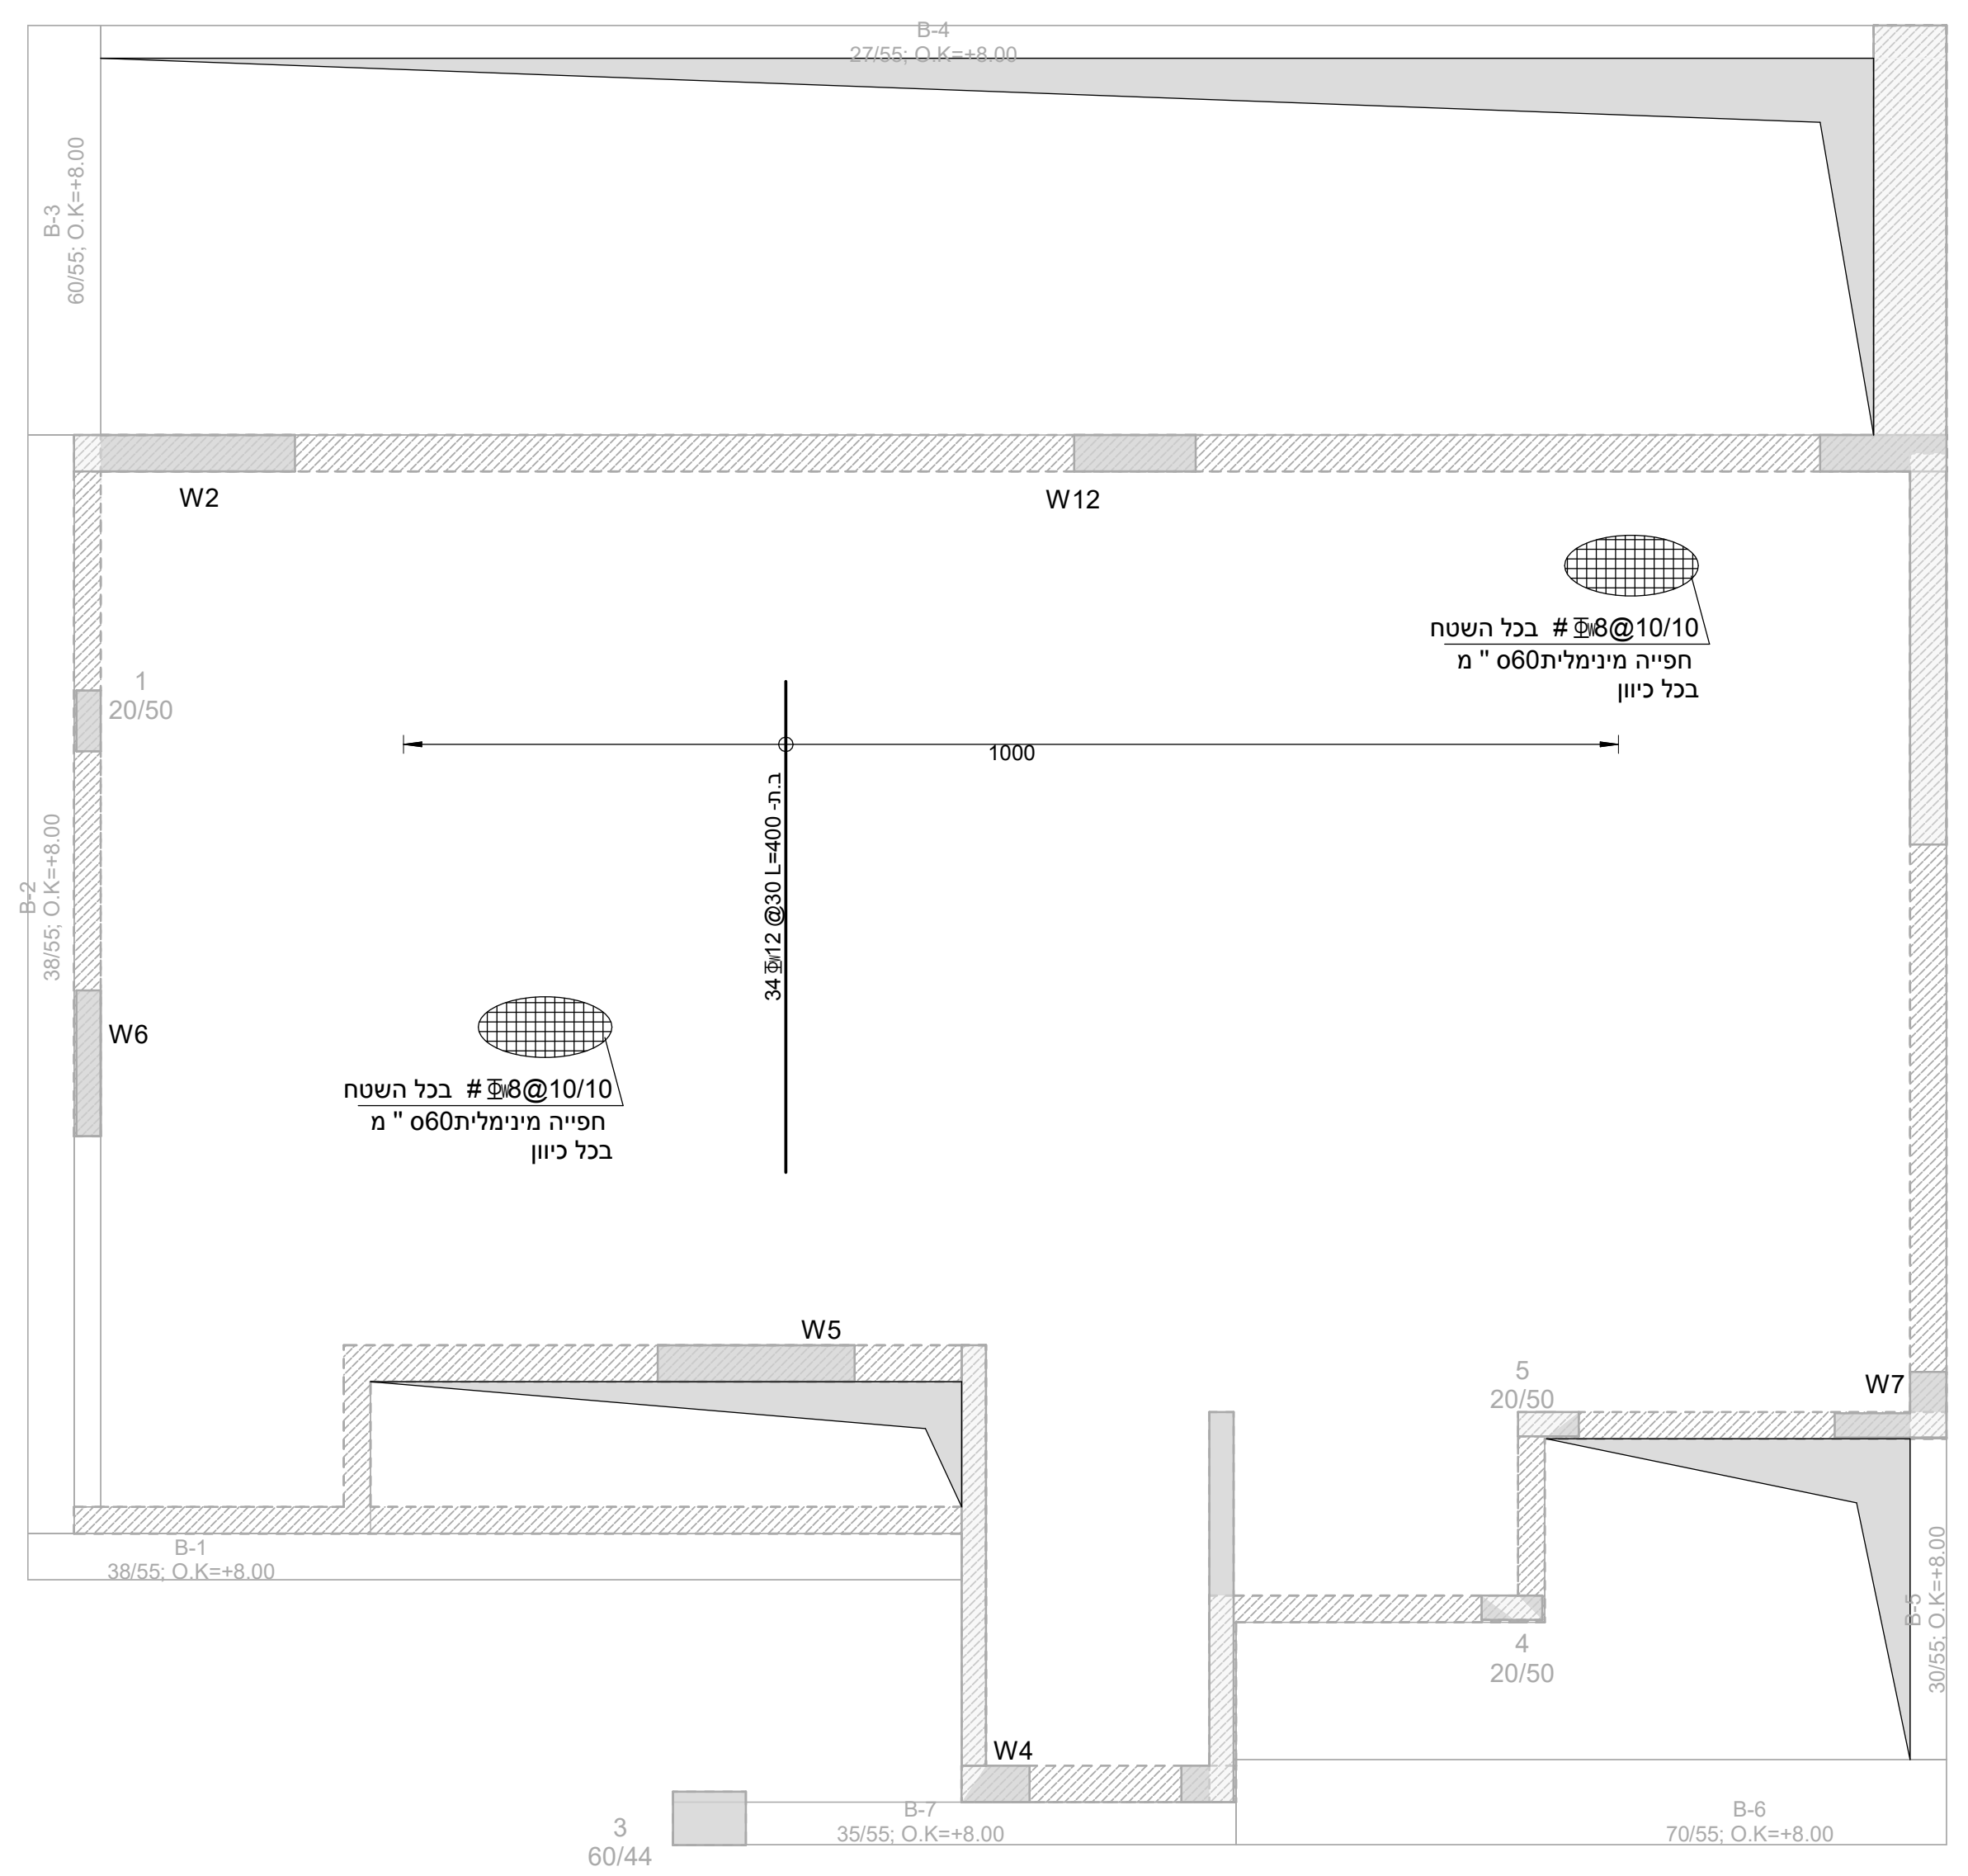
B-4
27/55; O.K=+8.00
B-3
60/55; O.K=+8.00
B-2
38/55; O.K=+8.00
W2
W12
W6
1
20/50
Φ8@10/10 # בכל השטח
חפייה מינימלית60ס " מ
בכל כיוון
1000
ב.ת- 34Φ12 @30 L=400
W5
W7
5
20/50
4
20/50
W4
B-1
38/55; O.K=+8.00
B-7
35/55; O.K=+8.00
B-6
70/55; O.K=+8.00
B-5
30/55; O.K=+8.00
3
60/44

ברזל תחתון

1 : 50

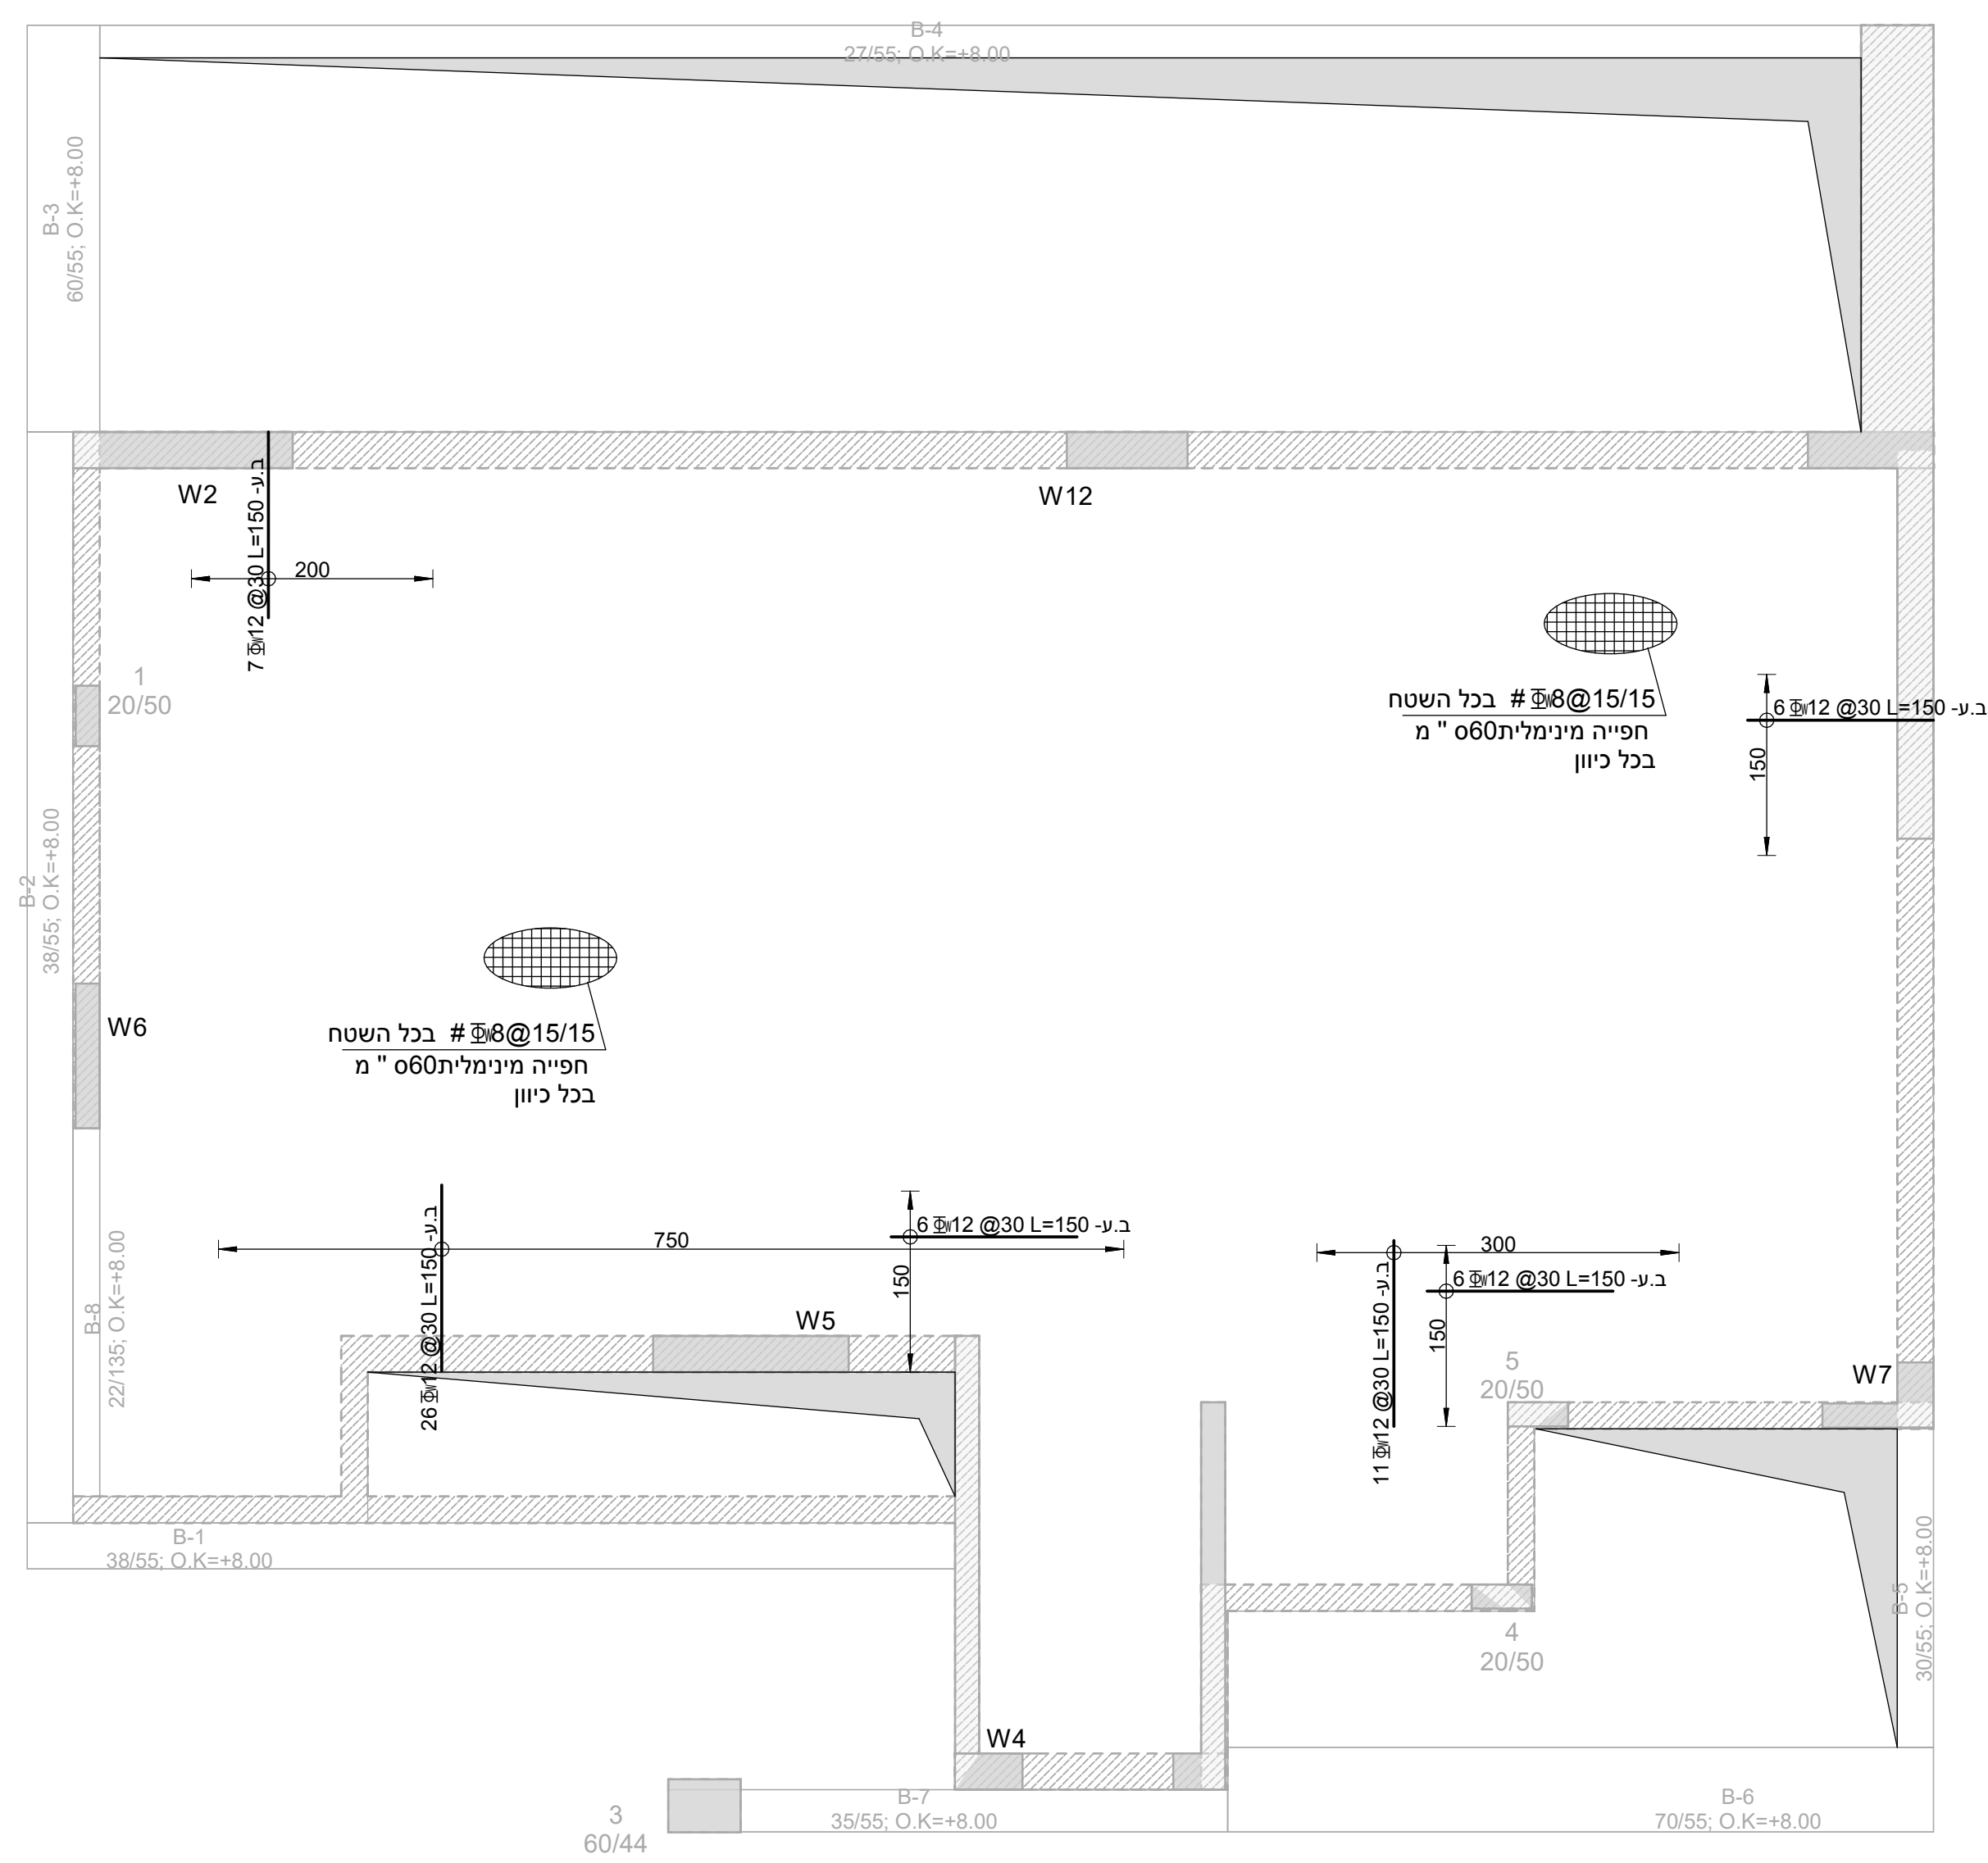
B-4
27/55; O.K=+8.00
B-3
60/55; O.K=+8.00
B-2
38/55; O.K=+8.00
B-8
22/135; O.K=+8.00
W2
W12
W6
1
20/50
200
ב.ע- 7Φ12 @30 L=150
Φ8@15/15 # בכל השטח
חפייה מינימלית60ס " מ
בכל כיוון
ב.ע- 6Φ12 @30 L=150
150
750
ב.ע- 26Φ12 @30 L=150
300
ב.ע- 11Φ12 @30 L=150
W5
W7
5
20/50
4
20/50
W4
B-1
38/55; O.K=+8.00
B-7
35/55; O.K=+8.00
B-6
70/55; O.K=+8.00
B-5
30/55; O.K=+8.00
3
60/44

ברזל עליון

1 : 50

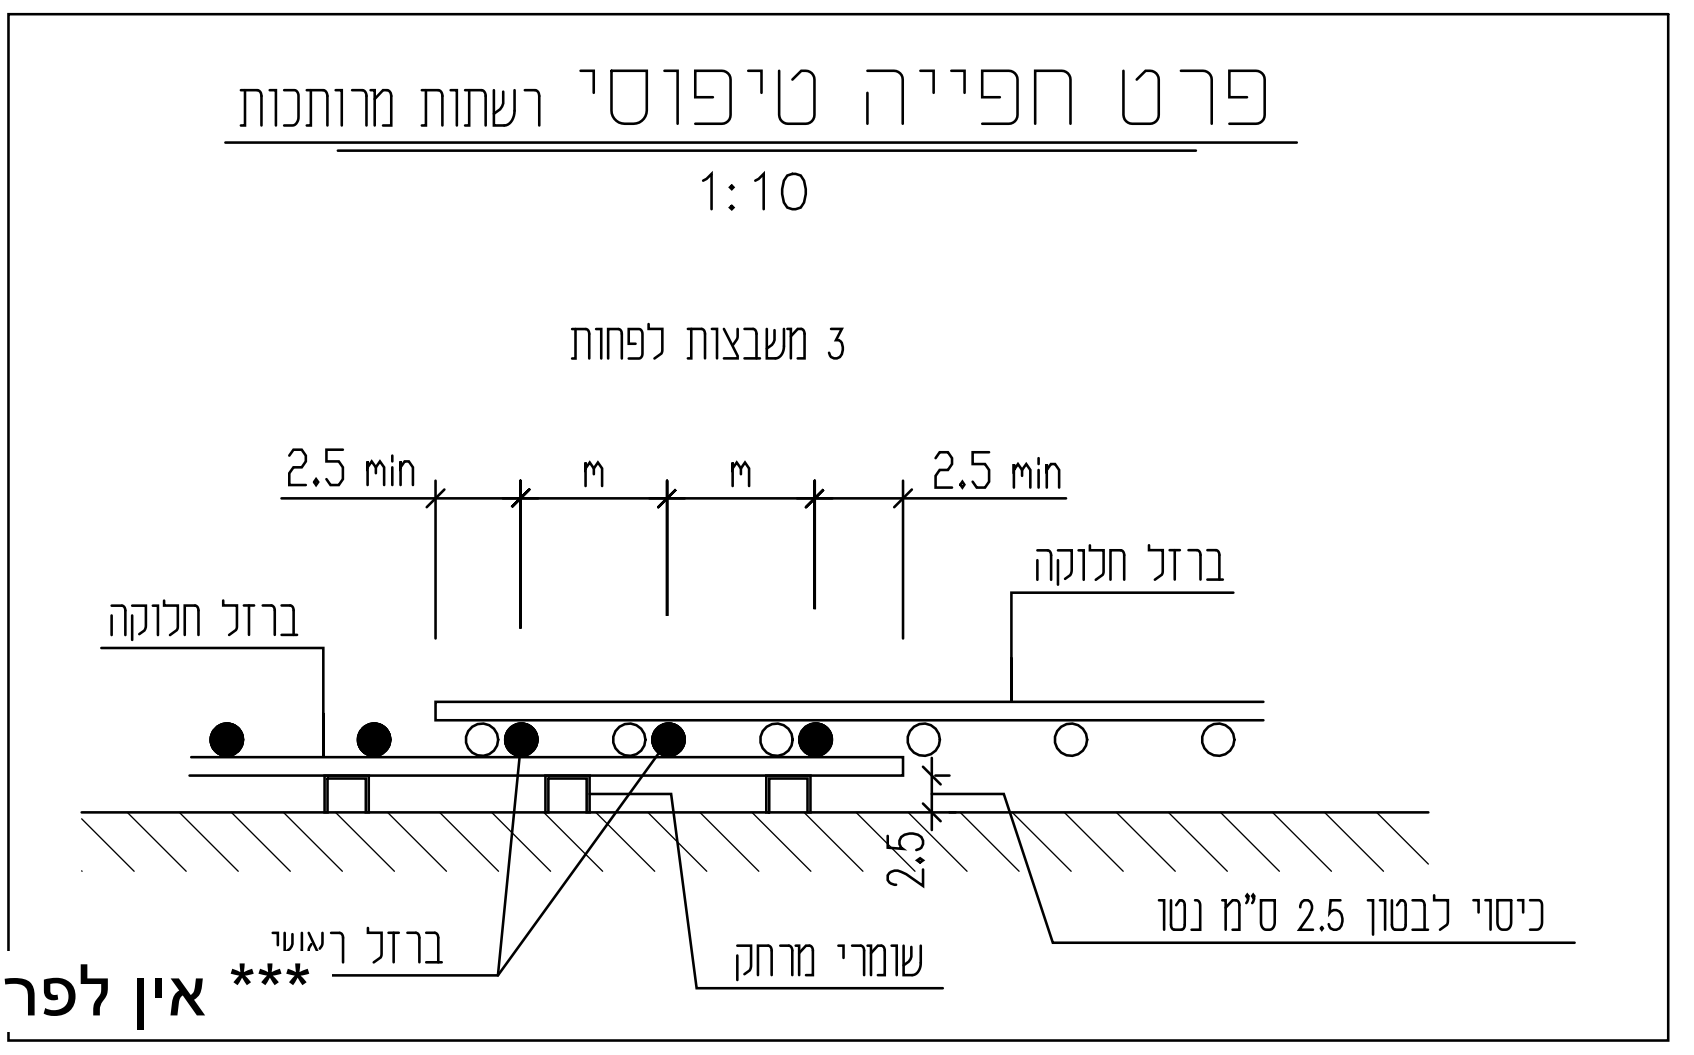

פרט חפייה טיפוסי רשתות מרותכות

1:10

3 משבצות לפחות
2.5 min
m
m
2.5 min
ברזל חלוקה
ברזל חלוקה
ברזל ראשי
שומרי מרחק
2.5
כיסוי לבטון 2.5 ס"מ נטו

*** אין לפרק תפסנות עד לקשיחות גג עליון- כולל***

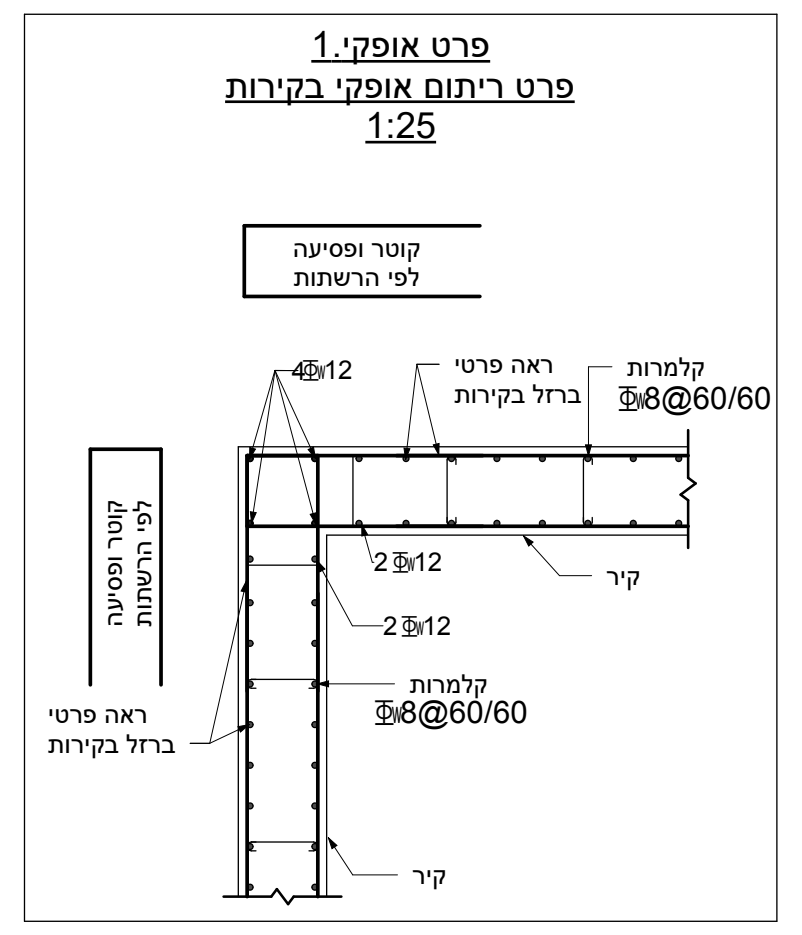

פרט אופקי.1
פרט ריתום אופקי בקירות
1:25

קוטר ופסיעה
לפי הרשתות
4Φ12
ראה פרטי
ברזל בקירות
קלמרות
Φ8@60/60
2Φ12
2Φ12
קיר

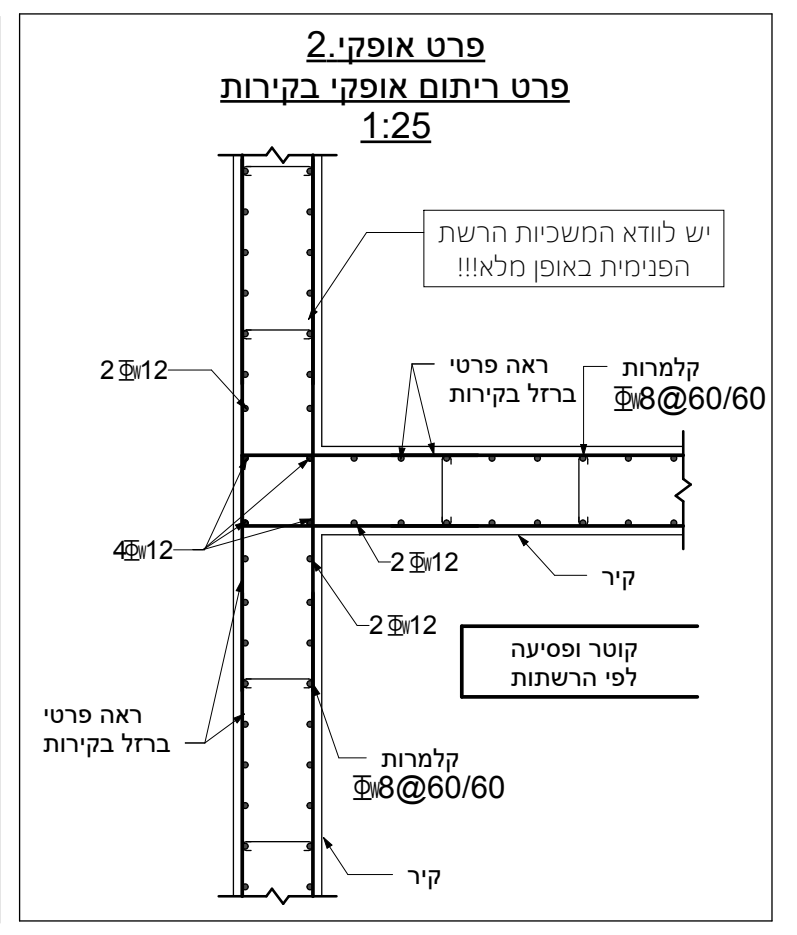

פרט אופקי.2
פרט ריתום אופקי בקירות
1:25

יש לוודא המשכיות הרשת
הפנימית באופן מלא!!!
2Φ12
4Φ12
ראה פרטי
ברזל בקירות
קלמרות
Φ8@60/60
קוטר ופסיעה
לפי הרשתות
קיר

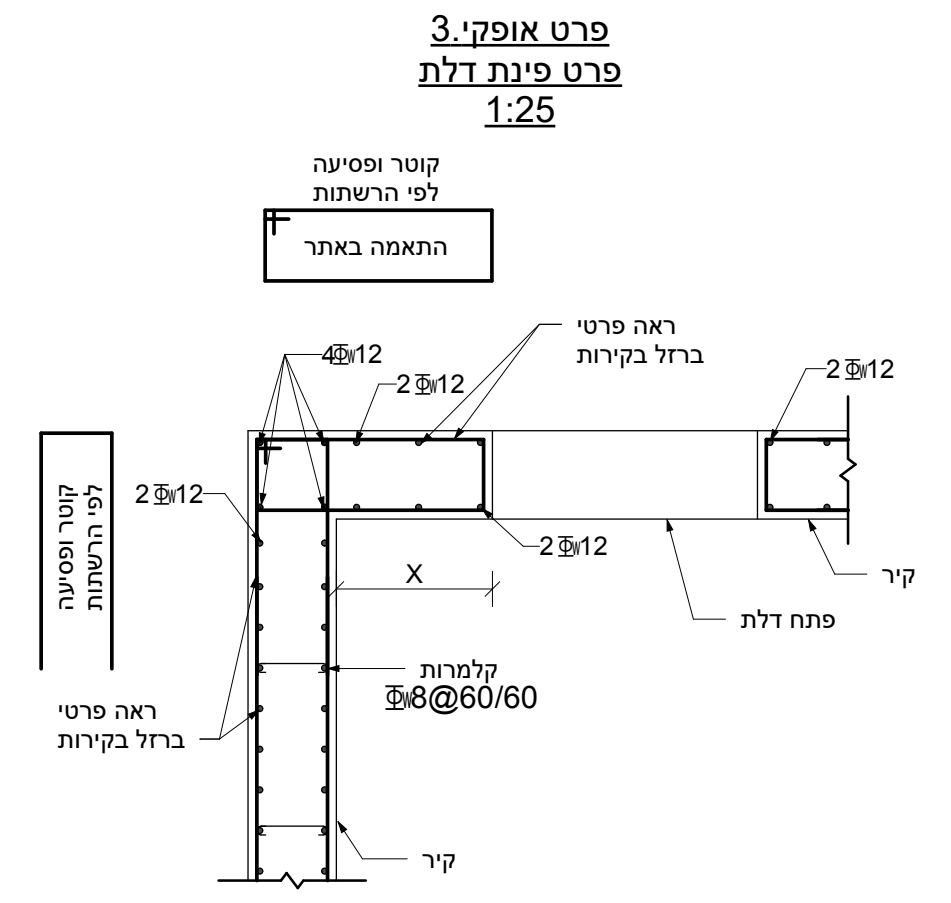

פרט אופקי.3
פרט פינת דלת
1:25

קוטר ופסיעה
לפי הרשתות
התאמה באתר
4Φ12
2Φ12
ראה פרטי
ברזל בקירות
X
קלמרות
Φ8@60/60
פתח דלת
קיר

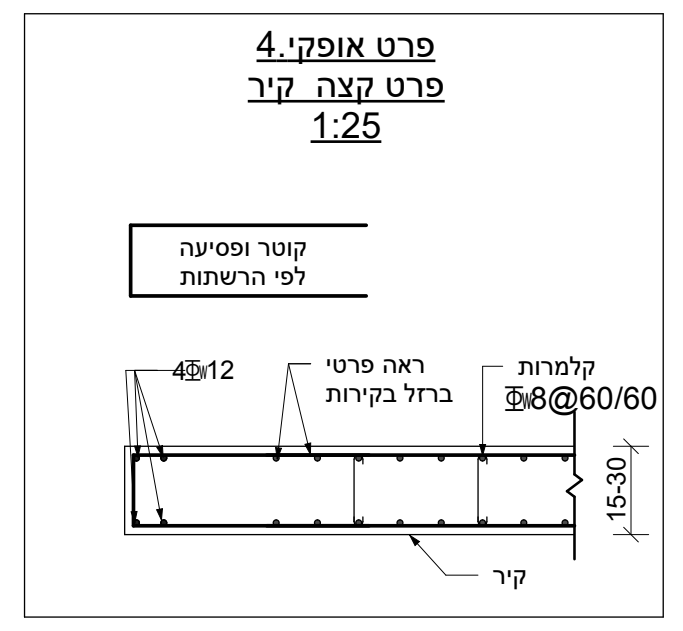

פרט אופקי.4
פרט קצה קיר
1:25

קוטר ופסיעה
לפי הרשתות
4Φ12
ראה פרטי
ברזל בקירות
קלמרות
Φ8@60/60
15-30
קיר

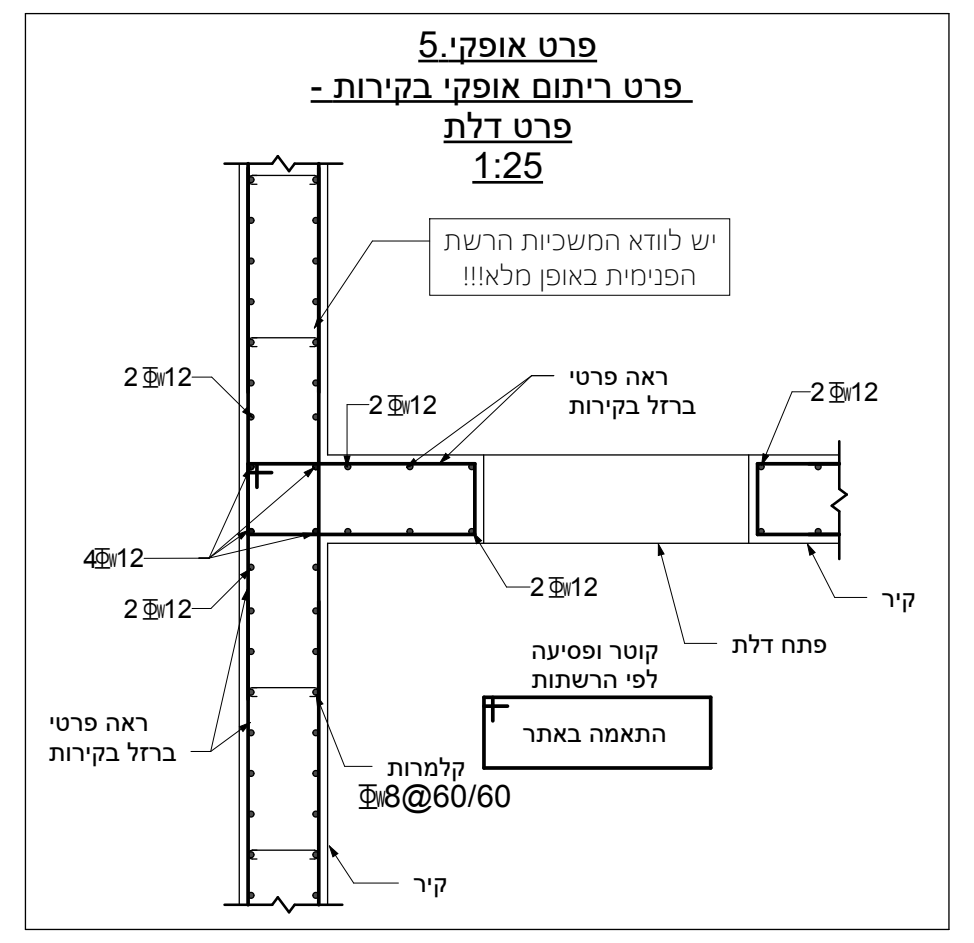

פרט אופקי.5
פרט ריתום אופקי בקירות -
פרט דלת
1:25

יש לוודא המשכיות הרשת
הפנימית באופן מלא!!!
2Φ12
4Φ12
ראה פרטי
ברזל בקירות
קוטר ופסיעה
לפי הרשתות
התאמה באתר
קלמרות
Φ8@60/60
פתח דלת
קיר

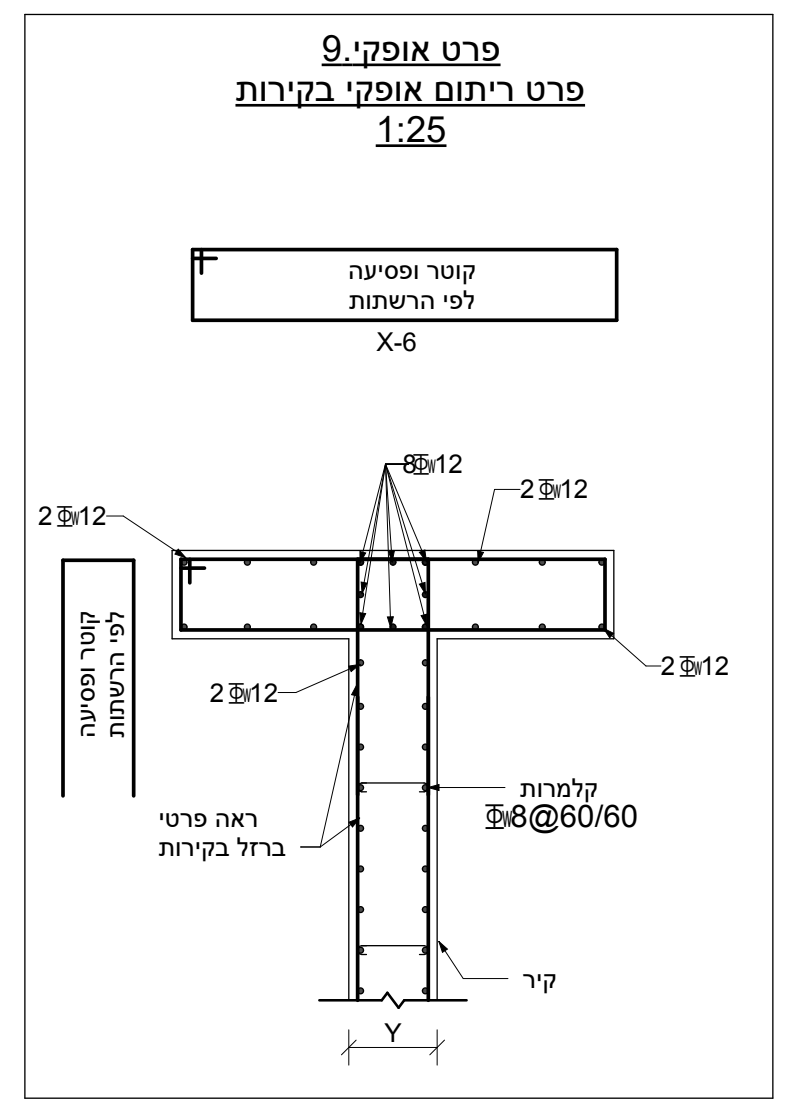

פרט אופקי.9
פרט ריתום אופקי בקירות
1:25

קוטר ופסיעה
לפי הרשתות
X-6
8Φ12
2Φ12
ראה פרטי
ברזל בקירות
קלמרות
Φ8@60/60
קיר
Y

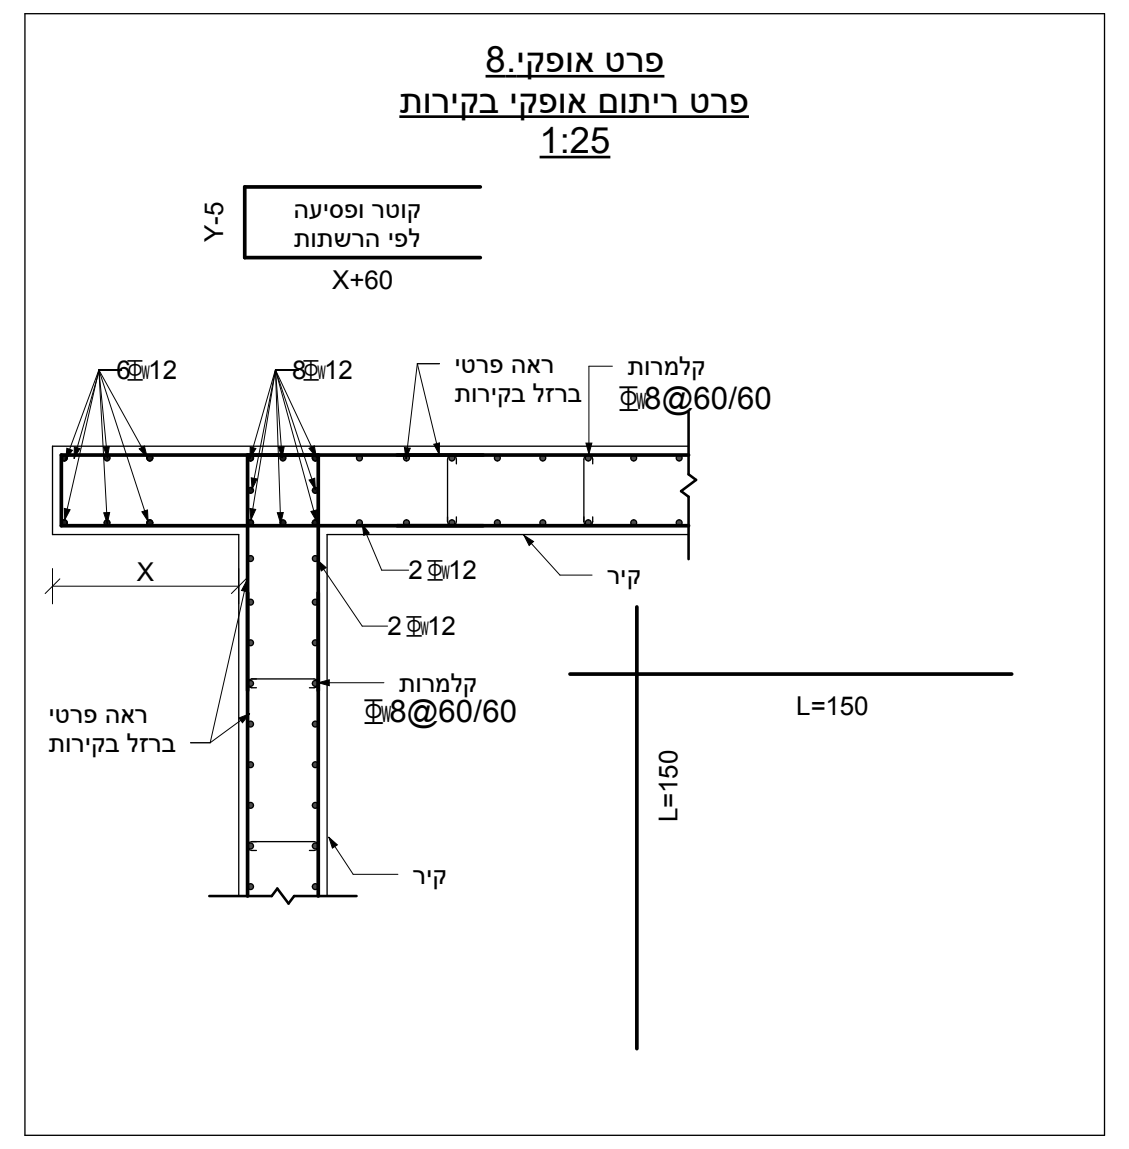

פרט אופקי.8
פרט ריתום אופקי בקירות
1:25

Y-5
קוטר ופסיעה
לפי הרשתות
X+60
6Φ12
8Φ12
ראה פרטי
ברזל בקירות
קלמרות
Φ8@60/60
2Φ12
X
L=150
L=150
קיר

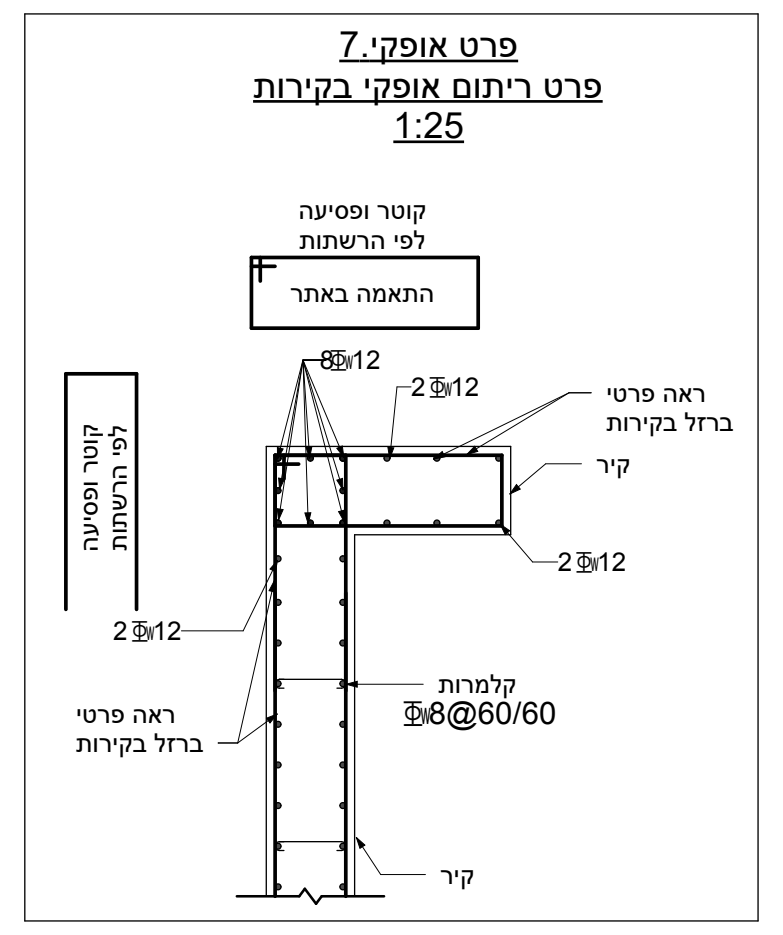

פרט אופקי.7
פרט ריתום אופקי בקירות
1:25

קוטר ופסיעה
לפי הרשתות
התאמה באתר
8Φ12
2Φ12
ראה פרטי
ברזל בקירות
קלמרות
Φ8@60/60
קיר

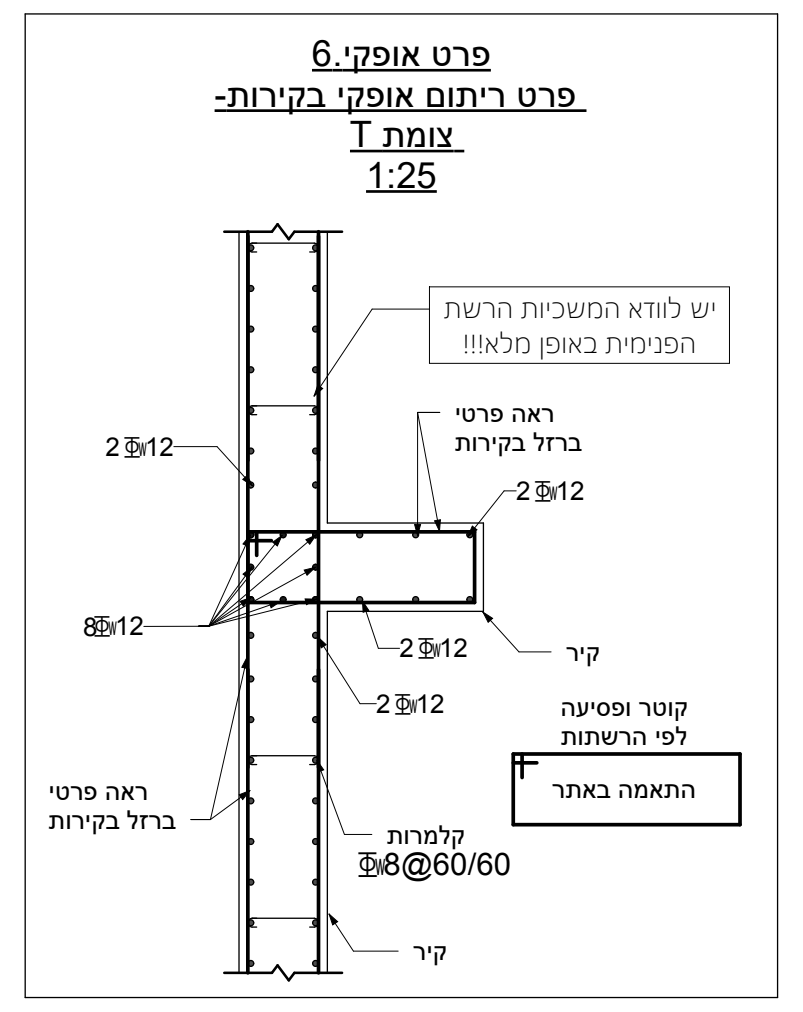

פרט אופקי.6
פרט ריתום אופקי בקירות-
צומת T
1:25

יש לוודא המשכיות הרשת
הפנימית באופן מלא!!!
2Φ12
8Φ12
ראה פרטי
ברזל בקירות
קוטר ופסיעה
לפי הרשתות
התאמה באתר
קלמרות
Φ8@60/60
קיר

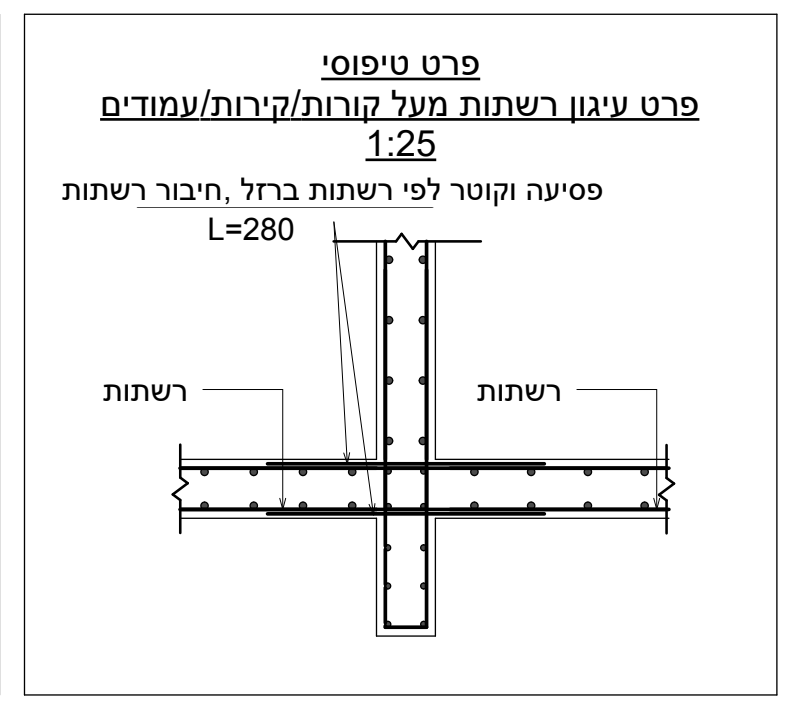

פרט טיפוסי
פרט עיגון רשתות מעל קורות/קירות/עמודים
1:25

פסיעה וקוטר לפי רשתות ברזל ,חיבור רשתות
L=280
רשתות
רשתות

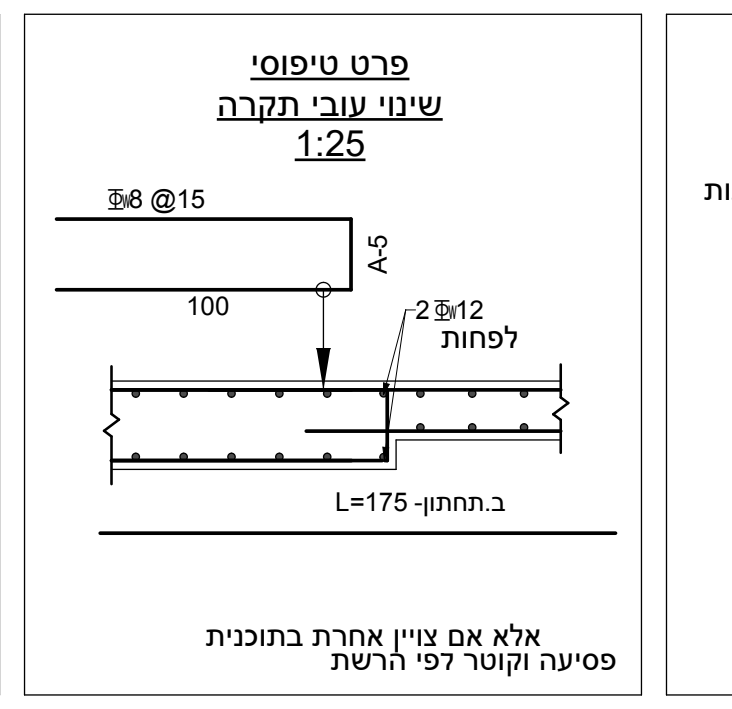

פרט טיפוסי
שינוי עובי תקרה
1:25

Φ8 @15
100
A-5
2Φ12
לפחות
ב.תחתון- L=175
אלא אם צויין אחרת בתוכנית
פסיעה וקוטר לפי הרשת

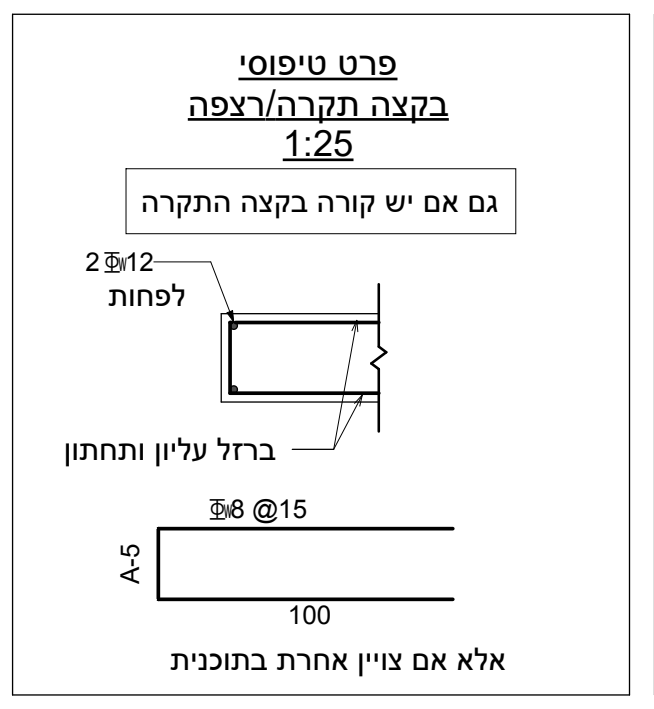

פרט טיפוסי
בקצה תקרה/רצפה
1:25

גם אם יש קורה בקצה התקרה
2Φ12
לפחות
ברזל עליון ותחתון
Φ8 @15
A-5
100
אלא אם צויין אחרת בתוכנית

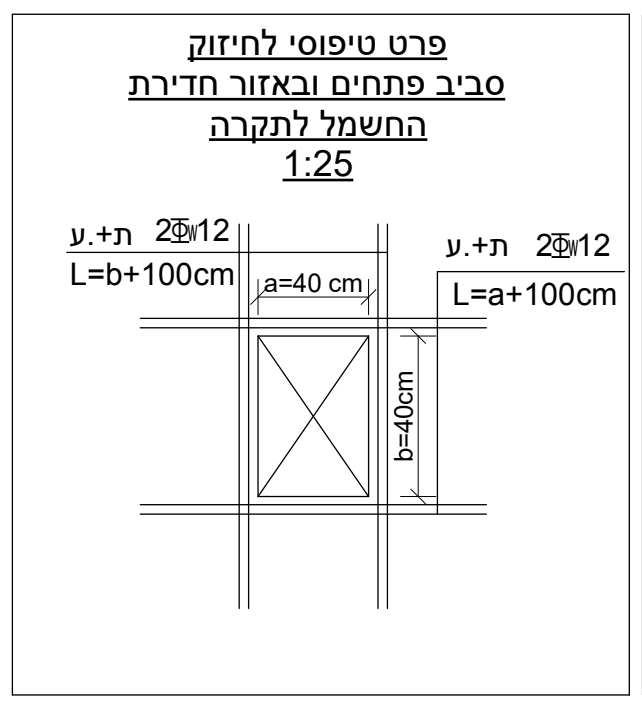

פרט טיפוסי לחיזוק
סביב פתחים ובאזור חדירת
החשמל לתקרה
1:25

ת+.ע 2Φ12
L=b+100cm
a=40 cm
ת+.ע 2Φ12
L=a+100cm
b=40cm

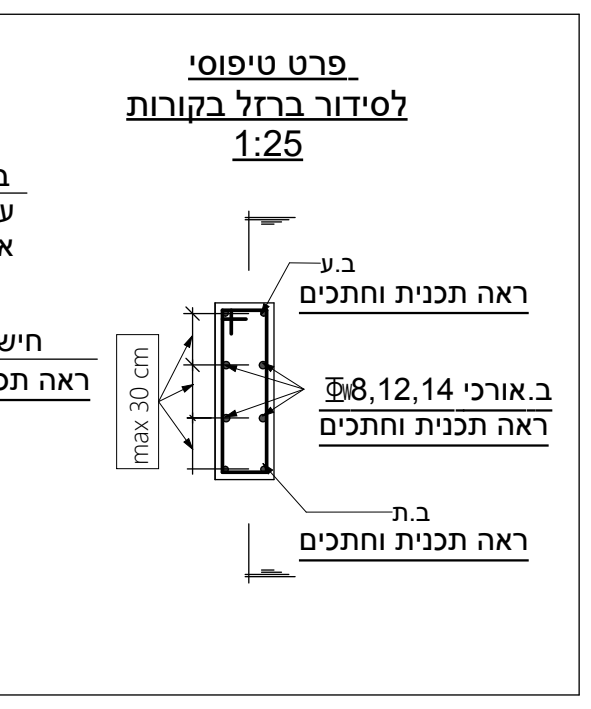

פרט טיפוסי
לסידור ברזל בקורות
1:25

ב.ע
ראה תכנית וחתכים
max 30 cm
Φ8,12,14 ב.אורכי
ראה תכנית וחתכים
ב.ת
ראה תכנית וחתכים

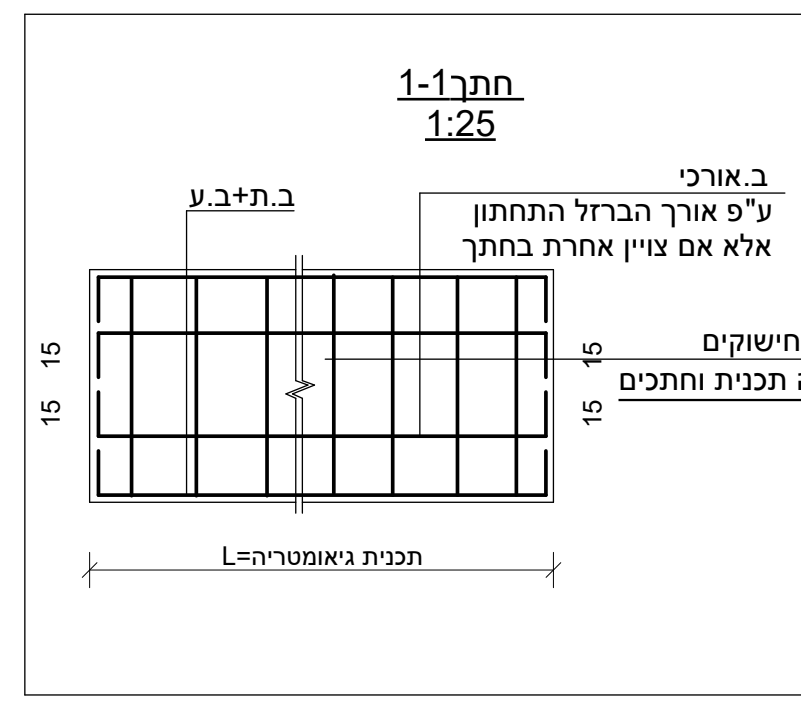

חתך1-1
1:25

ב.ת+ב.ע
ב.אורכי
ע"פ אורך הברזל התחתון
אלא אם צויין אחרת בחתך
חישוקים
ראה תכנית וחתכים
15
15
15
15
תכנית גיאומטריה=L

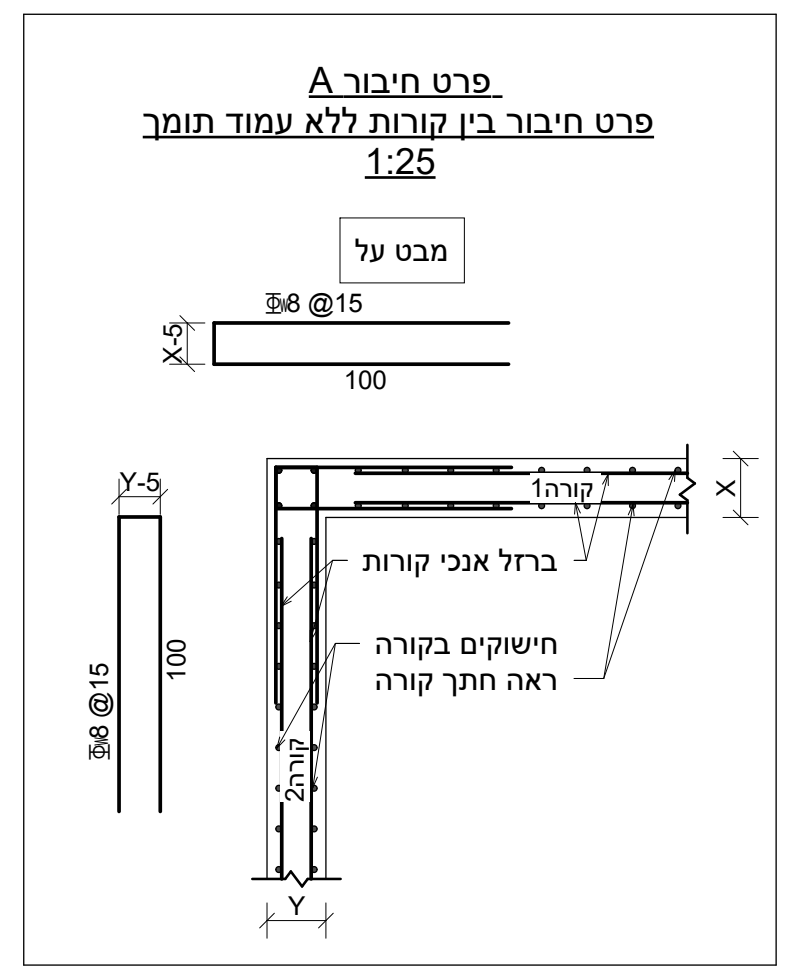

פרט חיבור A
פרט חיבור בין קורות ללא עמוד תומך
1:25

מבט על

Φ8 @15
X-5
100
Y-5
100
Φ8 @15
קורה1
קורה2
ברזל אנכי קורות
חישוקים בקורה
ראה חתך קורה
X
Y

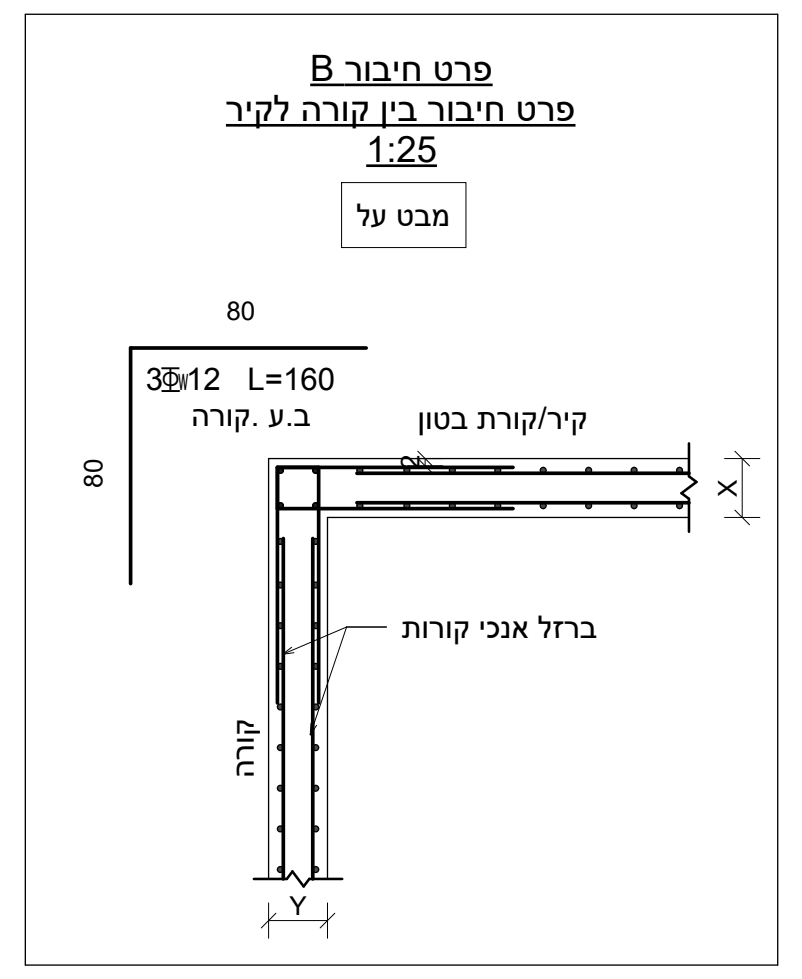

פרט חיבור B
פרט חיבור בין קורה לקיר
1:25

מבט על

80
3Φ12 L=160
ב.ע .קורה
80
קיר/קורת בטון
ברזל אנכי קורות
קורה
X
Y

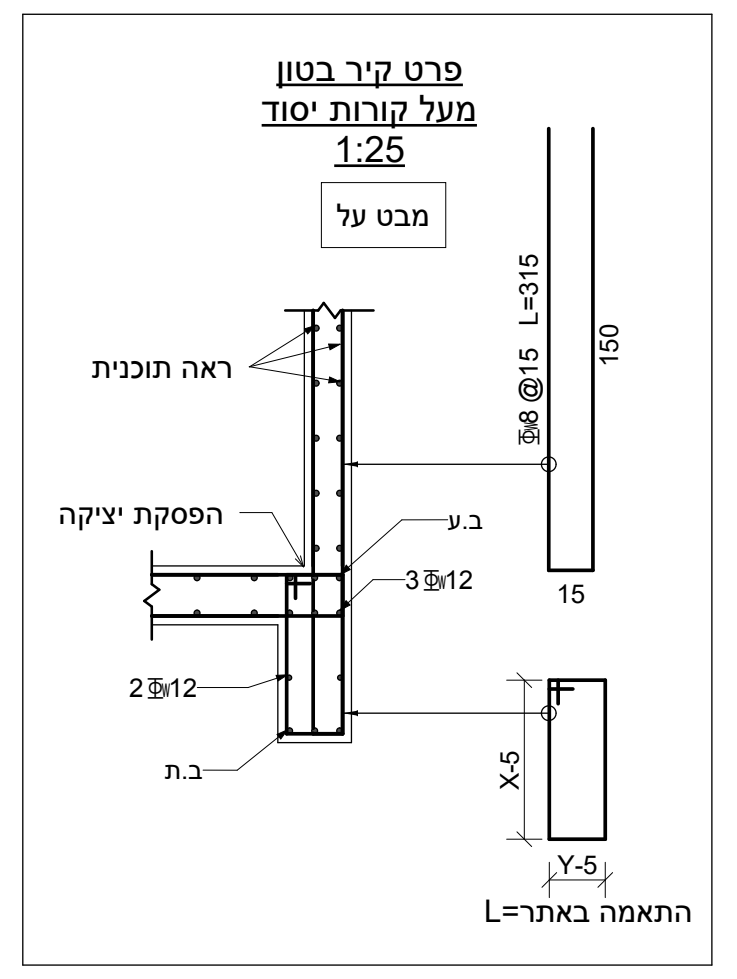

פרט קיר בטון
מעל קורות יסוד
1:25

מבט על

ראה תוכנית
Φ8 @15 L=315
150
15
הפסקת יציקה
ב.ע
3Φ12
2Φ12
ב.ת
X-5
Y-5
התאמה באתר=L

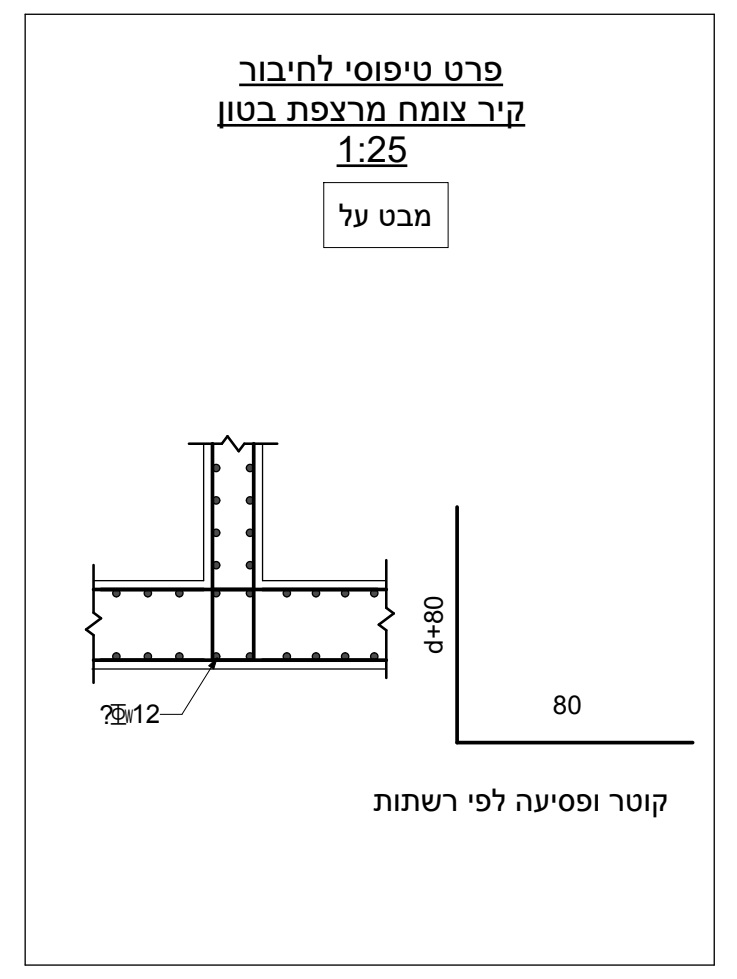

פרט טיפוסי לחיבור
קיר צומח מרצפת בטון
1:25

מבט על

?Φ12
d+80
80
קוטר ופסיעה לפי רשתות

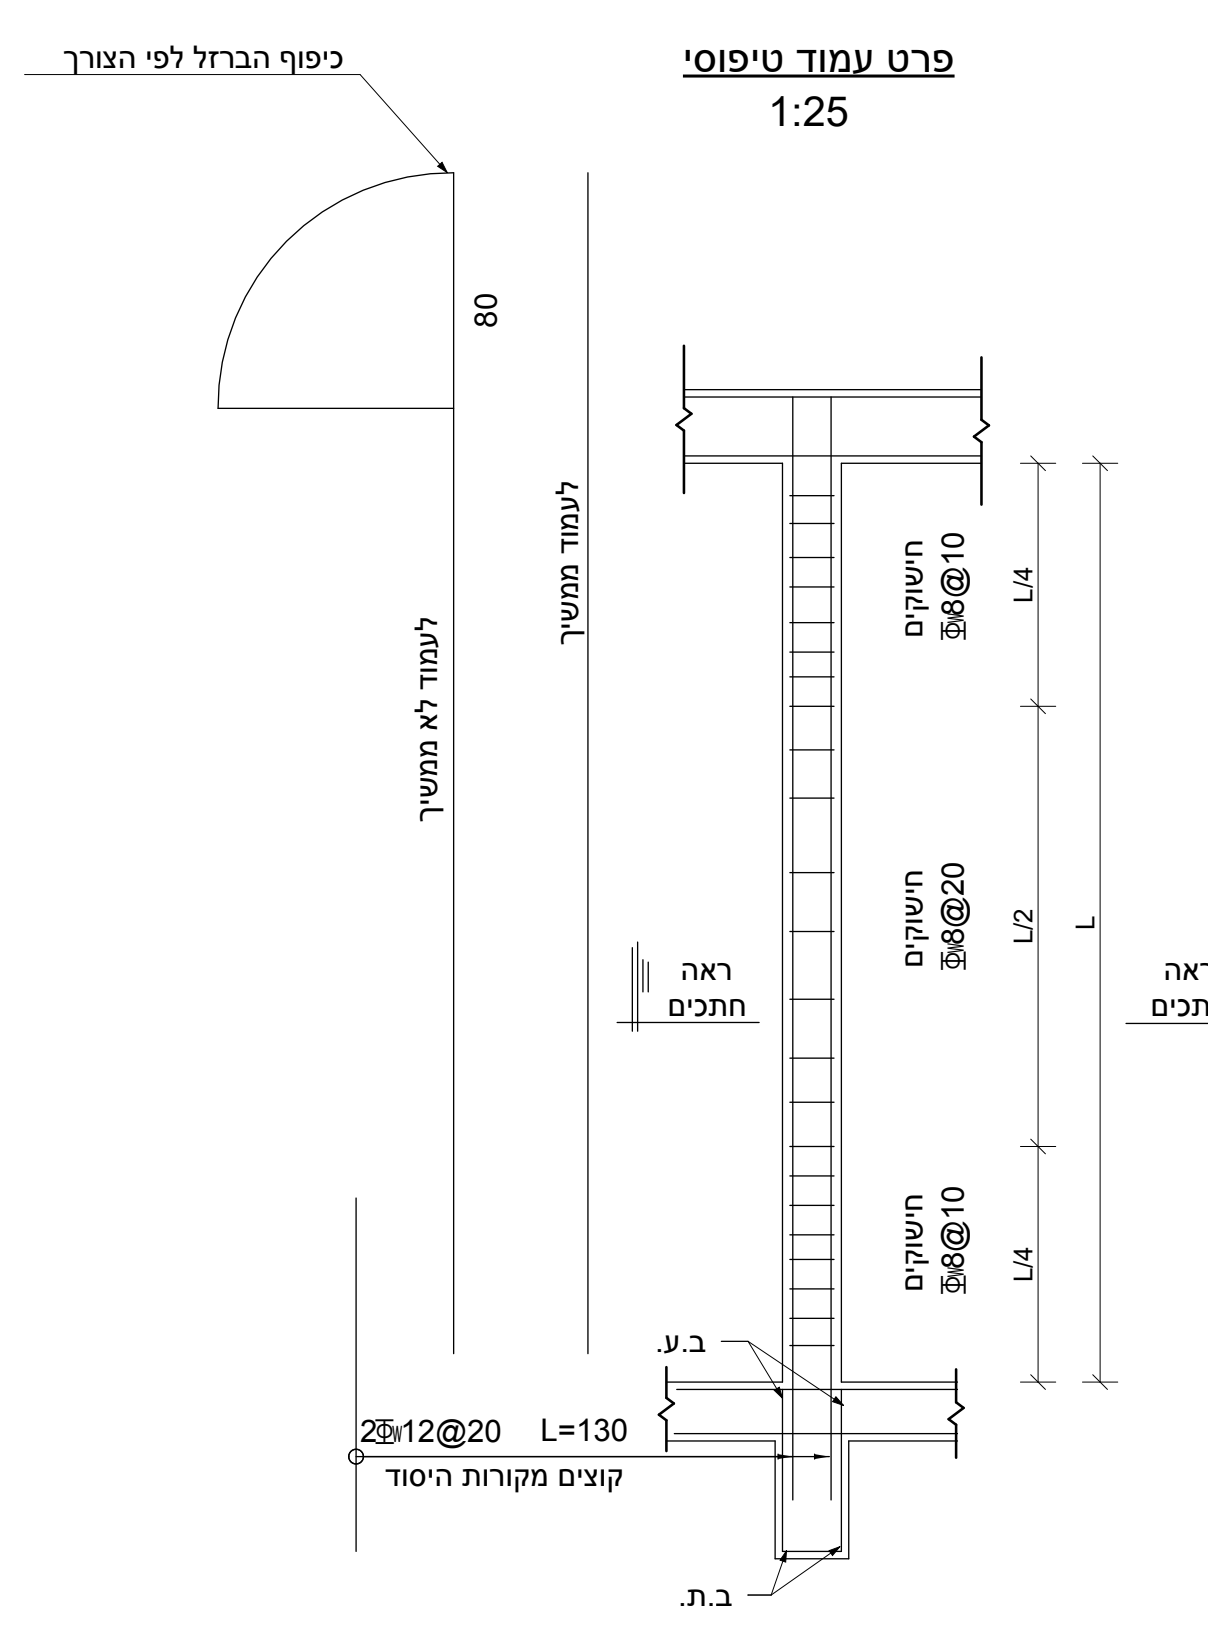

פרט עמוד טיפוסי
1:25

כיפוף הברזל לפי הצורך
80
לעמוד לא ממשיך
לעמוד ממשיך
חישוקים
Φ8@10
L/4
חישוקים
Φ8@20
L/2
חישוקים
Φ8@10
L/4
L
ראה
חתכים
ראה
חתכים
ב.ע.
2Φ12@20 L=130
קוצים מקורות היסוד
ב.ת.

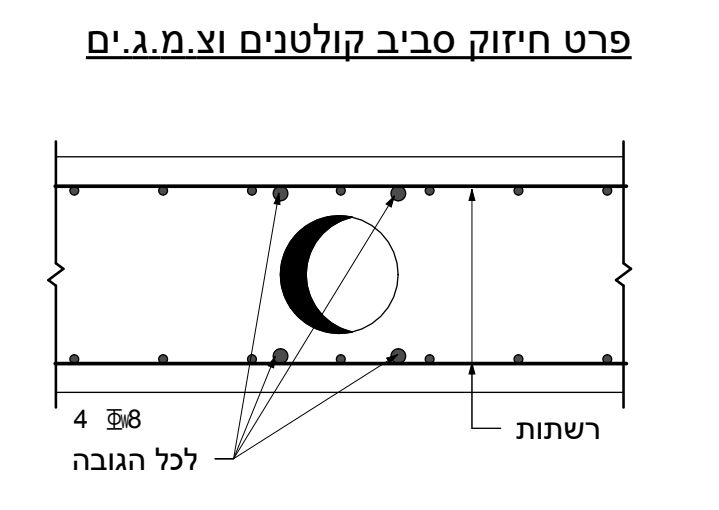

פרט חיזוק סביב קולטנים וצ.מ.ג.ים

4 Φ8
לכל הגובה
רשתות

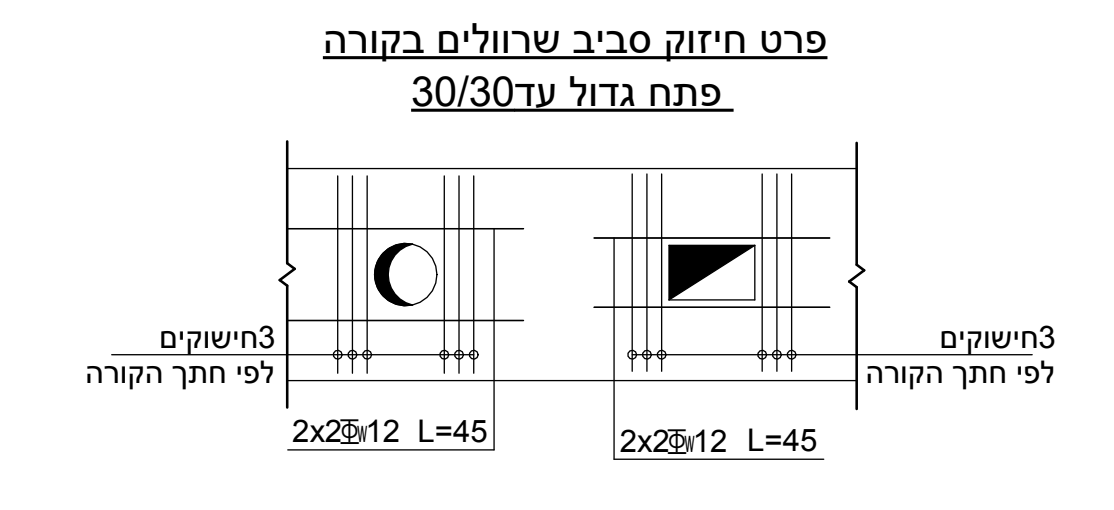

פרט חיזוק סביב שרוולים בקורה
פתח גדול עד30/30

3חישוקים
לפי חתך הקורה
2x2Φ12 L=45
3חישוקים
לפי חתך הקורה
2x2Φ12 L=45

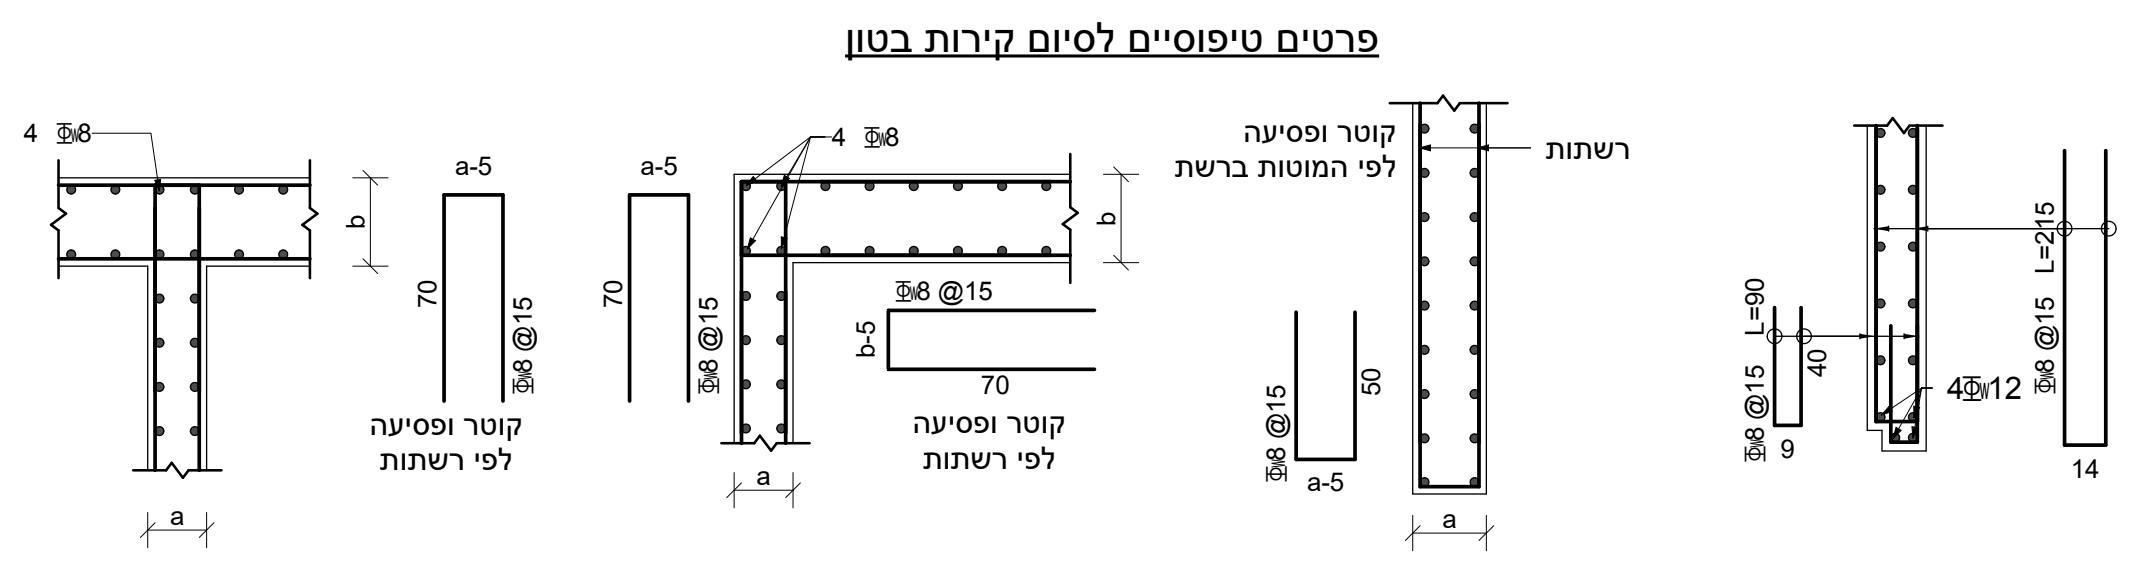

פרטים טיפוסיים לסיום קירות בטון

4 Φ8
a-5
b
70
Φ8 @15
קוטר ופסיעה
לפי רשתות
a
a-5
70
Φ8 @15
4 Φ8
Φ8 @15
b-5
70
קוטר ופסיעה
לפי רשתות
קוטר ופסיעה
לפי המוטות ברשת
רשתות
50
Φ8 @15
a-5
Φ8 @15 L=90
40
9
4Φ12
Φ8 @15 L=215
14

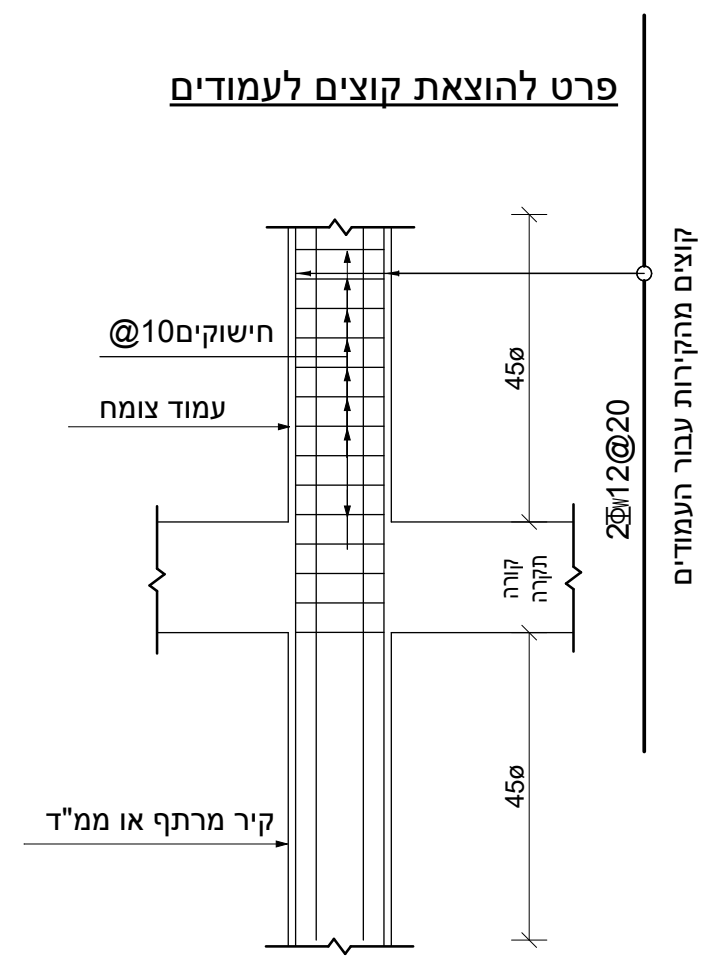

פרט להוצאת קוצים לעמודים

חישוקים@10
עמוד צומח
קיר מרתף או ממ"ד
45ø
45ø
קורה
תקרה
2Φ12@20
קוצים מהקירות עבור העמודים

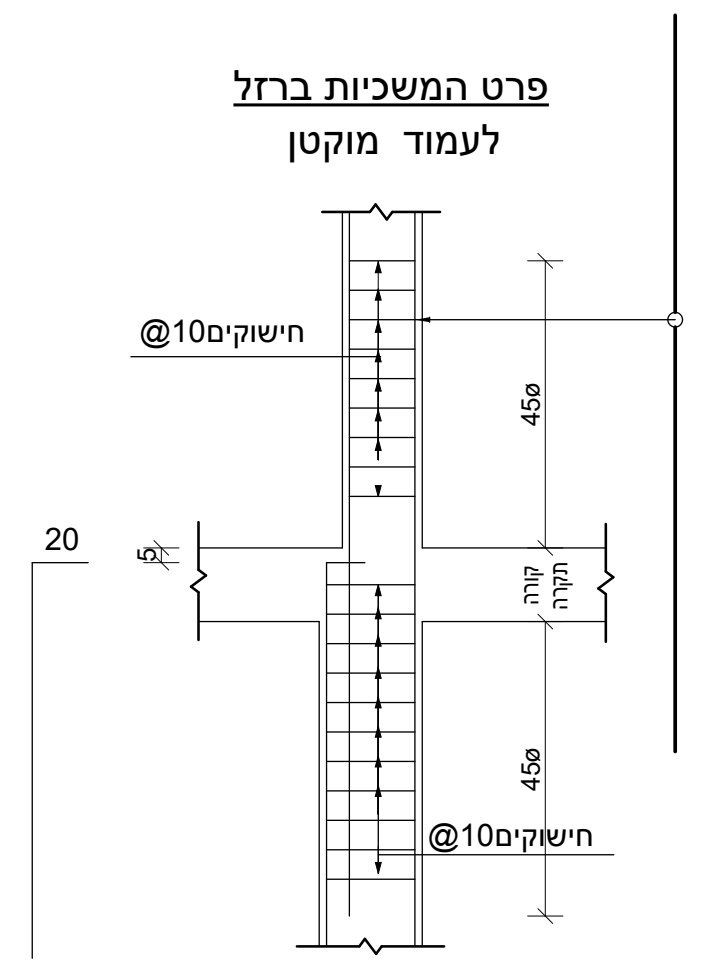

פרט המשכיות ברזל
לעמוד מוקטן

20
5
חישוקים@10
45ø
45ø
קורה
תקרה
חישוקים@10

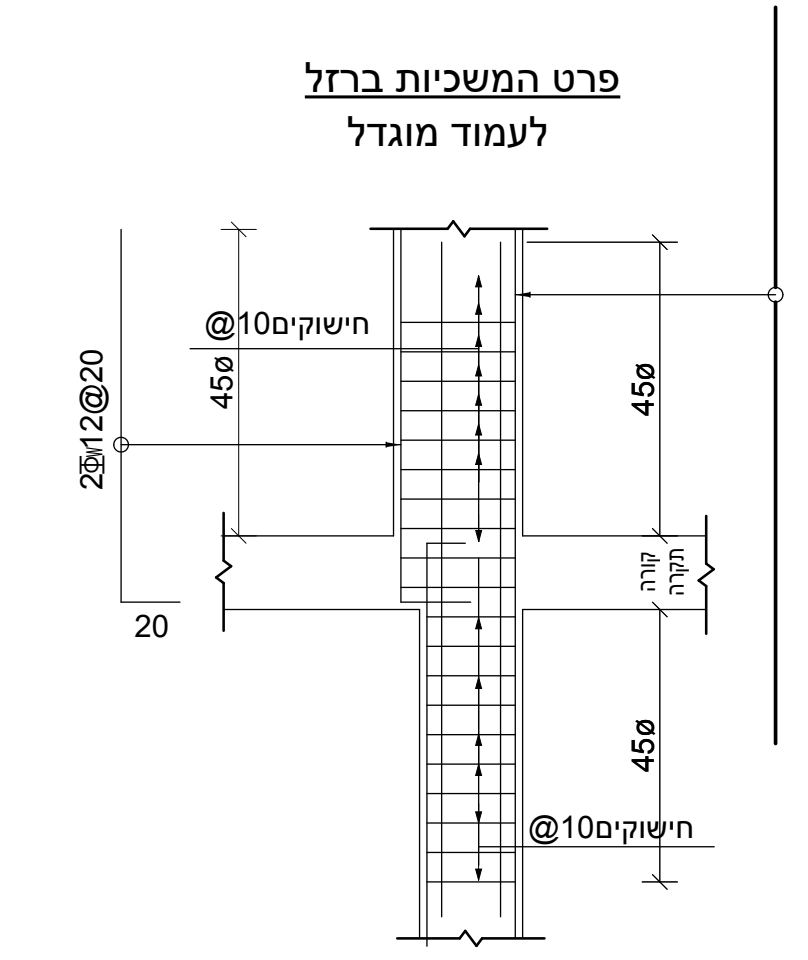

פרט המשכיות ברזל
לעמוד מוגדל

2Φ12@20
20
חישוקים@10
45ø
45ø
45ø
קורה
תקרה
חישוקים@10

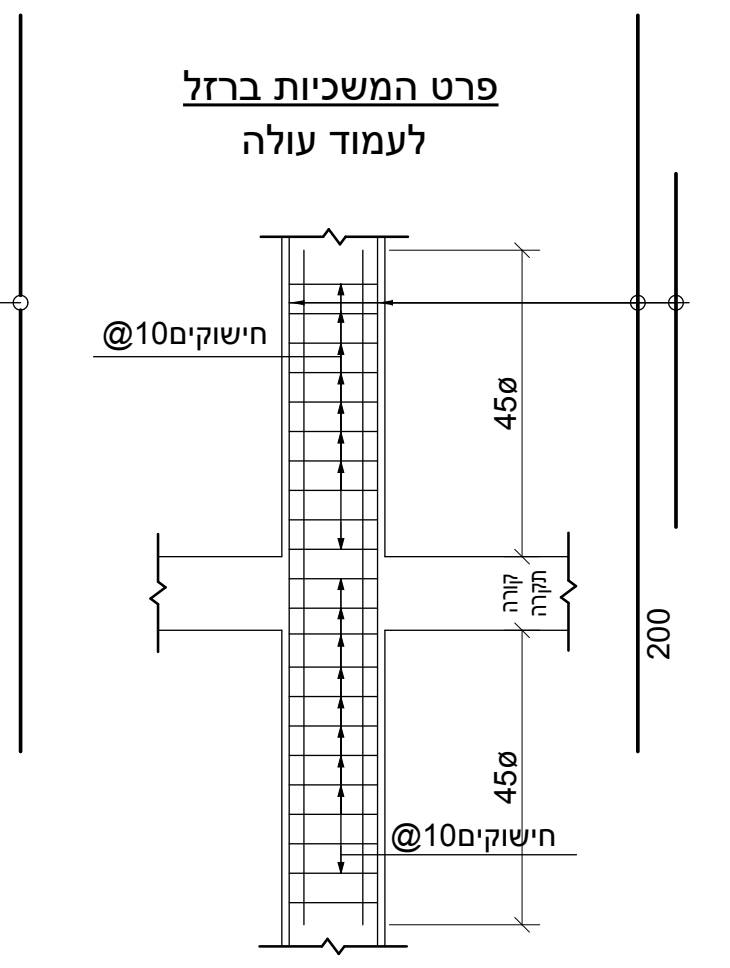

פרט המשכיות ברזל
לעמוד עולה

חישוקים@10
45ø
45ø
קורה
תקרה
200
חישוקים@10