הערות

1. יש לקרוא תוכנית זו יחד עם תוכנית חשמל אינסטלציה ואיטום.
2. תכנית זאת מיועדת לביצוע רק במידה ומולאו שני תנאים בסיסיים:
א .אישור האדריכל
ב . התוכנית מתאימה להיתר הבניה)באישור המהנדס האחראי על הביצוע)
3. תוכנית זאת תבוצע רק לאחר חתימת האדריכל והמודד עליה המאשרים כי היא מתאימה להיתר בניה והתקנים מבחינת העמדת המבנים במגרש
4. מיקום המבנה ביחס למגרש יקבע ע" י המודד בהתאם לתוכנית העמדה של האדריכל.
5. עובי כיסוי הבטון יהיה2.5ס " מ בכל האלמנטים מלבד אלה שבאים במגע עם הקרקע - שם עובי הכיסוי יהיה4ס "מ.
6. הארקת יסוד -יש לעיין בתכנית יועץ חשמל.
7. אין להעביר צינורות בקוטר גדול מ-50מ "מ ללא אישור מהמהנדס המתכנן.
8. דוח קרקע הינו חלק בלתי נפרד מתכנית זו.
9. סוג בטון ב-30 דרגת חשיפה 3.
10. יש לבצע התאמה בין תכניות האדריכליות ושאר היועצים לבין תכנית זו - לפני ביצוע.
11. אין להעמיס את המרפסות הן לפני הבנייה , והן אחרי הבנייה בעומס הגדול מהמצויין בתכנית!
12. פירוק טפסות בכל שלב יהיה - אך ורק באישור בכתב ממתכנן הקונסטרוקציה.

▨ עמוד / קיר-צומח

▩ עמוד / קיר-מפסיק

*סוגי בטון ראה ברשימת כמויות

מס 'עידכון	מהות העידכון	ע"י	תאריך
P1	W8 הזזת עמוד		1.11.26
P0	תוכניות לביצוע		5.10.26

עומסים

עומס קבוע נוסף	500 =ק"ג /מ"ר
עומס שימושי	150 =ק"ג /מ"ר
עומס מרפסות	350=ק"ג /מ"ר

גובה מפלס)אדריכלות): +3.85

מפלס פני בטון: +3.70

P1 מעודכן לתאריך: 1.11.26

לעיון	לאישור	למכרז	לביצוע
○	○	○	●

שם הפרויקט:
וילה ליאור ואביחי אטואן

תאור השרטוט:
קומה א -פריסת ברזל

מס 'השרטוט:
K-33

מס 'פרויקט: WORK-167
קנ"מ:
דוא" ל: tal@yarin-eng.co.il
גודל גליון: 1588 X 900
מהנדס אחראי: טל שיי אטיאס
מהנדס: רותם מאיר

ירין הנדסה
טל אטיאס: 050-444-4730
tal@yarin-eng.co.il
YARIN
תכנון | ניהול | פיקוח מבנים

01/11/2026 10:16:32
C:\Users\LENOVO P340\Desktop\עבודה\תוכניות עבודה\רותם\work
רויט\מודל רויט\קובץ\cons\פתיחת תיקייה רויט\אביחי אטואן\167-
התחלתי.rvt

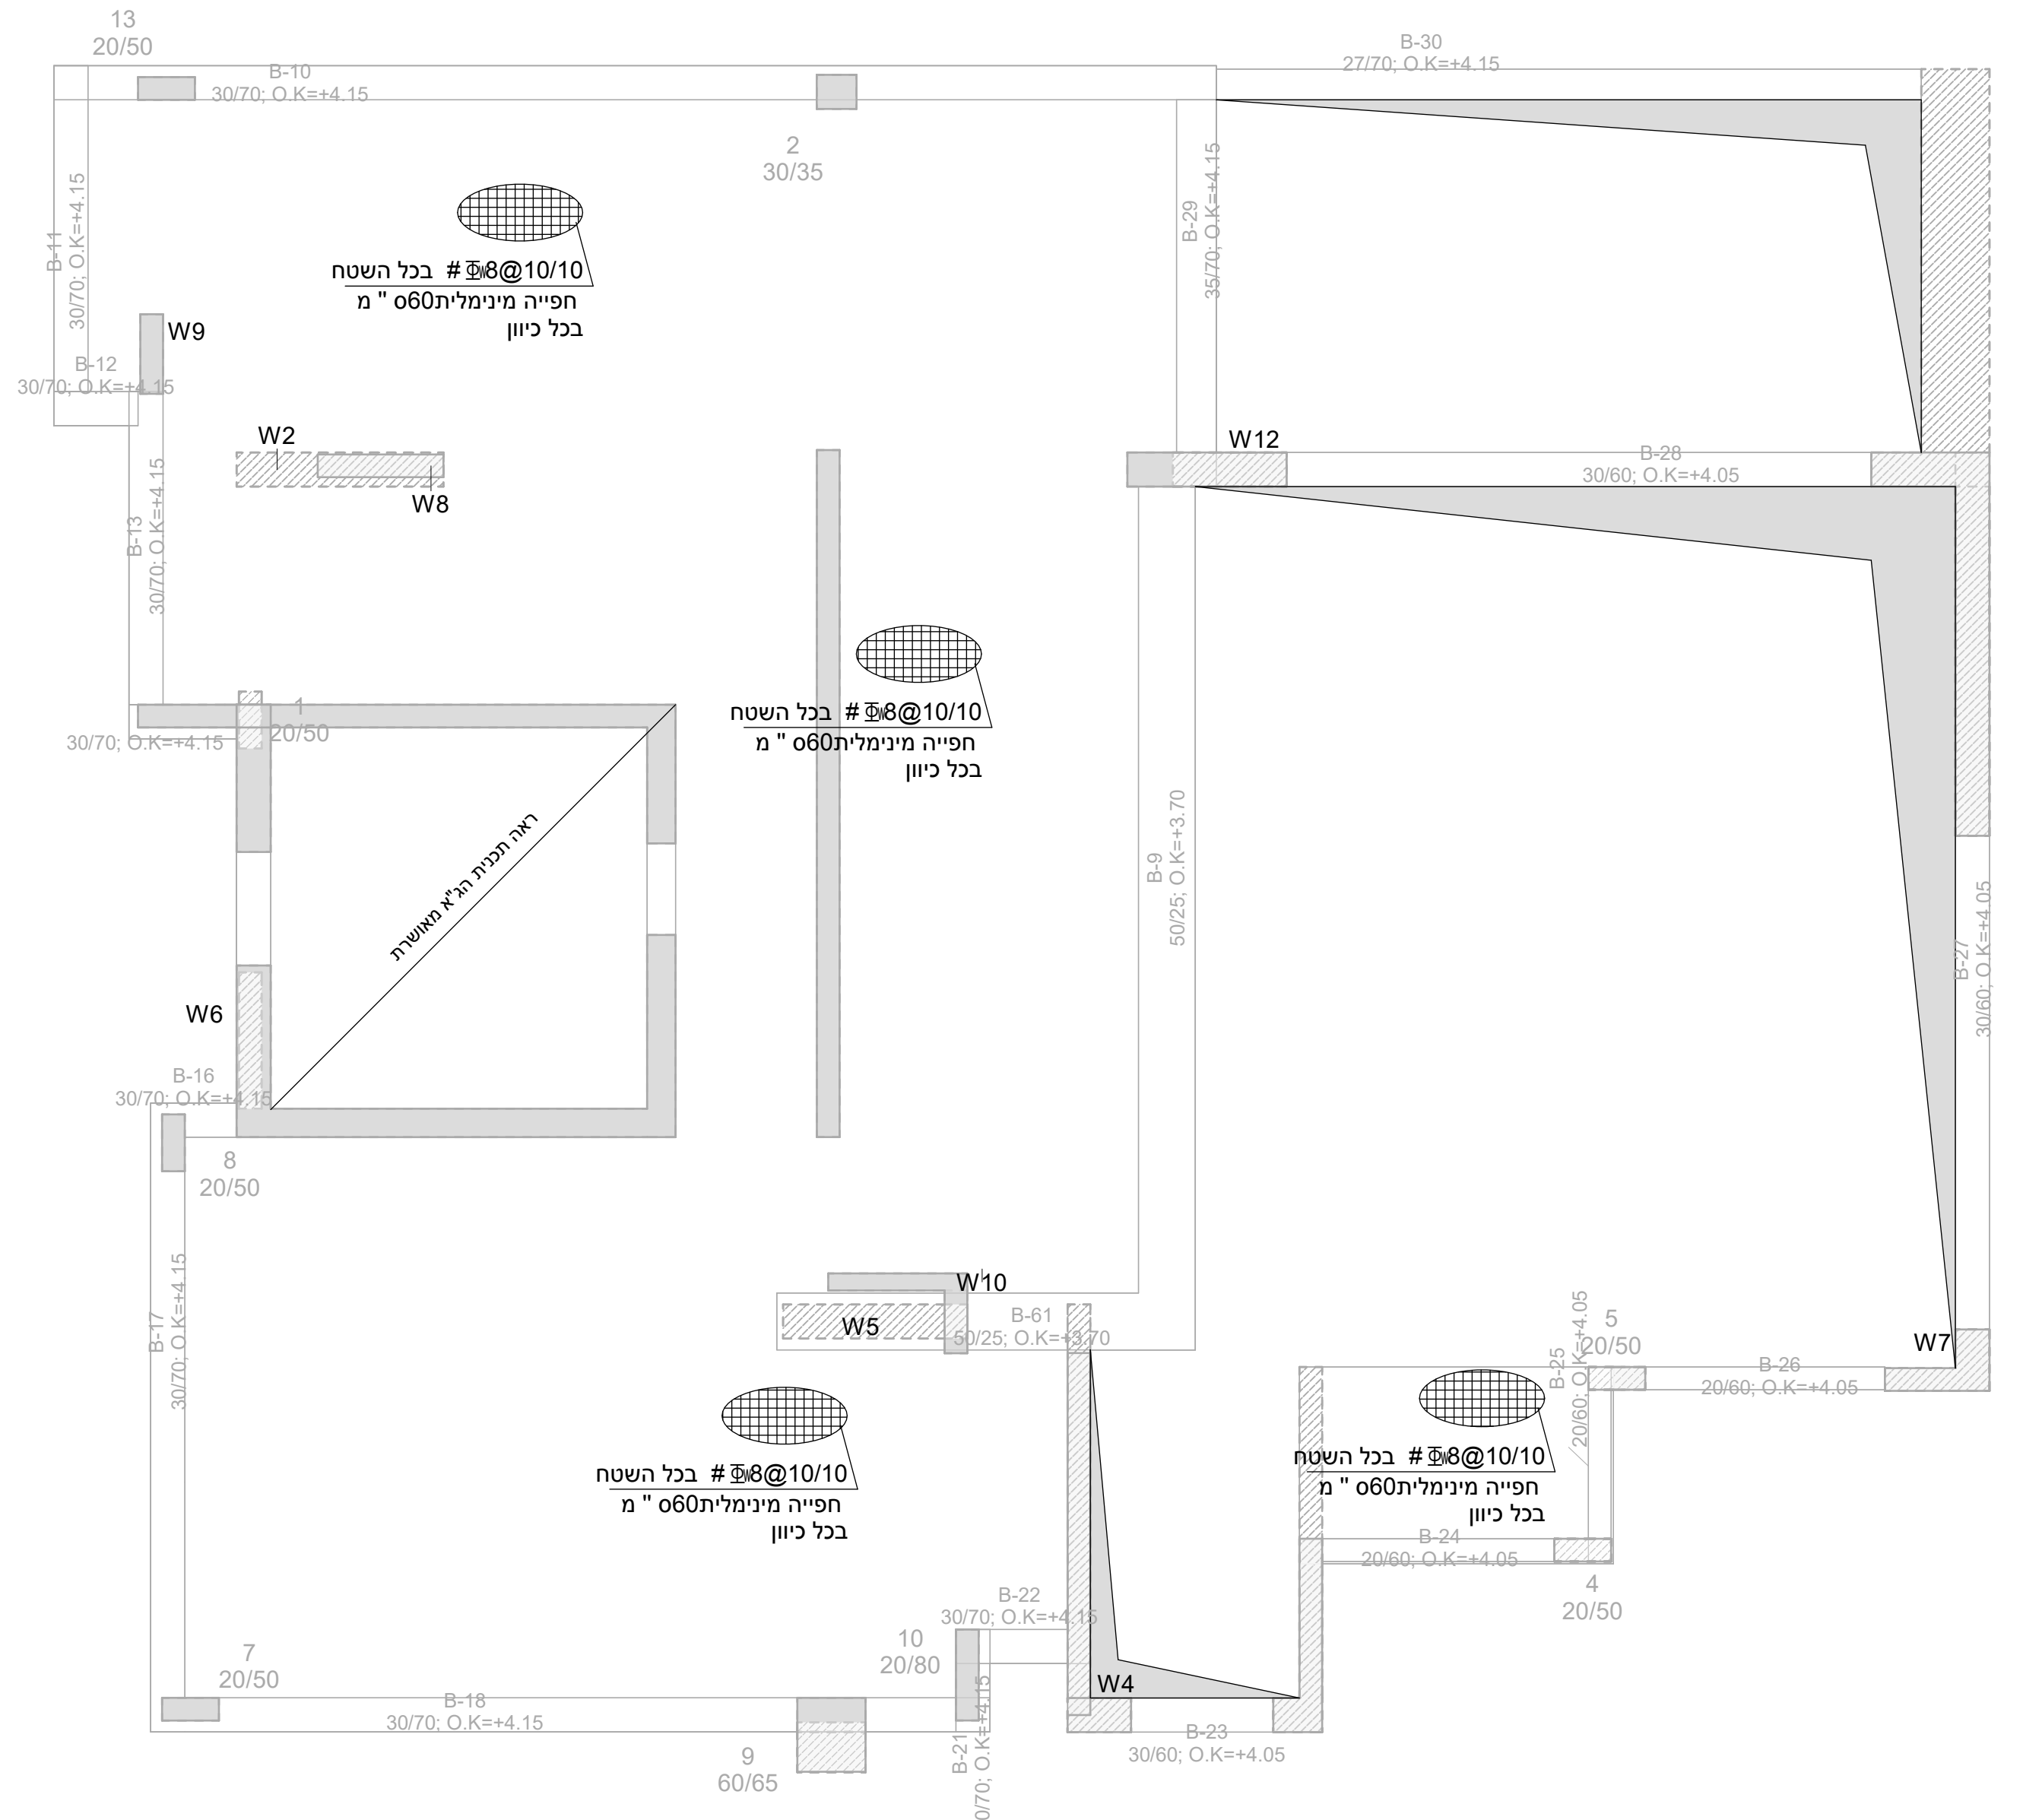

ברזל תחתון
1 : 50

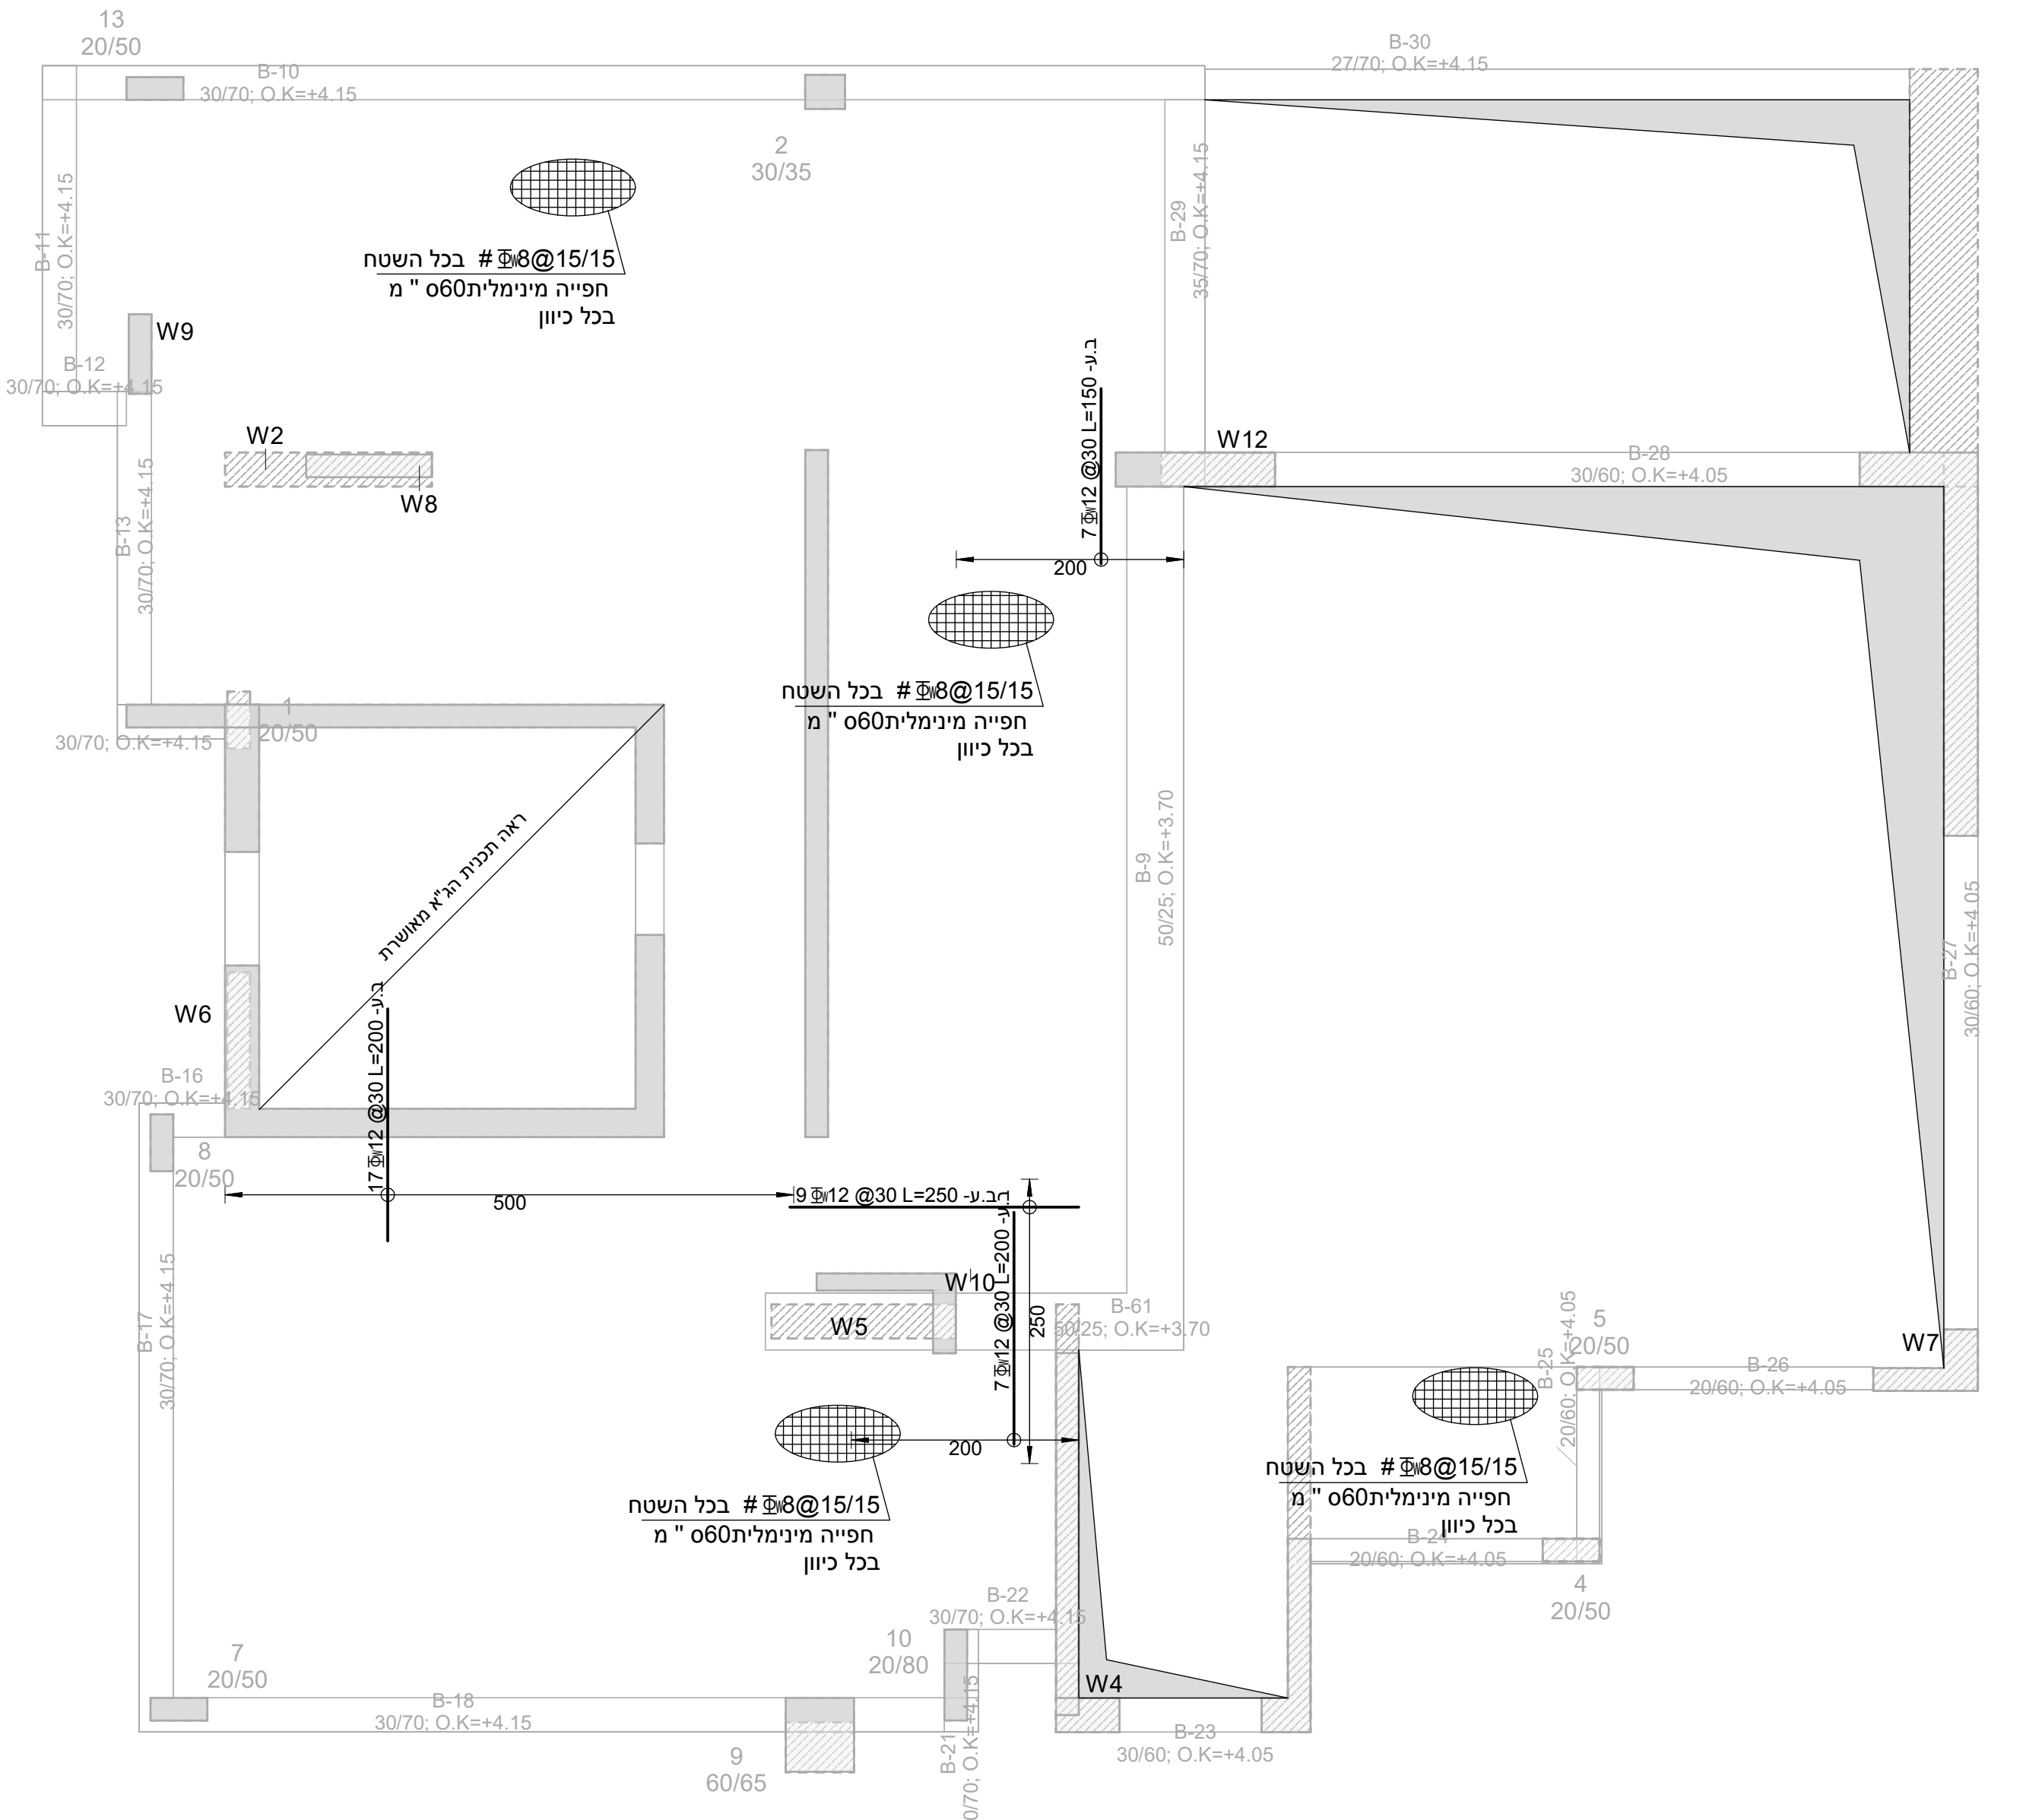

ברזל עליון
1 : 50

פרט חפייה טיפוסי רשתות מרותכות
1:10

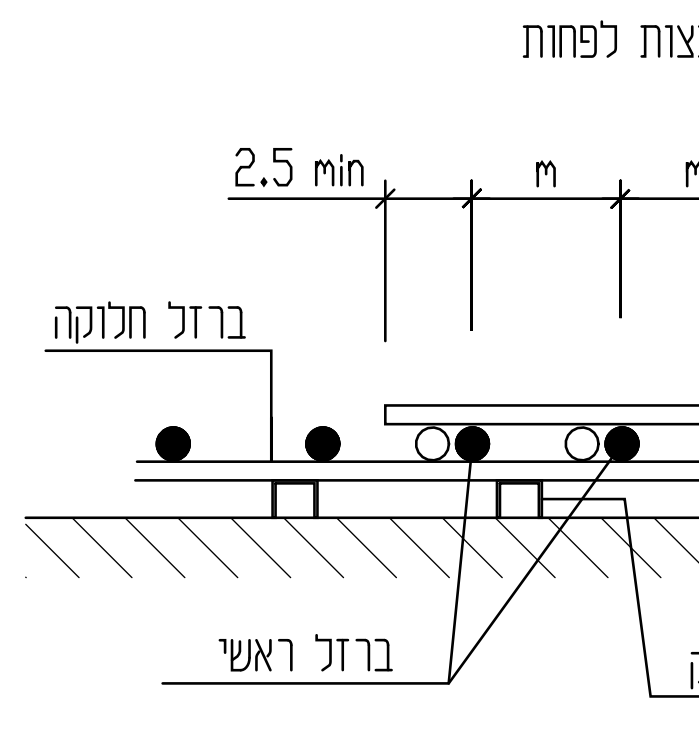

*** אין לפרק תפסנות עד לקשיחות גג עליון- כולל***

פרט אופקי.1
פרט ריתום אופקי בקירות
1:25

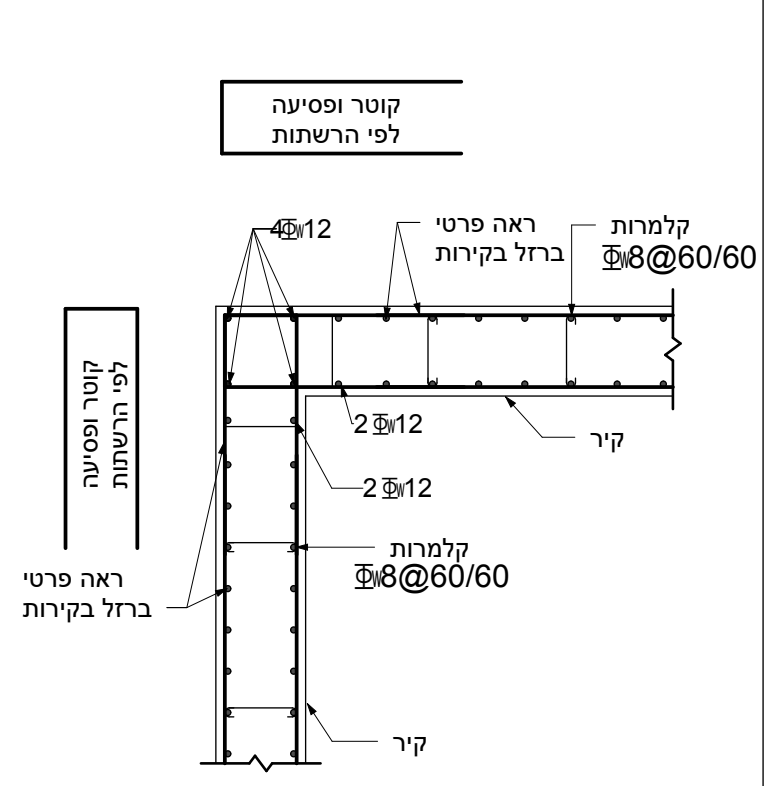

פרט אופקי.2
פרט ריתום אופקי בקירות
1:25

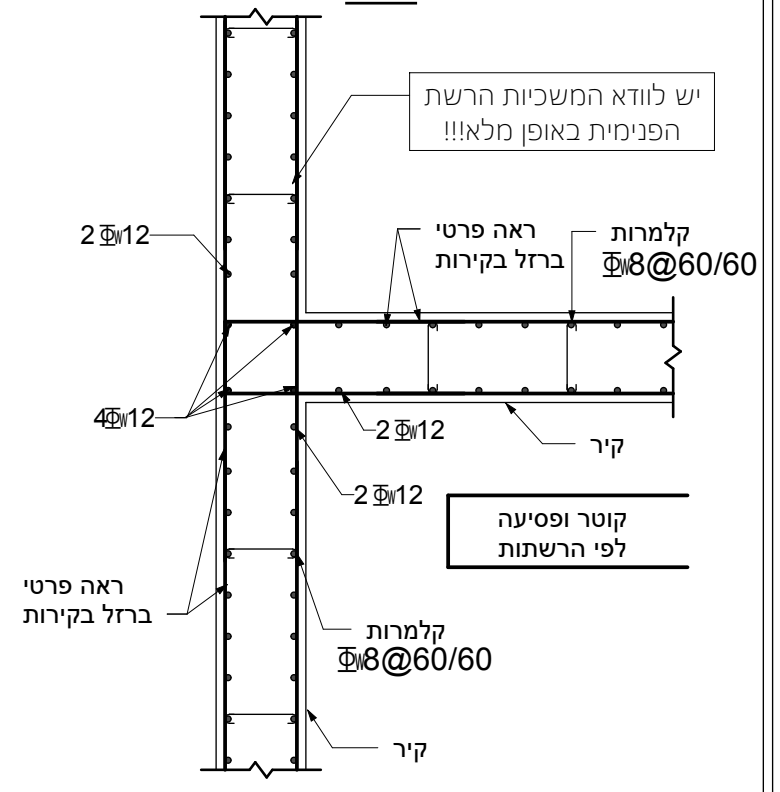

פרט אופקי.3
פרט פינת דלת
1:25

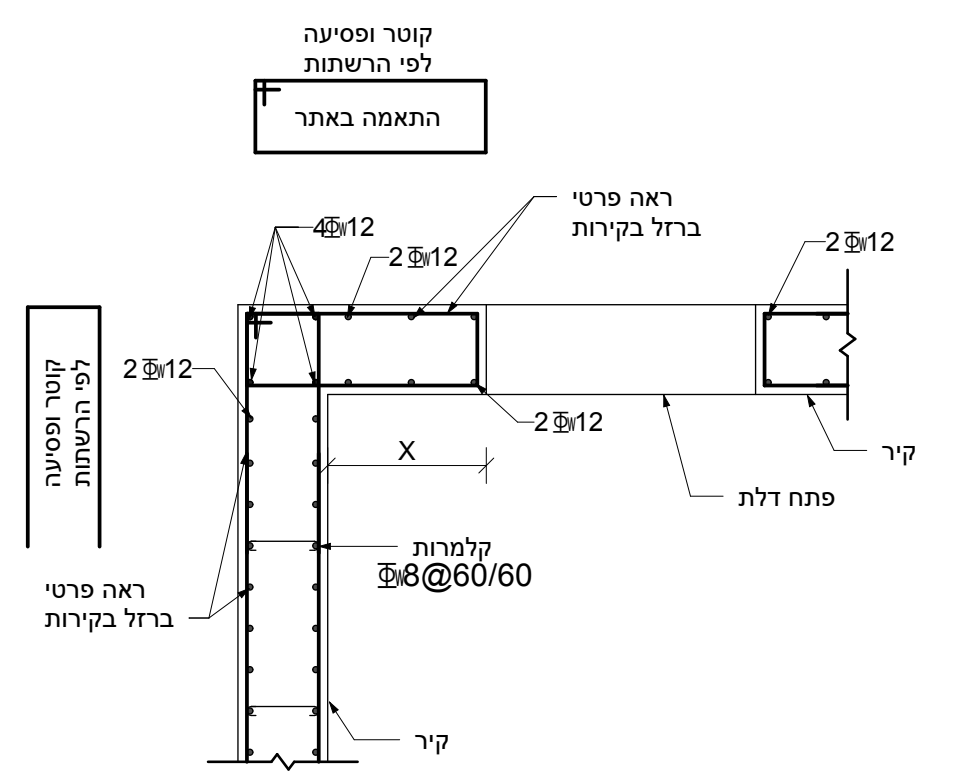

פרט אופקי.4
פרט קצה קיר
1:25

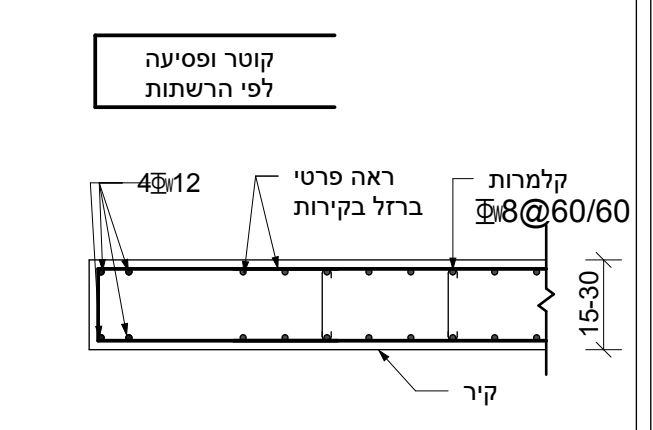

פרט אופקי.5
פרט ריתום אופקי בקירות -
פרט דלת
1:25

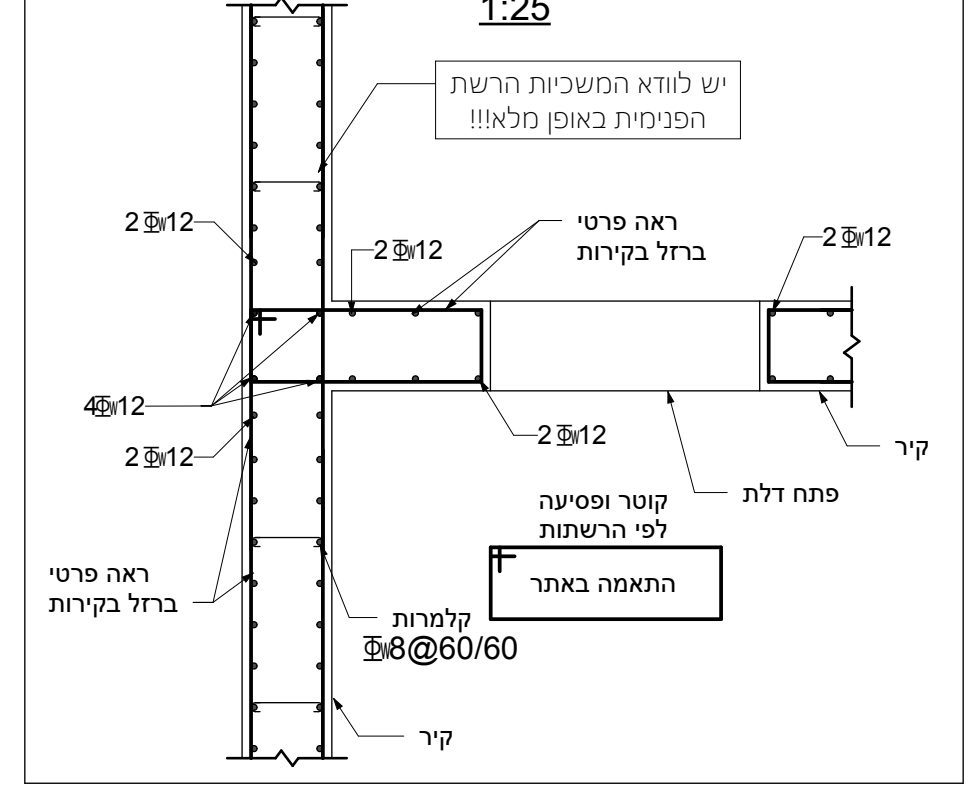

פרט אופקי.6
פרט ריתום אופקי בקירות-
צומת T
1:25

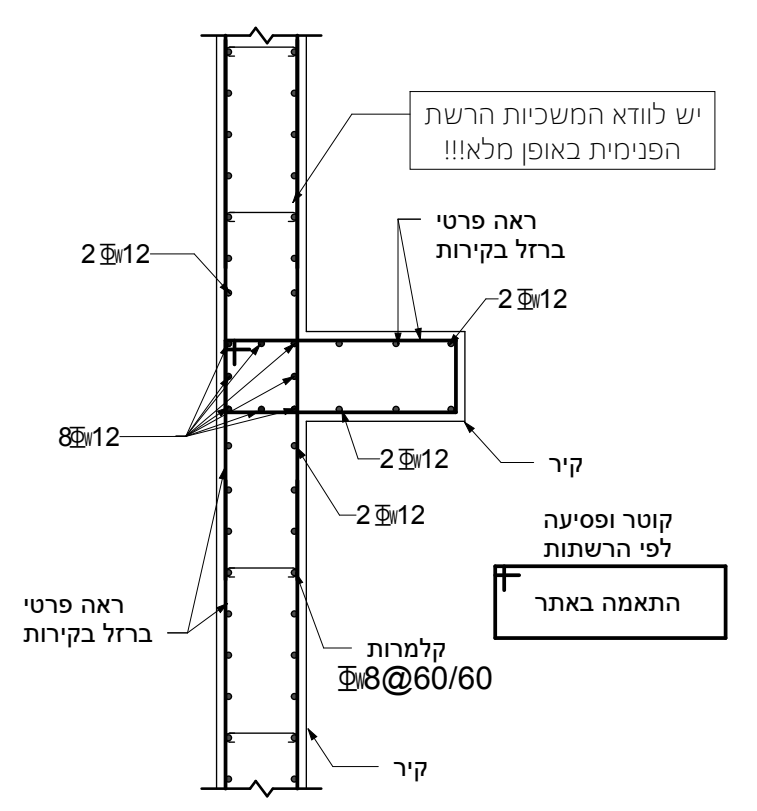

פרט אופקי.7
פרט ריתום אופקי בקירות
1:25

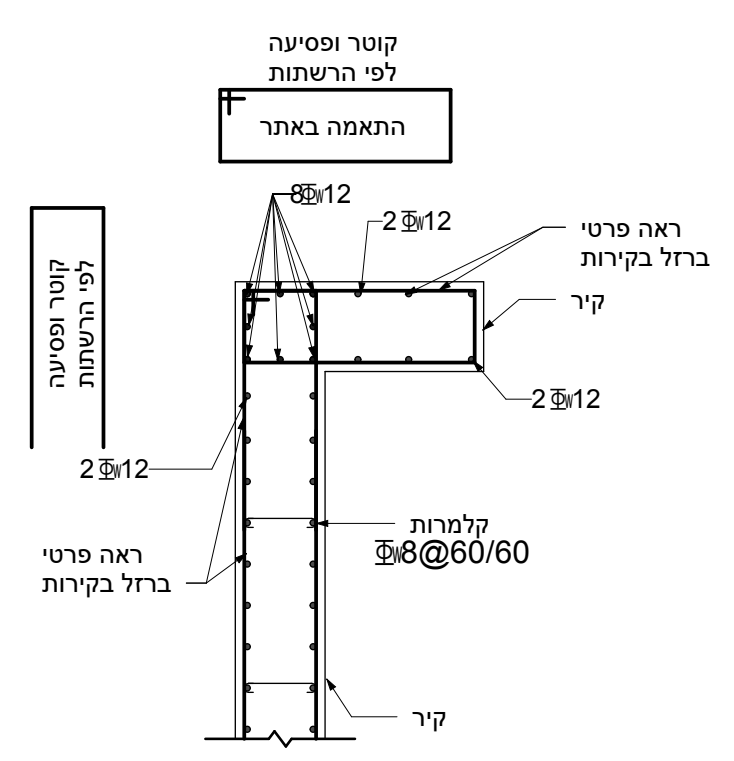

פרט אופקי.8
פרט ריתום אופקי בקירות
1:25

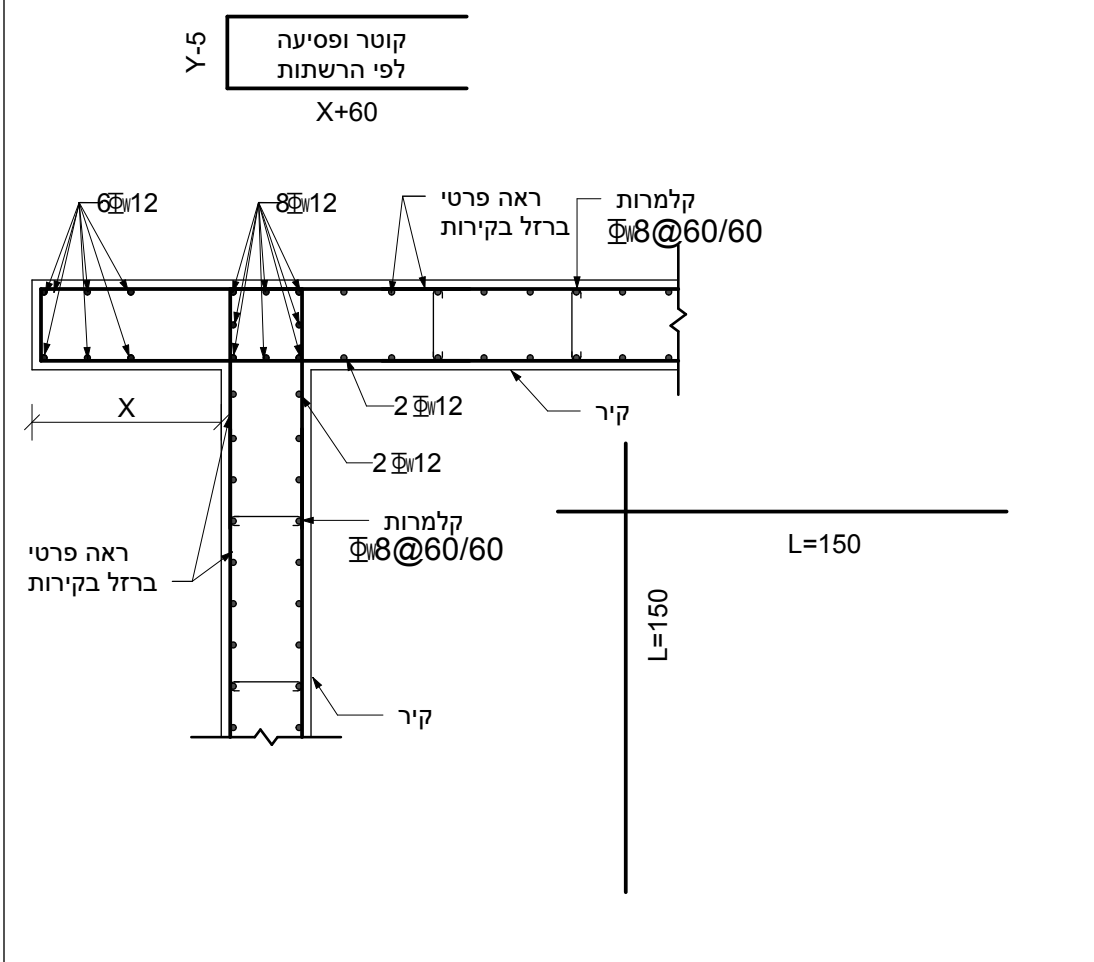

פרט אופקי.9
פרט ריתום אופקי בקירות
1:25

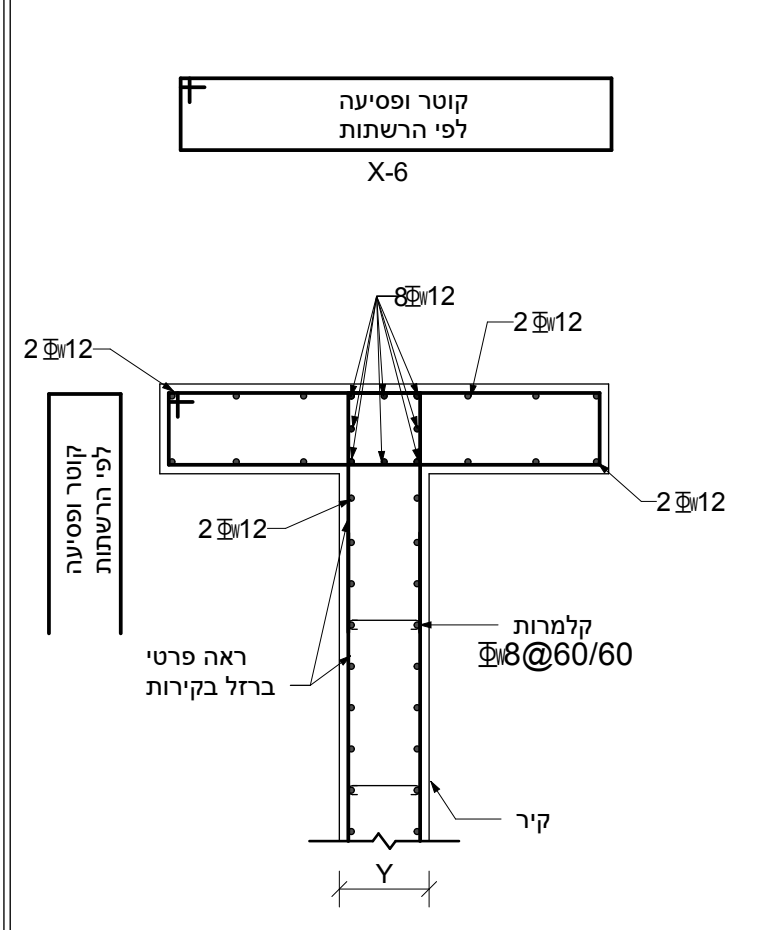

חתך1-1
1:25

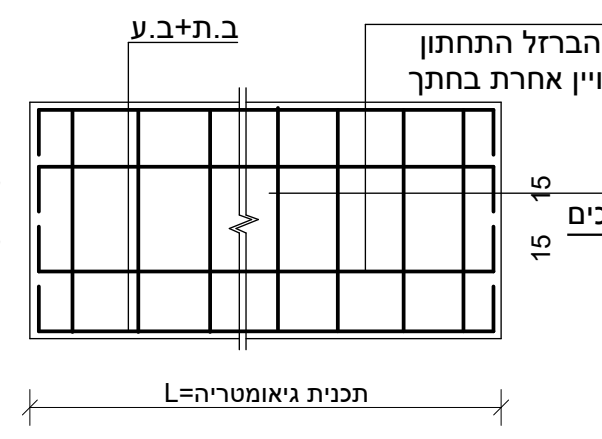

פרט טיפוסי
לסידור ברזל בקורות
1:25

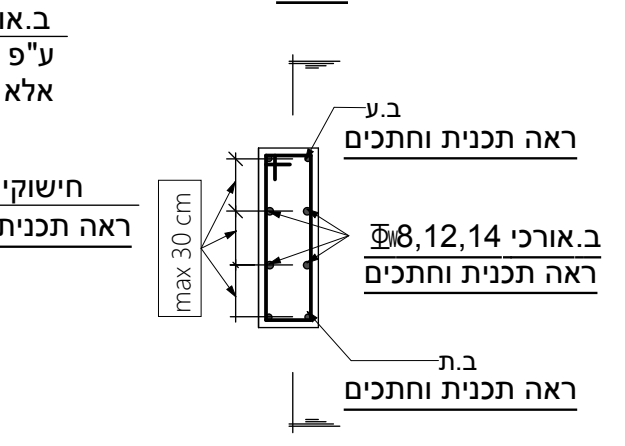

פרט טיפוסי לחיזוק
סביב פתחים ובאזור חדירת
החשמל לתקרה
1:25

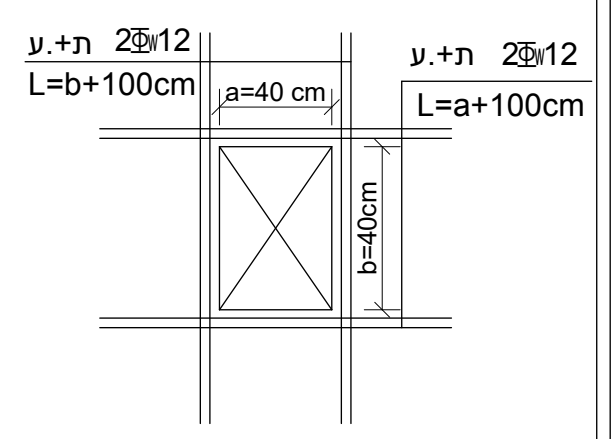

פרט טיפוסי
בקצה תקרה/רצפה
1:25

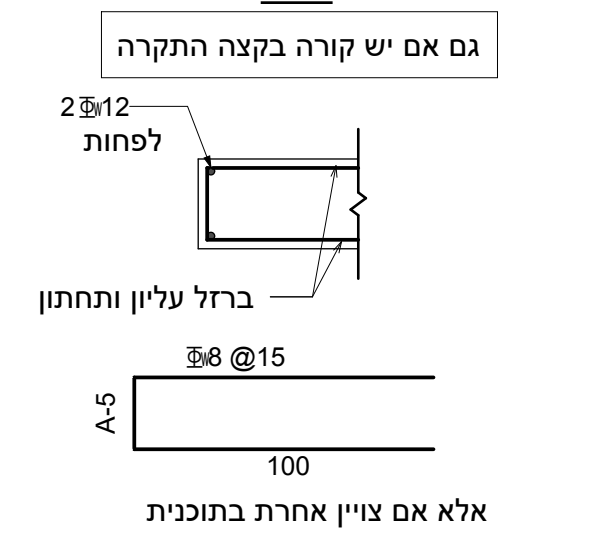

פרט טיפוסי
שינוי עובי תקרה
1:25

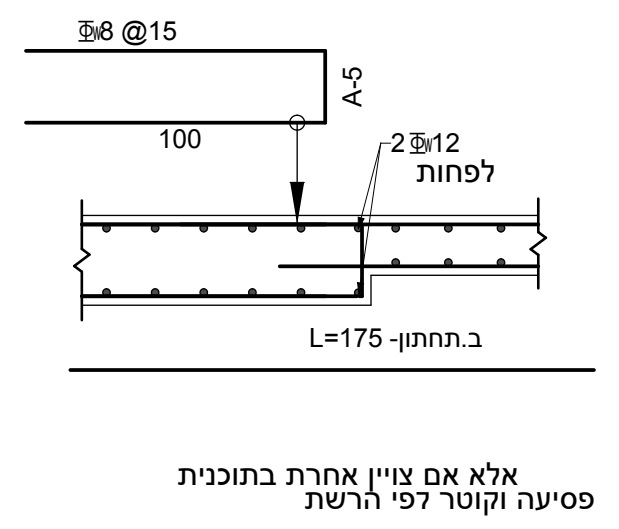

פרט טיפוסי
פרט עיגון רשתות מעל קורות/קירות/עמודים
1:25

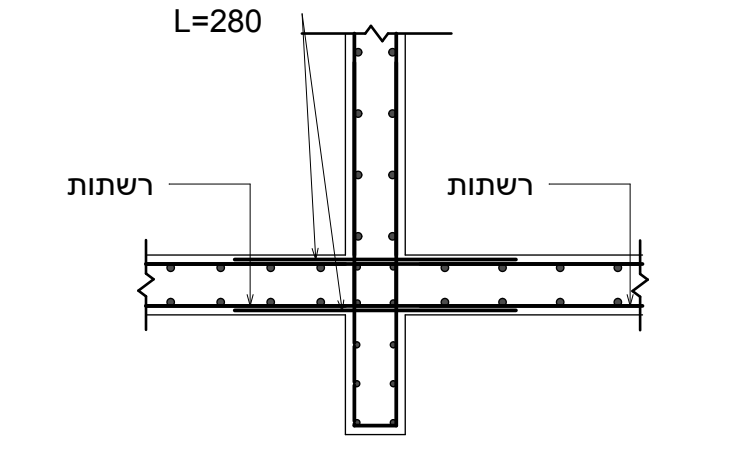

פרט טיפוסי לחיבור
קיר צומח מרצפת בטון
1:25

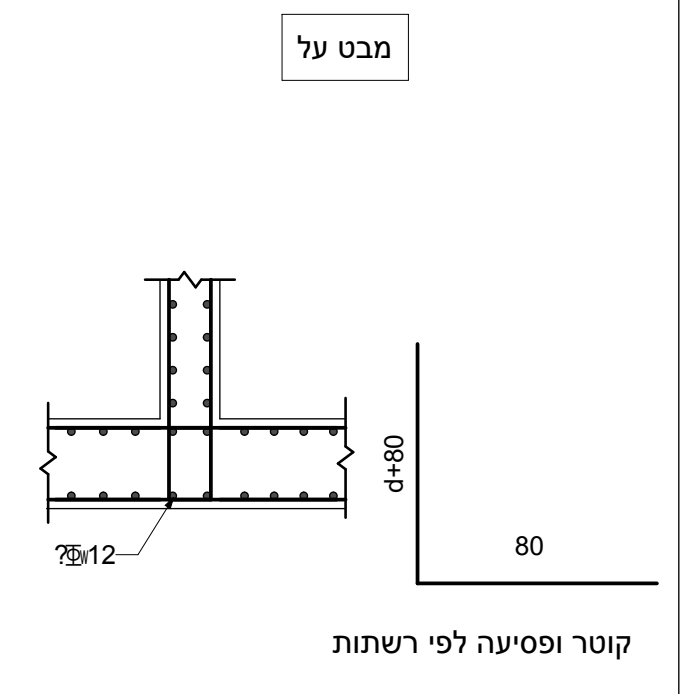

פרט קיר בטון
מעל קורות יסוד
1:25

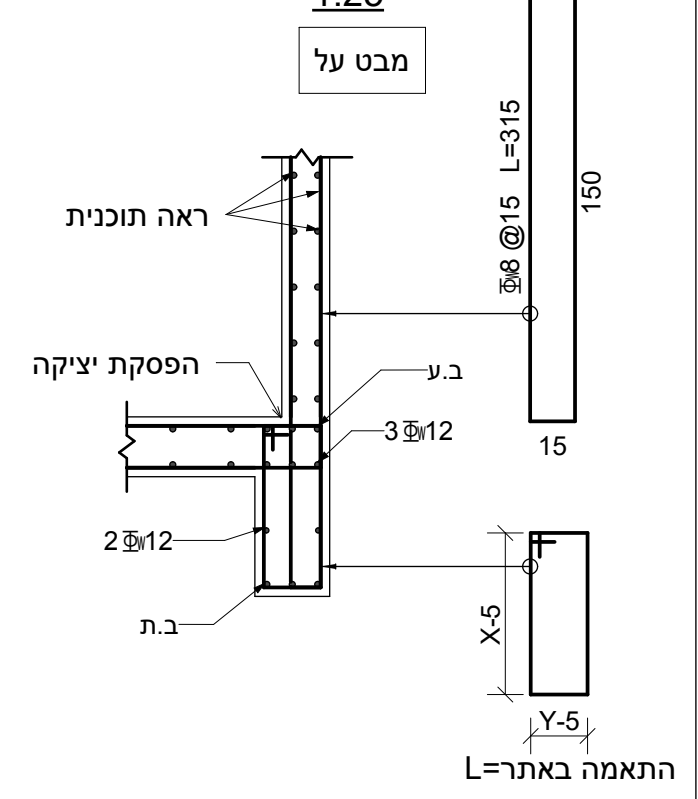

פרט חיבור B
פרט חיבור בין קורה לקיר
1:25

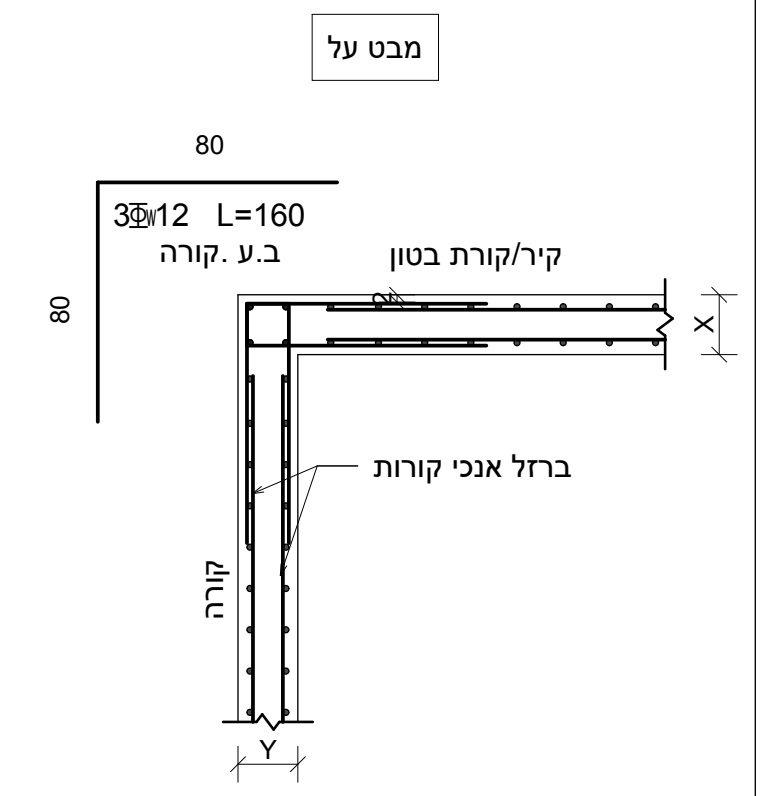

פרט חיבור A
פרט חיבור בין קורות ללא עמוד תומך
1:25

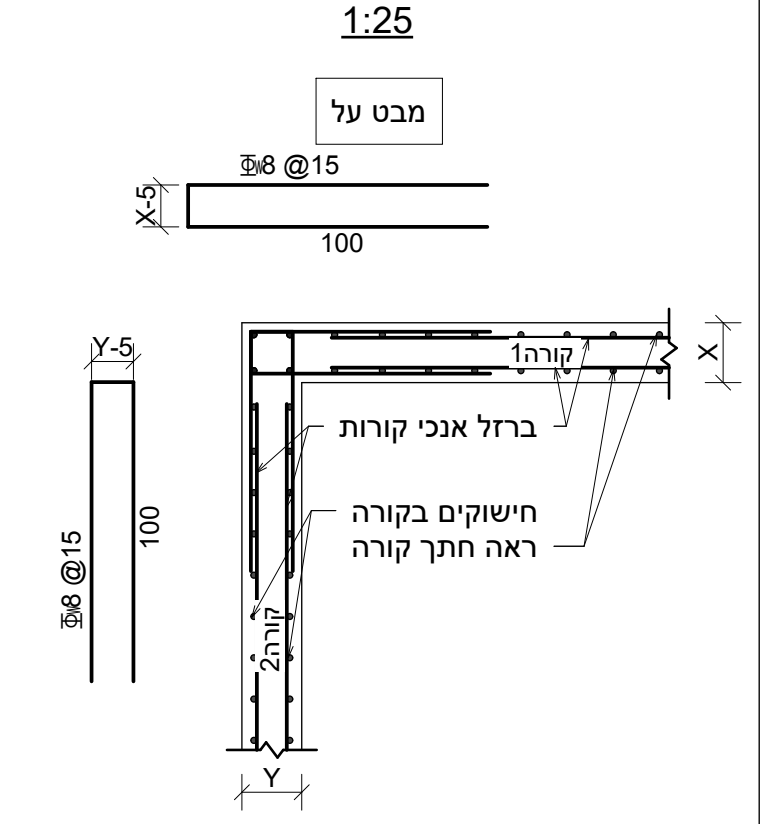

פרט עמוד טיפוסי
1:25

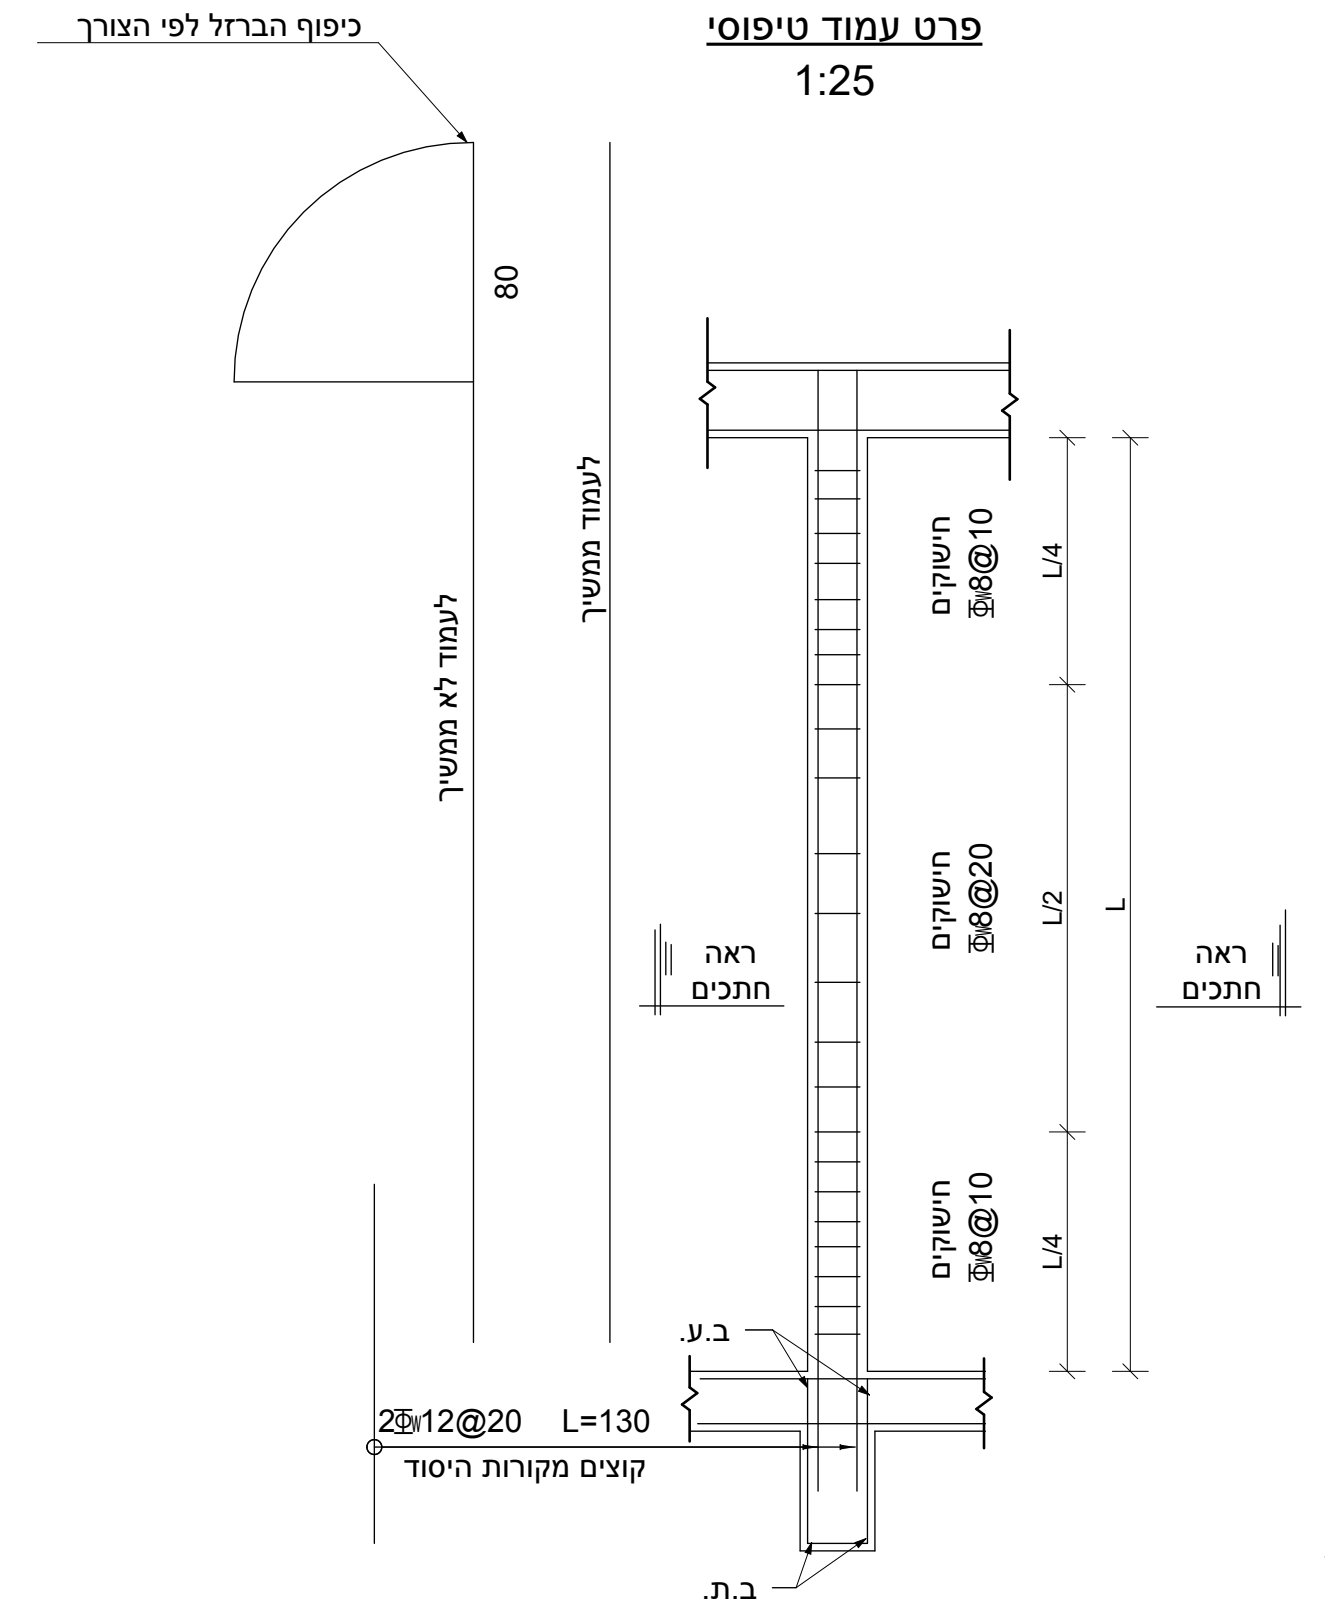

פרט חיזוק סביב קולטנים וצ.מ.ג.ים

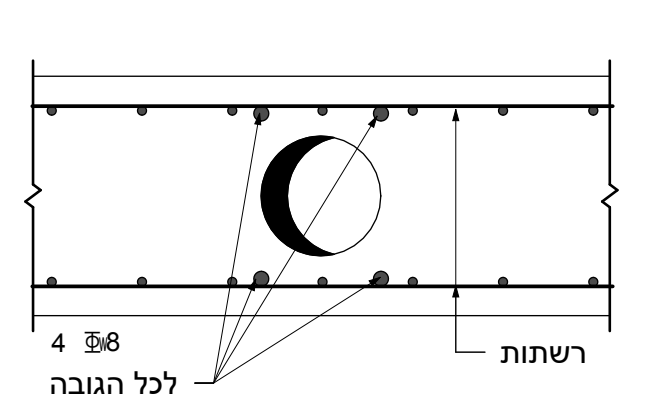

פרט חיזוק סביב שרוולים בקורה
פתח גדול עד30/30

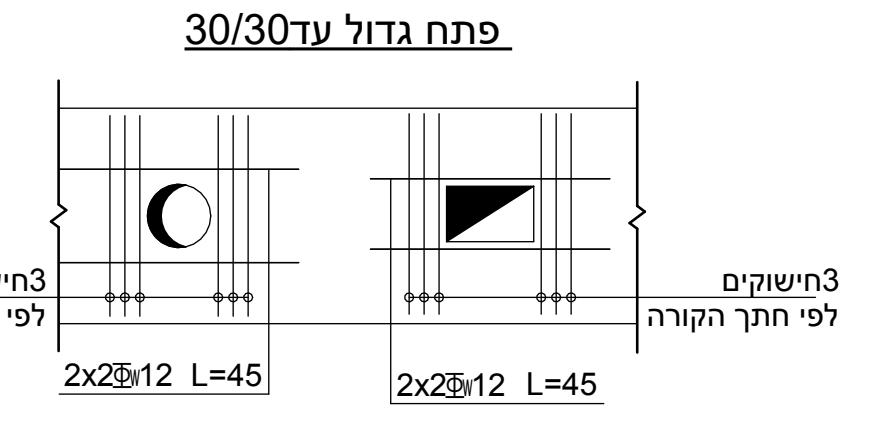

פרטים טיפוסיים לסיום קירות בטון

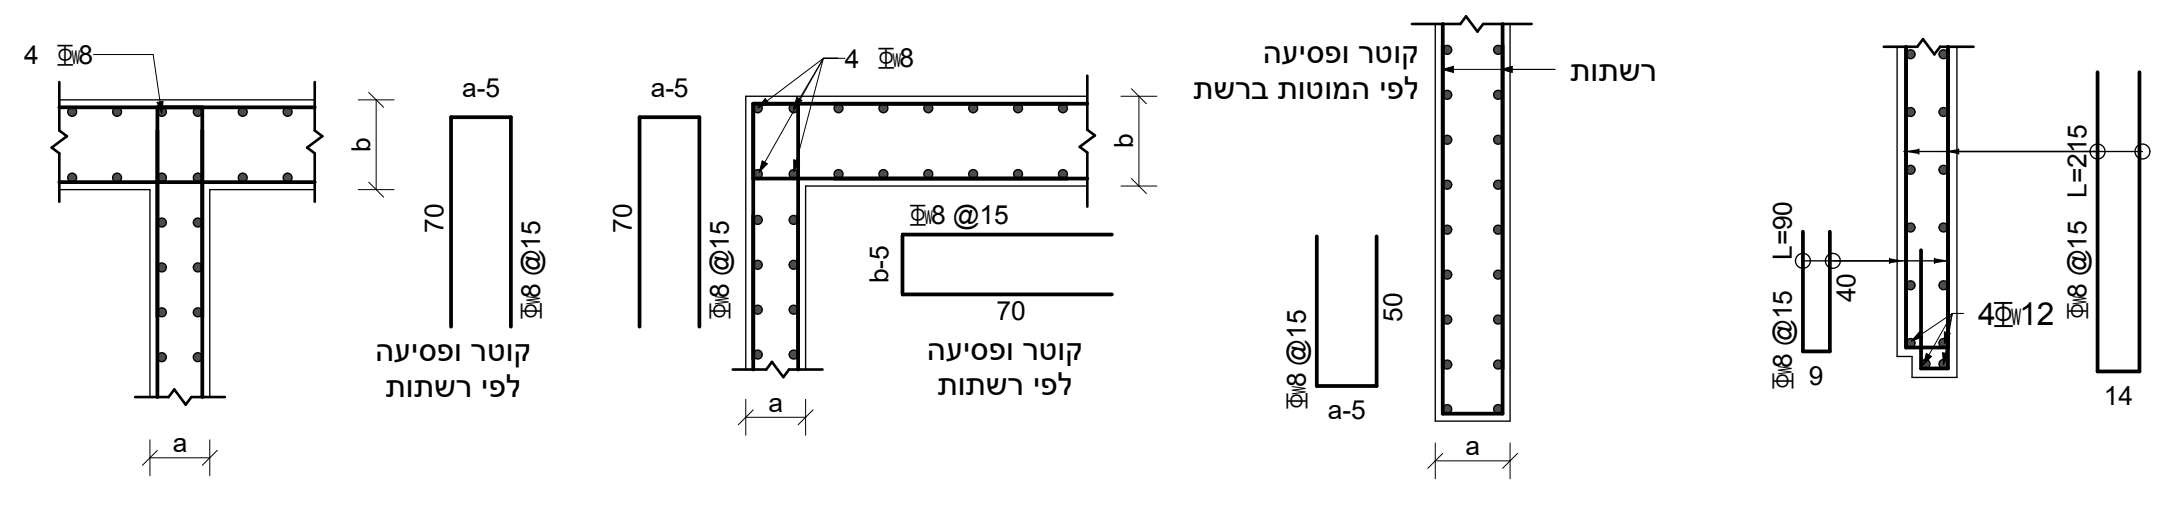

פרט להוצאת קוצים לעמודים

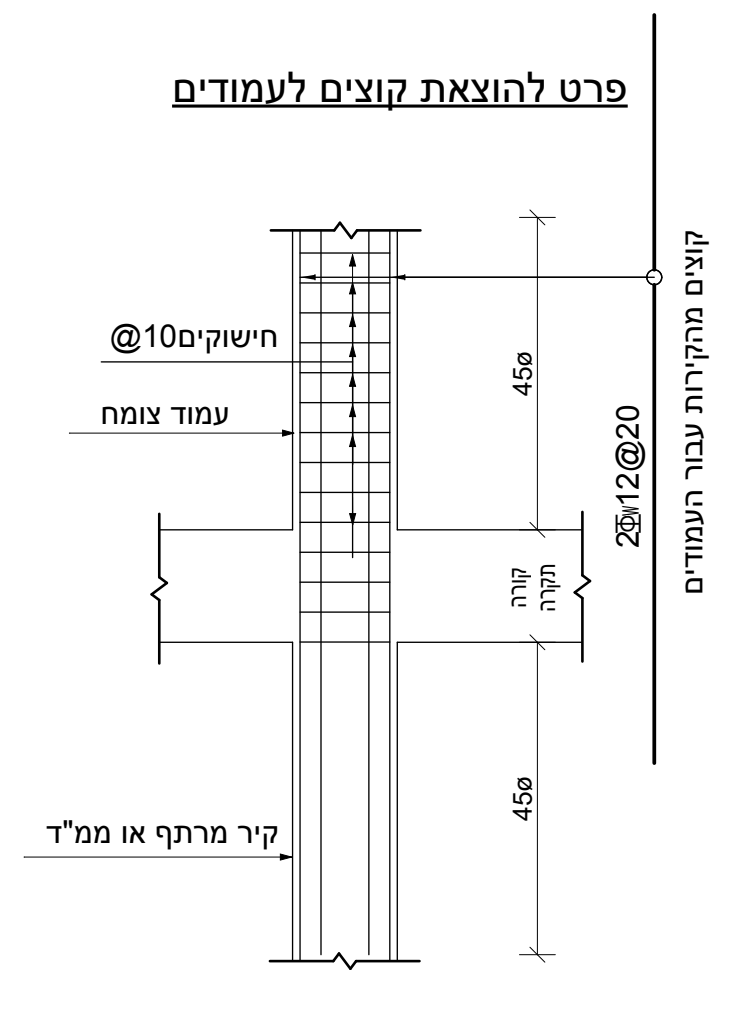

פרט המשכיות ברזל
לעמוד מוקטן

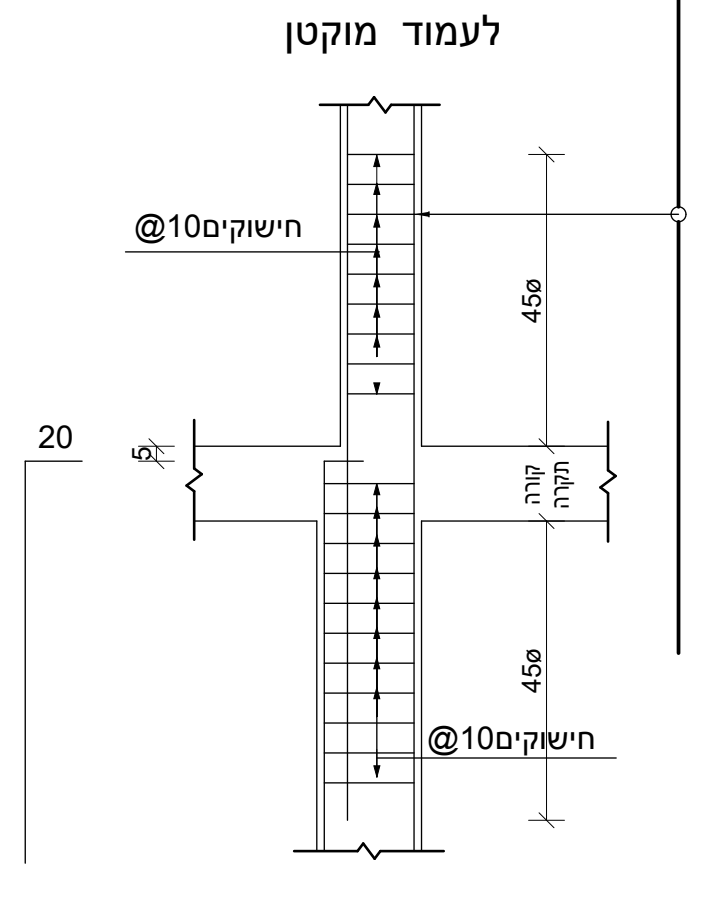

פרט המשכיות ברזל
לעמוד מוגדל

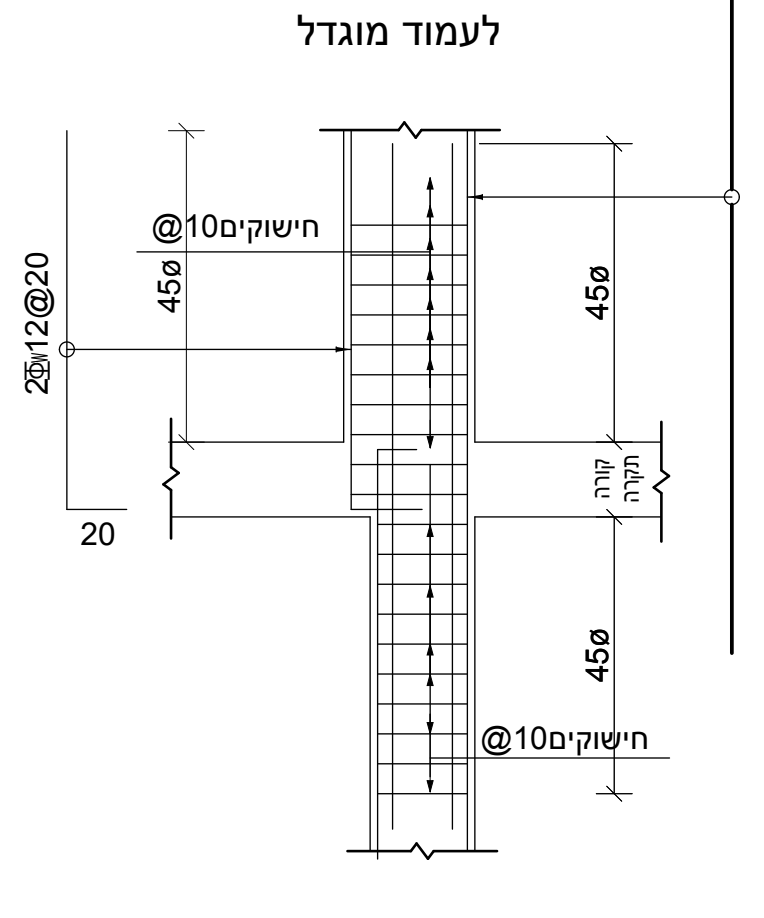

פרט המשכיות ברזל
לעמוד עולה