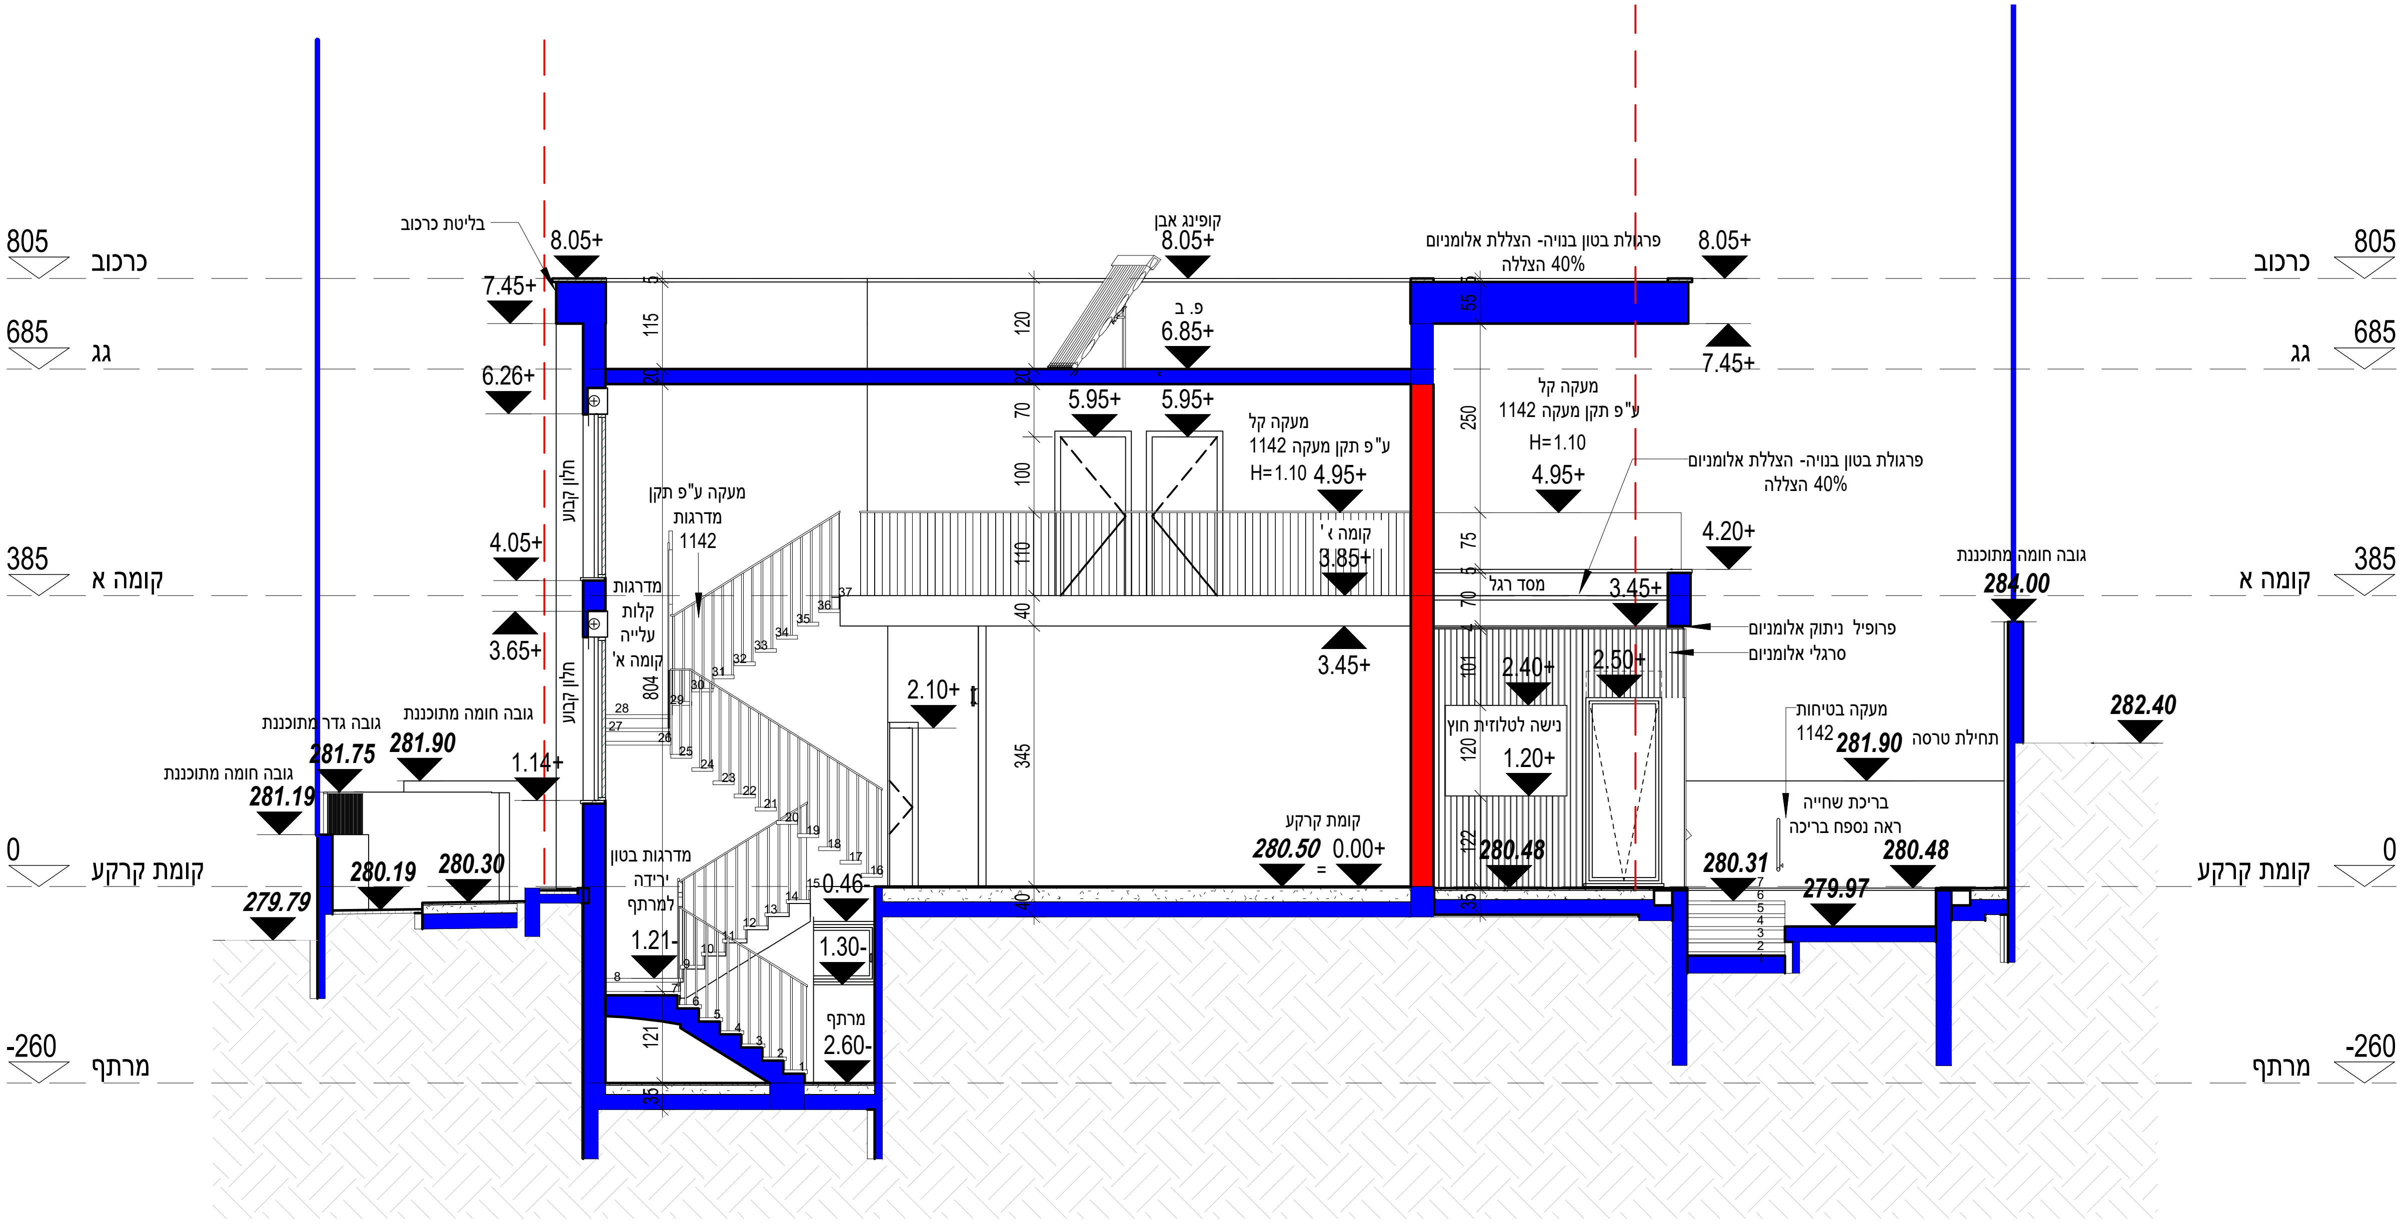

805 כרכוב
685 גג
385 קומה א
0 קומת קרקע
-260 מרתף
805 כרכוב
685 גג
385 קומה א
0 קומת קרקע
-260 מרתף
בליטת כרכוב
8.05+
7.45+
6.26+
4.05+
3.65+
1.14+
חלון קבוע
חלון קבוע
מעקה ע"פ תקן מדרגות 1142
מדרגות קלות עלייה קומה א'
804
גובה גדר מתוכננת
281.75
גובה חומה מתוכננת
281.90
גובה חומה מתוכננת
281.19
279.79
280.19
280.30
מדרגות בטון ירידה למרתף
1.21-
0.46-
1.30-
מרתף
2.60-
121
35
115
120
20
70
100
110
40
345
קופינג אבן
8.05+
פ. ב
6.85+
5.95+
5.95+
מעקה קל ע"פ תקן מעקה 1142 H=1.10
4.95+
קומה א'
3.85+
3.45+
2.10+
קומת קרקע
280.50
0.00+
פרגולת בטון בנויה- הצללת אלומניום הצללה 40%
8.05+
7.45+
55
250
מעקה קל ע"פ תקן מעקה 1142 H=1.10
4.95+
פרגולת בטון בנויה- הצללת אלומניום הצללה 40%
4.20+
75
70
מסד רגל
3.45+
פרופיל ניתוק אלומניום
סרגלי אלומניום
101
2.40+
2.50+
נישה לטלוזית חוץ
120
1.20+
122
280.48
35
גובה חומה מתוכננת
284.00
282.40
מעקה בטיחות 1142
281.90
תחילת טרסה
בריכת שחייה ראה נספח בריכה
280.31
279.97
280.48