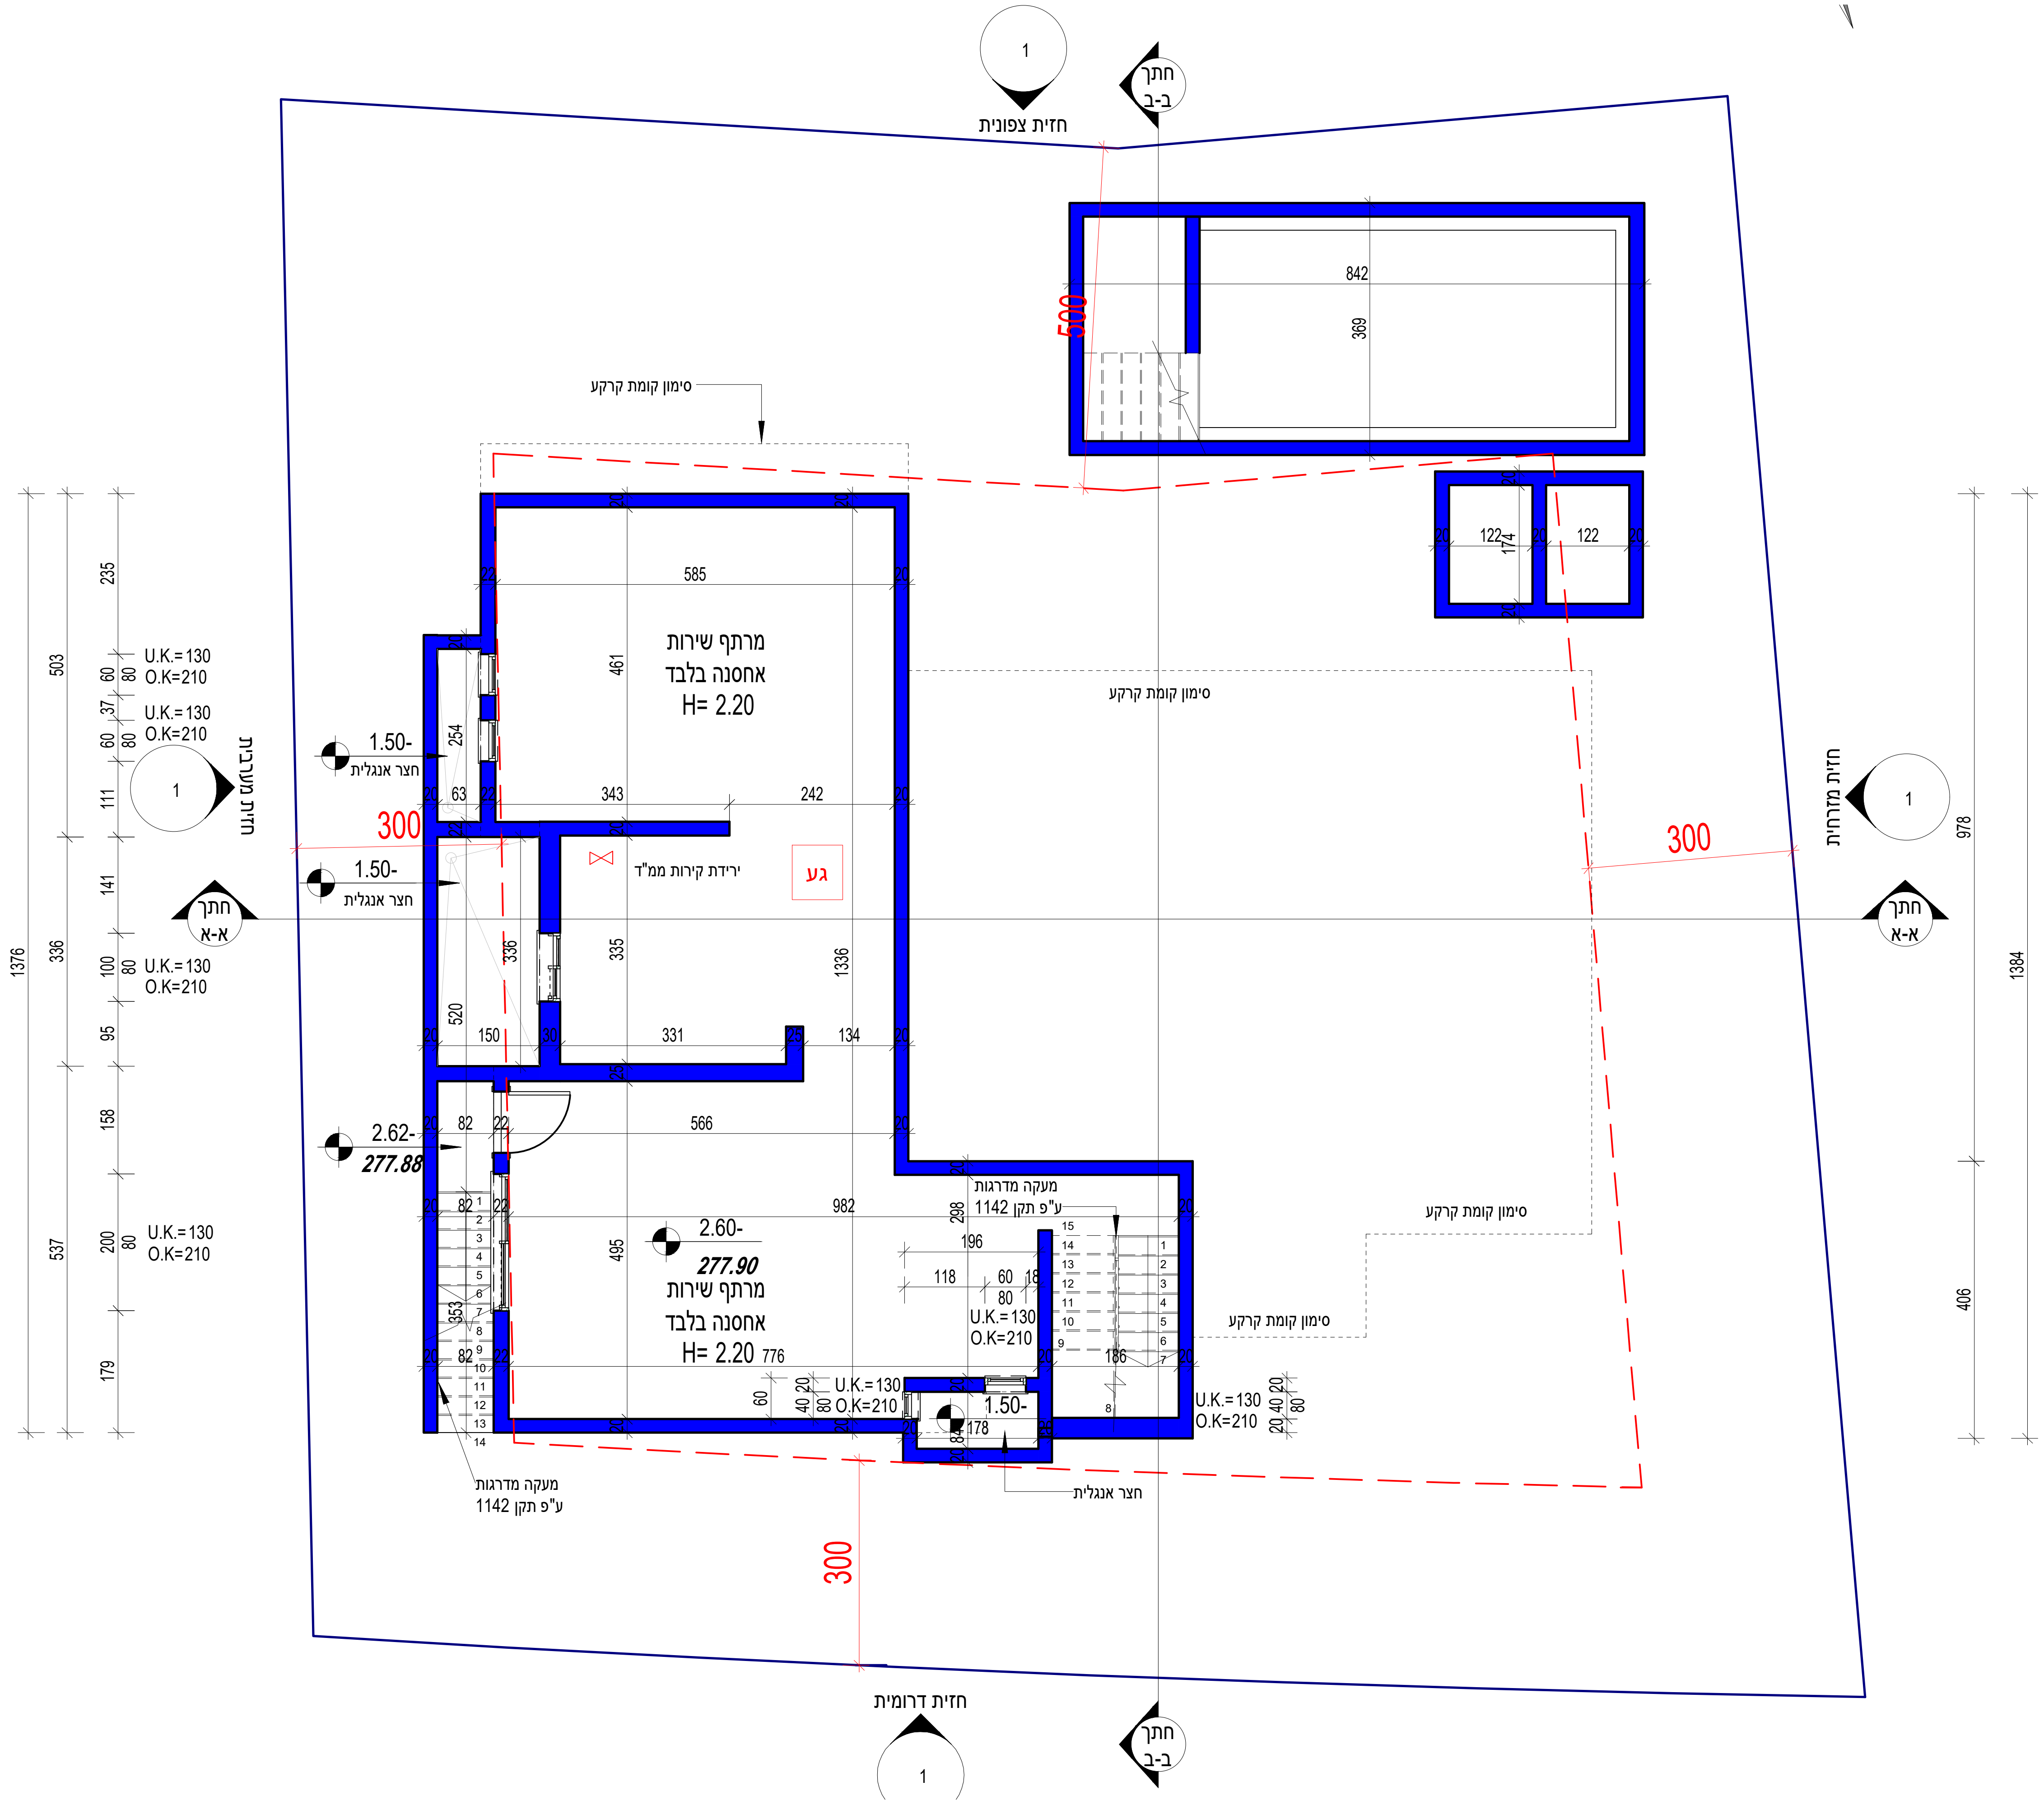

חזית צפונית
1
חתך ב-ב
סימון קומת קרקע
500
842
369
122
174
122
585
461
מרתף שירות
אחסנה בלבד
H= 2.20
343
242
63
254
1.50-
חצר אנגלית
300
ירידת קירות ממ"ד
גע
1.50-
חצר אנגלית
336
335
1336
520
150
331
134
2.62-
277.88
82
22
566
982
2.60-
277.90
מרתף שירות
אחסנה בלבד
H= 2.20
776
495
353
מעקה מדרגות
ע"פ תקן 1142
298
196
118
60
18
80
U.K.=130
O.K=210
186
1.50-
178
חצר אנגלית
U.K.=130
O.K=210
מעקה מדרגות
ע"פ תקן 1142
300
סימון קומת קרקע
סימון קומת קרקע
300
חזית מזרחית
חתך א-א
חתך א-א
חזית מערבית
U.K.=130
O.K=210
U.K.=130
O.K=210
U.K.=130
O.K=210
U.K.=130
O.K=210
1376
503
336
537
235
60
80
37
60
80
111
141
100
80
95
158
200
80
179
978
406
1384
חזית דרומית
חתך ב-ב