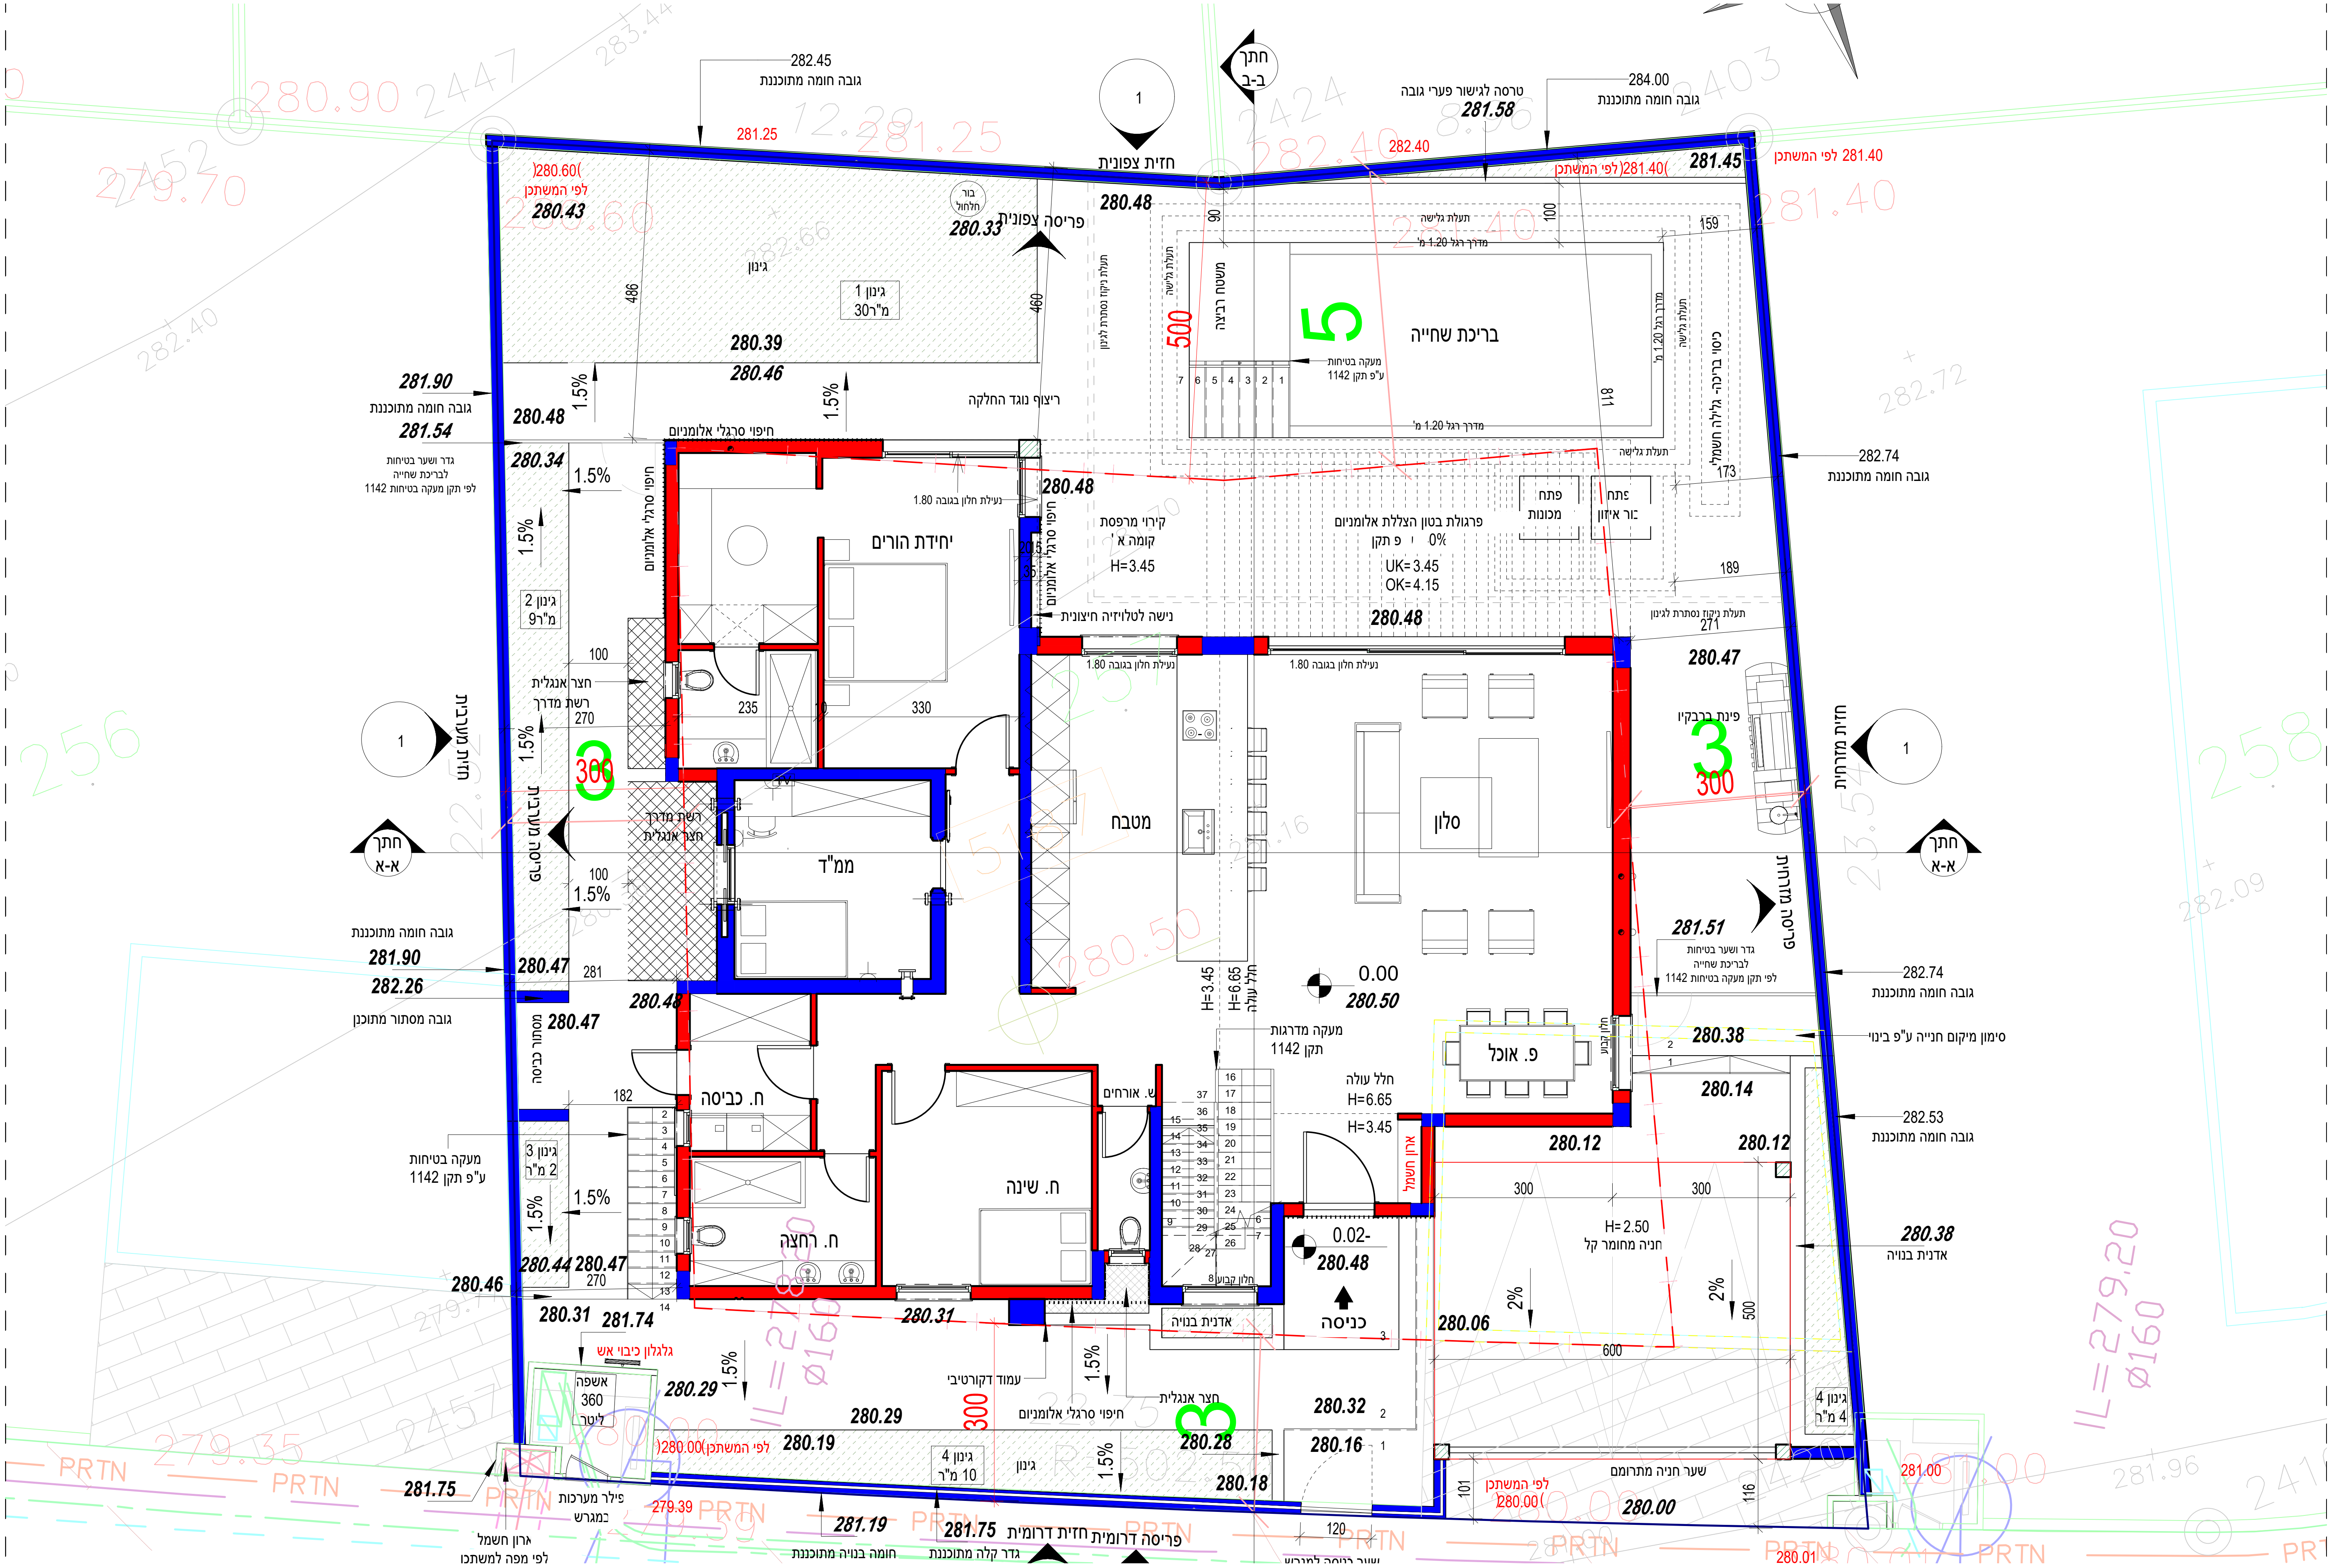
חזית צפונית
פריסה צפונית
1
חתך ב-ב
282.45
גובה חומה מתוכננת
281.25
284.00
גובה חומה מתוכננת
טרסה לגישור פערי גובה
281.58
282.40
(281.40 לפי המשתנה)
281.45
281.40 לפי המשתנה
(280.60
לפי המשתנה
280.43
בור חלחול
280.33
280.48
גינון
גינון 1
30 מ"ר
486
460
280.39
280.46
1.5%
ריצוף נגד החלקה
תעלת ניקוז נסתרת לגינון
90
100
משטח רביעה
500
תעלת גלישה
מדרך רגל 1.20 מ'
5
בריכת שחייה
מעקה בטיחות
ע"פ תקן 1142
7 6 5 4 3 2 1
מדרך רגל 1.20 מ'
118
159
כיסוי בריכה - גלילה חשמלי
173
281.90
גובה חומה מתוכננת
281.54
גדר ושער בטיחות
לבריכת שחייה
לפי תקן מעקה בטיחות 1142
280.48
280.34
חיפוי סרגלי אלומיניום
1.5%
גינון 2
9 מ"ר
נעילת חלון בגובה 1.80
יחידת הורים
280.48
חיפוי סרגלי אלומיניום
קיר מרפסת
קומה א'
H=3.45
פרגולת בטון הצללת אלומיניום
לפי תקן 0%
UK=3.45
OK=4.15
פתח מכונות
חדר איזון
282.74
גובה חומה מתוכננת
189
280.48
נישה לטלוויזיה חיצונית
תעלת ניקוז נסתרת לגינון
271
280.47
100
חצר אנגלית
רשת מדרך
270
235
330
נעילת חלון בגובה 1.80
נעילת חלון בגובה 1.80
פינת ברבקיו
3
300
חזית מזרחית
1
פריסה מערבית
3
300
רשת מדרך
חצר אנגלית
ממ"ד
מטבח
סלון
חתך א-א
חתך א-א
100
1.5%
גובה חומה מתוכננת
281.90
282.26
גובה מסתור מתוכנן
280.47
281
280.48
280.47
מסתור כביסה
H=3.45
H=6.65
חלל עולה
0.00
280.50
281.51
גדר ושער בטיחות
לבריכת שחייה
לפי תקן מעקה בטיחות 1142
פריסה מזרחית
282.74
גובה חומה מתוכננת
מעקה מדרגות
תקן 1142
פ. אוכל
280.38
סימון מיקום חנייה ע"פ בינוי
280.14
182
ח. כביסה
ש. אורחים
חלל עולה
H=6.65
H=3.45
ארון חשמל
280.12
280.12
282.53
גובה חומה מתוכננת
מעקה בטיחות
ע"פ תקן 1142
גינון 3
2 מ"ר
1.5%
ח. רחצה
ח. שינה
0.02-
280.48
300
300
H=2.50
חניה מקורה קל
280.38
אדנית בנויה
280.44
280.47
270
280.46
280.31
281.74
280.31
אדנית בנויה
כניסה
280.06
2%
2%
500
600
גלגלון כיבוי אש
אשפה
360
ליטר
1.5%
280.29
עמוד קורטיבי
1.5%
חצר אנגלית
חיפוי סרגלי אלומיניום
3
280.32
280.29
280.28
280.16
גינון 4
4 מ"ר
(280.00 לפי המשתנה
280.19
גינון 4
10 מ"ר
גינון
1.5%
280.18
שער חניה מתרומם
לפי המשתנה
280.00)
280.00
116
101
281.00
281.75
פילר מערכות
במגרש
279.39
281.19
281.75
פריסה דרומית
חזית דרומית
120
ארון חשמל
לפי מפה למשתנה
חומה בנויה מתוכננת
גדר קלה מתוכננת
שער מגורים
280.01
PRTN