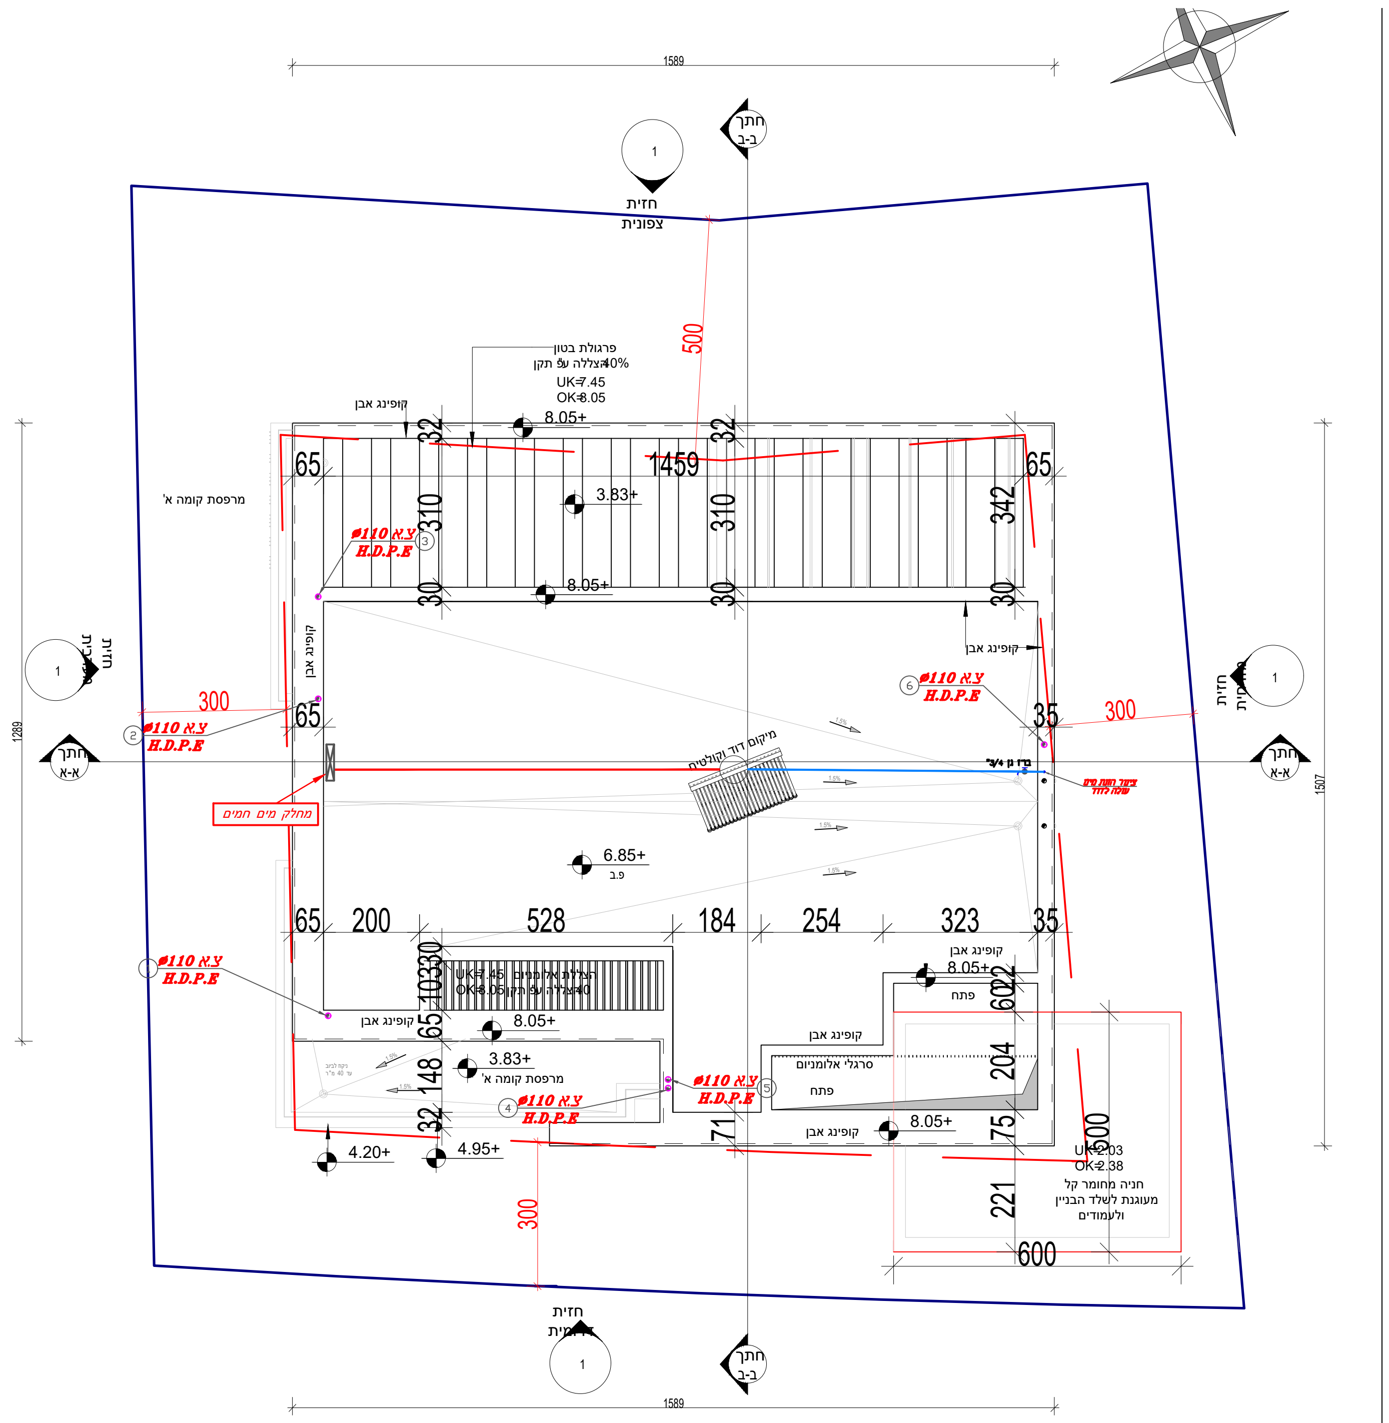1589
חתך
ב-ב
1
חזית
צפונית
500
פרגולת בטון
הצללה עפ"י תקן 40%
UK=7.45
OK=8.05
קופינג אבן
8.05+
32
1459
32
65
65
מרפסת קומה א'
3.83+
310
310
342
צ.ג ø110
H.D.P.E
3
8.05+
30
30
30
קופינג אבן
קופינג אבן
6
צ.ג ø110
H.D.P.E
300
300
65
35
2
צ.ג ø110
H.D.P.E
חתך
א-א
חתך
א-א
מיקום דוד וקולטים
ברז גן 3/4"
ציוד הזנת מים שלה לדוד
מחלק מים חמים
1.5%
1.5%
1.5%
1.5%
6.85+
פ.ב
1289
1507
65
200
528
184
254
323
35
צ.ג ø110
H.D.P.E
1
הצללת אלומניום
הצללה עפ"י תקן 40
UK=7.45
OK=8.05
10330
קופינג אבן
8.05+
קופינג אבן
8.05+
פתח
602
65
8.05+
קופינג אבן
3.83+
מרפסת קומה א'
ניקוז לביוב
עד 40 מ"ר
148
32
צ.ג ø110
H.D.P.E
4
צ.ג ø110
H.D.P.E
5
סרגלי אלומניום
פתח
204
71
75
קופינג אבן
8.05+
4.20+
4.95+
500
UK=2.03
OK=2.38
חניה מחומר קל
מעוגנת לשלד הבניין
ולעמודים
221
600
300
חזית
דרומית
1
חתך
ב-ב
1589