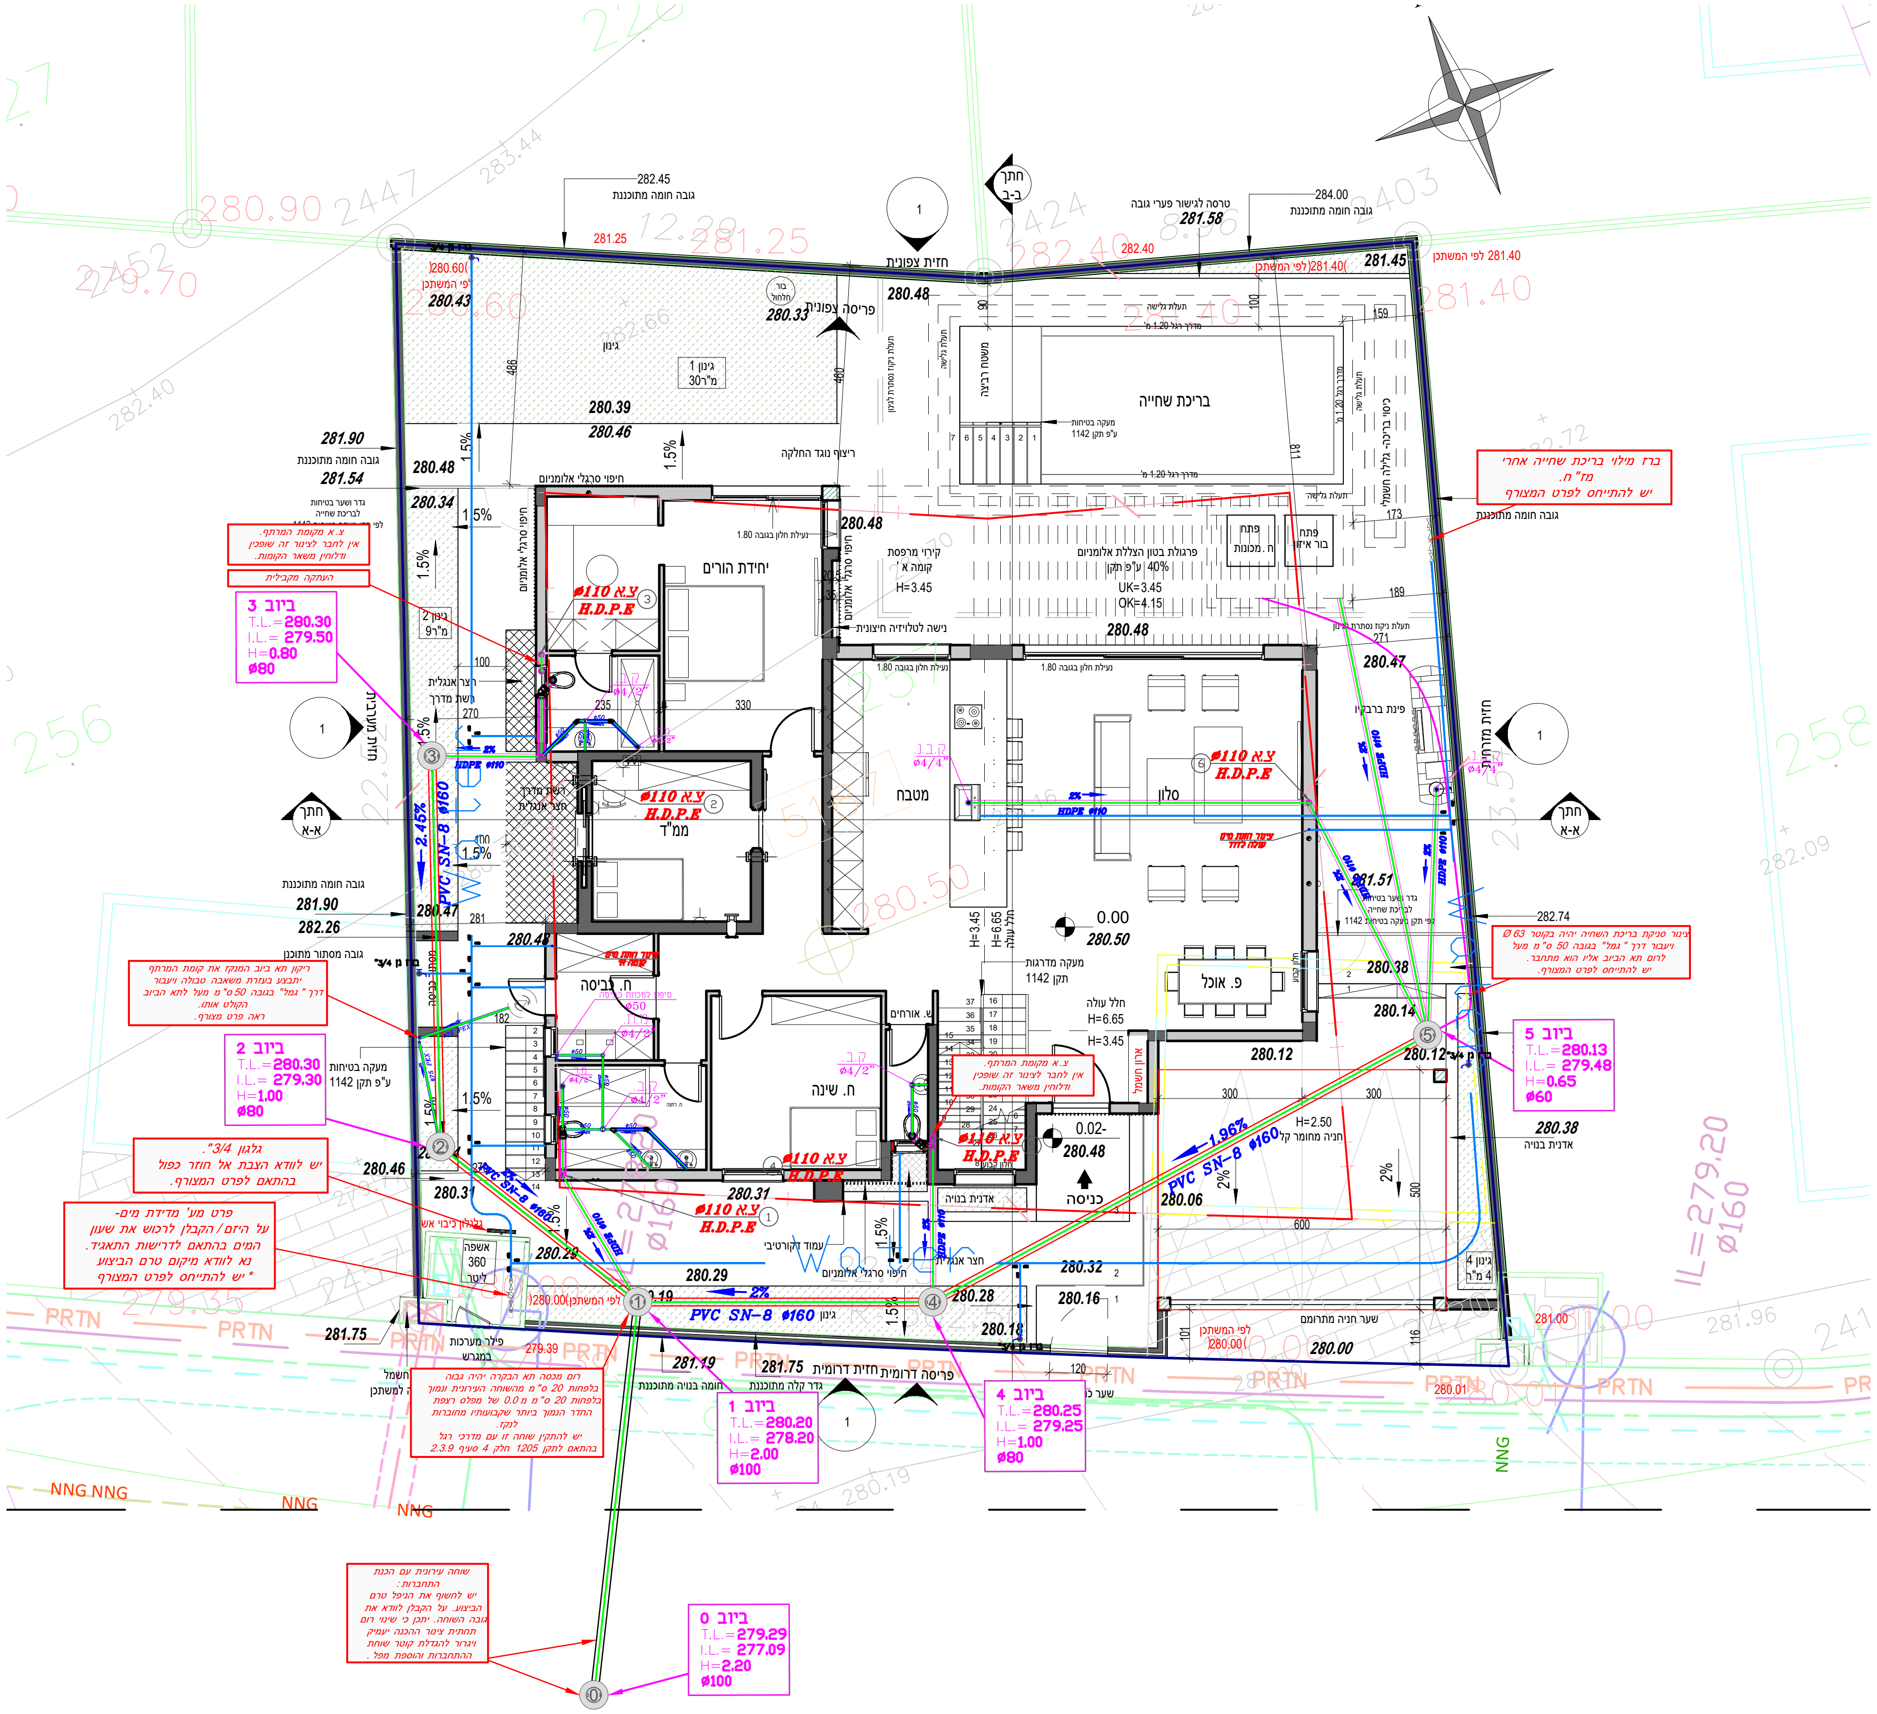

חזית צפונית
חזית דרומית
חזית מזרחית
חזית מערבית
פריסה צפונית
פריסה דרומית
חתך א-א
חתך ב-ב
בריכת שחייה
משטח רביצה
פרגולת בטון הצללת אלומיניום 40% ע"פ תקן
UK=3.45
OK=4.15
יחידת הורים
ממ"ד
מטבח
סלון
פ. אוכל
ח. שינה
ח. רחצה
ש. אורחים
כניסה
ארון חשמל
חניה מחומר קל
H=2.50
שער חניה מתרומם
אדנית בנויה
גינון
גינון 1 30 מ"ר
גינון 2 9 מ"ר
גינון 4 4 מ"ר
פינת ברבקיו
פתח בור איזון
פתח מכונות
כיסוי בריכה- גלילה חשמלי
תעלת גלישה
תעלת ניקוז נסתרת בגינון
מדרך רגל 1.20 מ'
מעקה בטיחות 1142 ע"פ תקן
מעקה מדרגות 1142 תקן
גדר ושער בטיחות לבריכת שחייה לפי תקן מעקה בטיחות 1142
גובה חומה מתוכננת
גובה מסתור מתוכנן
חומה בנויה מתוכננת
גדר קלה מתוכננת
פילר מערכות במגרש
חשמל
אשפה 360 ליטר
גלגלון כיבוי אש
עמוד דקורטיבי
חיפוי סרגלי אלומיניום
חצר אנגלית
רשת מדרך
ריצוף נוגד החלקה
חלל עולה H=6.65
H=3.45
0.00
280.50
0.02-
280.48
PVC SN-8 ø160
2.45%
1.96%
2%
1.5%
ø110 צ.א H.D.P.E
HDPE ø110
ברז גן 3/4"
281.25
280.43
280.33
280.48
281.45
281.90
281.54
280.34
280.47
281.90
282.26
280.46
280.31
280.29
281.75
281.19
281.75
280.28
280.18
280.16
280.32
280.06
280.12
280.14
280.38
281.51
282.74
280.00
282.45
284.00
281.58
IL=279.20
ø160
PRTN
NNG

צ.א מקומת המרתף.
אין לחבר לצינור זה שופכין ודלוחין משאר הקומות.

העתקה מקבילית

ביוב 3
T.L.=280.30
I.L.= 279.50
H=0.80
ø80

ריקון תא ביוב המנקז את קומת המרתף יתבצע בעזרת משאבה טבולה ויעבור דרך " גמל" בגובה 50 ס"מ מעל לתא הביוב הקולט אותו.
ראה פרט מצורף.

ביוב 2
T.L.=280.30
I.L.= 279.30
H=1.00
ø80

גלגון 3/4".
יש לוודא הצבת אל חוזר כפול בהתאם לפרט המצורף.

פרט מע' מדידת מים-
על היזם/הקבלן לרכוש את שעון המים בהתאם לדרישות התאגיד.
נא לוודא מיקום טרם הביצוע
* יש להתייחס לפרט המצורף

רום מכסה תא הבקרה יהיה גבוה בלפחות 20 ס"מ מהשוחה העירונית ונמוך בלפחות 20 ס"מ מ 0.0 של מפלס רצפת החדר הנמוך ביותר שקבועותיו מחוברות לנקז.
יש להתקין שוחה זו עם מדרכי רגל בהתאם לתקן 1205 חלק 4 סעיף 2.3.9

ביוב 1
T.L.=280.20
I.L.= 278.20
H=2.00
ø100

ביוב 4
T.L.=280.25
I.L.= 279.25
H=1.00
ø80

ביוב 5
T.L.=280.13
I.L.= 279.48
H=0.65
ø60

שוחה עירונית עם הכנת התחברות:
יש לחשוף את הניפל טרם הביצוע. על הקבלן לוודא את גובה השוחה. יתכן כי שינוי רום תחתית צינור ההכנה יעמיק ויגרור להגדלת קוטר שוחת ההתחברות והוספת מפל.

ביוב 0
T.L.=279.29
I.L.= 277.09
H=2.20
ø100

ברז מילוי בריכת שחייה אחרי מז"ח.
יש להתייחס לפרט המצורף

צינור סניקת בריכת השחיה יהיה בקוטר Ø 63 ויעבור דרך " גמל" בגובה 50 ס"מ מעל לרום תא הביוב אליו הוא מתחבר.
יש להתייחס לפרט המצורף.

281.40 לפי המשתכן
280.60 לפי המשתכן
280.00 לפי המשתכן