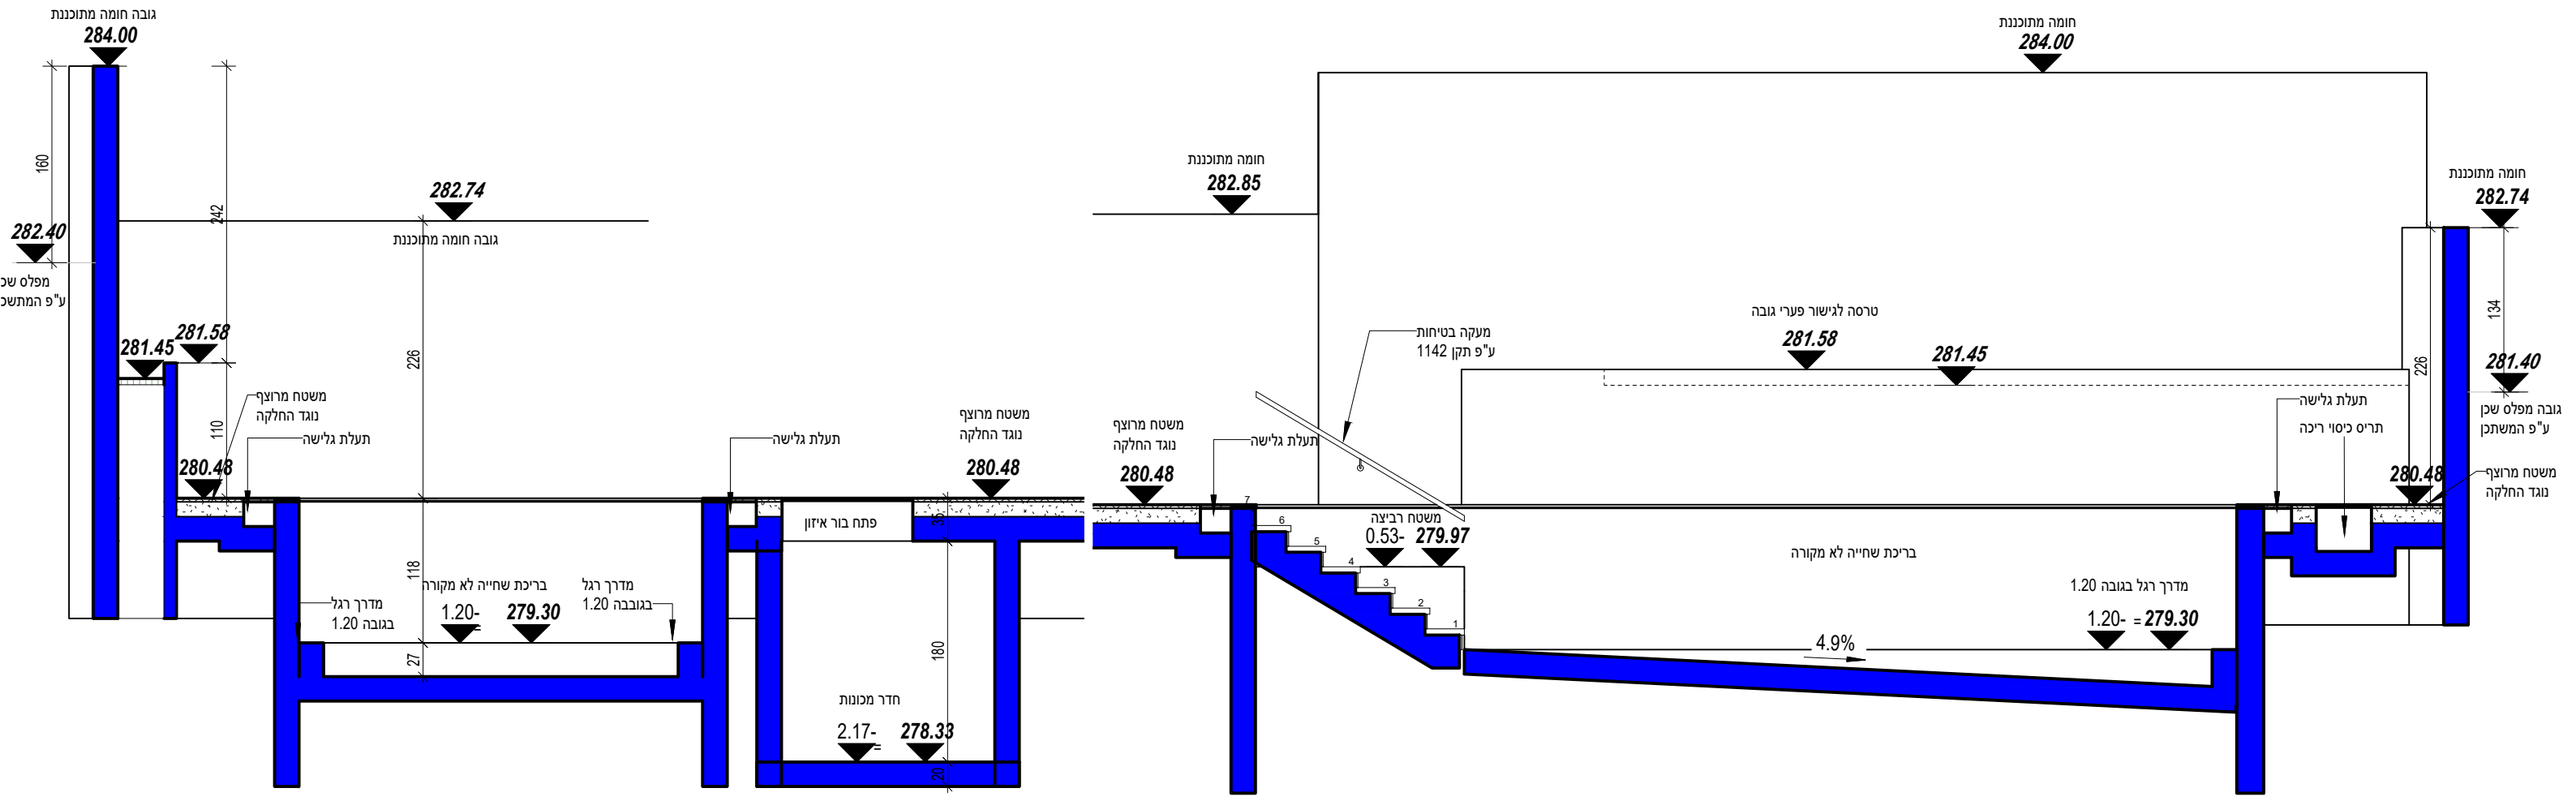

גובה חומה מתוכננת
284.00
160
282.40
מפלס שכ
ע"פ המתשכ
281.45
281.58
110
משטח מרוצף
נוגד החלקה
תעלת גלישה
280.48
226
242
282.74
גובה חומה מתוכננת
118
מדרך רגל
בגובה 1.20
בריכת שחייה לא מקורה
1.20-
279.30
מדרך רגל
בגובהבה 1.20
27
תעלת גלישה
משטח מרוצף
נוגד החלקה
280.48
פתח בור איזון
180
חדר מכונות
2.17-
278.33
20
חומה מתוכננת
284.00
חומה מתוכננת
282.85
טרסה לגישור פערי גובה
281.58
281.45
מעקה בטיחות
ע"פ תקן 1142
משטח מרוצף
נוגד החלקה
280.48
תעלת גלישה
משטח רביצה
0.53-
279.97
בריכת שחייה לא מקורה
4.9%
מדרך רגל בגובה 1.20
1.20-
279.30
חומה מתוכננת
282.74
134
281.40
גובה מפלס שכן
ע"פ המשתכן
226
תעלת גלישה
תריס כיסוי ריכה
280.48
משטח מרוצף
נוגד החלקה