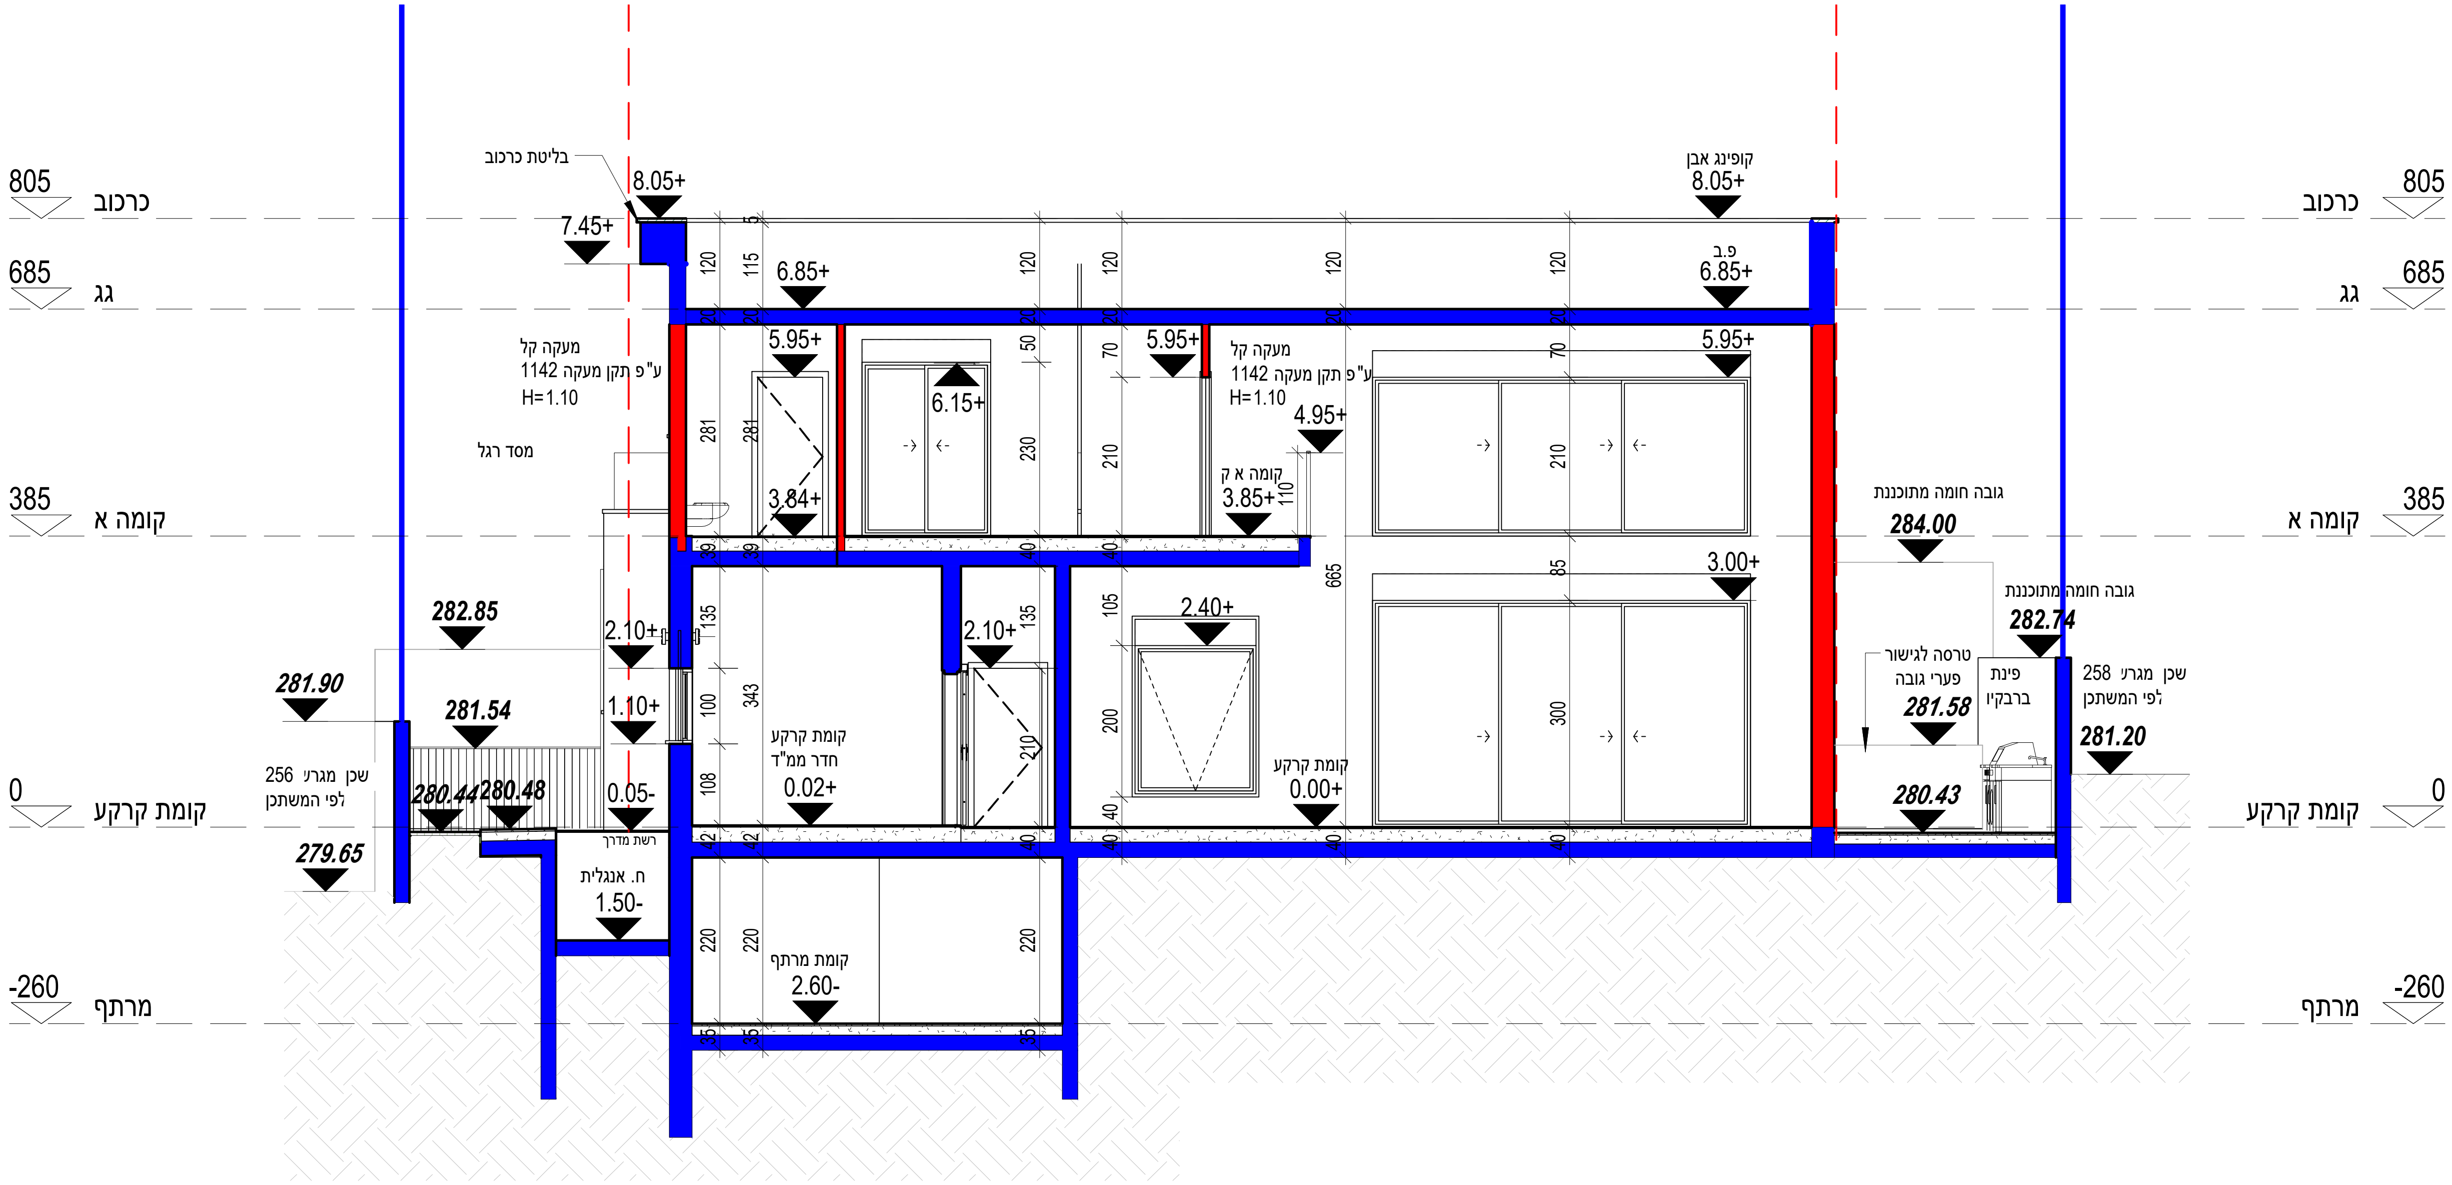
805 כרכוב
685 גג
385 קומה א
0 קומת קרקע
-260 מרתף
בליטת כרכוב
8.05+
7.45+
קופינג אבן
8.05+
פ.ב
6.85+
6.85+
5.95+
5.95+
5.95+
6.15+
מעקה קל
ע"פ תקן מעקה 1142
H=1.10
מסד רגל
מעקה קל
ע"פ תקן מעקה 1142
H=1.10
4.95+
קומה א ק
3.85+
3.84+
3.00+
2.40+
282.85
2.10+
2.10+
281.90
281.54
1.10+
קומת קרקע
חדר ממ"ד
0.02+
קומת קרקע
0.00+
0.05-
280.44
280.48
שכן מגרש 256
לפי המשתנן
279.65
רשת מדרך
ח. אנגלית
1.50-
קומת מרתף
2.60-
גובה חומה מתוכננת
284.00
גובה חומה מתוכננת
282.74
טרסה לגישור
פערי גובה
281.58
פינת
ברבקיו
שכן מגרש 258
לפי המשתנן
281.20
280.43
120
115
120
120
120
120
281
281
230
210
210
665
135
135
105
200
85
300
100
343
108
210
110
220
220
220
50
70
70
40
40
40
40
40
40
40
40
40