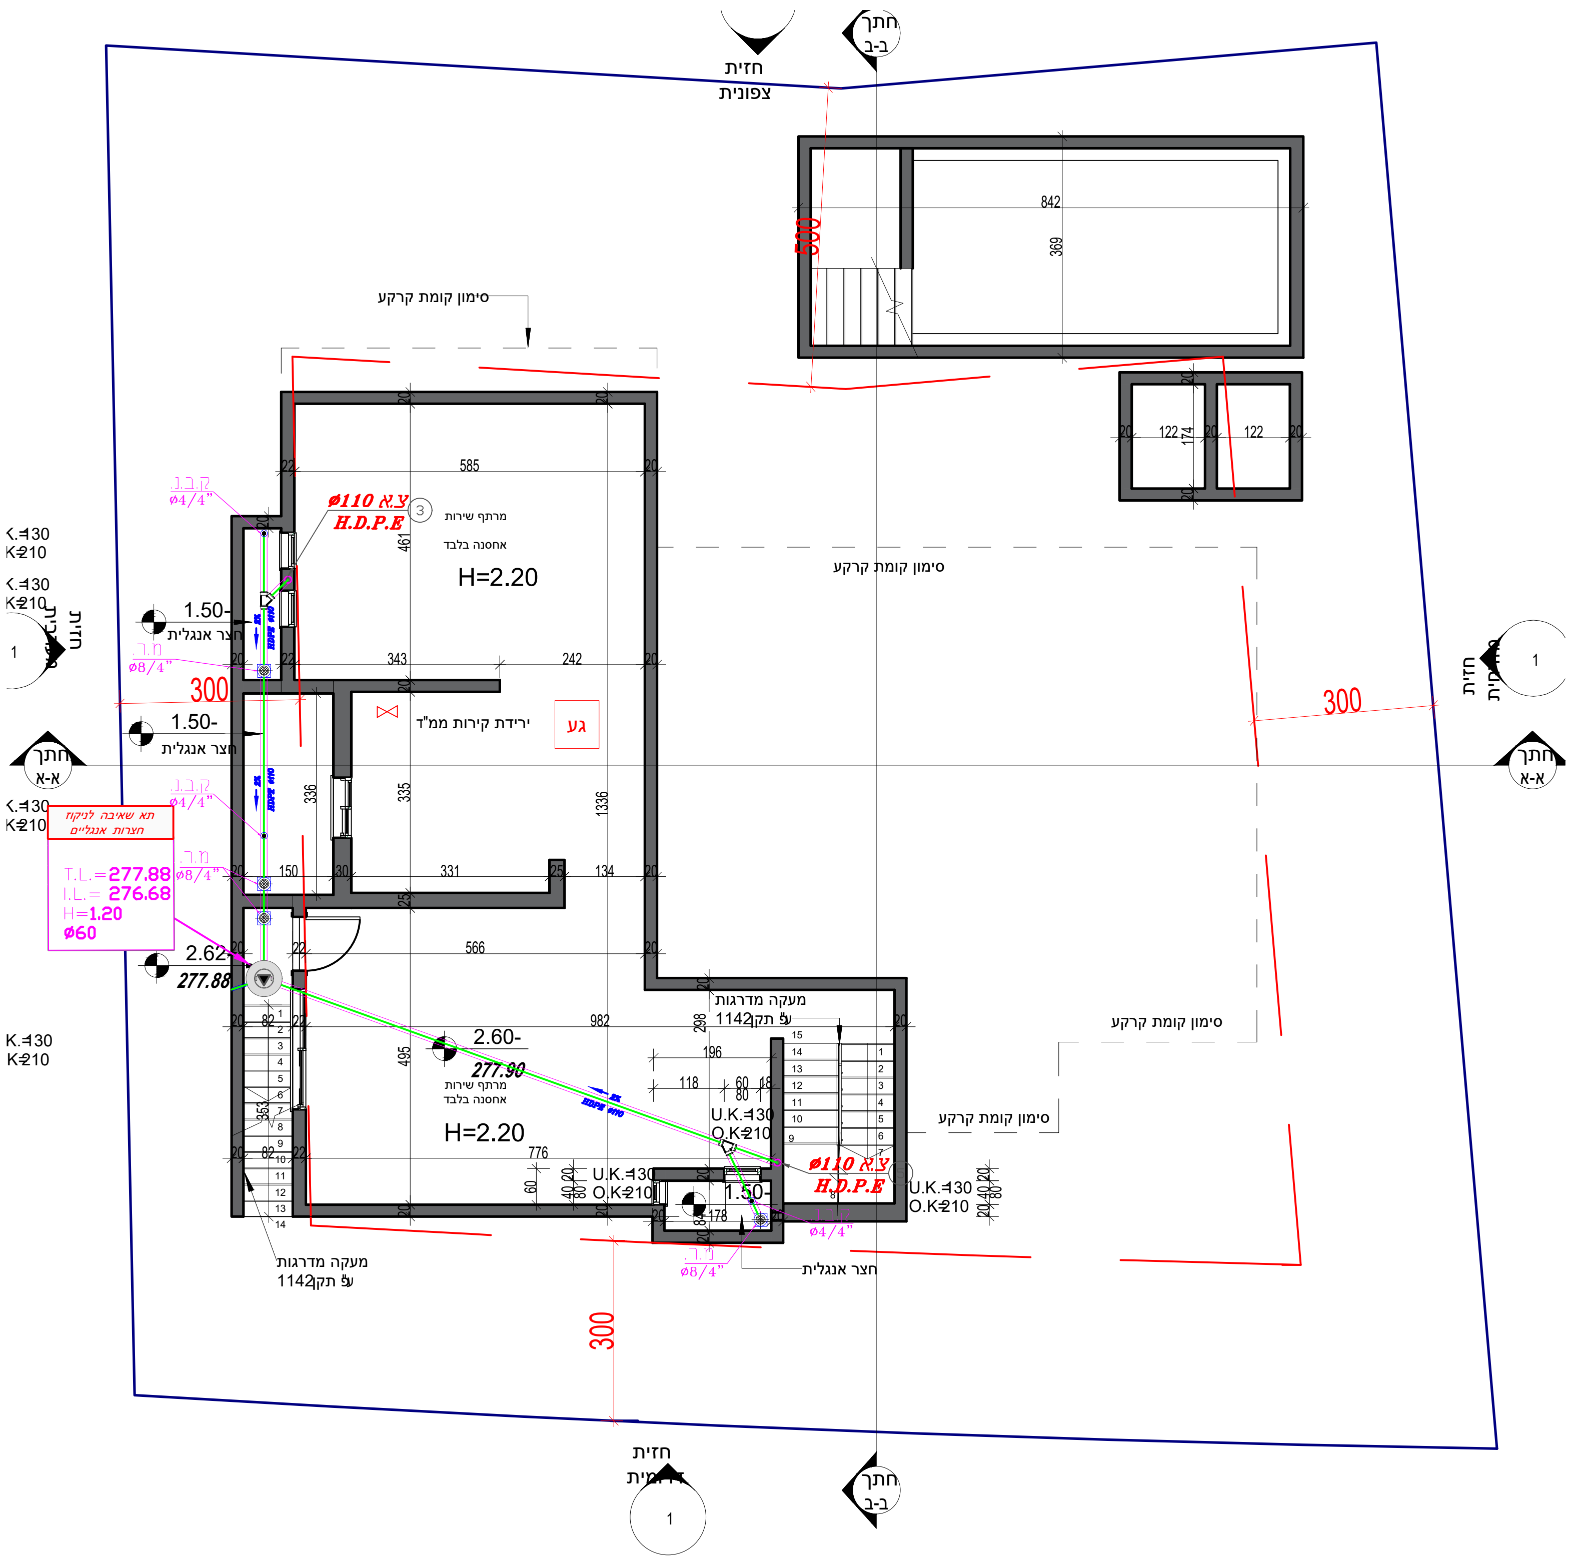
חזית
צפונית
חתך
ב-ב
500
842
369
122
174
122
סימון קומת קרקע
585
ø110 צ.א
H.D.P.E
3
מרתף שירות
אחסנה בלבד
H=2.20
461
ק.ב.נ.
ø4/4"
K.=130
K=210
1.50-
חצר אנגלית
מ.ר.
ø8/4"
343
242
300
ירידת קירות ממ"ד
גע
1.50-
חצר אנגלית
חתך
א-א
336
335
1336
תא שאיבה לניקוז
חצרות אנגליים
T.L.=277.88
I.L.= 276.68
H=1.20
ø60
150
331
134
566
2.62-
277.88
982
מעקה מדרגות
1142 עפ' תקן
298
2.60-
277.90
495
196
118
60
80
18
U.K.=130
O.K=210
מרתף שירות
אחסנה בלבד
H=2.20
776
353
1.50-
178
ø110 צ.א
H.D.P.E
ø4/4"
ø8/4"
חצר אנגלית
מעקה מדרגות
1142 עפ' תקן
סימון קומת קרקע
300
חזית
1
300
חזית
1